


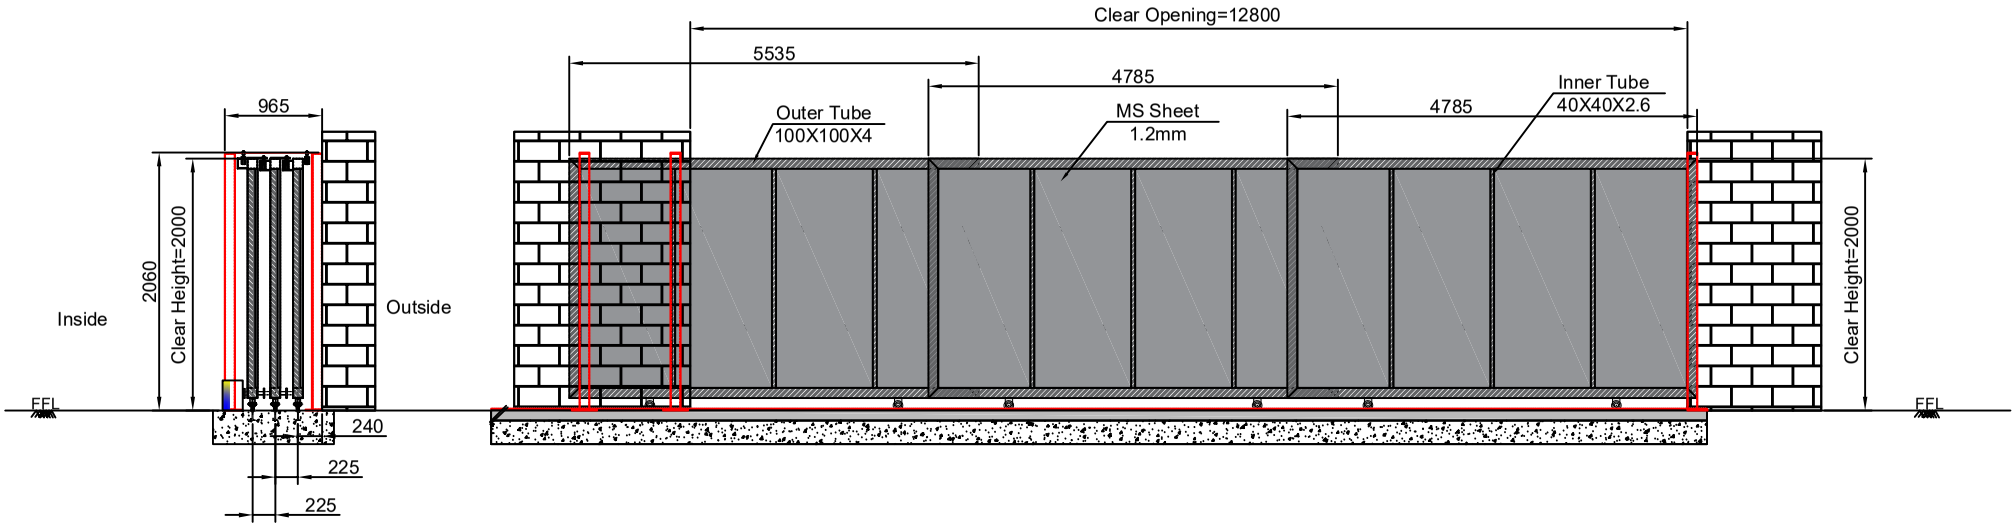

Note:-

1. All Dimension are in MM.
2. Given Above GA drawing is only for the Client Understanding purpose.
   MS sheet Cladding placing or design and leaf size may change.
3. All Civil work will be in Client scope
4. Civil,Installation and Fabrication Tolerance will be ±20mm
5. Available parking at site 6000mm is ok

RAL CODE	SHADE	COLOUR
RAL 9001	CREAM	
RAL 9002	GREY WHITE	
RAL 9010	PURE WHITE	
RAL 5002	ULTRAMARINE BLUE	
RAL 7035	LIGHT GREY	
RAL 7001	SILVER GREY	

This drawing & design is the property of NIHVA TECHNOLOGIES. Not to be sold or copied to any other concern.

TITLE:- 3L Telescopic Sliding Gate (E17,WH)

	NAME	DATE	SIGN
DRAWN	SUJATA	07/06/2022	
CHECK			
APPRD.	V.T	07/06/2022	

If any queries contact : design@nihva.com

ALL DIMENSION ARE IN mm

NIHVA
NIHVA TECHNOLOGIES PVT. LTD.

NIHVA TECHNOLOGIES PVT. LTD. PUNE
Tel : 020 66304033
Email:- info@nihva.com
Website:- www.nihva.com

CLIENT - OC Specialities

LOCATION - Solapur

PRODUCT - Telescopic Sliding Gate | QTY-

DWG NO:- NIHVA/22-23/CLT/0051 | REV- 0

SCALE: NTS | SCALE:-- 1:1 | SHEET: 01 OF 01

Rev No.	Revision	Date	Revised By