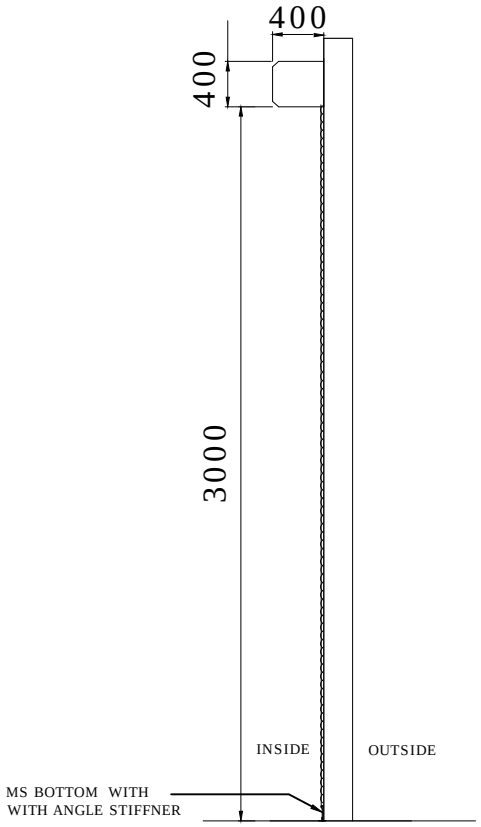

SIDE VIEW

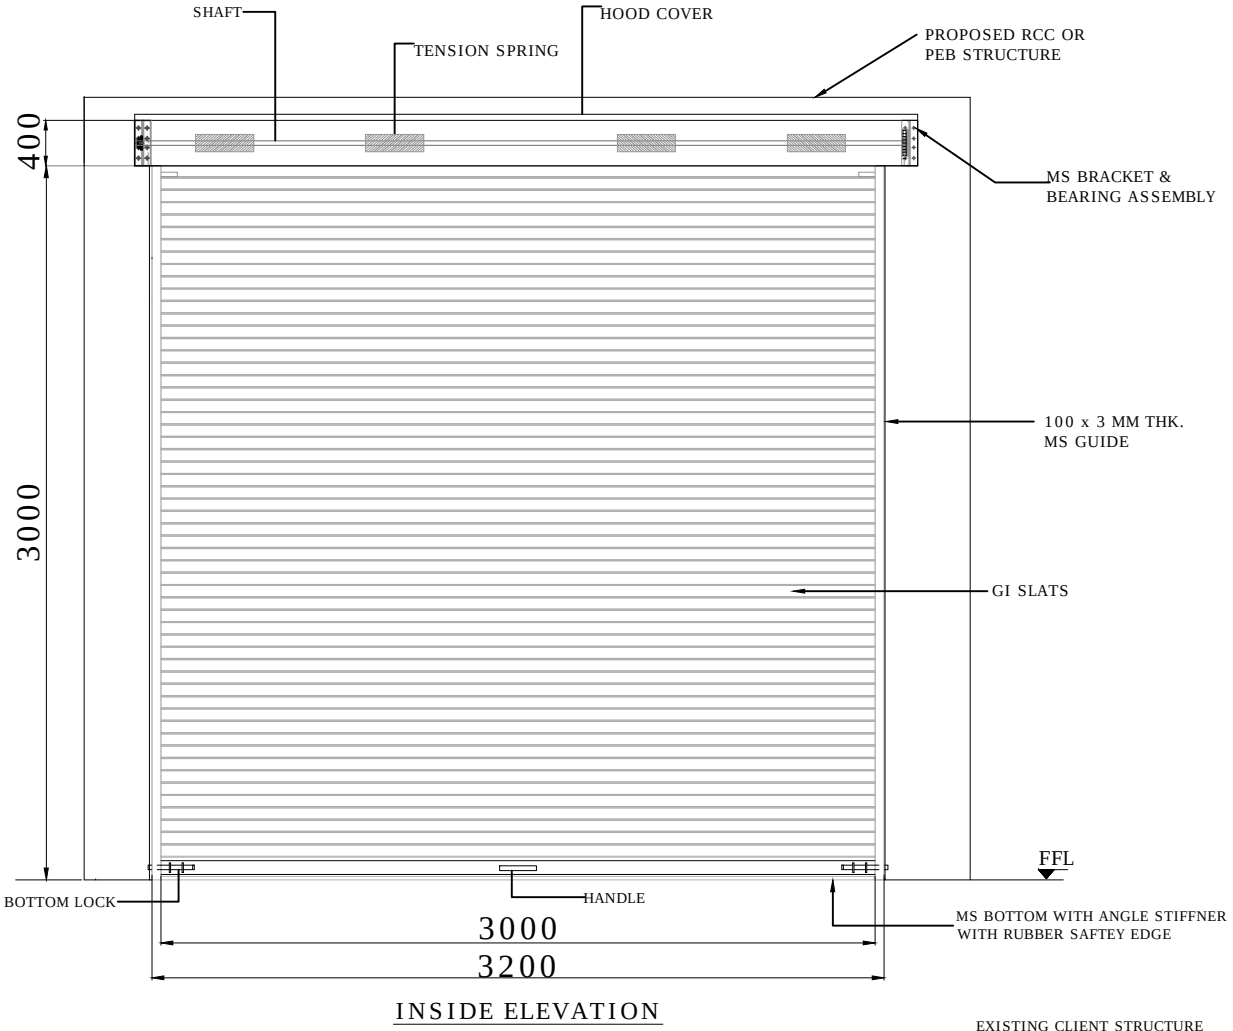

INSIDE ELEVATION

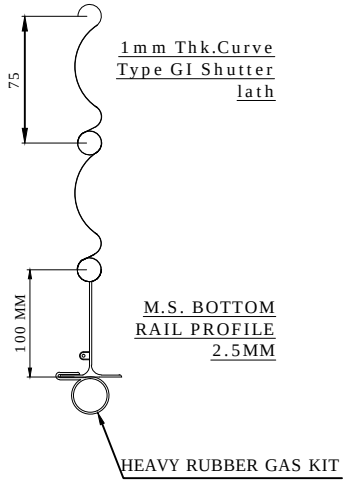

M.S. BOTTOM RAIL PROFILE 2.5MM

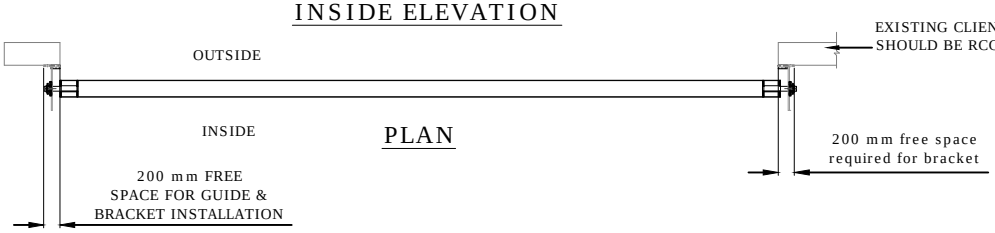

PLAN

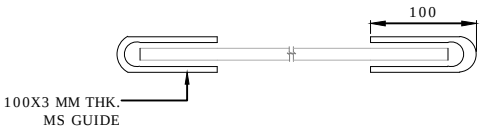

CLEAR WIDTH (CW)	CLEAR HEIGHT (CH)	QUANTITY
3000	3000	01 NO

This drawing & designing is the property of NIHVA TECHNOLOGIES. Not to be sold or copied to any other concern.

TITLE
MANUAL ROLLING SHUTTER

	SIGN	DATE
DRAWN	SURAJ	02.06.18
CHECK	PRADEEP	02.06.18
APPROVAL	PRADEEP	02.06.18
MFG.		

If any queries contact : design@nihva.com

ALL DIMENSION ARE IN mm

NIHVA TECHNOLOGIES PVT. LTD.
NIHVA TECHNOLOGIES PVT. LTD. PUNE
Tel : 020 66304033
Email:- info@nihva.com
Website:- www.nihva.com

CLIENT - Shapoorji Pallonji and Co.Pvt Ltd

PROJECT -

SITE -

DWG. NO. : NIHVA/18-19/0051 | REV-00

SCALE: NTS | WT: | SHEET: 01 OF 01