


TOP VIEW

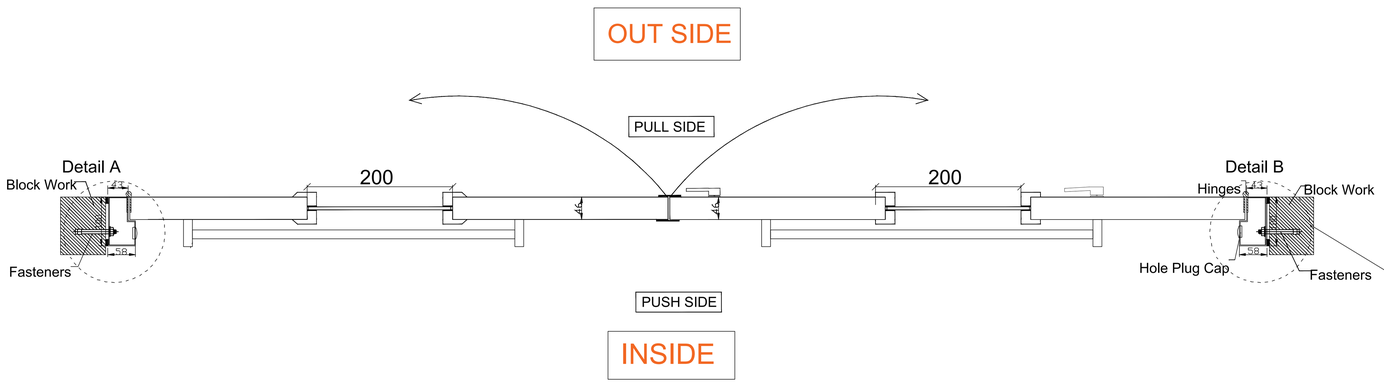


SECTION 'X'-'X'

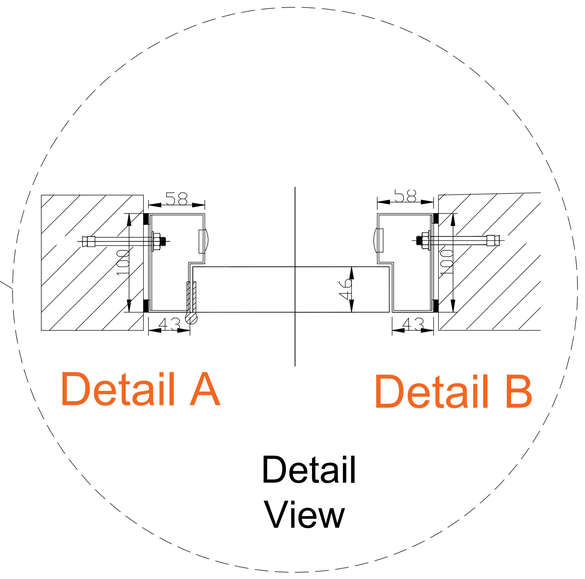

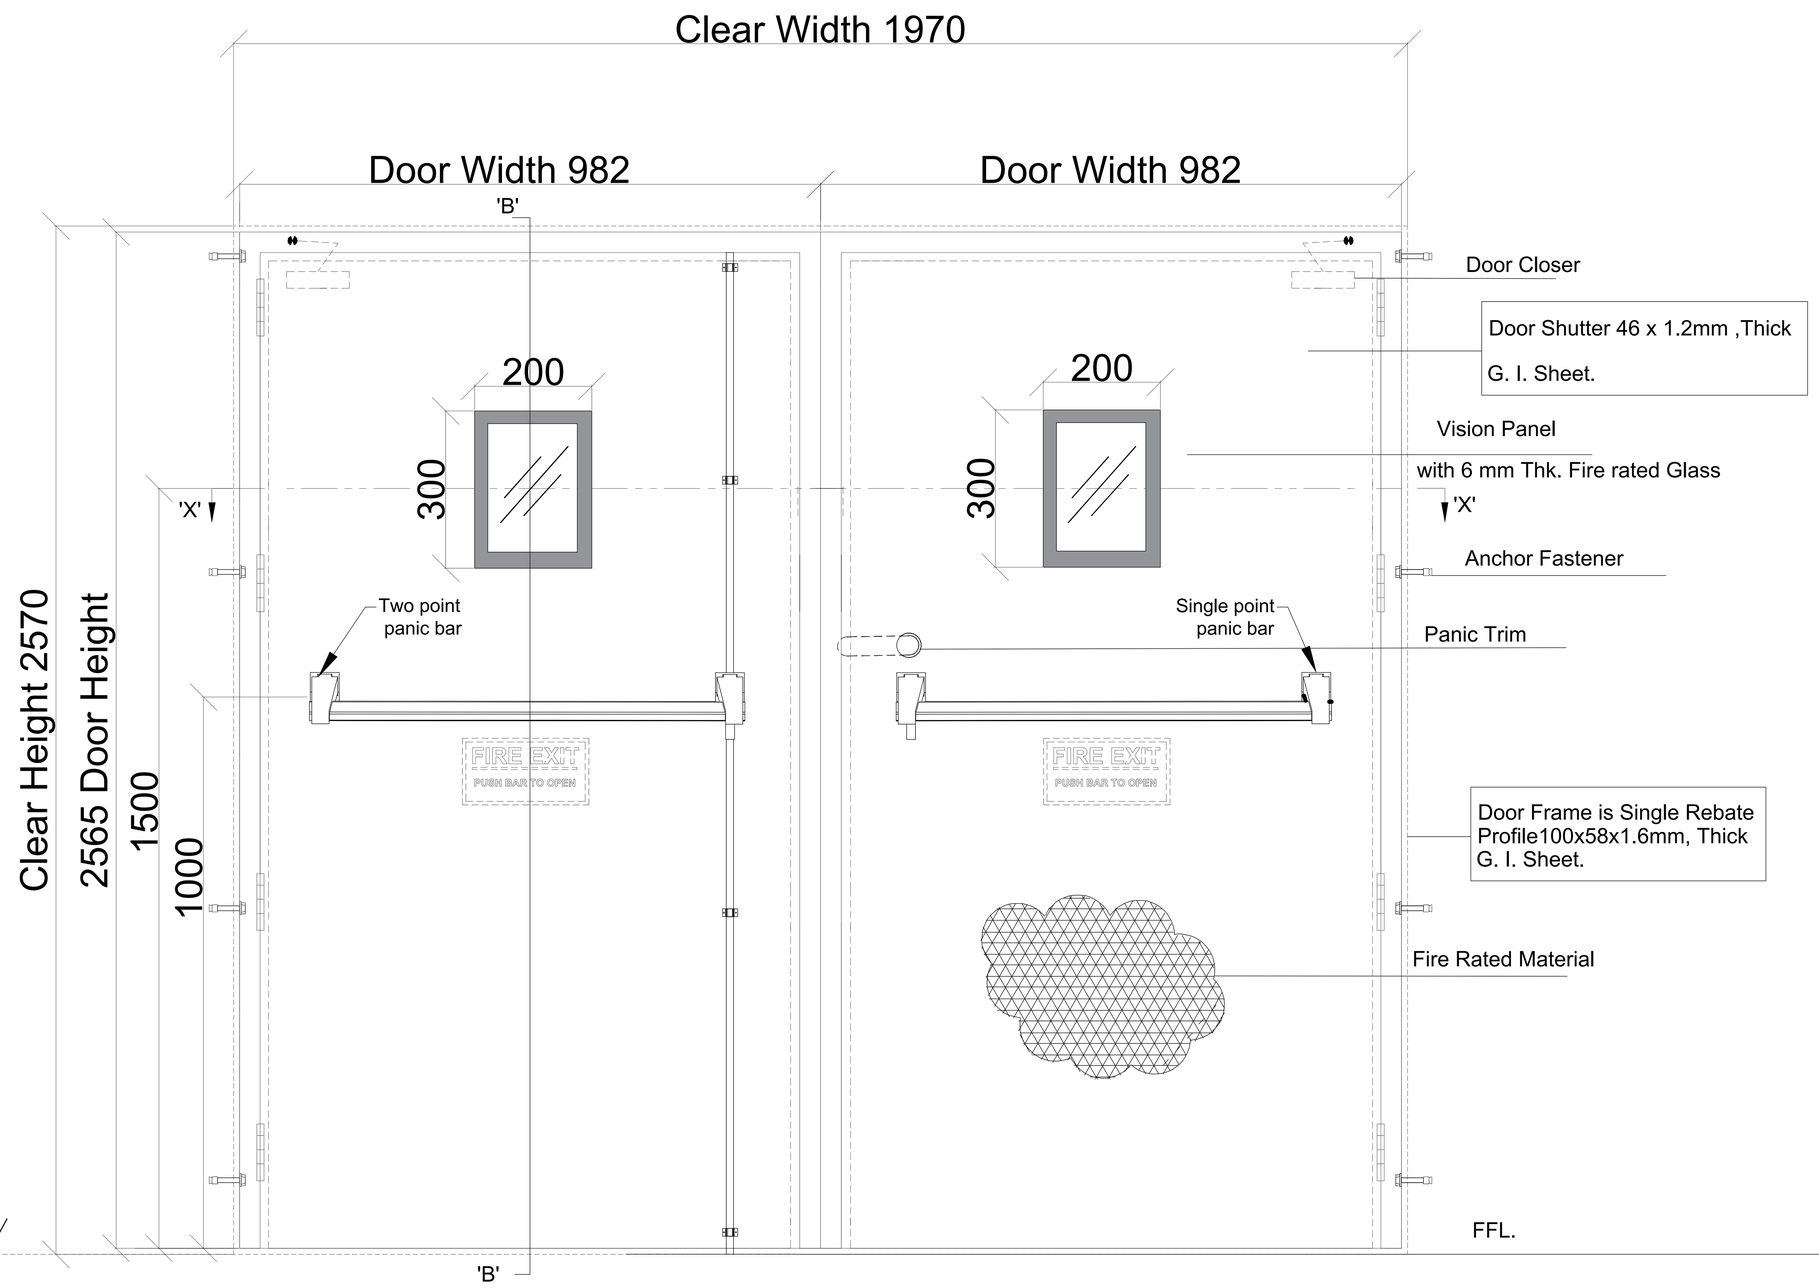

ELEVATION

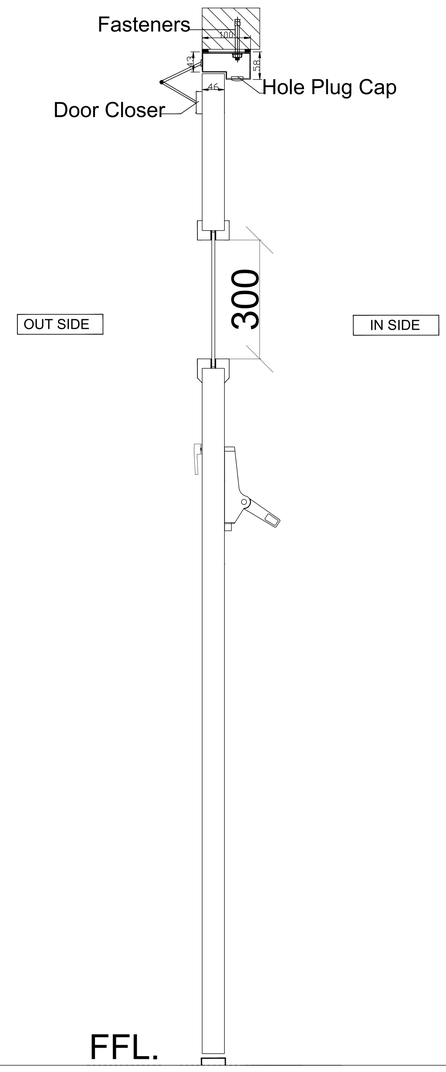

SECTION B-B

TECHNICAL SPECIFICATION :

Sr.	DESCRIPTION & DETAILS
01	Door frame - 100X58 mm x1.6mm thick G.I. Sheet
02	Door Shutter - 46 mm x1.2mm thick G.I. Sheet
03	SS Ball Bearing Hinges 4"x3"x3mm
04	Single Point Panic Bar
05	Tow Point Panic Bar
06	External Panic Trim
07	Anchor Fasteners (M10x100mm Dia)
08	Heavy Duty Door Closer (TS 1000)
09	Vision Window With 6mm fire Rated Glass
10	Fire Rating - 120 Minutes

Note :-

1. All Dimension are in mm
2. This drawing is only for understanding purpose
3. RAL code confirm by client

SIZE:

Sr.	Clear Width	Clear Height	Qty
01	1970	2570	01

This Drawing & Design is the property of NIHVA TECHNOLOGIES. Not to be sold or copied to any other concern.

TITLE :- FIRE DOOR

NAME	DATE	SIGN
S.J	03/10/2024	
S.W	03/10/2024	
V.T	03/10/2024	

NIHVA TECHNOLOGIES PVT. LTD. PUNE
NIHVA TECHNOLOGIES PVT. LTD.
Tel : 020 66304033
Email:- info@nihva.com
Website:- www.nihva.com

CLIENT - TATA Motor
LOCATION - CHICHWAD,PUNE
PRODUCT - FIRE DOOR | QTY-01
If any queries contact : design1@nihva.com | DWG NO - NIHVA/23-24/00XX | REV- 0
MENSION ARE IN mm | SCALE : NTS | SHEET : 01 OF 01