

THIS PRINT IS THE PROPERTY OF NIHVA IT IS TO BE USED ONLY FOR THE PURPOSE FOR WHICH IT WAS LENT AND MUST NOT BE USED IN ANY WAY DERTIMENTAL TO THE INTEREST OF THIS COMPANY AND IS SUBJECT TO RETURN ON DEMAND.

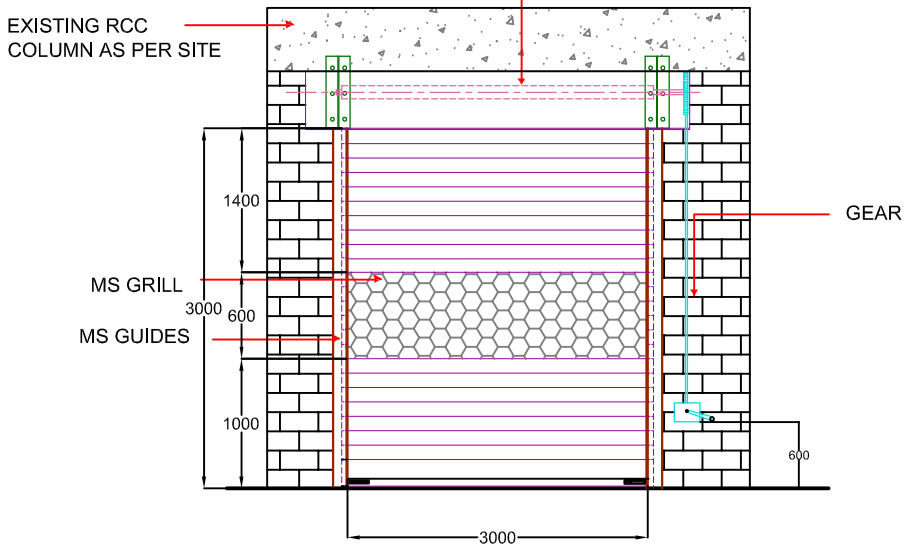


INSIDE ELEVATION


Clear Opening size:-
(W)3.0m x (H)3.0m

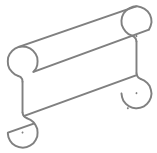


Box/Straight Type Slat Profile

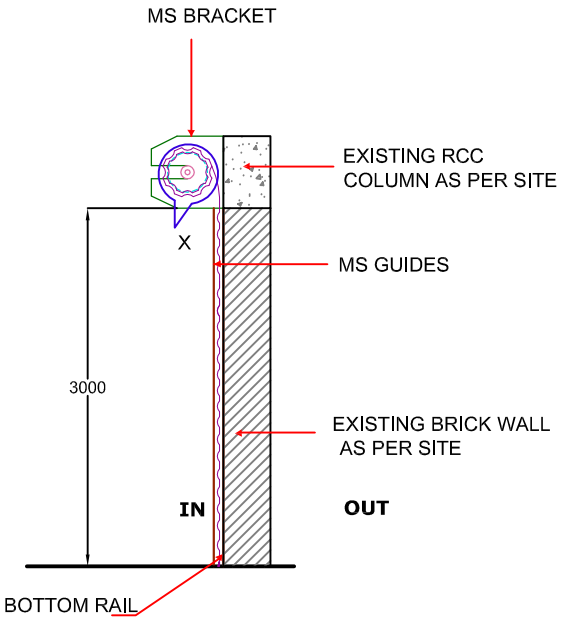


SIDE VIEW

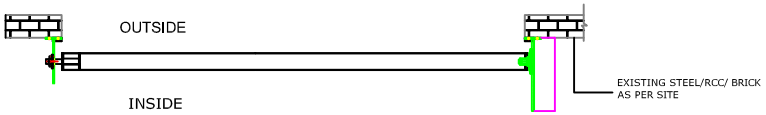

PLAN

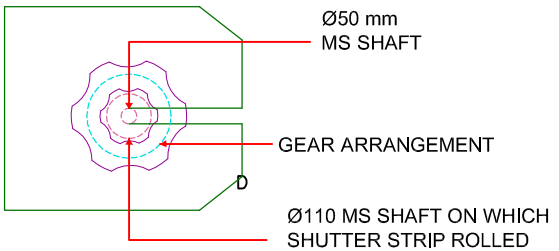

Bracket

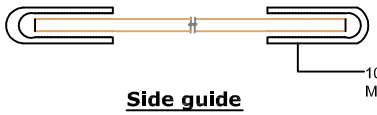

Side guide

Location :- 33 K.V Reciving station
Size :- 3.0m(W) X 3.0M (H)
Qty :- 03 nos
Type :- RS7-Partly grilled

TITLE: Manual Gear Operated Rolling Shutter	DO NOT SCALE DRAWING		NIHVA TECHNOLOGIES PVT. LTD. Pune:-411044 Tel :- 020 66304033 Email :- info@nihva.com
		SIGN	DATE	
CLIENTS APPROVEL:–	DRAWN	Anil		
	CHECK			CLIENT: Shapoorji Palonji Co. Ltd
	ENG			PROJECT / SITE: GE,CHAKAN
	APPRD.			PRODUCT NAME:
UNLESS & OTHERWISE SPECIFIED DIMENSION ARE IN M.M.	PROD			DWG. NO.: NVA/SP/04R
	MFG			REV.: 0
	Ref. No.			SCALE: NTS WT: SHEET: 1 OF 1