
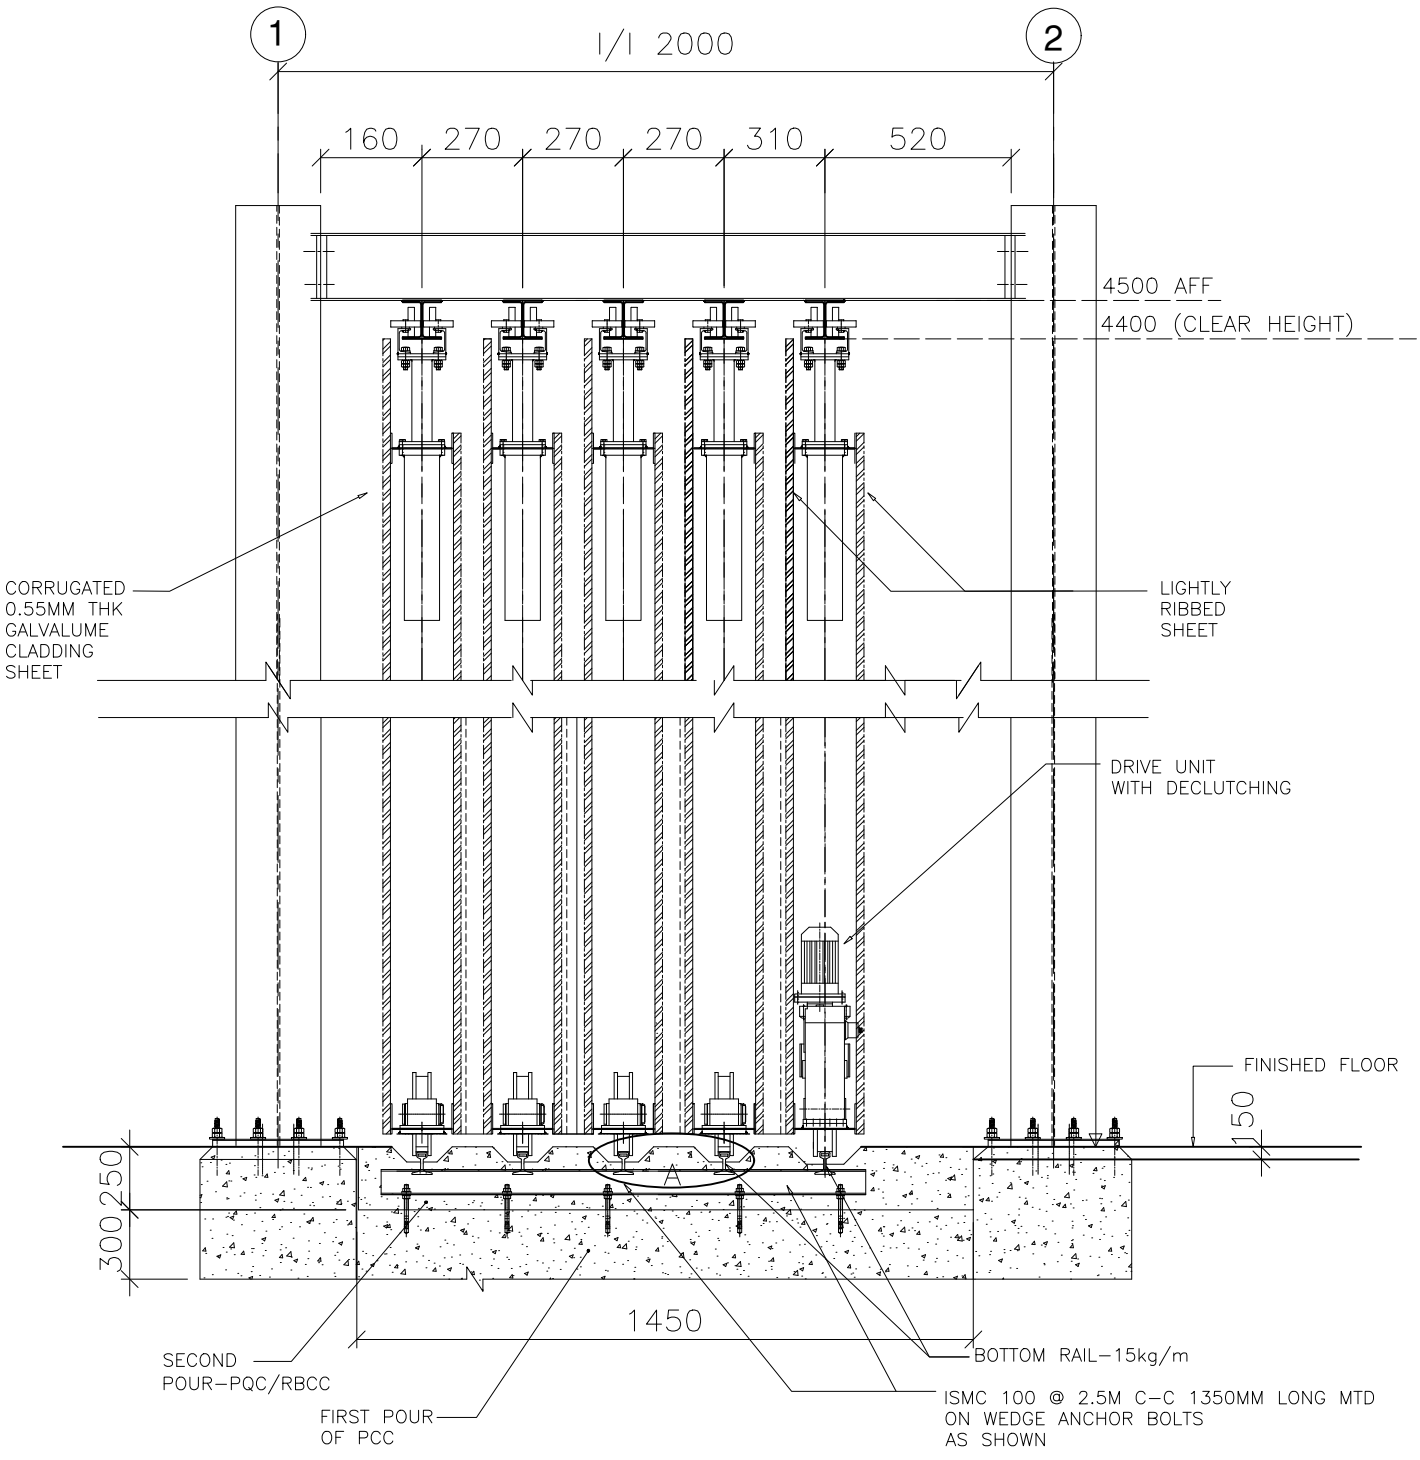


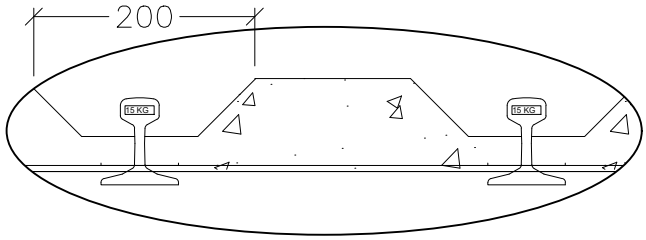

SECT. 'A - A'

NOTE:-

1.ALL DIMENSION ARE IN MM

2.BEAM & BOLTS SHALL BE SUPPLIED & INSTALLED BY IN NIHVA SCOPE

3.GAP BETWEEN THE RAIL AND FLOOR NEED TO FILLED BY CONCRETE DURING RAIL INSTALLATION AS SHOWN IN DESIGN.

Rev No.	Revision	Date	Revised By

This drawing & design is the property of NIHVA TECHNOLOGIES. Not to be sold or copied to any other concern.

TITLE:- FOUNDATION DRAWING

	NAME	DATE	SIGN
DRAWN	S.B	05/09/2023	
CHECK	A.K	05/09/2023	
APPRD.	V.T	05/09/2023	

If any queries contact : design1@nihva.com

ALL DIMENSION ARE IN mm

NIHVA TECHNOLOGIES PVT. LTD.

CLIENT - SHREE PRE FAB

LOCATION -HYDERABAD

PRODUCT - HANGER DOOR | QTY:-

DWG NO:-NIHVA/23-24/VDR/0140_HD_FD | REV- 00

SCALE: NTS | SCALE:-- 1:1 | SHEET: 01 OF 01