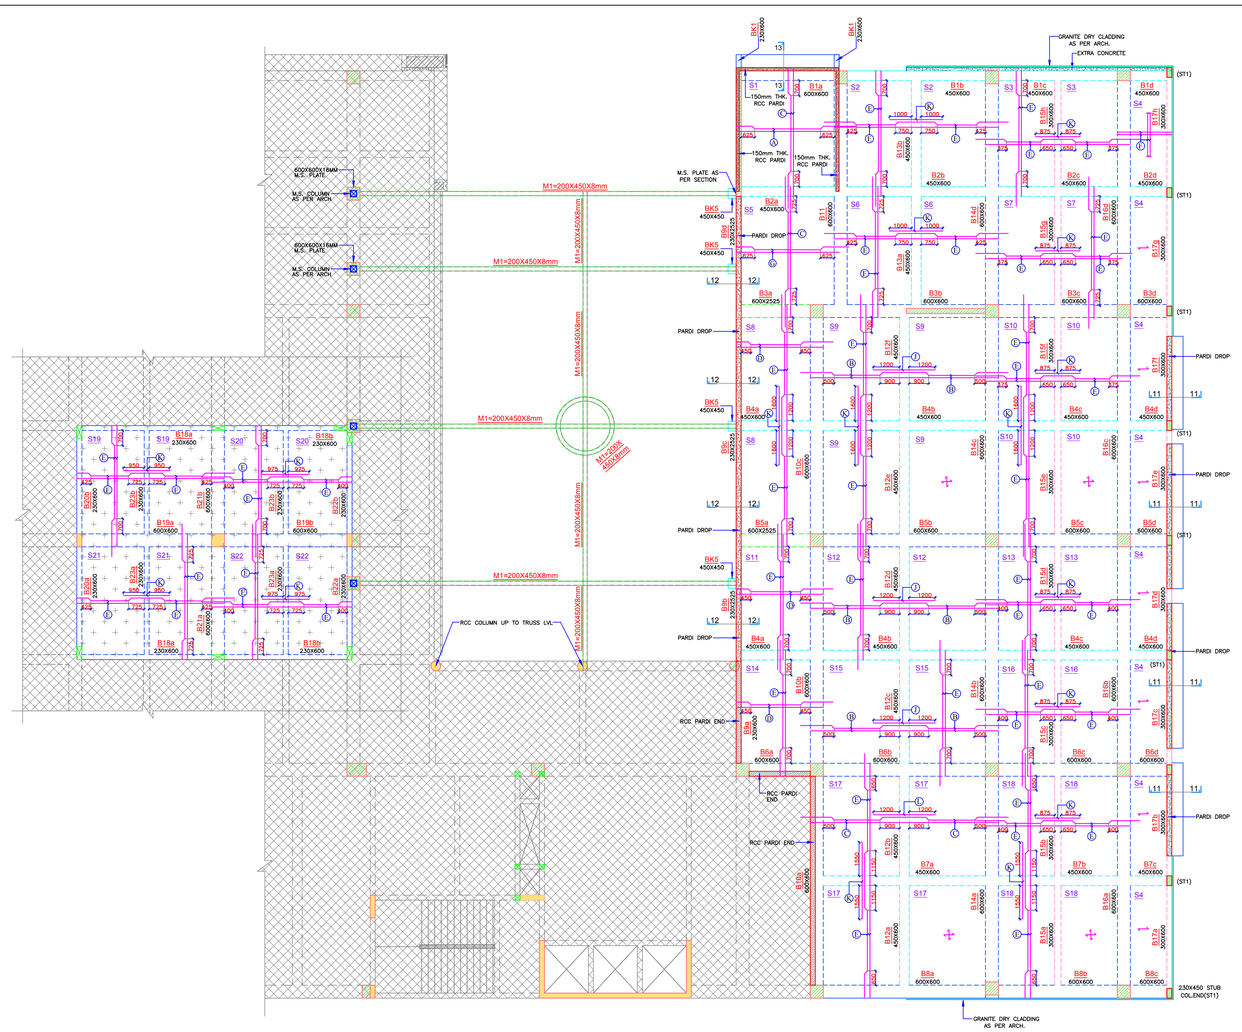


STRUCTURAL LAY OUT AT UPPER TERRACE SLAB LVL

NOTE:–ALL CENTER LINE DIMENSION SHALL BE CONFORM WITH ARCHITECT DRAWING.

* ALL SLABS THICKNESS ARE 150mm THK. UNLESS AND OTHERWISE SPECIFIED IN STRUCTURE LAYOUT
* SLAB BENT UP BAR EXTENDED UP TO DEVELOPMENT LENGTH.
* ALL SLEEVE LOCATION & MEP CUT–OUT AS PER MEP DRAWING.

THUS MARKED CUT OUT

THUS MARKED EXTRA CONC.

THUS MARKED BELOW TERRACE SLAB LVL

THUS MARKED COLUMN END AT THIS LVL

THUS MARKED SLAB LVL & BEAM AS PER ARCH

SCHEDULE OF SLAB R/F	
A	10T–150 c/c ALT BENT UP AT BOTTOM
B	8T–125 c/c ALT BENT UP AT BOTTOM
C	8T–150 c/c ALT BENT UP AT BOTTOM
D	8T–175 c/c ALT BENT UP AT BOTTOM
E	8T–200 c/c ALT BENT UP AT BOTTOM
F	8T–200 c/c STRAIGHT BAR
G	10T–100 c/c ALT BENT UP AT BOTTOM
J	10T–250 c/c EXTRA AT TOP
K	10T–400 c/c EXTRA AT TOP
L	10T–300 c/c EXTRA AT TOP

GENERAL NOTES:

1. REFER THIS DRAWING BEFORE REFER ANY STRUCTURAL DETAILS DRAWING & ALL DETAILS MUST BE AS PER THIS STANDARDS
2. EXCAVATION DETAILS FOLLOWED AS PER DRAWING.
3. WE SHALL NOT REMAIN RESPONSIBLE FOR.
   (A) CONCRETE MIX, QUALITY, SHUTTERING, CURING, SUBSTANDARD CONSTRUCTION MATERIAL, WORKMANSHIP & FAULTY CONSTRUCTION PROCEDURE.
   (B) SAFETY OF OLD STRUCTURE DURING DEMOLITION AND SAFETY OF ABATING STRUCTURE / BUILDING ANY ACCIDENT OCCURRING DUE TO CONSTRUCTION OF ELEMENT OF BUILDING NOT DESIGNED BY US.

KEY PLAN:

PRINTS ISSUED

Date	Rev.	Client	Site	Stru.	Plum.	Elec.	Office	Total	REMARK
07.12.22	R0	MAIL	MAIL	MAIL	MAIL	MAIL	MAIL	MAIL	FOR APP.
20.01.23	R0	MAIL		MAIL	MAIL	MAIL	MAIL	MAIL	G.F.C.

DESCRIPTION OF BUILDING:

Rev	Description	Date	Drawn	Checked

REVISIONS / ISSUE

THIS DRAWING MUST NOT BE REPRODUCED IN WHOLE OR IN PART WITHOUT THE PRIOR APPROVAL OF CONSULTANTS

CLIENT:

ADANI ESTATE MANAGEMENT PVT. LTD.
CBD, SHANTIGRAM, NR. VAISHNODEVI CIRCLE, S.G. HIGHWAY, AHMEDABAD 382421, GUJARAT, INDIA.

ARCHITECT:

274, MANEKBAUG SOCIETY, LANE NO: 22,
OPP. MANEKBAUG HALL, AMBAWADI, A'BAD-15.
PH: +91 79 26600903
EMAIL: design@adsapl.in

STRUCTURE CONSULTANT

P-CUBE CONSULTANTS LLP
A–1111, KP EPITOME, NEAR KATARIA ARCADE, MAKARBA, S.G.HIGHWAY AHMEDABAD–380051
MOBILE: 9925661341, 7435956798
EMAIL ID: contact@pcubeconsultants.com

MEP CONSULTANT:

MEPTech
Building Services...Building Confidence...
MEPTECH CONSULTANTS
Address : 904,Supath Building,opp Mc Donald's, 132' Ring Road,Vijay cross Road,Navrangpura, Ahmedabad-380009
Email : info@meptech.in
Web : www.meptech.in
Contact : 079-48011496

PROJECT:

RETAIL CENTRE ON PLOT-M14

DISCIPLINE:

STRUCTURAL

DRAWING TITLE:

STRUCTURAL LAY OUT AT UPPER TERRACE SLAB LVL

Project code	Discipline code	Drawing serial no.			Drawing revision no.		
N-EMACC02	C	6	0	1	R	0	0

Project Ref No.				
Original Scale 1:135	Drawn RAHUL	Checked PARTH	Authorised PARTH	
	Date: 12.03.22	Date: 12.03.22	Date: 12.03.22	34 X 24