

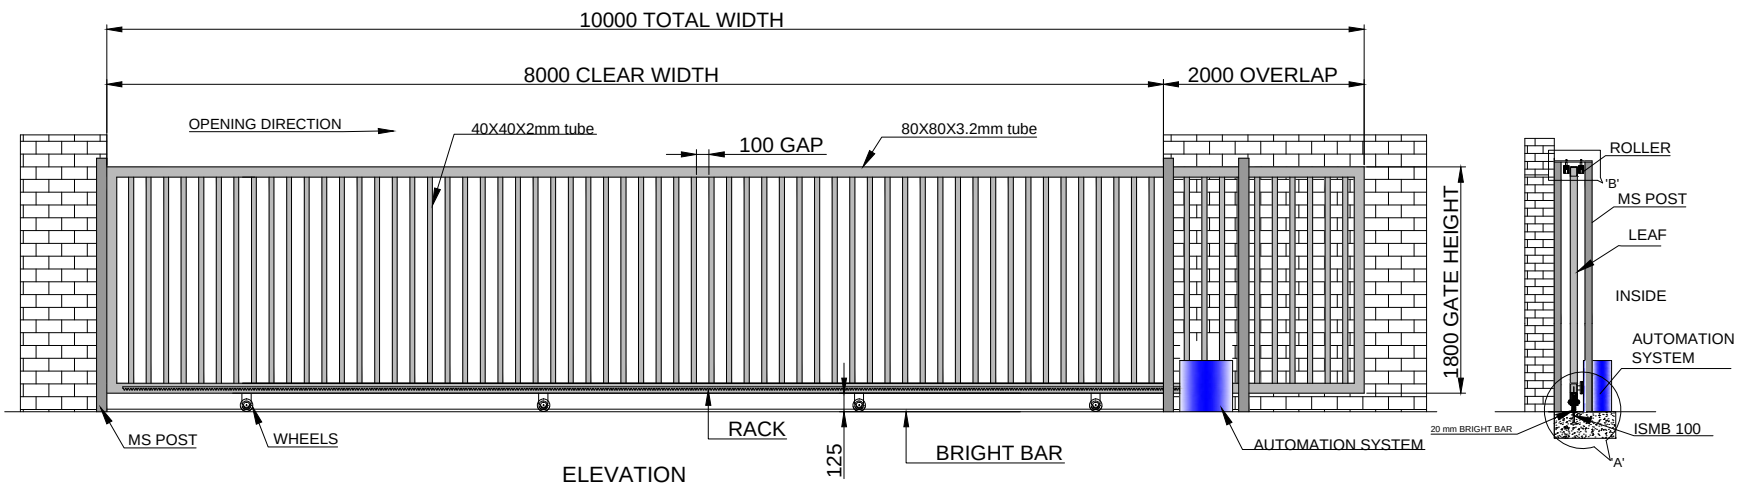



ELEVATION

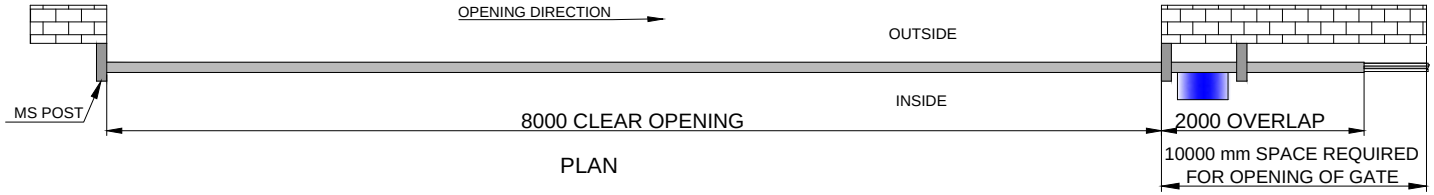

PLAN

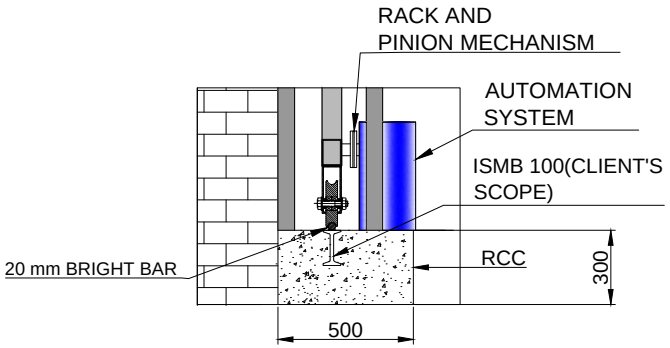

DETAIL VIEW OF A

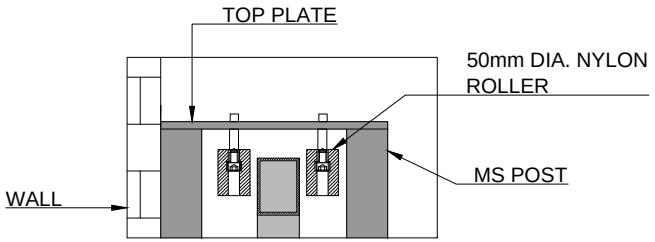

DETAIL VIEW OF B

SR NO	TUBE SPECIFICATION	
1	80X80X3.2mm	OUTER FRAME
2	40X40X2mm	INNER PATTERN
3	80X80X3.2mm	FOR MS POST

TOTAL NO OF POST ARE 5.

TOLERANCE- ±10mm

CLEAR WIDTH	CLEAR HEIGHT	QUANTITY	LOCATION
8000mm	1800mm	1 NOS	MAIN ENTRANCE TO LPC
8000mm	1800mm	1 NOS	MAIN ENTRANCE TO FACTORY

DIMENSION :

CLEAR WIDTH	CLEAR HEIGHT	QUANTITY
8000mm	1800mm	2 NOS

MATERIAL:

THICKNESS :

NOTE-
1. ALL REQUIRED CIVIL WORK WILL BE IN CLIENTS SCOPE.
2. ONE COAT OF RED OXIDE & TWO COAT OF APPROVED RAL SHADE WILL BE GIVEN TO THE GATE.
3.GATE LEAF WILL BE IN TWO PARTS FOR TRANSPORTATION & WILL BE WELD TOGETHER ON SITE.

NIHVA TECHNOLOGIES PVT. LTD.
NIHVA TECHNOLOGIES PVT. LTD. PUNE
Email:- info@nihva.com
Website:- www.nihva.com

TITLE:

AUTOMATIC SINGLE LEAF SLIDING GATE

CLIENT'S APPROVAL :

CLIENT - TATA PROJECTS LIMITED

PROJECT - ALSTOM

SITE LOCATION -MADHEPURA,BIHAR

DWG. NO. : NIHVA/17-18/0078

SCALE: NTS	WT:	SHEET:1 OF 1

DRAWN BY: SURAJ	DATE: 17-05-2017
CHECK BY : SAGAR P	DATE: 17-05-2017
APPROVED BY : S.S	DATE: 17-05-2017

If any queries contact : projects@nihva.com

NOTE: ALL DIMENSIONS ARE IN mm

THIS DRAWING & DESIGN IS THE PROPERTY OF NIHVA TECHNOLOGIES. NOT TO BE SOLD OR COPIED TO ANY OTHER CONCERN.