


DRAWING

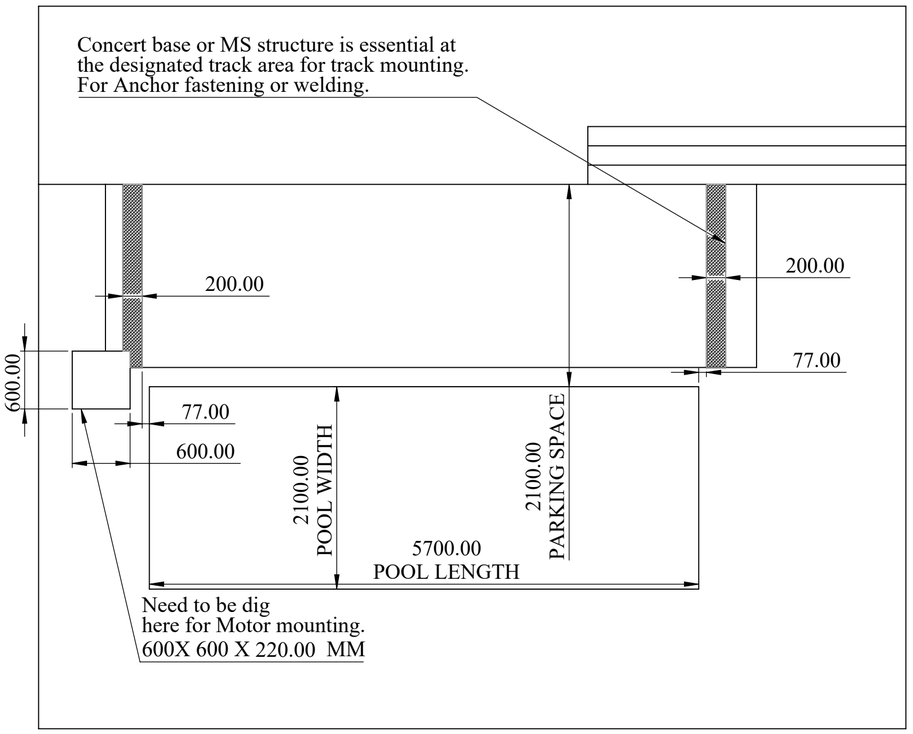


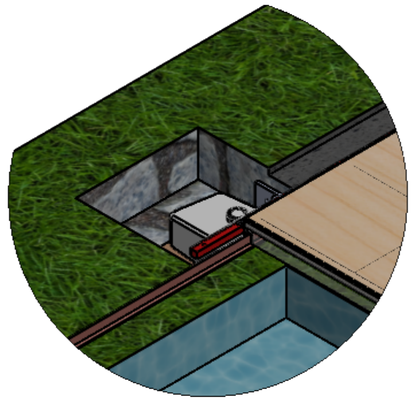


DETAIL G
SCALE 1 : 15

MOTOR ARRANGEMENT

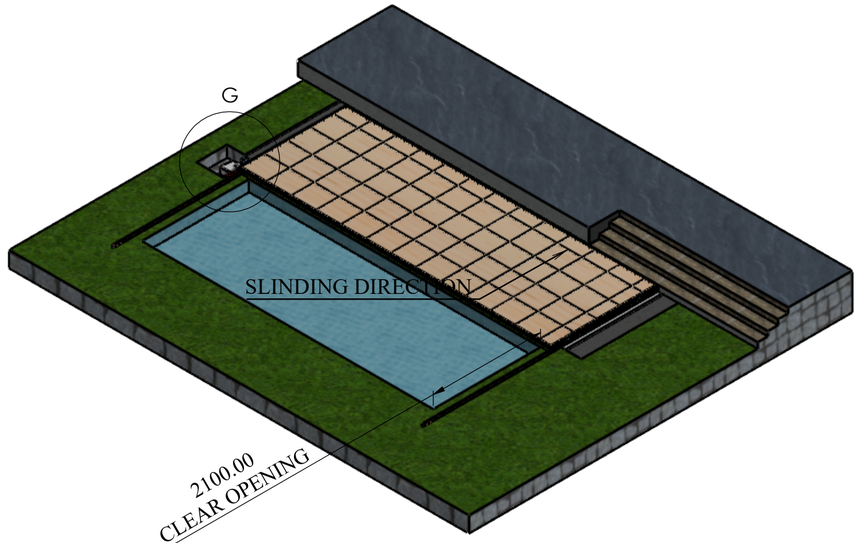

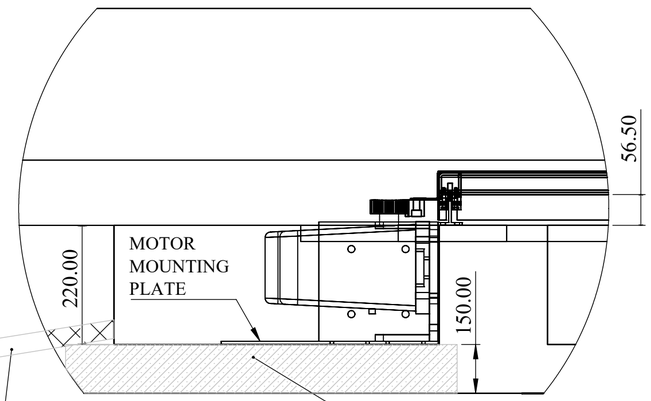

DETAIL K
SCALE 1 : 8

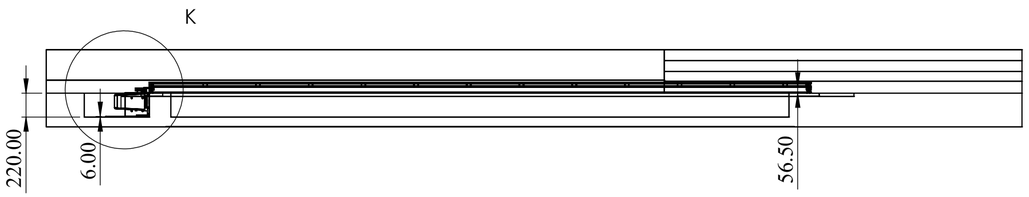

REV DESCRIPTION	DATE	REV NO
	25-07-2025	REV 00
1.		

NOTE :

All civil work is under the end client scope.

SPECIAL INSTRUCTION'S :

TITLE - SWIMMING POOL ENCLOSER				NIHVA Technologies Pvt. Ltd.	NIHVA TECHNOLOGIES PVT.LTD.PUNE Website - www.nihva.com
DWG NO - NTPL-000-PM-001-00-00-00				PRODUCT - SWIMMING POOL DECK	
	NAME	SIGNATURE	DATE	PROJECT NO - NTPL-000-PM	REVISION - 00
DRAWN	V.W.		25-07-2025	SITE LOCATION -	WEIGHT -
CHK'D	P.M.		27-07-2025	MATRIAL -	QTY - 1
APPV'D	V.T.		27-07-2025	PROJECTION METHOD:	SCALE :
If any queries contact - design.nihva@gmail.com					SHEET 2 OF 2
ALL DIMENSION ARE IN mm			A2		