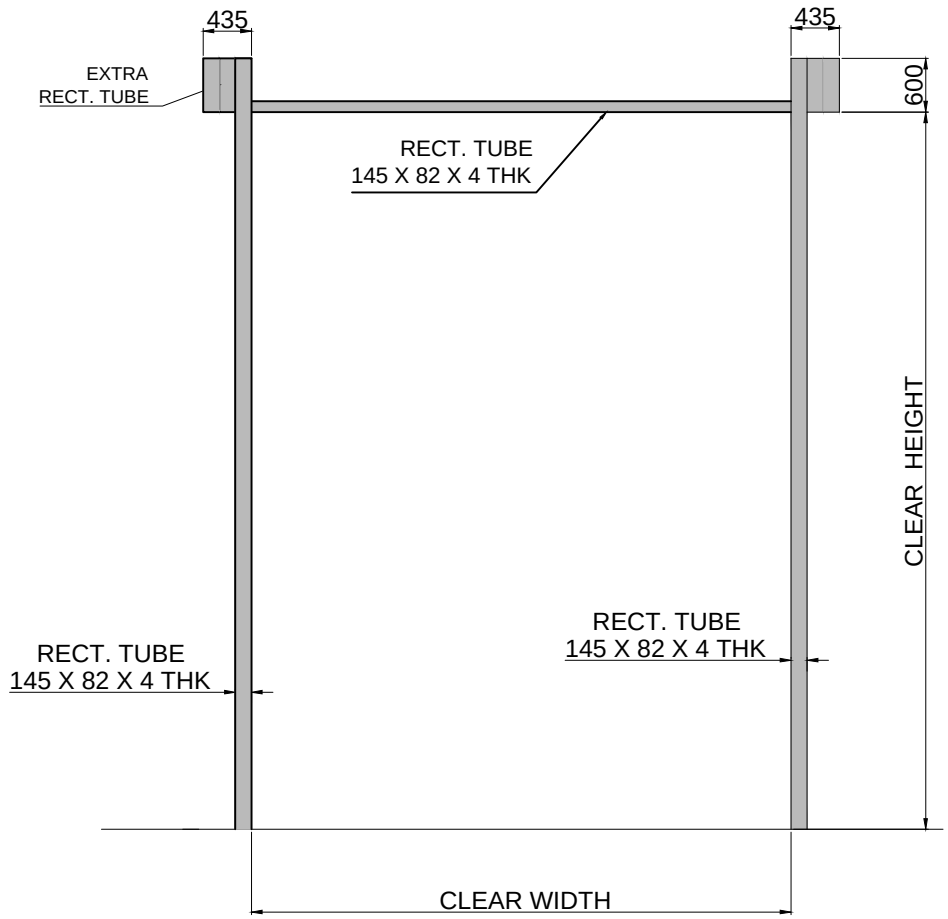


CLEAR WIDTH	CLEAR HEIGHT	QTY.
4000mm	5000mm	01 NO

TOLERANCE - ±10mm

NOTE :

1. MATERIAL FOR ALL STRUCTURE = M.S
2. CIVIL WORK & M.S STRUCTURE WILL BE IN CLIENT SCOPE

This drawing & design is the property of NIHVA TECHNOLOGIES. Not to be sold or copied to any other concern.

TITLE
STRUCTURE FOR MOTORIZED OPERATED ROLLING SHUTTER

	NAME	SIGN	DATE
DRAWN	P.V.A		25.09.2019
CHECK	G.J		25.09.2019
APPRD.			

If any queries contact : design@nihva.com

ALL DIMENSION ARE IN mm

NIHVA
NIHVA TECHNOLOGIES PVT. LTD.
NIHVA TECHNOLOGIES PVT. LTD. PUNE
Tel : 020 66304033
Email:- info@nihva.com
Website:- www.nihva.com

CLIENT - HIRANANDANI

PROJECT-

SITE LOCATION - TALEGAON

DWG. NO. : NIHVA/19-20/0102 | REV- 00

SCALE: NTS | WT: | SHEET: 01 OF 01