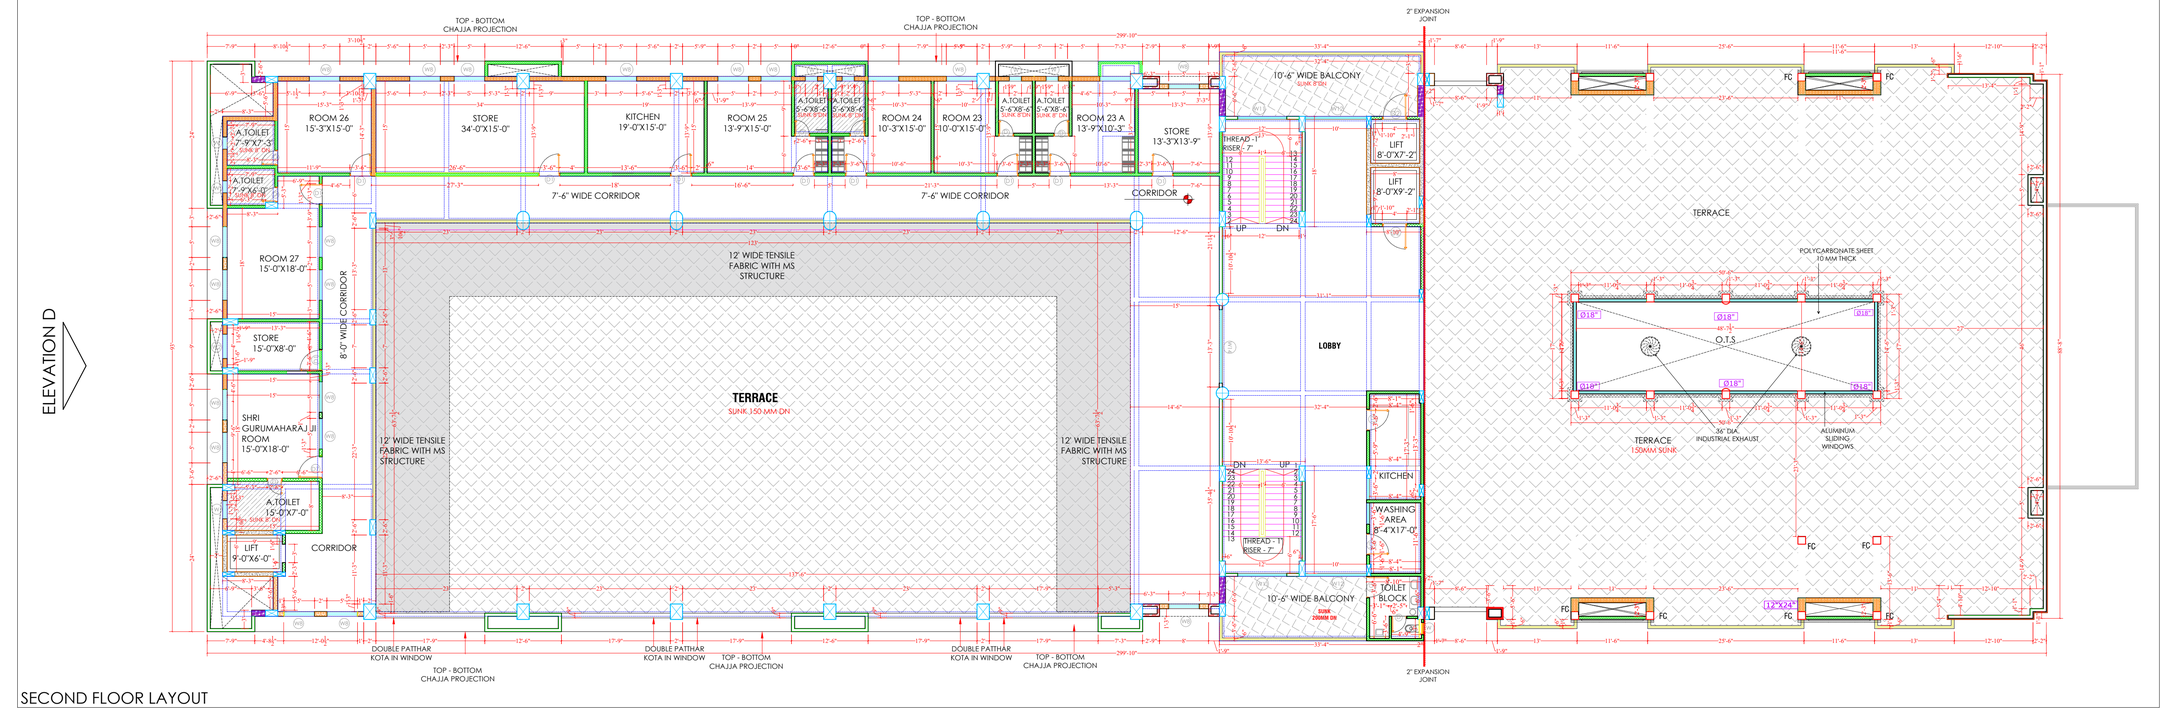
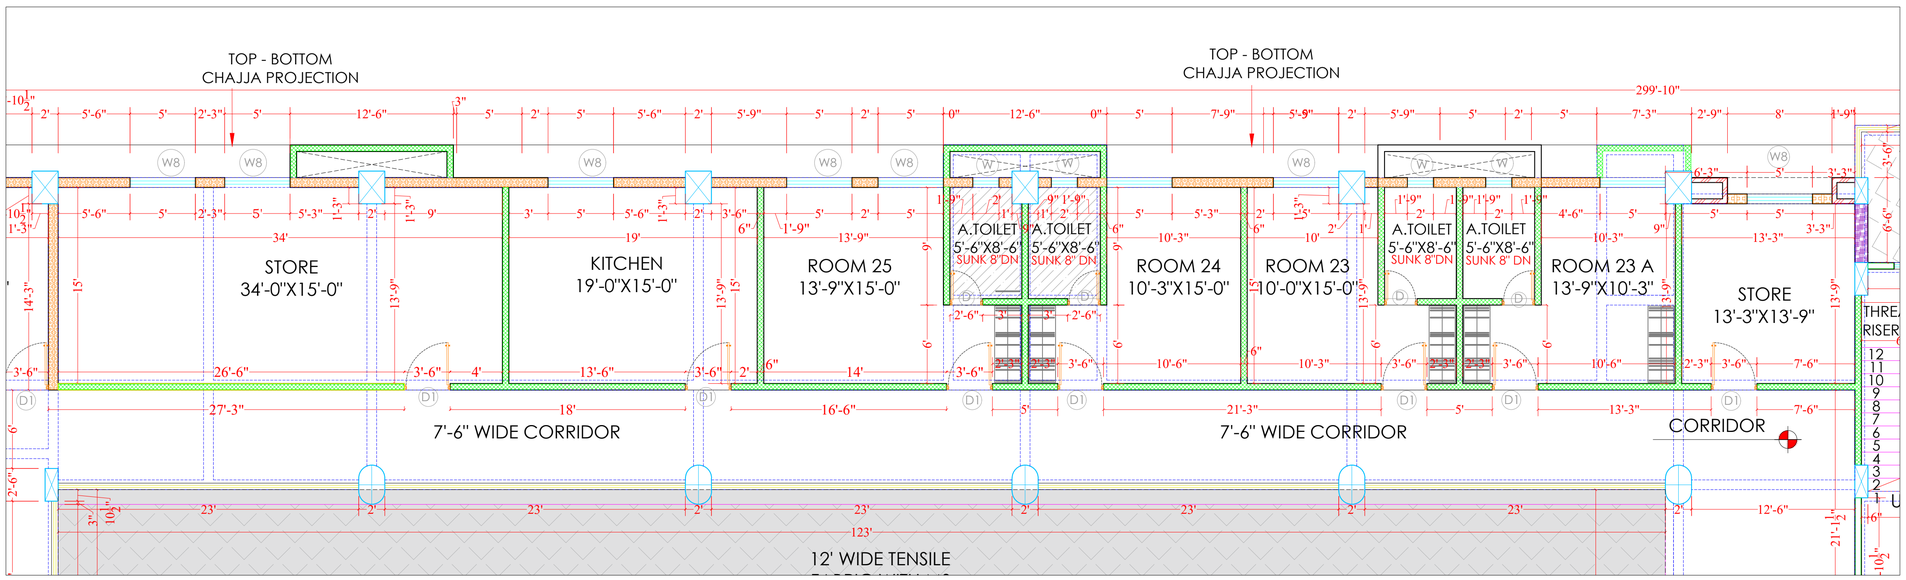
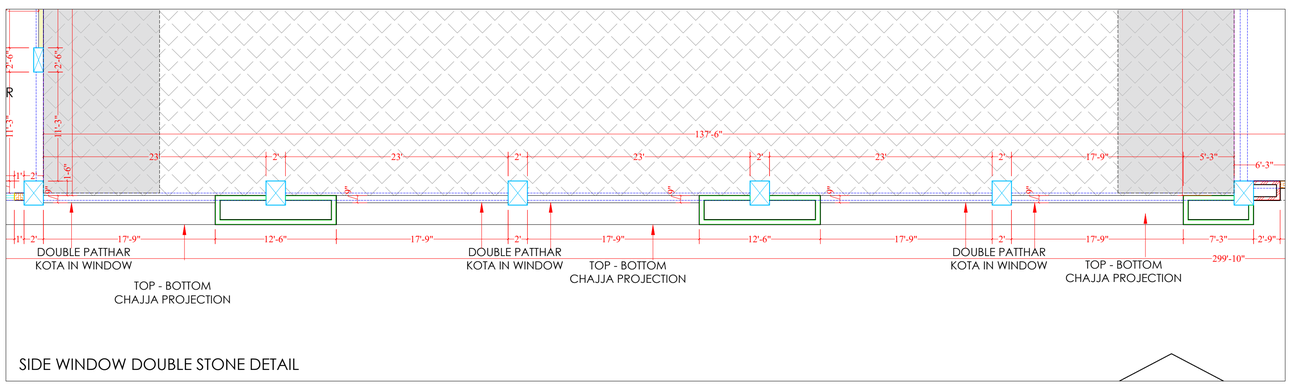


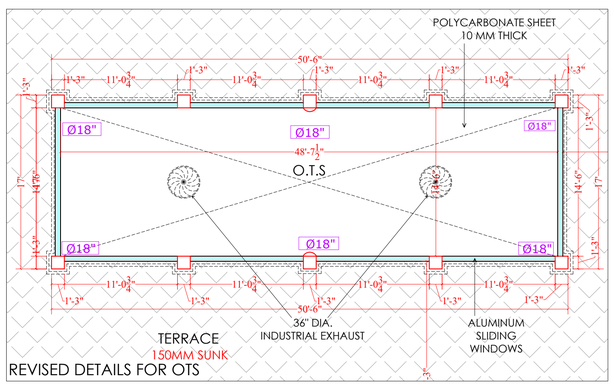

SECOND FLOOR LAYOUT



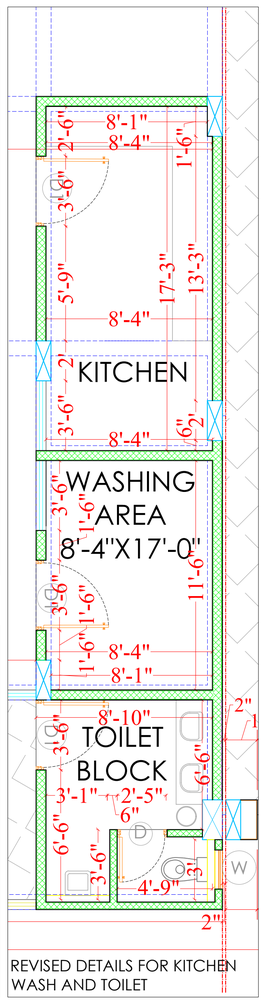

REVISED LAYOUT FOR ROOMS, KITCHEN AND STORE




SIDE WINDOW DOUBLE STONE DETAIL




REVISED DETAILS FOR OTS




REVISED DETAILS FOR KITCHEN WASH AND TOILET

# SECOND FLOOR PLAN

## GENERAL NOTES :

1. ALL DIMENSIONS ARE IN MM.
2. DRAWINGS ARE NOT TO BE SCALED AND ONLY WRITTEN DIMENSIONS ARE TO BE FOLLOWED.
3. ALL DIMENSIONS ARE FROM UNFINISHED TO UNFINISHED SURFACES.
4. ALL LEVELS ARE UNFINISHED LEVELS.

## LEGEND

| | |
|---|---|
| | 4" WALL |
| | 4½" WALL |
| | 6" WALL |
| | 9" WALL |
| | 1' WALL |
| | RCC WALL |
| | WATER PROOFING |
| | 6" SUNK |
| | 9" SUNK |
| | STONE CLADDING |

## DOOR SCHEDULE :

| NO. | SIZE | SPECIFICATIONS |
|---|---|---|
| D | 2'6" x 7' | |
| D1 | 3'3" x 7' | |
| D2 | 4' x 7' | |
| D3 | 7'6" x 7' | |
| D4 | 8' x 7' | |
| D5 | 14'6" x 7' | |
| D6 | 5'9" x 7' | |
| D7 | 3'-6" x 7' | |
| D8 | 10'-0" x 13' | |

## WINDOW SCHEDULE :

| NO. | SIZE | CILL HT. | SPECIFICATIONS |
|---|---|---|---|
| W | 3' x 3' | 4' | |
| W1 | 3' x 5' | 3' | |
| W2 | 4' x 5' | 3' | |
| W3 | 7' x 5' | 3' | |
| W4 | 8' x 5' | 3' | |
| W5 | 8'6" x 5' | 3' | |
| W6 | 9'9" x 10' | | |
| W7 | 10' x 5' | 3' | |
| W8 | 5' x 4' | 3' | |
| W9 | 14'2" x 8' | | |
| W10 | 8' x 3' | 3' | |
| W11 | 8'0" x 5' | 3' | |
| W12 | 10' x 8' | | |
| W13 | 5' x 8' | | |
| W14 | 12' x 8' | | |
| W15 | 9'9" x 5' | 3' | |

| | |
|---|---|
| ☐ FOR ESTIMATE | ☐ FOR APPROVAL/CHECKING |
| ■ ADVANCE COPY | ☐ FOR MUNICIPAL SUBMISSION |
| ☐ FOR INFORMATION | ☐ VALID FOR CONSTRUCTION |

| REVISION NO. | DESCRIPTION |
|---|---|
| | |

☐ PROJECT TITLE

ASHRAM AT KOLHAPUR (MOHAN AHUJA )

☐ DRAWING TITLE

SECOND FLOOR PLAN R4

| | |
|---|---|
| ☐ DRAWN BY : | |
| ☐ CHECKED BY : | |
| ☐ DRAWING NO : | |
| ☐ DATE : 20.06.2022 | ☐ NORTH : |
| ☐ SCALE : N.T.S. | |


ALMAK
PROJECT MANAGEMENT & AUDIT CONSULTANTS
AN ISO-9001-2015 CERTIFIED ORGANIZATION
Regd.Office: 1201/23, SHAKTI NAGAR SOCIETY,NR.MOTHERS SCHOOL,GOTRI ROAD,VADODARA-390021,GUJARAT.
Head.Office: 1, ASHRAY, B/H LINDE ENGG., NILAMBER CIRCLE, SAIYAD VASNA, VADODARA - 390007, GUJARAT.
CONTACT : + 91 7573026650, + 917573026640
E-MAIL: info@almak.in WEB: www.almak.in


☐ STAMP & SIGN: