



RECT. TUBE 40 X 60 X 1.6

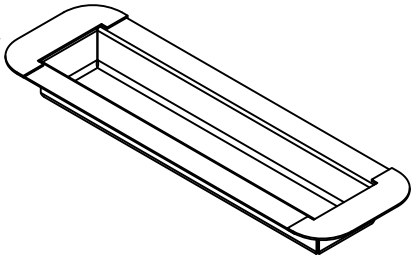

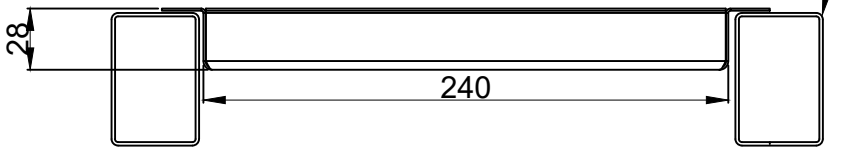

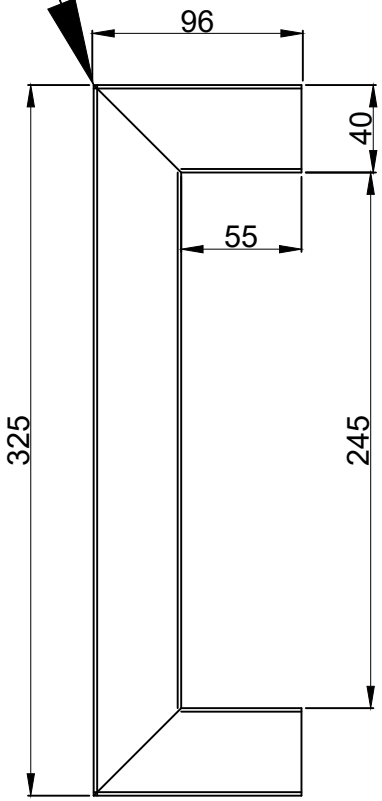

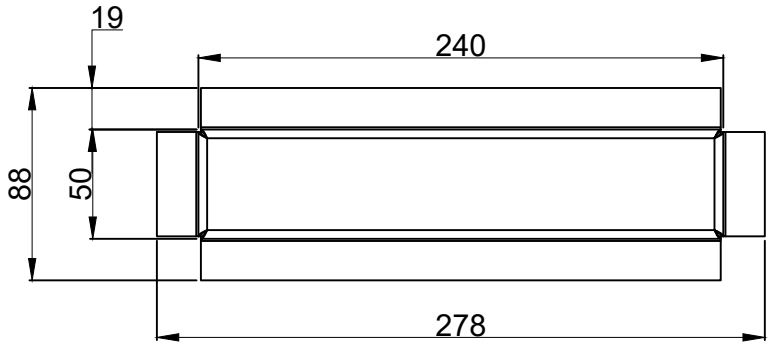

QTY . 25 NOS.

SS SHEET 1.2 MM

This drawing & design is the property of NIHVA TECHNOLOGIES. Not to be sold or copied to any other concern.

TITLE:- SS HANDLE BRACKET CRM DOOR

NIHVA TECHNOLOGIES PVT. LTD. PUNE
Tel : 020 66304033
Email:- info@nihva.com
Website:- www.nihva.com

	NAME	DATE	SIGN
DRAWN	M.SUTAR	23/05/2022	
CHECK	M.SUTAR	23/05/2022	
APPRD.			

If any queries contact : design@nihva.com

ALL DIMENSION ARE IN mm

CLIENT - NIHVA TECHNOLOGIES PVT.LTD

LOCATION -

PRODUCT - SLIDING DOOR - PPGI CLADDING

DWG NO:-NIHVA/22-23/MNFG/0015 REV- 0

SCALE: NTS SCALE:-- 1:1 SHEET: 02 OF 02

REV.	REVISION DESCRIPTION	Date	Revised By
000	RELEASED FOR PRODUCTION	23/05/2022	MAHESH S.

