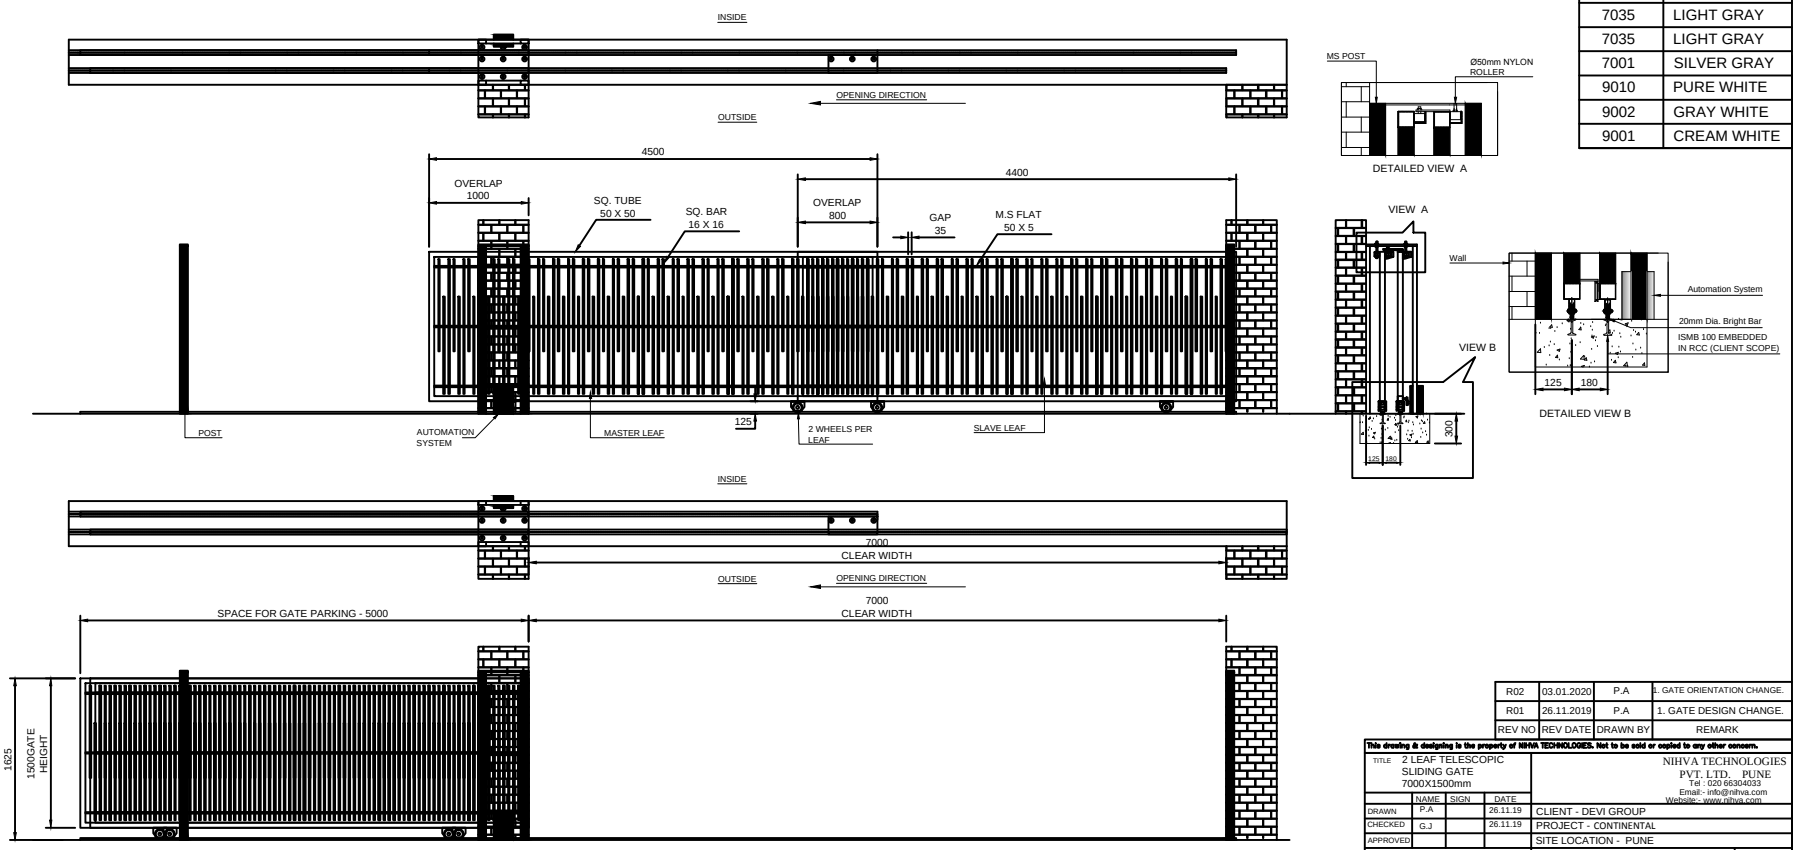


RAL CODE	COLOR SHADE
7035	LIGHT GRAY
7035	LIGHT GRAY
7001	SILVER GRAY
9010	PURE WHITE
9002	GRAY WHITE
9001	CREAM WHITE

REV NO	REV DATE	DRAWN BY	REMARK
R02	03.01.2020	P.A	1. GATE ORIENTATION CHANGE.
R01	26.11.2019	P.A	1. GATE DESIGN CHANGE.

This drawing & designing is the property of NIHVA TECHNOLOGIES. Not to be sold or copied to any other concern.

TITLE: 2 LEAF TELESCOPIC SLIDING GATE 7000X1500mm

NIHVA TECHNOLOGIES PVT. LTD. PUNE
Tel : 020 66304033
Email:- info@nihva.com
Website:- www.nihva.com

	NAME	SIGN	DATE
DRAWN	P.A		26.11.19
CHECKED	G.J		26.11.19
APPROVED			

CLIENT - DEVI GROUP
PROJECT - CONTINENTAL
SITE LOCATION - PUNE
DWG. NO. : NIHVA/19-20/0158/R02 | REV: R02
SCALE: NTS | WT: | SHEET: 01 OF 01

If any queries contact : projects@nihva.com
ALL DIMENSION ARE IN mm