




This drawing & design is the property of NIHVA TECHNOLOGIES Not to be sold or copied to any other concern			
TITLE:- STRUCTURAL DRAWING FOR DOOR FRAME	NIHVA TECHNOLOGIES PVT. LTD.		
	NIHVA TECHNOLOGIES PVT. LTD. PUNE Tel : 020 66304033 Email:- info@nihva.com Website:- www.nihva.com		
	NAME	DATE	SIGN
DRAWN	MAHESH S.	19/08/2022	
CHECK	MAHESH S.	19/08/2022	
APPRD.	AMIT K.	19/08/2022	
CLIENT - NIHVA TECHNOLOGIES PVT LTD			
LOCATION - PUNE			
PRODUCT - STRUCTURAL DRAWING FOR DOOR FRAME			
If any queries contact : design@nihva.com		DWG NO:- NIHVA/22-23/VDR/0070	REV- 0
ALL DIMENSION ARE IN mm		SCALE:NTS	SHEET:01 OF 01

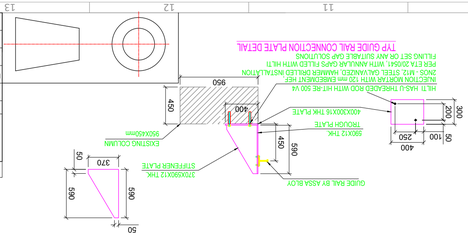


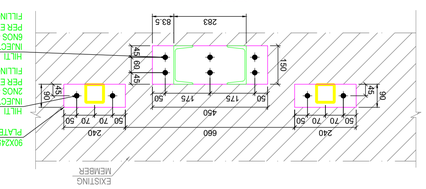


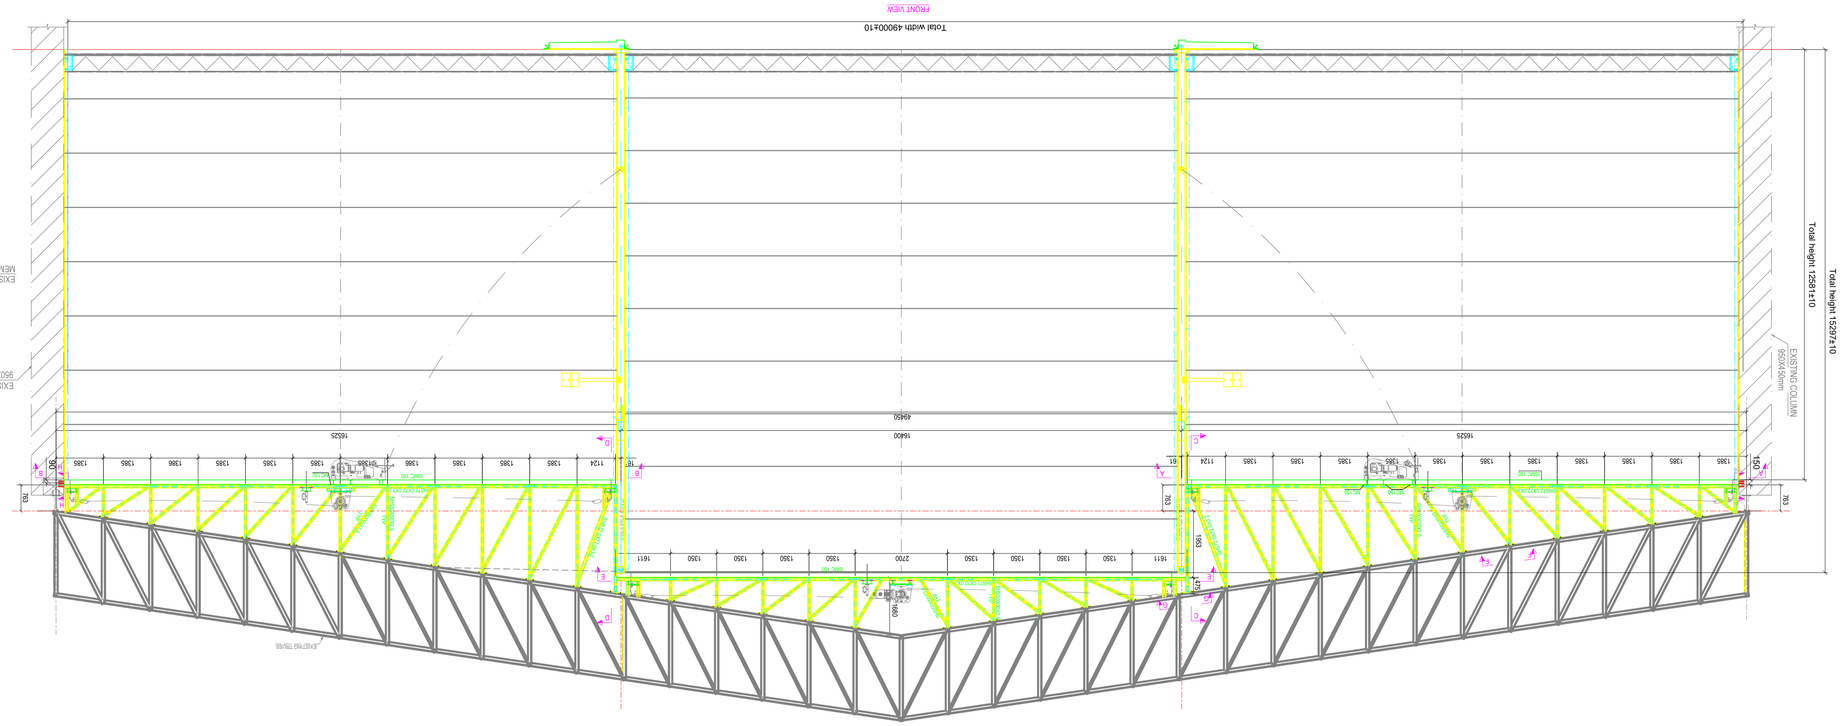


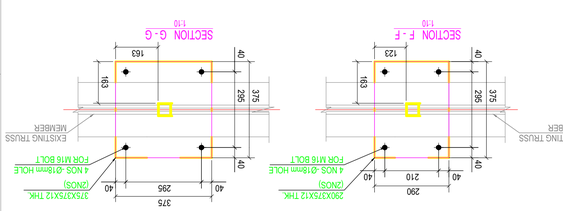


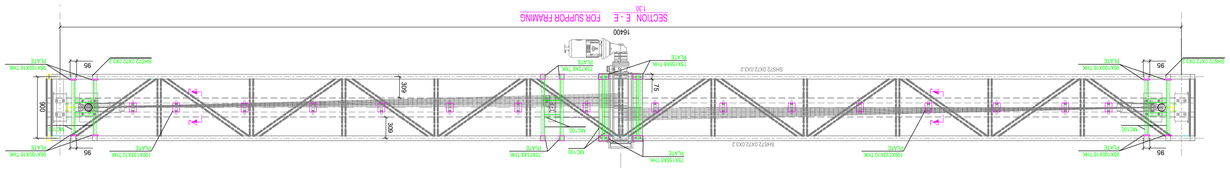


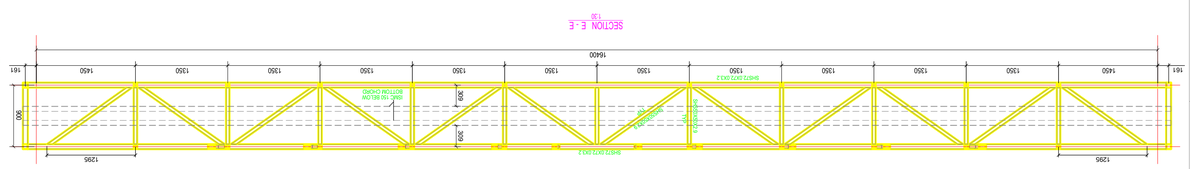

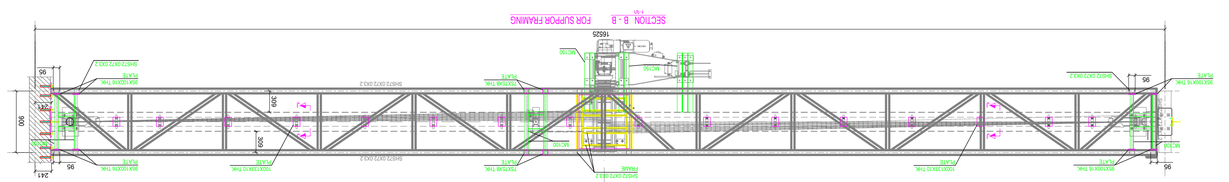

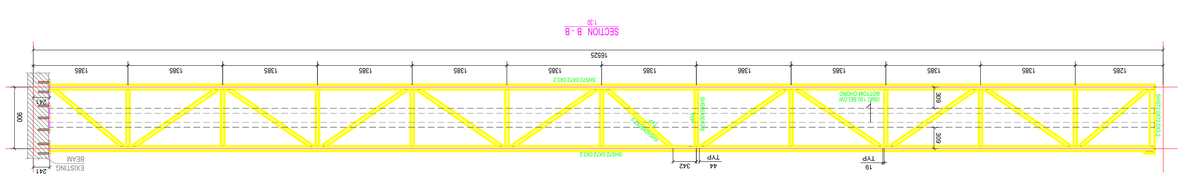

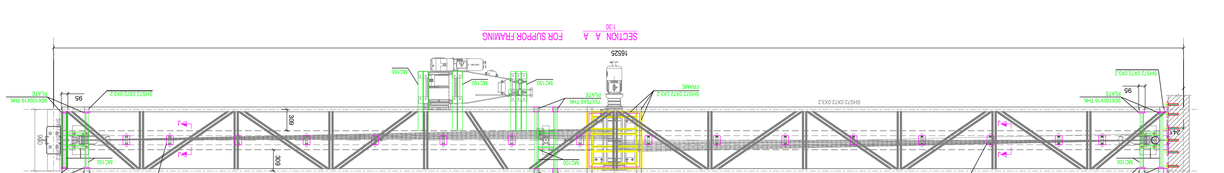

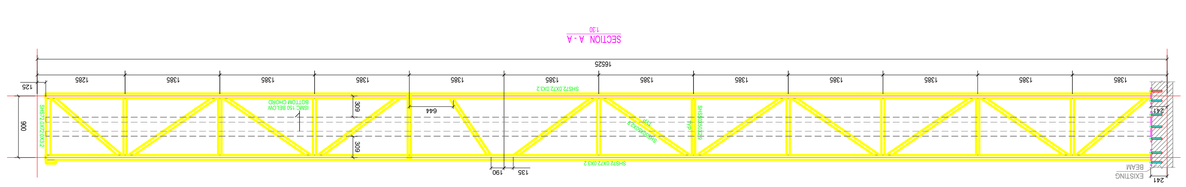

DWG.NO: SALT_1714_STR_01_R0