

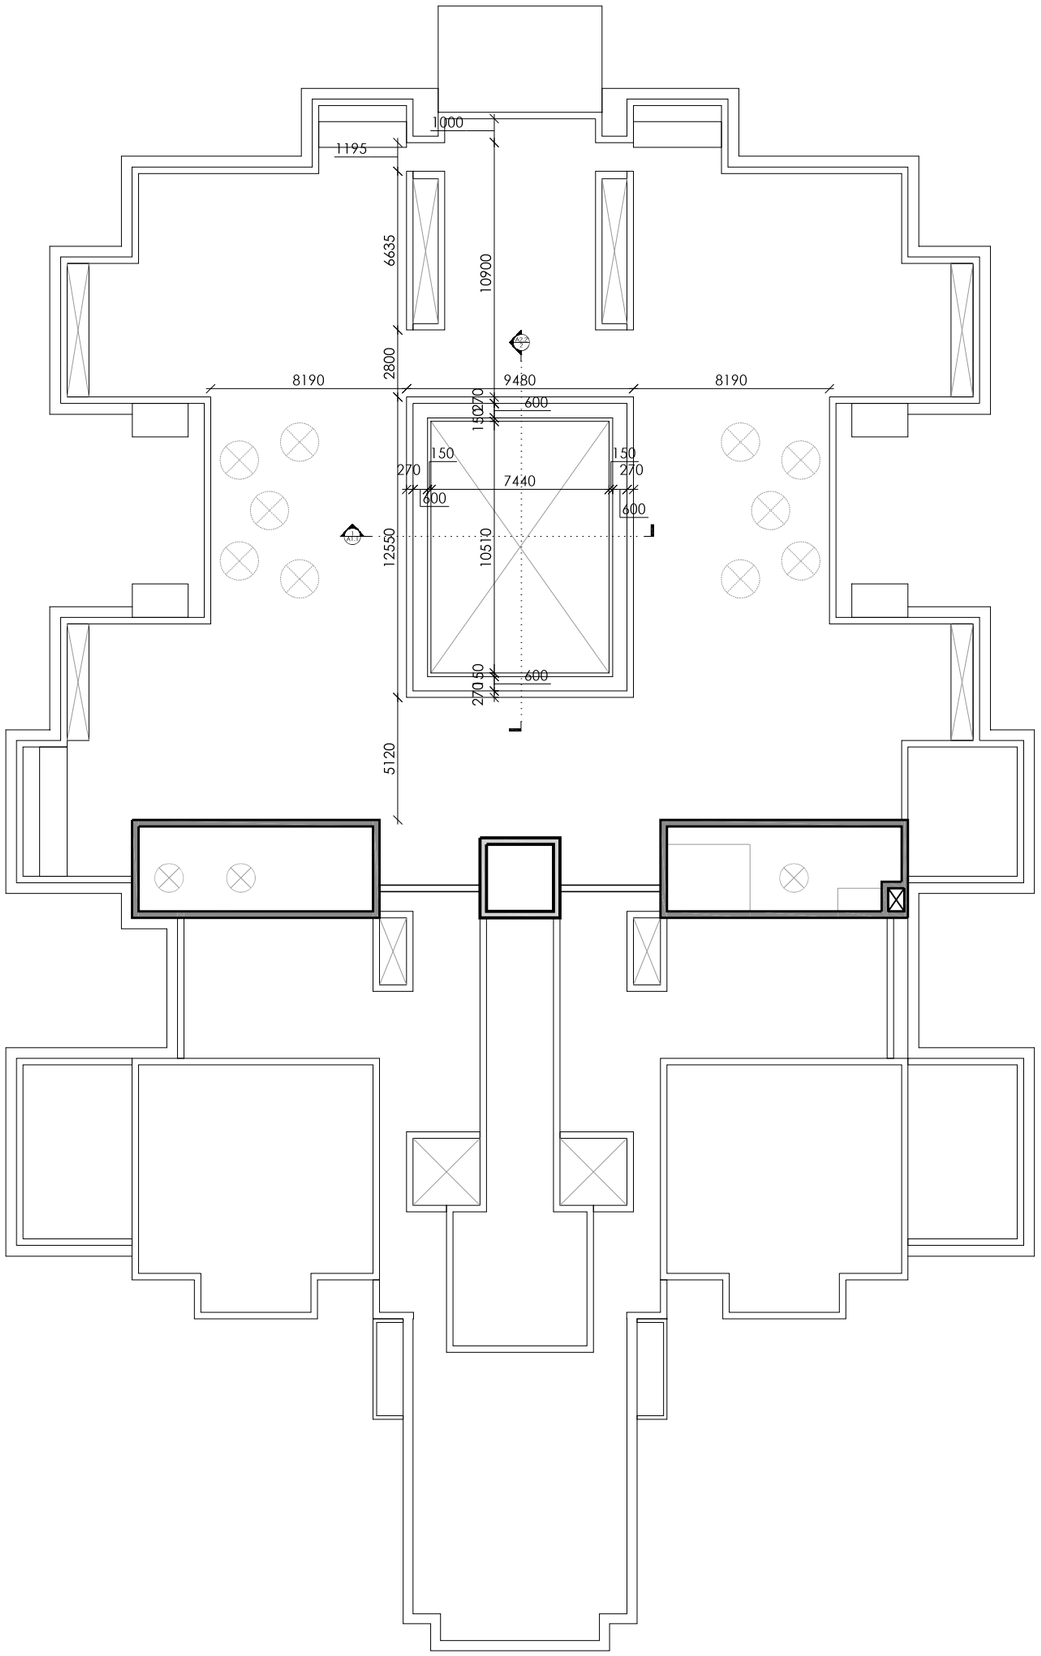


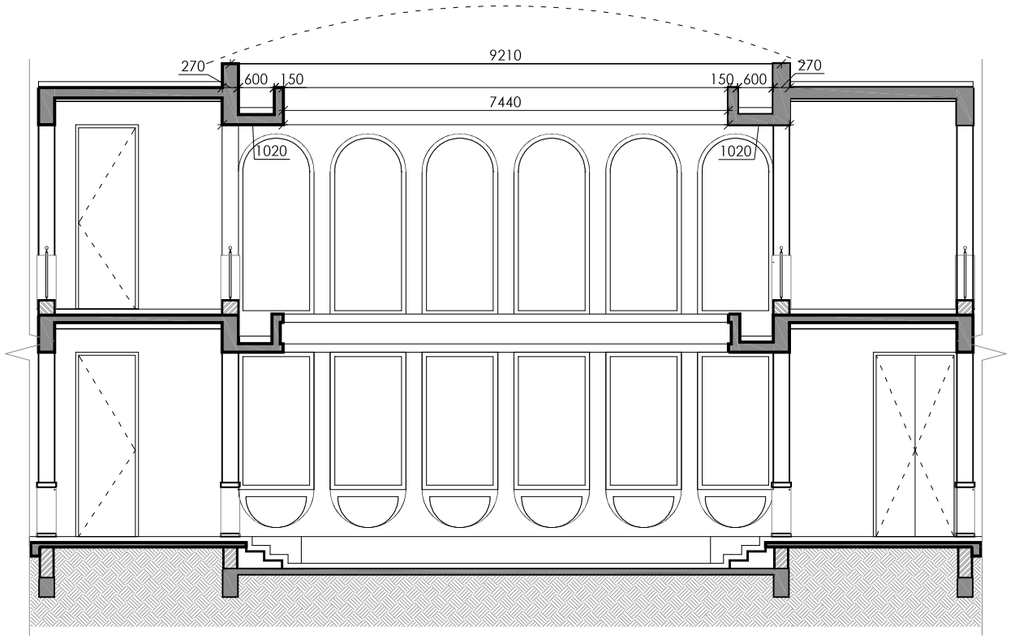

SECTION 1

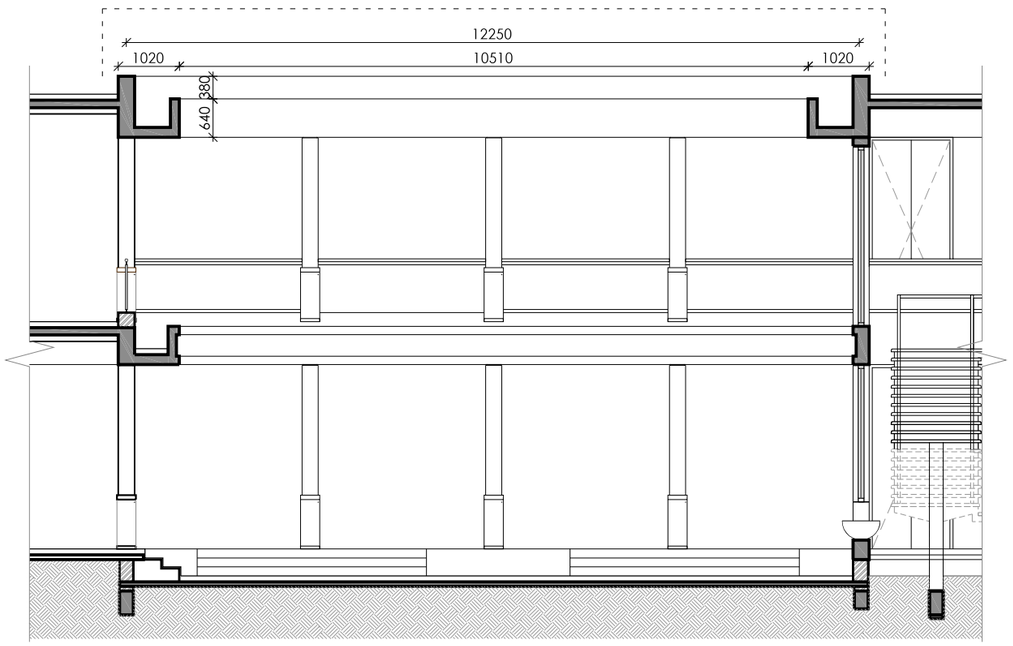

SECTION 2

BRIQMORT
PVT. LTD.
ARCHITECTURE | INTERIOR

916-917, Shilp Zaveri,
Shyamal cross road,
Ahmedabad - 380015
E-mail : design@briqmort.com
office: 079 4002 8016
contact: +91 94262 70374

Drawings and design are the property of BRIQMORT PVT LTD and are not to be copied or used without prior permission.


1. All dimensions shall be checked and co-related with the structural drawings and any ambiguity shall be immediately brought to the notice of the architect before commencement of the work.

2. All dimensions are in mm unless and otherwise specified.

3. All levels are finished levels.

4. All margins, clearances etc. required as per by-laws should be checked and provided by the contractor and any discrepancies found should be immediately brought to the notice of architect before commencement of work.

LEGENDS:

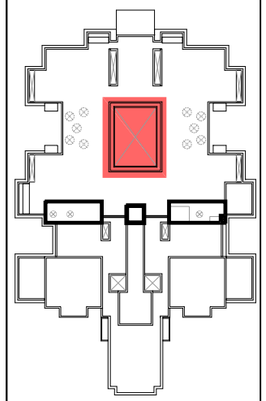

KEY PLAN

NO.	REVISION/ISSUE	DATE

PROJECT NAME:
RESIDENCE @RAJKOT

CLIENT NAME:
-

DONE BY: NIKITA	N
CHECK BY: JAYDIP	
DATE : 30/05/22	1:100 / A3

A 9.16_ A

RETRACTABLE ROOF

FOR DISCUSSION