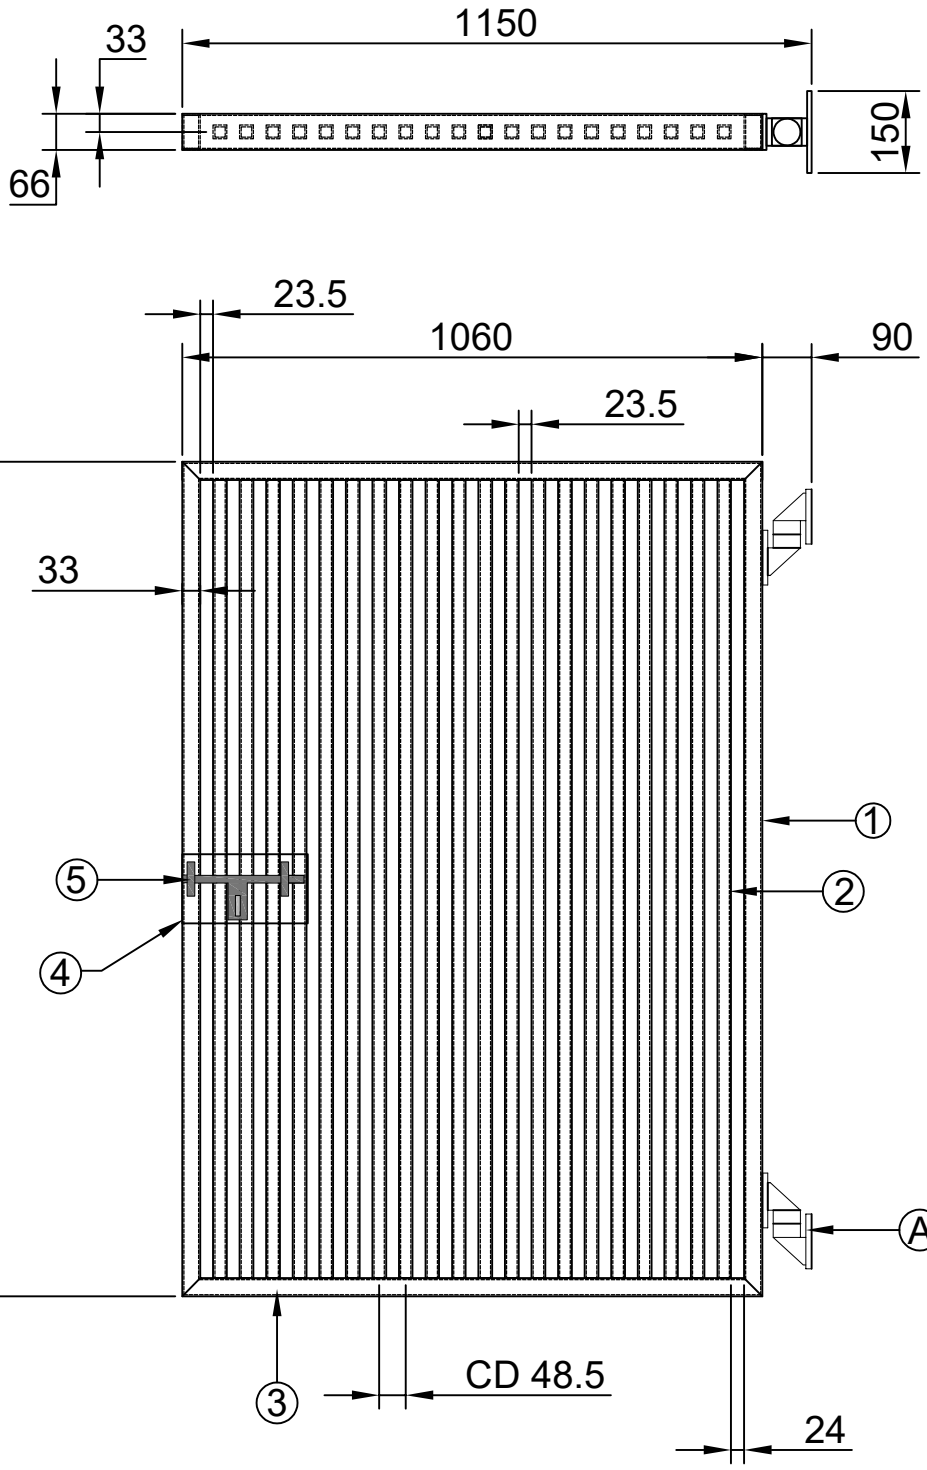


DETAILS: A

BOM			
SL NO.	DESCRIPTION	SPECIFICATION	QTY
1	MS RECT. TUBE	66X33X2.9X1525L	2NOS
2	MS SQ. TUBE	25X25X3X1459L	20NOS
3	MS RECT. TUBE	66X33X2.9X1060L	2NOS
4	MS PLATE	230X130X5THK	1NO
5	LOCK	ALDROP	1NO
6	SUPPORT PLATE1	64X50X5THK	4NOS
7	SUPPORT PLATE2	50X64X5THK	2NOS
8	SUPPORT PLATE3	66X100X8THK	2NOS
9	SUPPORT PLATE4	150X100X8THK	2NOS

This drawing & design is the property of NIHVA TECHNOLOGIES. Not to be sold or copied to any other concern.

TITLE:- WICKET GATE

NIHVA TECHNOLOGIES PVT. LTD.
NIHVA TECHNOLOGIES PVT. LTD. PUNE
Tel : 020 66304033
Email:- info@nihva.com
Website:- www.nihva.com

	NAME	DATE	SIGN
DRAWN	SUJATA	07/03/2022	
CHECK	G.PATIL	08/03/2022	
APPRD.	A.K	08/03/2022	

If any queries contact : design@nihva.com

ALL DIMENSION ARE IN mm

CLIENT -

LOCATION -

PRODUCT -WICKET GATE | QTY:-02NOS

DWG NO:-NIHVA/21-22/MFG/037 | REV- 0

SCALE: NTS | SCALE:-- 1:1 | SHEET: 01 OF 01

Rev No.	Revision	Date	Revised By