


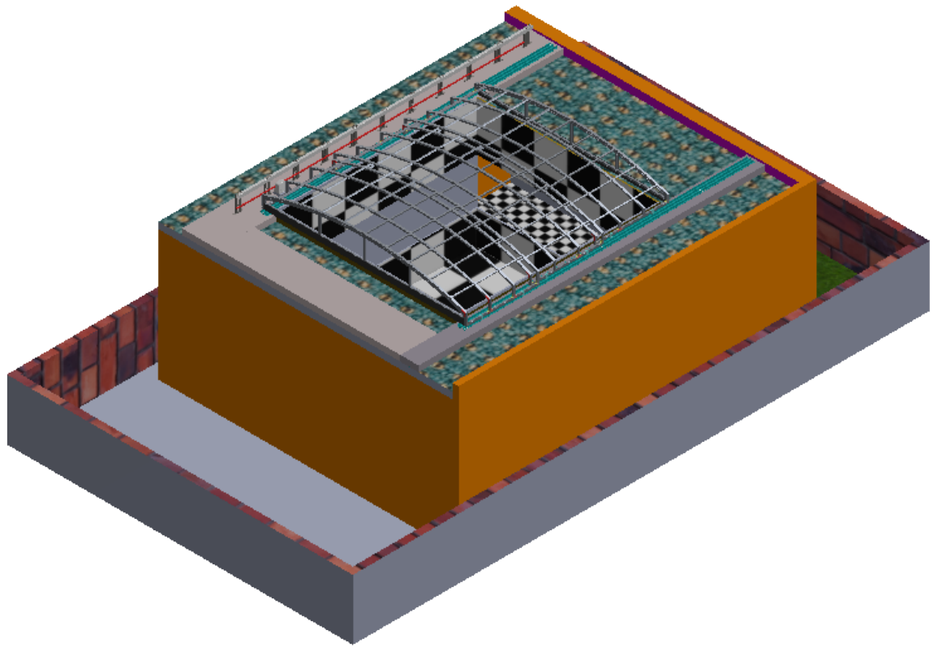


ITEM NO.	PART NUMBER	DESCRIPTION	QTY.
1	2D DRAWING SALAVI MAM CIVIL BASE	CLIENT SCOP	1
2	GUIDE RAILS-T75-1B	STD (10060 mm)	6
3	2D DRAWING SALAVI MAM Anchor Bolt M10x75	STD	76
4	2D DRAWING SALAVI MAM PANEL_01 ASM	INHOUSE	1
5	2D DRAWING SALAVI MAM PANEL_02 ASM	INHOUSE	1
6	2D DRAWING SALAVI MAM PANEL_03 ASM	INHOUSE	1
7	2D DRAWING SALAVI MAM NICE MOTOR 1T	STD	1
8	2D DRAWING SALAVI MAM Rack support_575	STD (LOOSE PART)	11
9	2D DRAWING SALAVI MAM RACK	STD (M4 RACK, 30x8x1000 mm, ZINC COATED WITH SPACERS AND SCREWS.)	11
10	2D DRAWING SALAVI MAM BUSBAR FLASHER	STD (LOOSE PART)	5

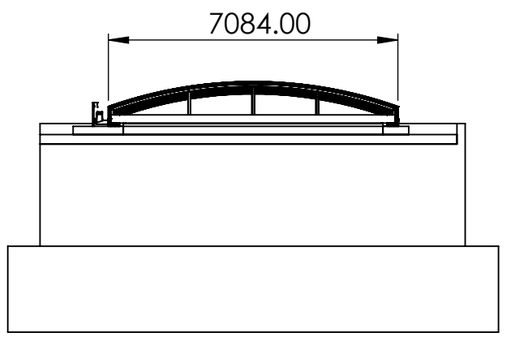


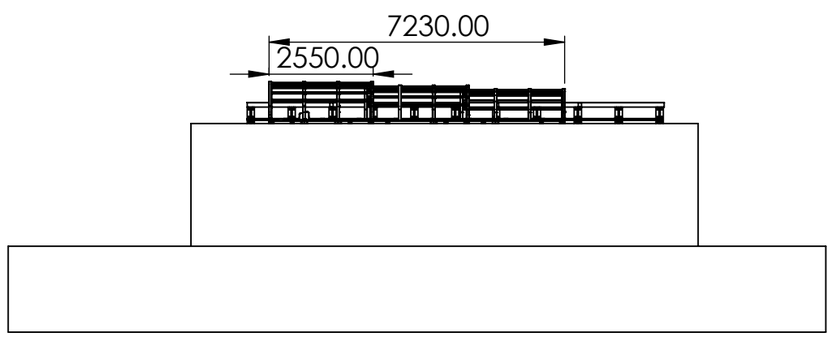



TITLE - RETRACTABLE ROOF				NIHVA TECHNOLOGIES PVT.LTD.PUNE
DWG NO - NTPL276-001-00-000-000				Website - www.nihva.com
	NAME	SIGNATURE	DATE	PROJECT NO - NTPL276-PM
DRAWN	S.W		28-03-2025	PRODUCT - RETRACTABLE ROOF
CHK'D	P.M.		28-03-2025	SITE LOCATION - GUJARAT
APPV'D	V.T.		28-03-2025	
if any queries contact - supportautomation@nihva.com				REVISION - QTY - 1
ALL DIMENSION ARE IN mm		A3		SCALE - SHEET 1 OF 36

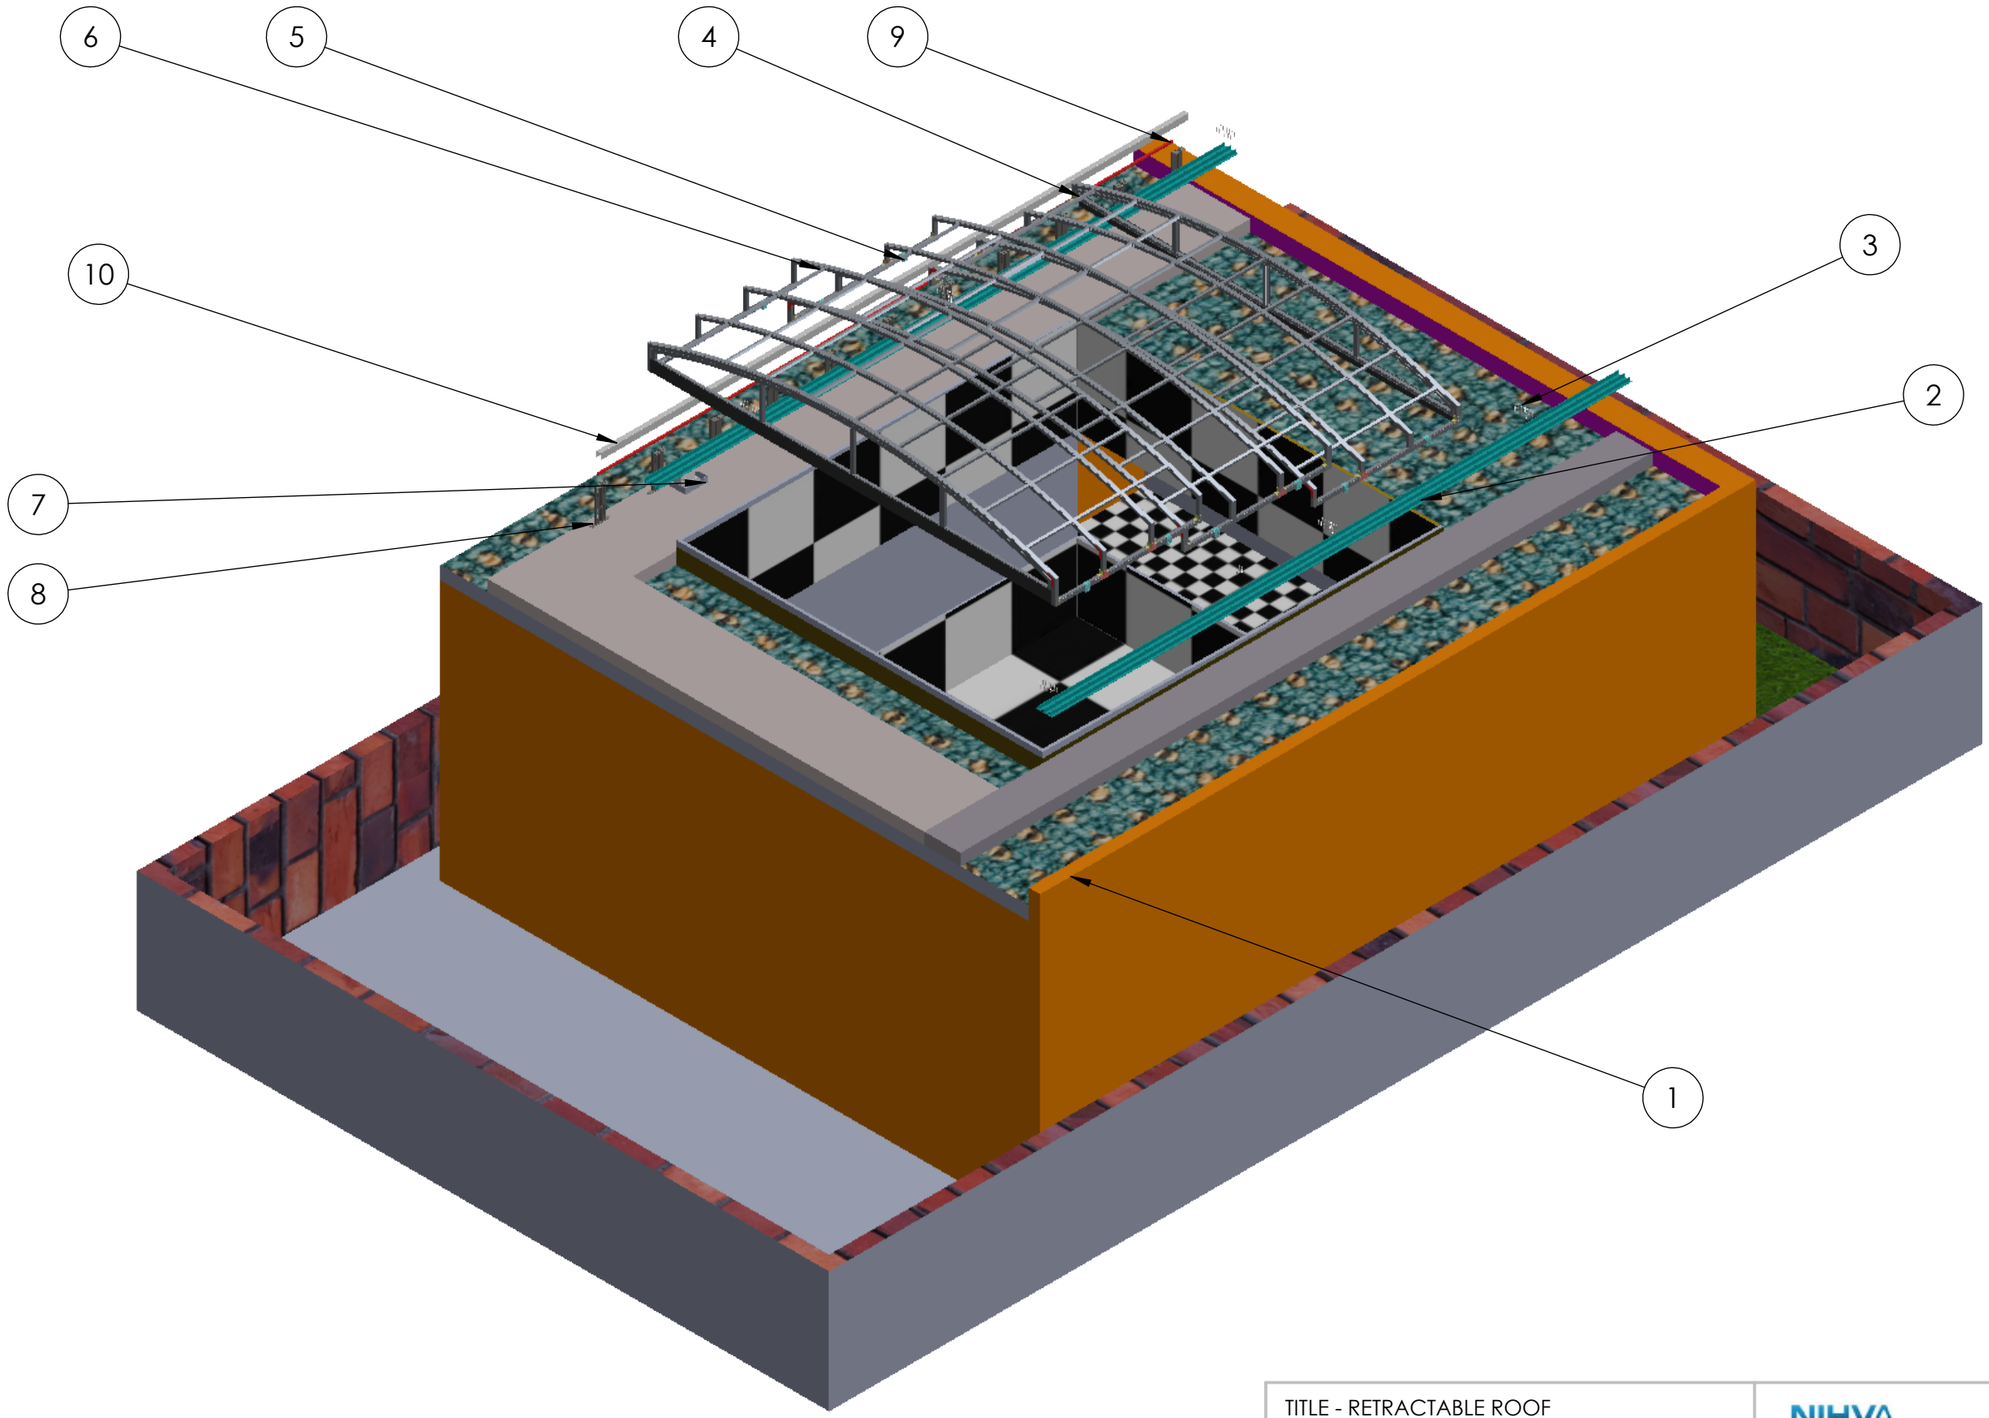

TITLE - RETRACTABLE ROOF				NIHVA TECHNOLOGIES PVT.LTD.PUNE
DWG NO - NTPL276-001-00-000-000				Website - www.nihva.com
	NAME	SIGNATURE	DATE	PROJECT NO - NTPL276-PM
DRAWN	S.W		28-03-2025	PRODUCT - RETRACTABLE ROOF
CHK'D	P.M.		28-03-2025	SITE LOCATION - GUJARAT
APPV'D	V.T.		28-03-2025	
if any queries contact - supportautomation@nihva.com				REVISION - QTY - 1
ALL DIMENSION ARE IN mm			A3	SCALE - SHEET 2 OF 36

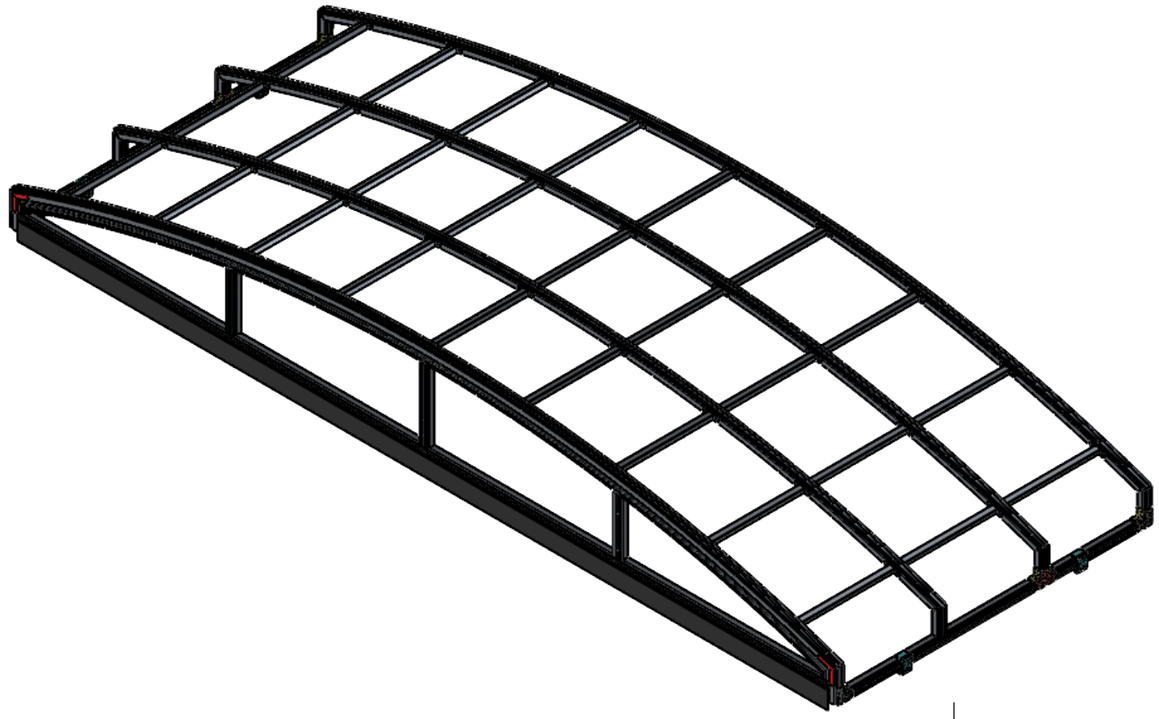

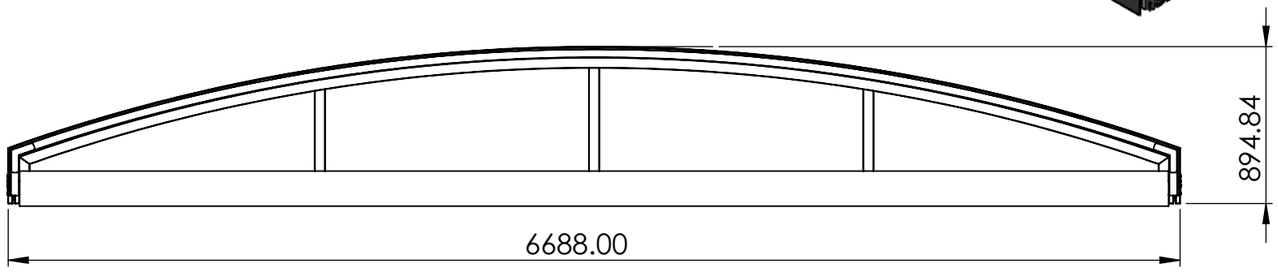

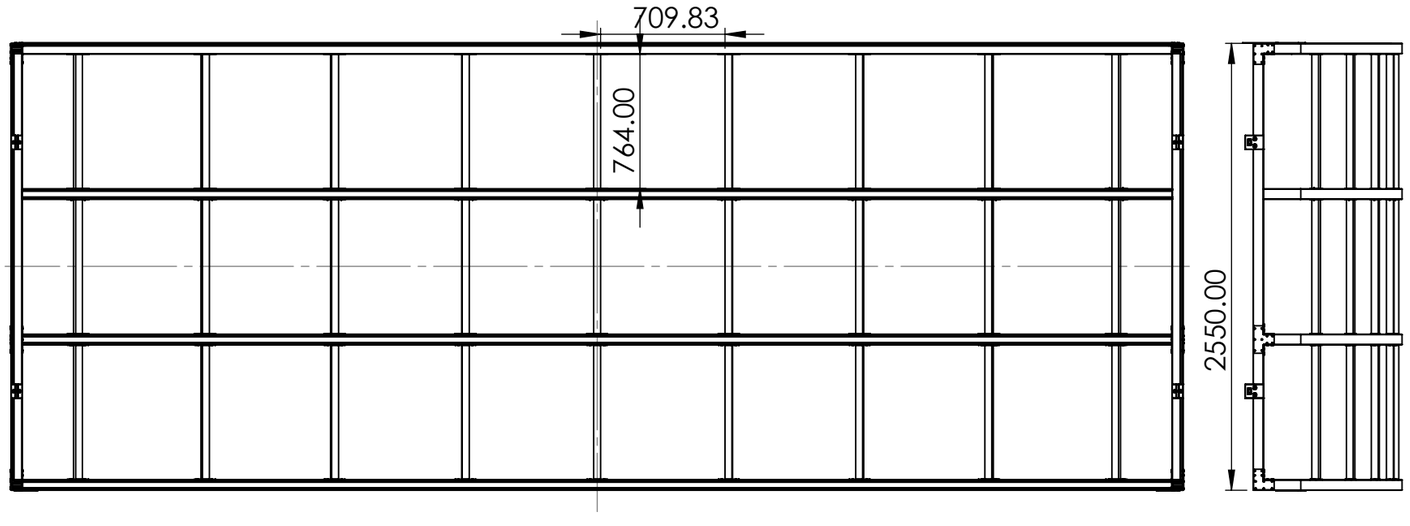


ITEM NO.	PART NUMBER	DESCRIPTION	QTY.
1	2D DRAWING SALAVI MAM NTPL-268-PM-PANEL_01	PANEL_01 FRAME	1
2	AL Support tube SQ TUBE 40X40X1.5 MM L-734 MM	AL INTERMEDIAT SUPPORT TUBE	27
3	2D DRAWING SALAVI MAM rivet_iso_15977_4_x_16_0	RIVET M4X16	267
4	T PLATE	SS304 - 117.5X156X3 MM THK	4
5	L PLATE	SS304- 91X106X3 MM THK	8
6	L ANGLE PLATE	SS304 - 60X60X3 MM	8
7	2D DRAWING SALAVI MAM PROFILE L ANGLE WELDING PLATE	JOINING PLATE Al metal	4
8	BEARING BLOCK (T75-1B)	80X105X63 MM (VMC PART)	4
9	SKF_NATR 12	BRG(STD)	8
10	SKF_NATR 8	BRG(STD)	8
11	2D DRAWING SALAVI MAM SHOULDER BOLT NATR 12 12x36 M10		8
12	ISO 7379 - 8 x 32 M6		8
13	2D DRAWING SALAVI MAM ENCLOSURE NTPL-268-PM-PANEL_01	ENCLOSURE _01	1
14	2D DRAWING EPDM RUBBER		1

PANEL-1


TITLE - RETRACTABLE ROOF				NIHVA TECHNOLOGIES PVT.LTD.PUNE
DWG NO - NTPL276-001-01-000-000				Website - www.nihva.com
	NAME	SIGNATURE	DATE	PROJECT NO - NTPL276-PM
DRAWN	S.W		28-03-2025	PRODUCT - RETRACTABLE ROOF
CHK'D	P.M.		28-03-2025	SITE LOCATION - GUJARAT
APPV'D	V.T.		28-03-2025	
if any queries contact - supportautomation@nihva.com				REVISION - QTY - 1
ALL DIMENSION ARE IN mm			A3	SCALE - SHEET 3 OF 36


ITEM NO.	PART NUMBER	DESCRIPTION	QTY.
1	2D DRAWING SALAVI MAM ENCLOSURE NTPL-268-PM-PANEL_01	ENCLOSURE _01	1

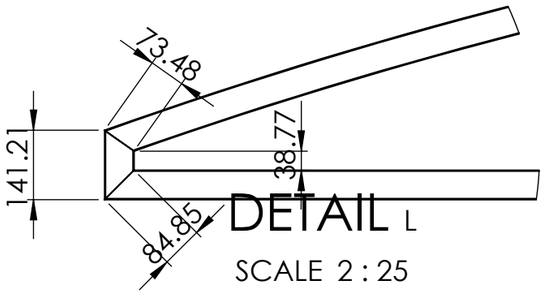



DETAIL L

SCALE 2 : 25

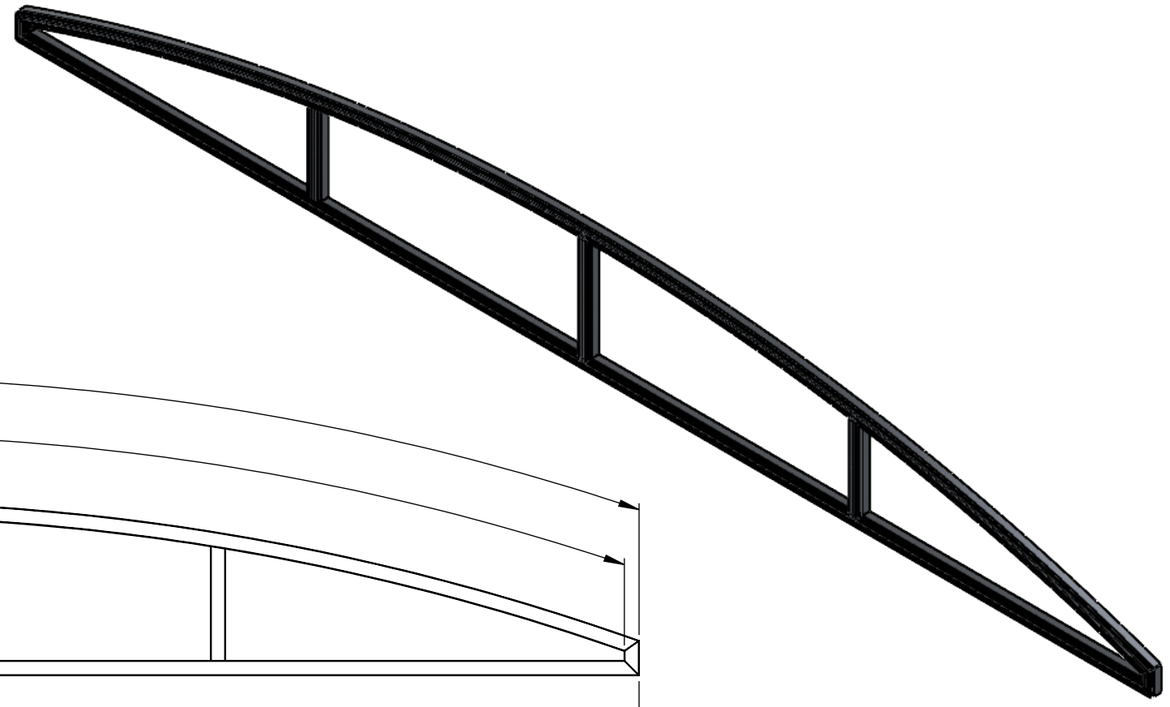


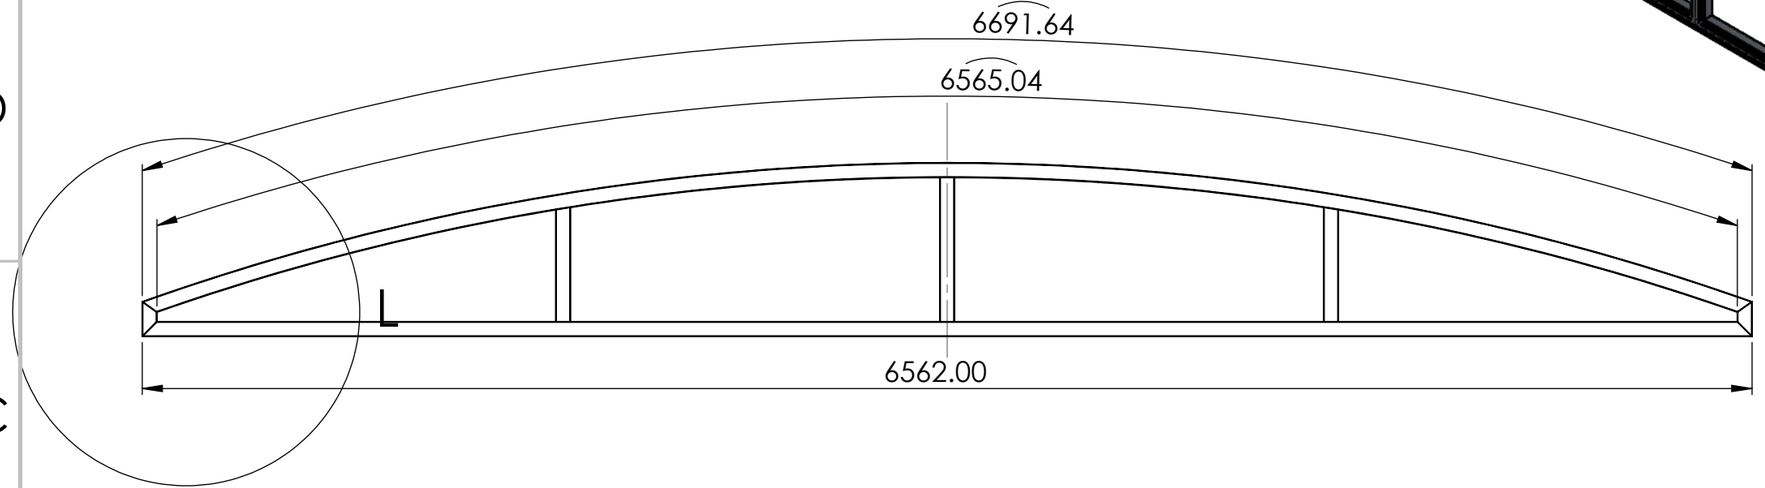

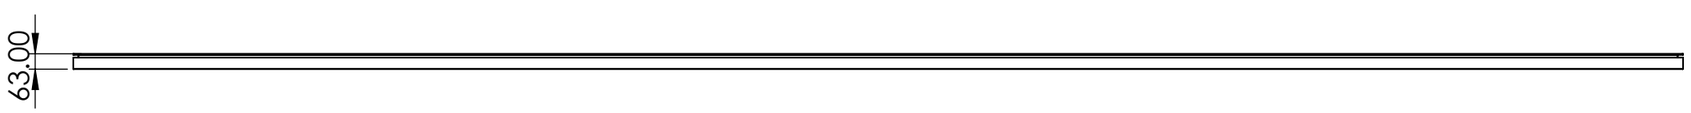


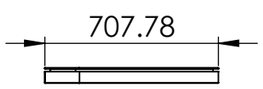



TITLE - RETRACTABLE ROOF				NIHVA TECHNOLOGIES PVT.LTD.PUNE
DWG NO - NTPL276-001-01-00-001				Website - www.nihva.com
	NAME	SIGNATURE	DATE	PROJECT NO - NTPL276-PM
DRAWN	S.W		28-03-2025	PRODUCT - RETRACTABLE ROOF
CHK'D	P.M.		28-03-2025	SITE LOCATION - GUJARAT
APPV'D	V.T.		28-03-2025	
if any queries contact - supportautomation@nihva.com				REVISION - QTY - 1
ALL DIMENSION ARE IN mm			A3	SCALE - SHEET 4 OF 36

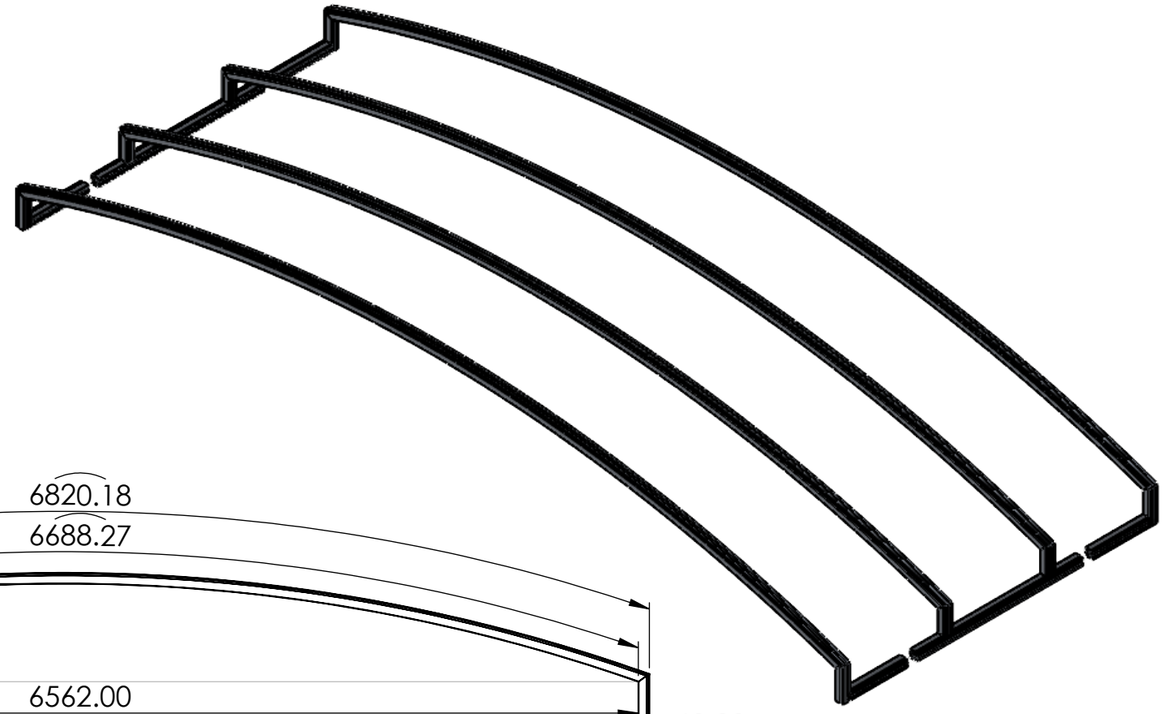

ITEM NO.	PART NUMBER	DESCRIPTION	QTY.
1	2D DRAWING SALAVI MAM NTPL-268-PM-PANEL_01	PANEL_01 FRAME	1

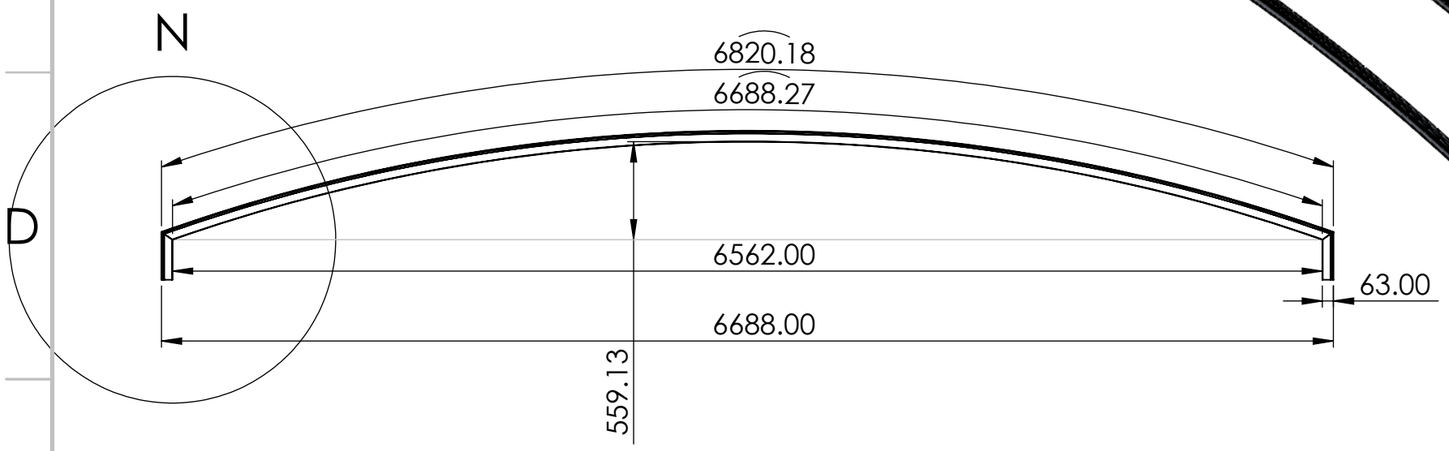


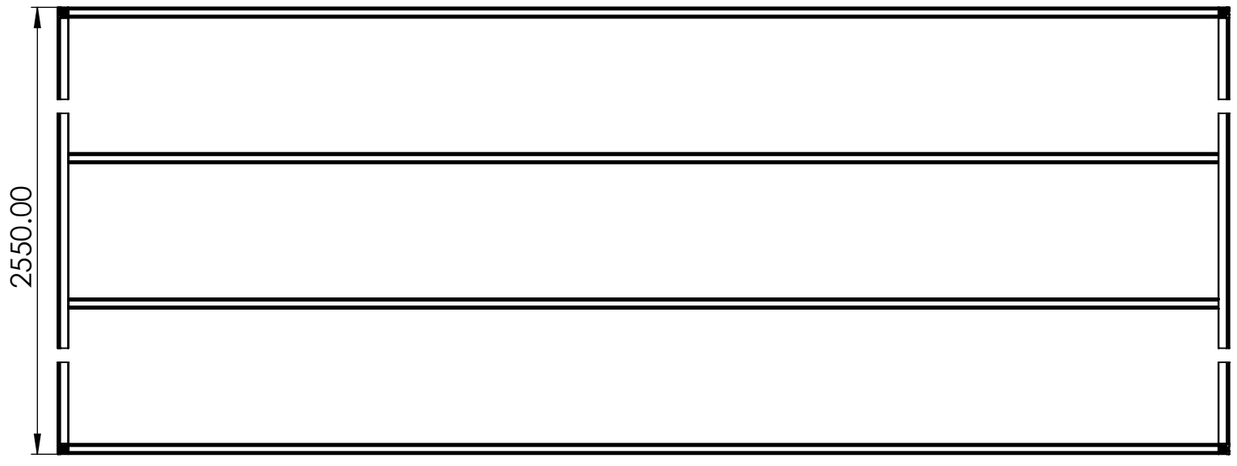

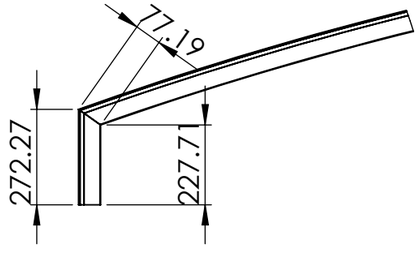


DETAIL N


SCALE 2 : 35

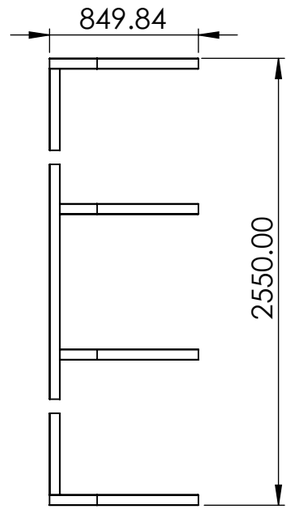



TITLE - RETRACTABLE ROOF				NIHVA TECHNOLOGIES PVT.LTD.PUNE
DWG NO - NTPL276-001-01-000-002				Website - www.nihva.com
	NAME	SIGNATURE	DATE	PROJECT NO - NTPL276-PM
DRAWN	S.W		28-03-2025	PRODUCT - RETRACTABLE ROOF
CHK'D	P.M.		28-03-2025	SITE LOCATION - GUJARAT
APPV'D	V.T.		28-03-2025	
if any queries contact - supportautomation@nihva.com				REVISION - / QTY - 1
ALL DIMENSION ARE IN mm			A3	SCALE - / SHEET 5 OF 36

ITEM NO.	PART NUMBER	DESCRIPTION	QTY.
1	AL Support tube SQ TUBE 40X40X1.5 MM L-734 MM	AL INTERMEDIAT SUPPORT TUBE	81

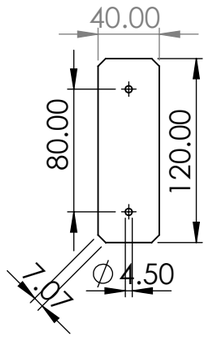


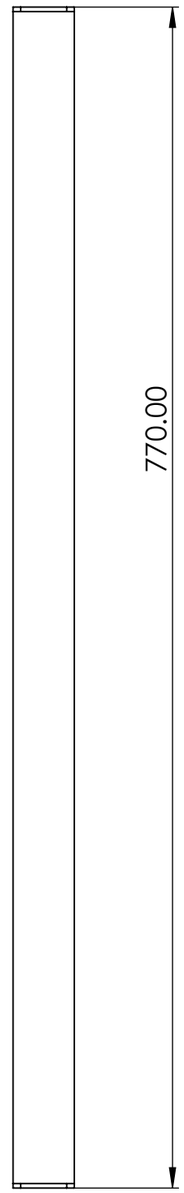

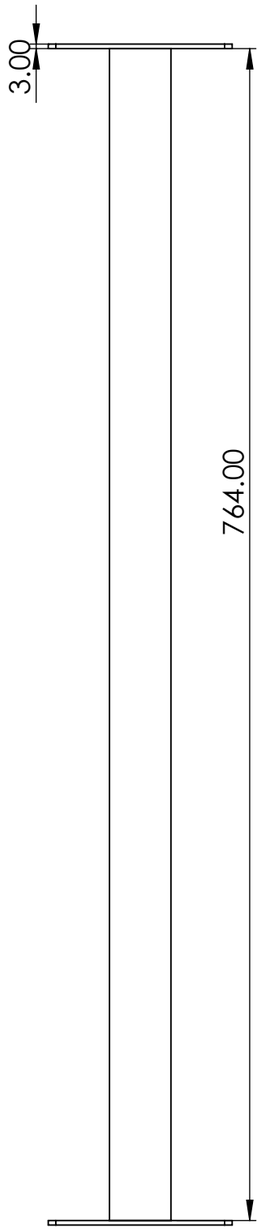

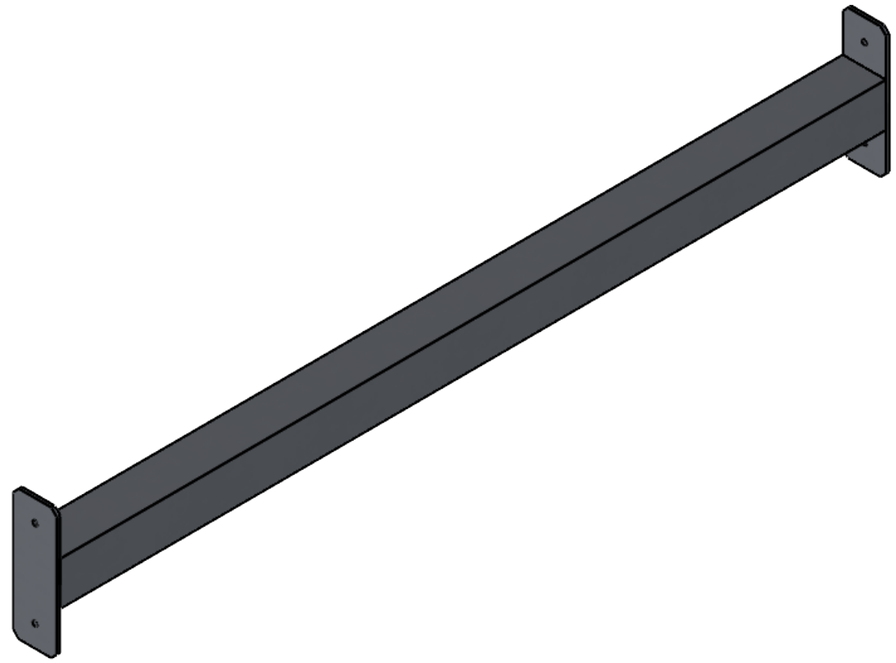


TITLE - RETRACTABLE ROOF				NIHVA TECHNOLOGIES PVT.LTD.PUNE
DWG NO - NTPL276-001-01-000-003				Website - www.nihva.com
	NAME	SIGNATURE	DATE	PROJECT NO - NTPL276-PM
DRAWN	S.W		28-03-2025	PRODUCT - RETRACTABLE ROOF
CHK'D	P.M.		28-03-2025	SITE LOCATION - GUJARAT
APPV'D	V.T.		28-03-2025	
if any queries contact - supportautomation@nihva.com				REVISION - QTY - 1
ALL DIMENSION ARE IN mm			A3	SCALE - SHEET 6 OF 36

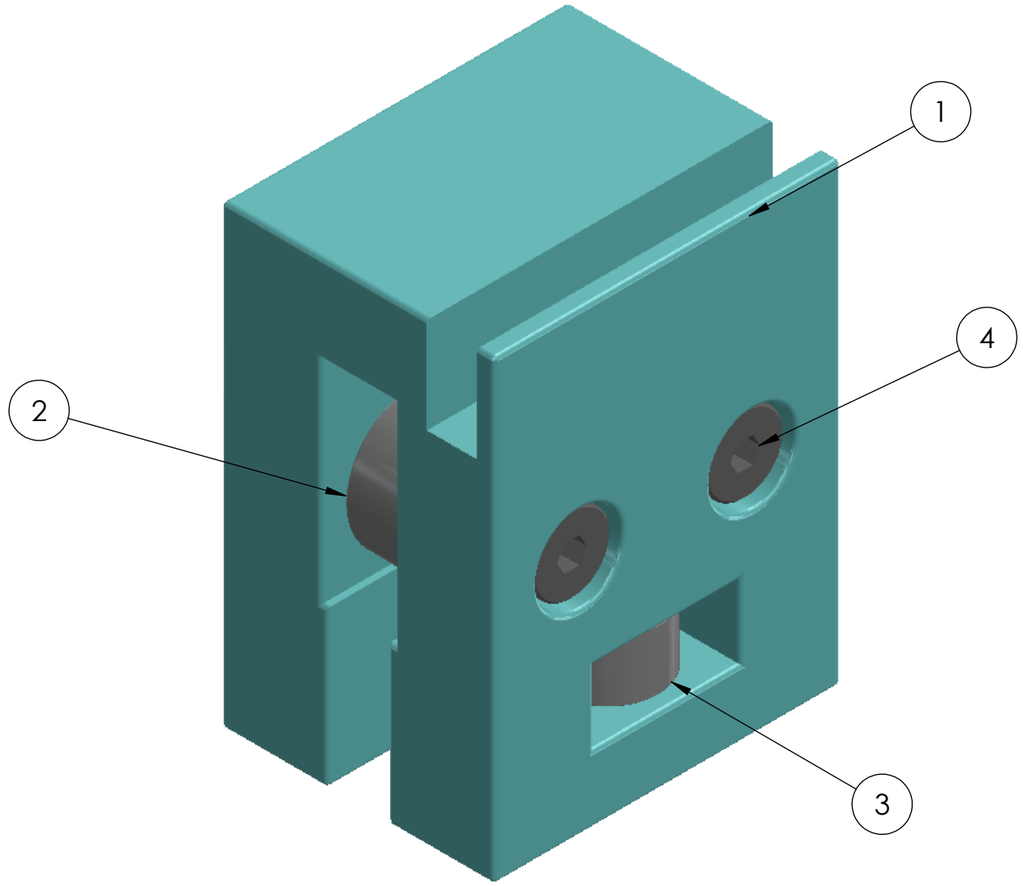


ITEM NO.	PART NUMBER	DESCRIPTION	QTY.
1	BEARING BLOCK (T75-1B)	80X105X63 MM (VMC PART)	1
2	SKF_NATR 12	BRG(STD)	2
3	SKF_NATR 8	BRG(STD)	2
4	2D DRAWING SALAVI MAM SHOULDER BOLT NATR 12 12x36 M10		2
5	ISO 7379 - 8 x 32 M8		2


Total Quantity- 12

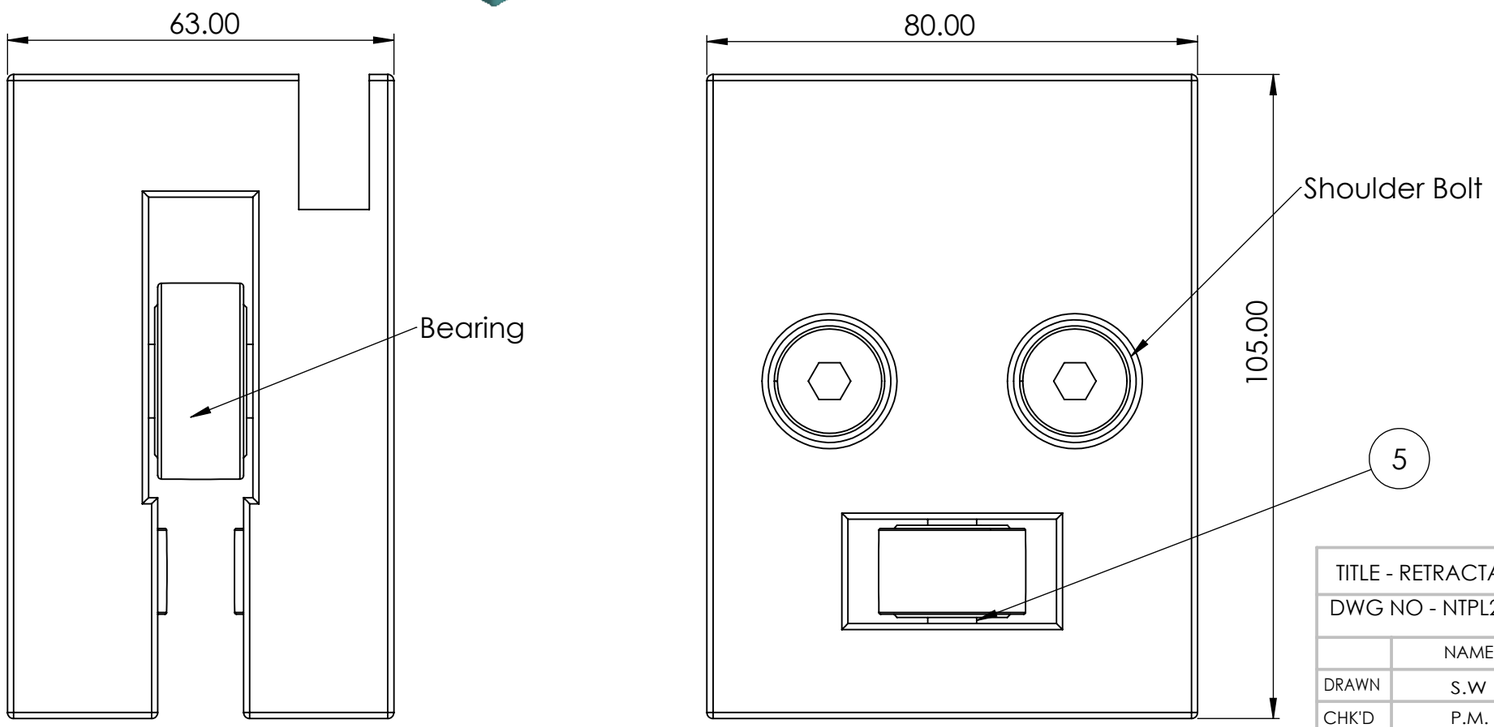


TITLE - RETRACTABLE ROOF				NIHVA TECHNOLOGIES PVT.LTD.PUNE
DWG NO - NTPL276-001-01-001-000				Website - www.nihva.com
	NAME	SIGNATURE	DATE	PROJECT NO - NTPL276-PM
DRAWN	S.W		28-03-2025	PRODUCT - RETRACTABLE ROOF
CHK'D	P.M.		28-03-2025	SITE LOCATION - GUJARAT
APPV'D	V.T.		28-03-2025	
if any queries contact - supportautomation@nihva.com				REVISION - QTY - 1
ALL DIMENSION ARE IN mm			A3	SCALE - SHEET 7 OF 36

ITEM NO.	PART NUMBER	DESCRIPTION	QTY.
1	BEARING BLOCK (T75-1B)	80X105X63 MM (VMC PART)	12

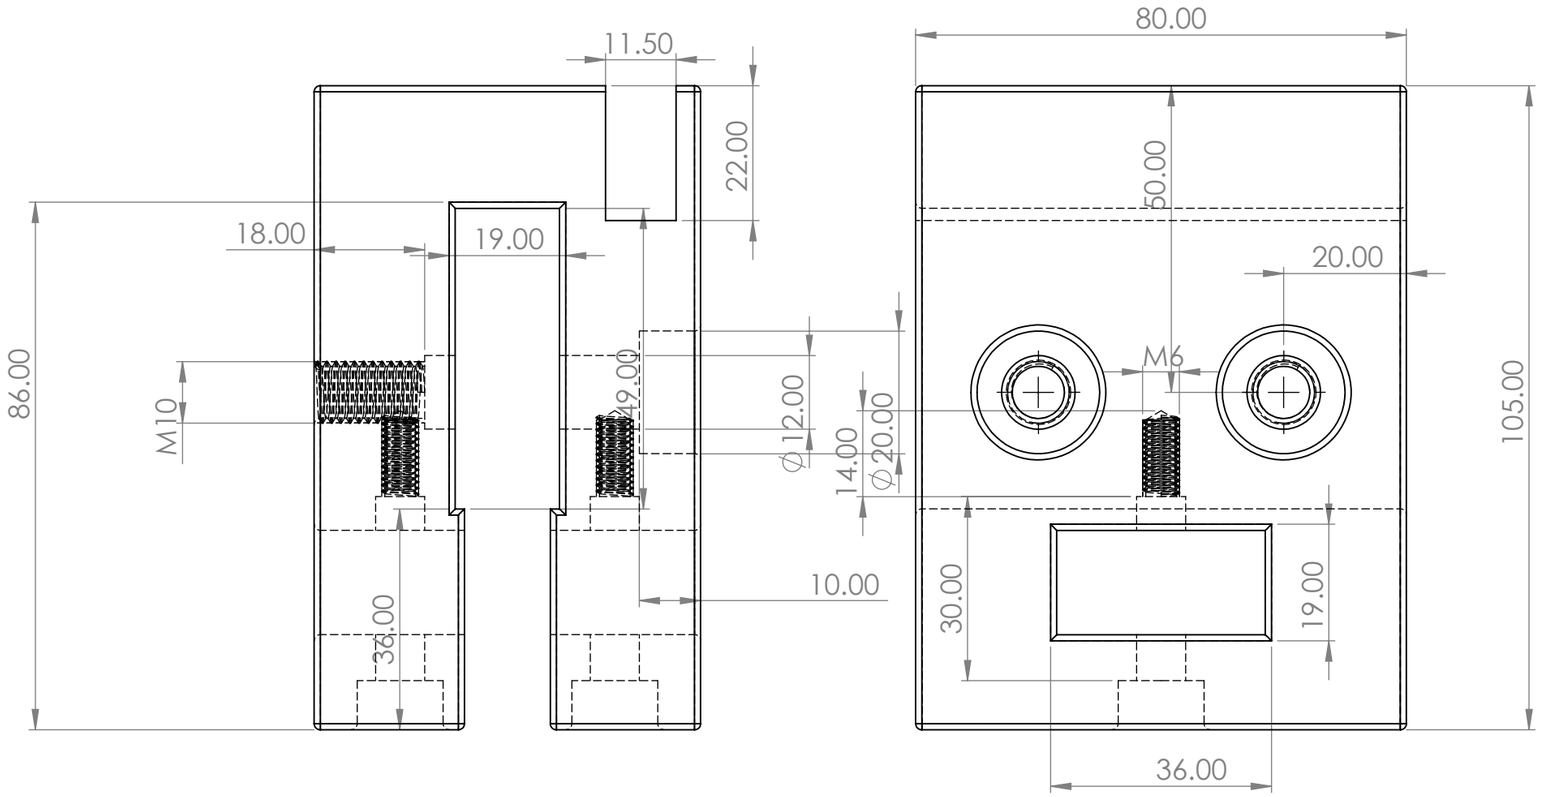

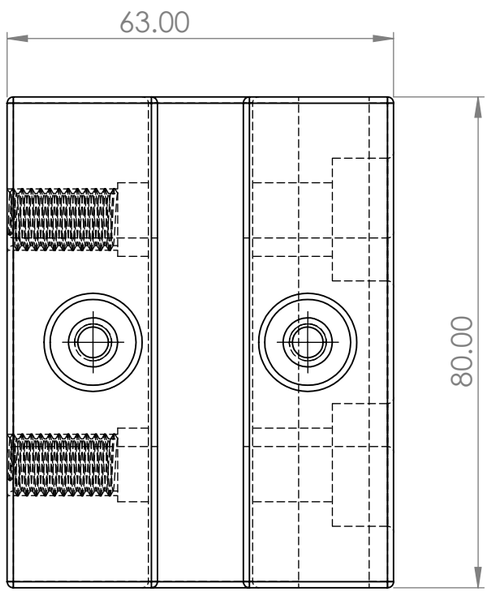


TITLE - RETRACTABLE ROOF				NIHVA TECHNOLOGIES PVT.LTD.PUNE
DWG NO - NTPL276-001-01-001-001				Website - www.nihva.com
	NAME	SIGNATURE	DATE	PROJECT NO - NTPL276-PM
DRAWN	S.W		28-03-2025	PRODUCT - RETRACTABLE ROOF
CHK'D	P.M.		28-03-2025	SITE LOCATION - GUJARAT
APPV'D	V.T.		28-03-2025	
if any queries contact - supportautomation@nihva.com				REVISION - QTY - 1
ALL DIMENSION ARE IN mm			A3	SCALE - SHEET 8 OF 36

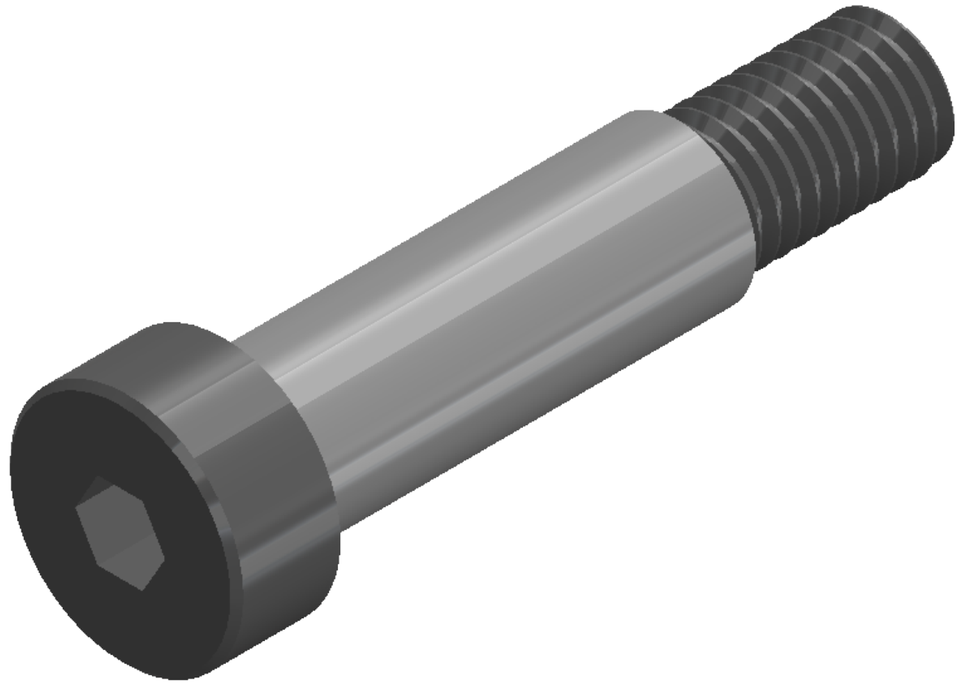

ITEM NO.	PART NUMBER	DESCRIPTION	QTY.
1	2D DRAWING SALAVI MAM SHOULDER BOLT NATR 12 12x36 M10		1


Total Quantity- 24

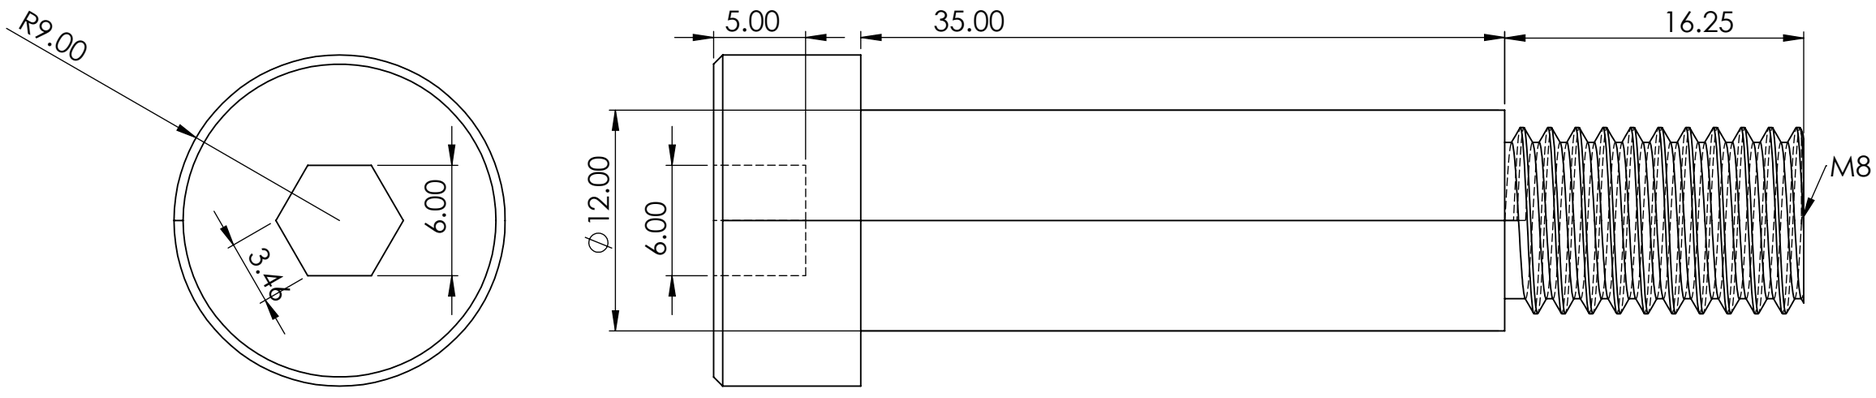


TITLE - RETRACTABLE ROOF				NIHVA TECHNOLOGIES PVT.LTD.PUNE
DWG NO - NTPL276-001-01-001-002				Website - www.nihva.com
	NAME	SIGNATURE	DATE	PROJECT NO - NTPL276-PM
DRAWN	S.W		28-03-2025	PRODUCT - RETRACTABLE ROOF
CHK'D	P.M.		28-03-2025	SITE LOCATION - GUJARAT
APPV'D	V.T.		28-03-2025	
if any queries contact - supportautomation@nihva.com				REVISION - QTY - 1
ALL DIMENSION ARE IN mm			A3	SCALE - SHEET 9 OF 36

ITEM NO.	PART NUMBER	DESCRIPTION	QTY.
1	ISO 7379 - 8 x 30 --- N		1

Total Quantity - 24

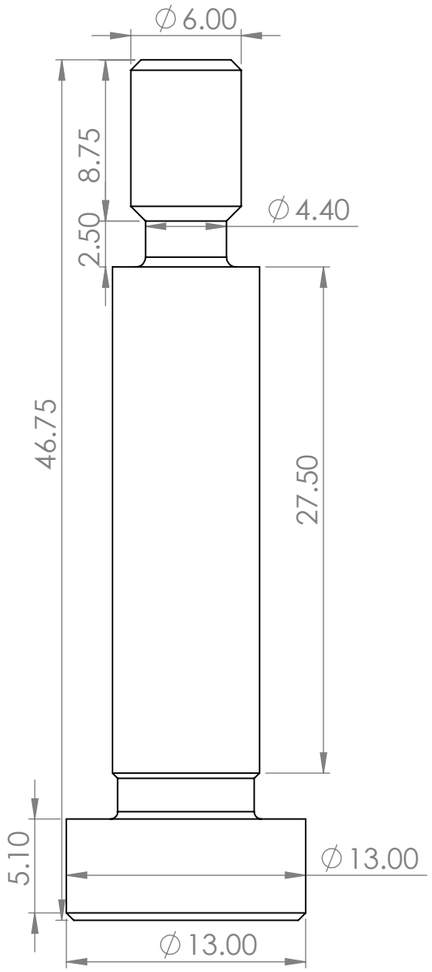




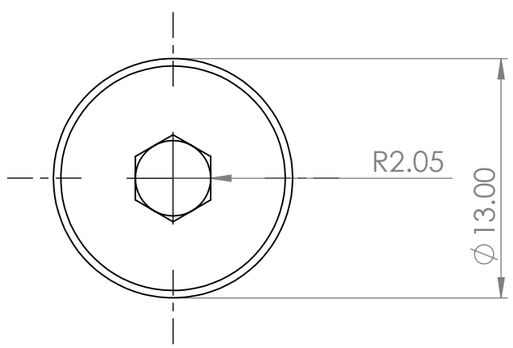


TITLE - RETRACTABLE ROOF				NIHVA TECHNOLOGIES PVT.LTD.PUNE
DWG NO - NTPL276-001-01-001-003				Website - www.nihva.com
	NAME	SIGNATURE	DATE	PROJECT NO - NTPL276-PM
DRAWN	S.W		28-03-2025	PRODUCT - RETRACTABLE ROOF
CHK'D	P.M.		28-03-2025	SITE LOCATION - GUJARAT
APPV'D	V.T.		28-03-2025	
if any queries contact - supportautomation@nihva.com				REVISION - QTY - 1
ALL DIMENSION ARE IN mm			A3	SCALE - SHEET 10 OF 36

ITEM NO.	PART NUMBER	DESCRIPTION	QTY.
1	SKF_NATR 8	BRG(STD)	1

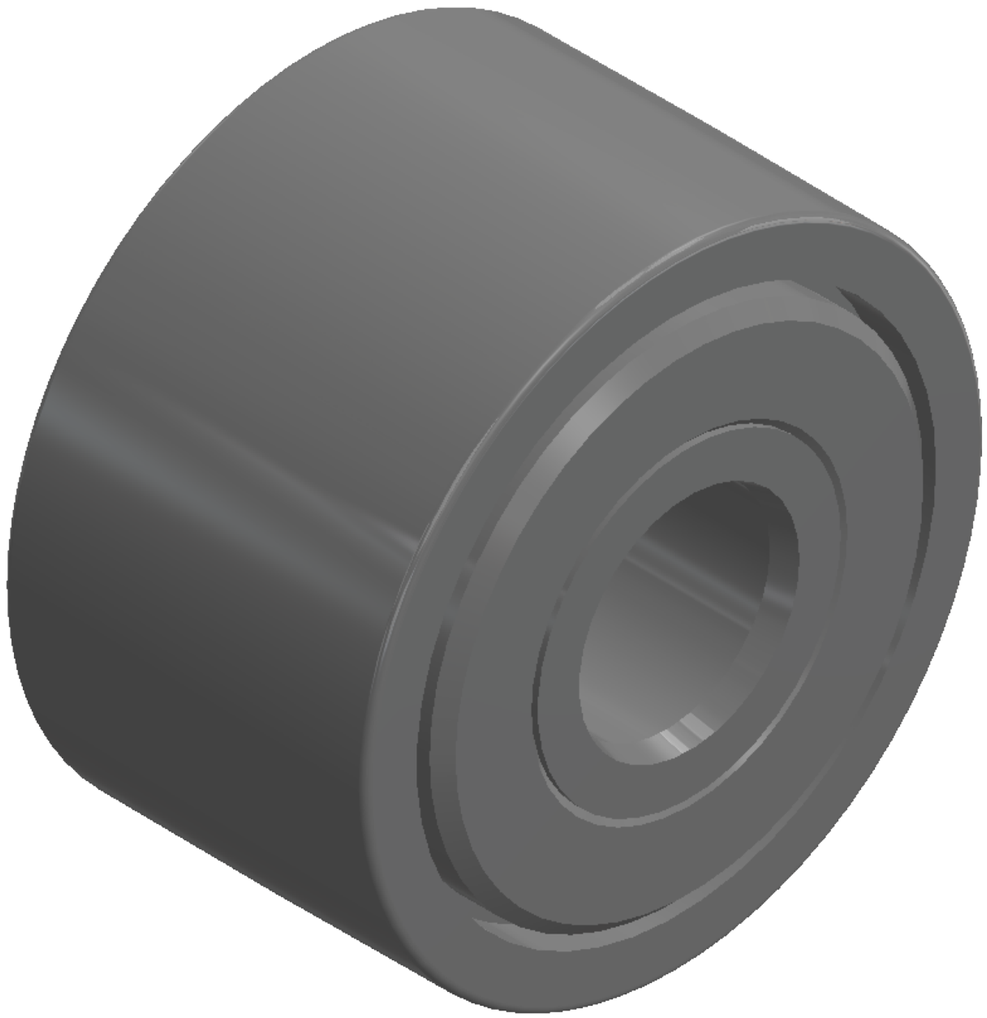

TITLE - RETRACTABLE ROOF				NIHVA TECHNOLOGIES PVT.LTD.PUNE
DWG NO - NTPL276-001-01-001-004				Website - www.nihva.com
	NAME	SIGNATURE	DATE	PROJECT NO - NTPL276-PM
DRAWN	S.W		28-03-2025	PRODUCT - RETRACTABLE ROOF
CHK'D	P.M.		28-03-2025	SITE LOCATION - GUJARAT
APPV'D	V.T.		28-03-2025	
if any queries contact - supportautomation@nihva.com				REVISION - QTY - 1
ALL DIMENSION ARE IN mm			A3	SCALE - SHEET 11 OF 36


ITEM NO.	PART NUMBER	DESCRIPTION	QTY.
1	SKF_NATR 12	BRG(STD)	1

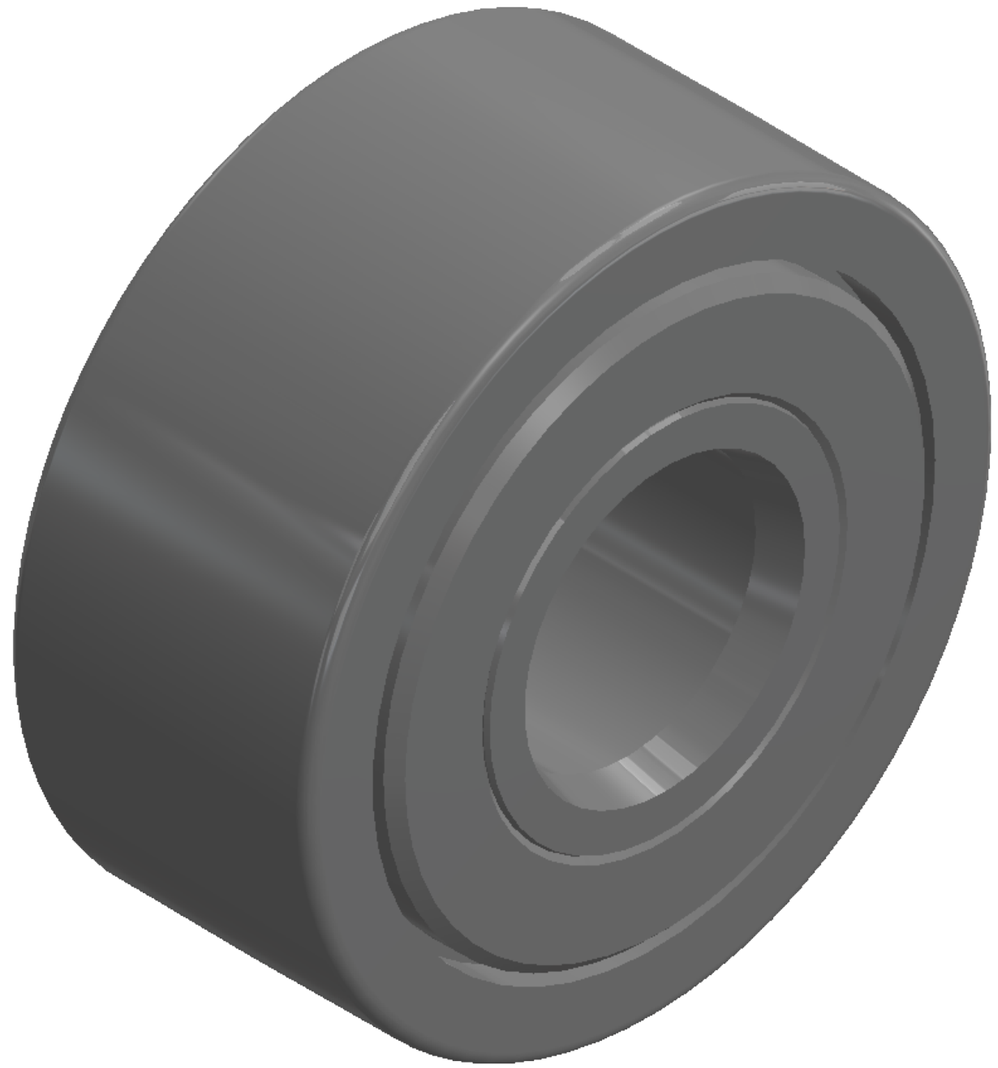



TITLE - RETRACTABLE ROOF				NIHVA TECHNOLOGIES PVT.LTD.PUNE
DWG NO - NTPL276-001-01-001-005				Website - www.nihva.com
	NAME	SIGNATURE	DATE	PROJECT NO - NTPL276-PM
DRAWN	S.W		28-03-2025	PRODUCT - RETRACTABLE ROOF
CHK'D	P.M.		28-03-2025	SITE LOCATION - GUJARAT
APPV'D	V.T.		28-03-2025	
if any queries contact - supportautomation@nihva.com				REVISION - QTY - 1
ALL DIMENSION ARE IN mm			A3	SCALE - SHEET 12 OF 36

ITEM NO.	PART NUMBER	DESCRIPTION	QTY.
1	L ANGLE PLATE	SS304 - 60X60X3 MM	1
2	2D DRAWING SALAVI MAM rivet_iso_15977_4_x_16_0	RIVET M4X16	8

Total Quantity - 24

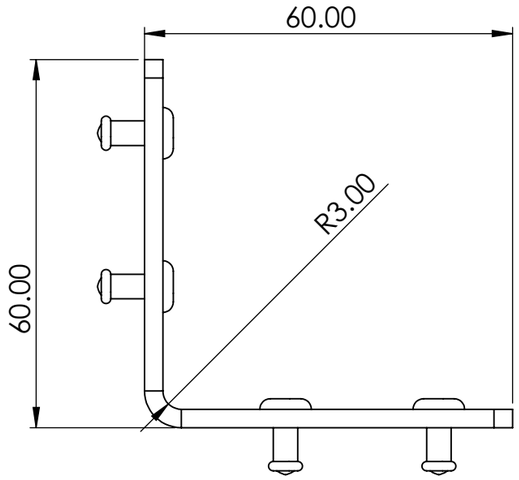


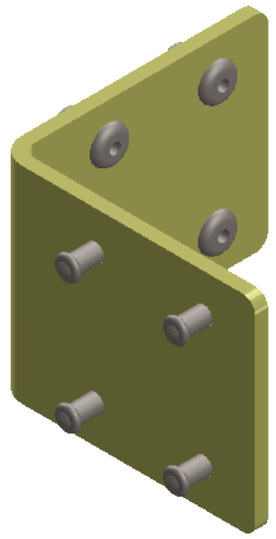


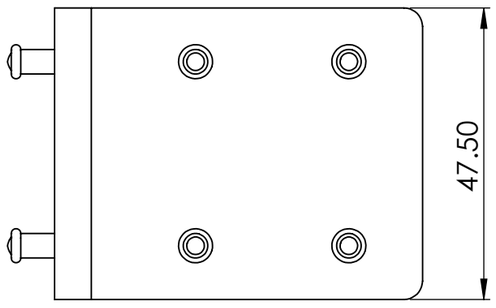



TITLE - RETRACTABLE ROOF				NIHVA TECHNOLOGIES PVT.LTD.PUNE Website - www.nihva.com
DWG NO - NTPL276-001-01-002-000				
	NAME	SIGNATURE	DATE	PROJECT NO - NTPL276-PM
DRAWN	S.W		28-03-2025	PRODUCT - RETRACTABLE ROOF
CHK'D	P.M.		28-03-2025	SITE LOCATION - GUJARAT
APPV'D	V.T.		28-03-2025	
if any queries contact - supportautomation@nihva.com				REVISION - / QTY - 1
ALL DIMENSION ARE IN mm			A3	SCALE - / SHEET 13 OF 36

ITEM NO.	PART NUMBER	DESCRIPTION	QTY.
1	L ANGLE PLATE	SS304 - 60X60X3 MM	24

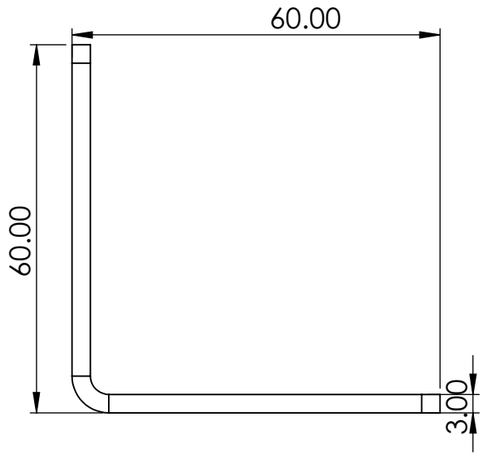


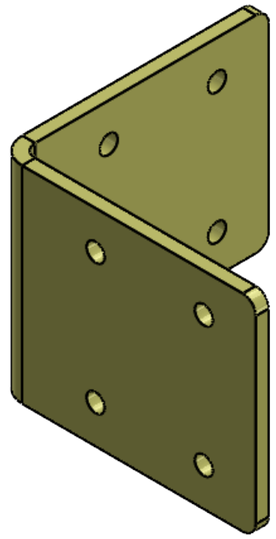

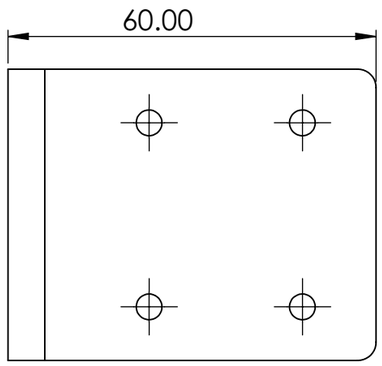


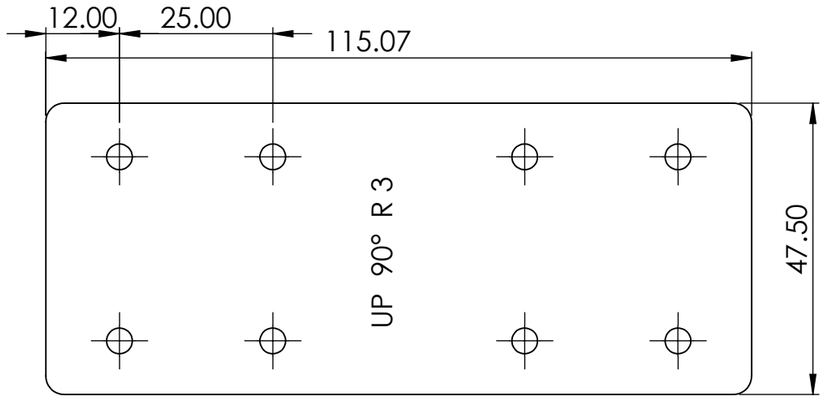



TITLE - RETRACTABLE ROOF				NIHVA TECHNOLOGIES PVT.LTD.PUNE
DWG NO - NTPL276-001-01-002-001				Website - www.nihva.com
	NAME	SIGNATURE	DATE	PROJECT NO - NTPL276-PM
DRAWN	S.W		28-03-2025	PRODUCT - RETRACTABLE ROOF
CHK'D	P.M.		28-03-2025	SITE LOCATION - GUJARAT
APPV'D	V.T.		28-03-2025	
if any queries contact - supportautomation@nihva.com				REVISION - / QTY - 1
ALL DIMENSION ARE IN mm		A3		SCALE - / SHEET 14 OF 36

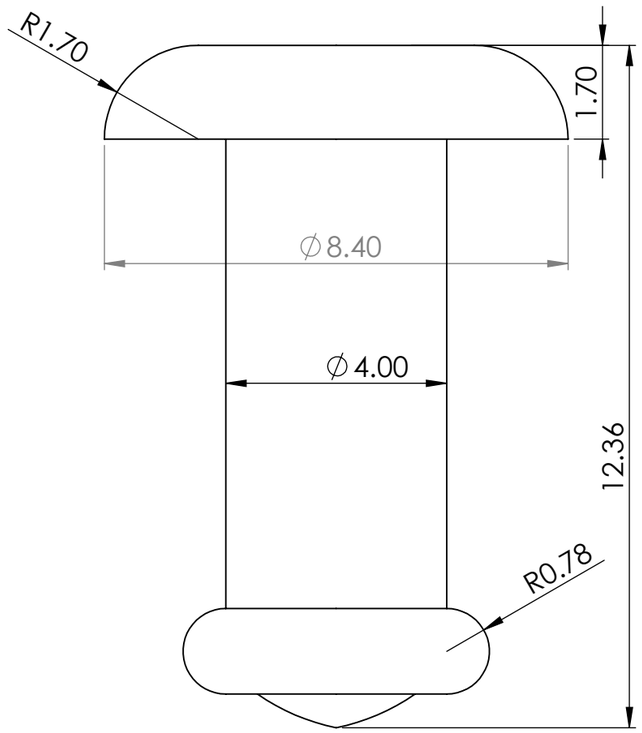

ITEM NO.	PART NUMBER	DESCRIPTION	QTY.
1	2D DRAWING SALAVI MAM rivet_iso_15977_4_x_16_0	RIVET M4X16	1

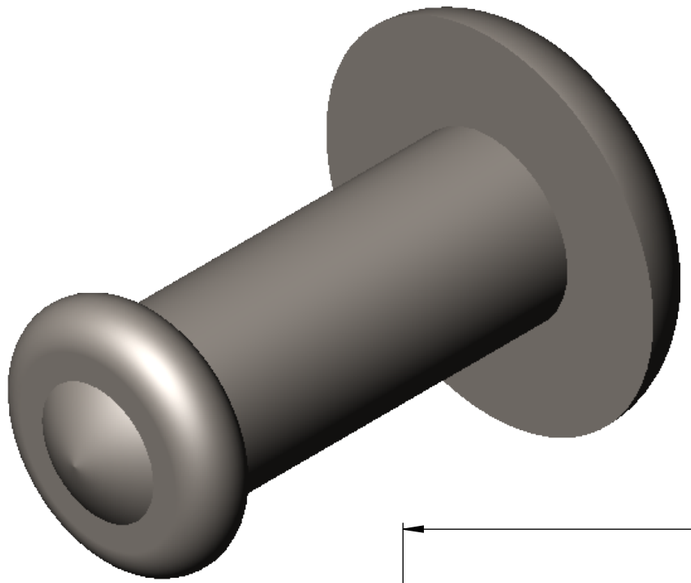

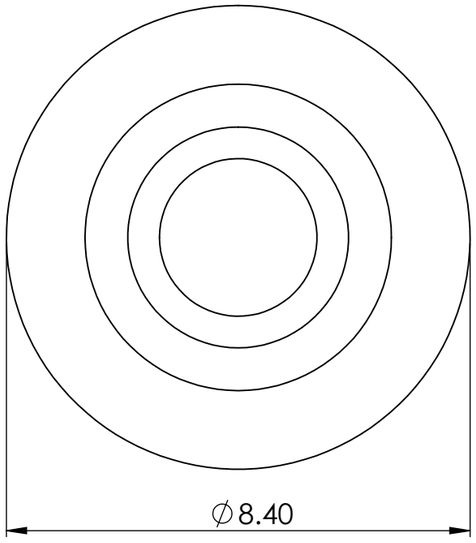


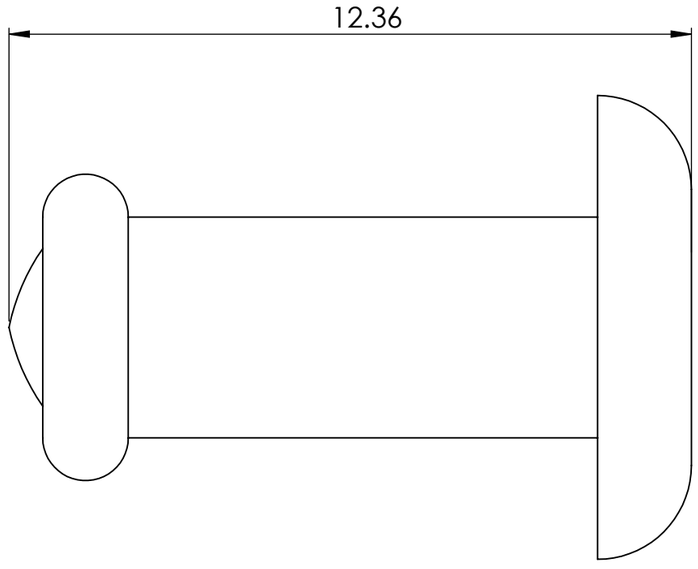



TITLE - RETRACTABLE ROOF				NIHVA TECHNOLOGIES PVT.LTD.PUNE
DWG NO - NTPL276-001-01-002-002				Website - www.nihva.com
	NAME	SIGNATURE	DATE	PROJECT NO - NTPL276-PM
DRAWN	S.W		28-03-2025	PRODUCT - RETRACTABLE ROOF
CHK'D	P.M.		28-03-2025	SITE LOCATION - GUJARAT
APPV'D	V.T.		28-03-2025	
if any queries contact - supportautomation@nihva.com				REVISION - QTY - 1
ALL DIMENSION ARE IN mm			A3	SCALE - SHEET 15 OF 36

ITEM NO.	PART NUMBER	DESCRIPTION	QTY.
1	L PLATE	SS304- 91X106X3 MM THK	1
2	2D DRAWING SALAVI MAM rivet_iso_15977_4_x_16_0	RIVET M4X16	10

Total Quantity - 12

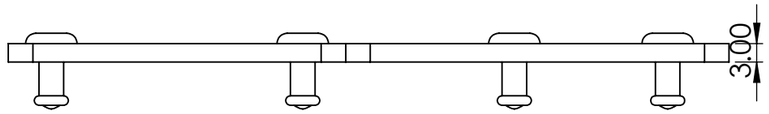


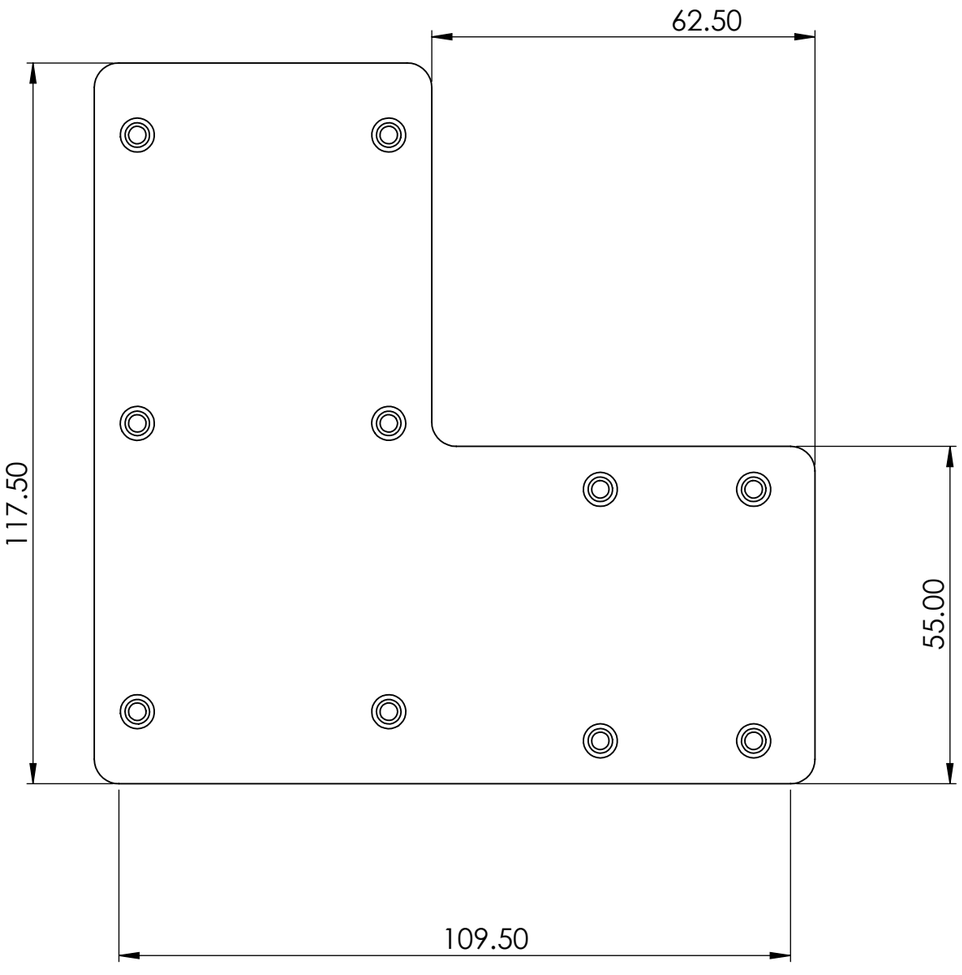


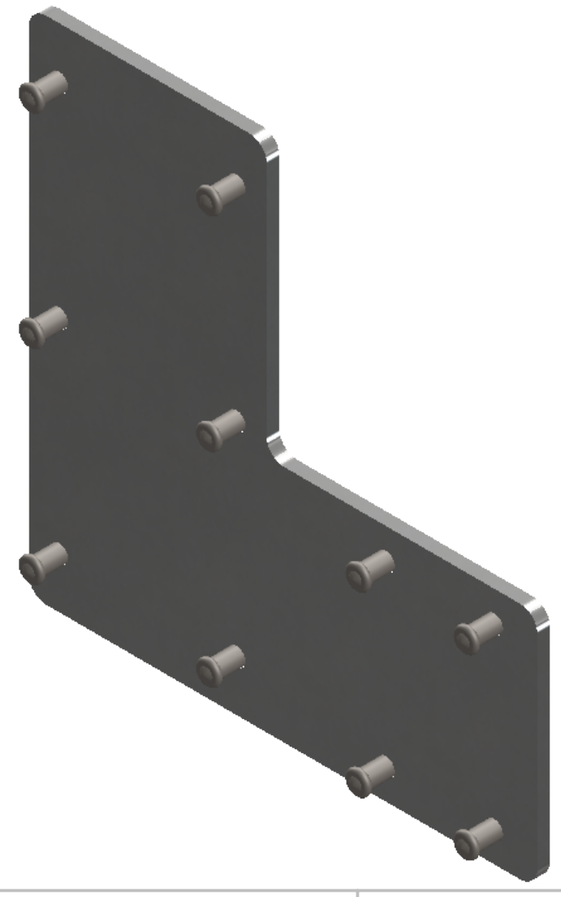


TITLE - RETRACTABLE ROOF				NIHVA TECHNOLOGIES PVT.LTD.PUNE
DWG NO - NTPL276-001-01-003-000				Website - www.nihva.com
	NAME	SIGNATURE	DATE	PROJECT NO - NTPL276-PM
DRAWN	S.W		28-03-2025	PRODUCT - RETRACTABLE ROOF
CHK'D	P.M.		28-03-2025	SITE LOCATION - GUJARAT
APPV'D	V.T.		28-03-2025	
if any queries contact - supportautomation@nihva.com				REVISION - QTY - 1
ALL DIMENSION ARE IN mm			A3	SCALE - SHEET 16 OF 36

ITEM NO.	PART NUMBER	DESCRIPTION	QTY.
1	L PLATE	SS304- 91X106X3 MM THK	12

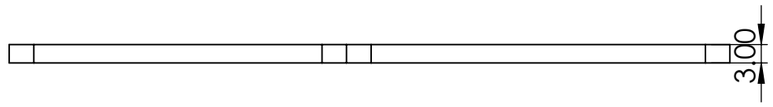

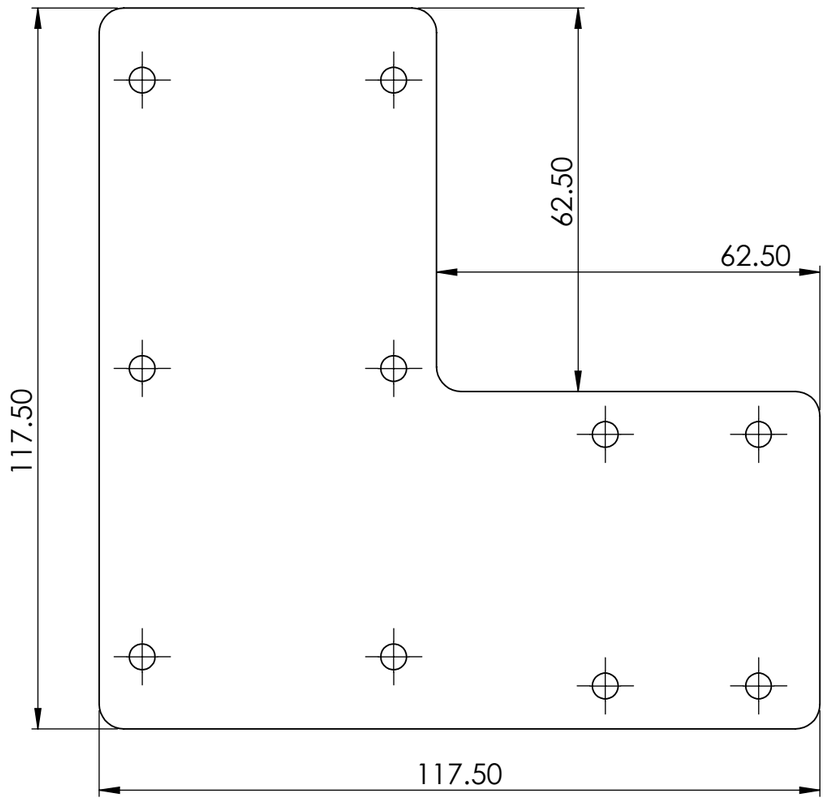


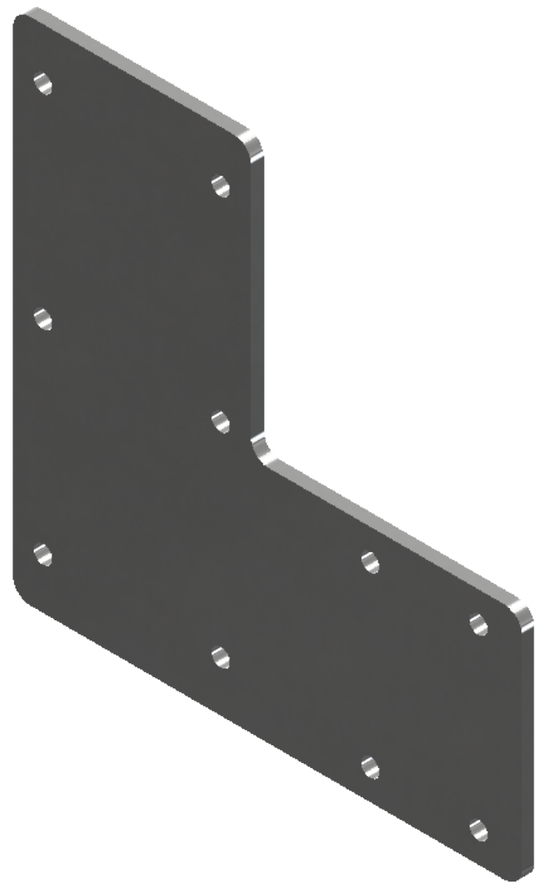



TITLE - RETRACTABLE ROOF				NIHVA TECHNOLOGIES PVT.LTD.PUNE
DWG NO - NTPL276-001-01-003-001				Website - www.nihva.com
	NAME	SIGNATURE	DATE	PROJECT NO - NTPL276-PM
DRAWN	S.W		28-03-2025	PRODUCT - RETRACTABLE ROOF
CHK'D	P.M.		28-03-2025	SITE LOCATION - GUJARAT
APPV'D	V.T.		28-03-2025	
if any queries contact - supportautomation@nihva.com				REVISION - QTY - 1
ALL DIMENSION ARE IN mm		A3		SCALE - SHEET 17 OF 36

ITEM NO.	PART NUMBER	DESCRIPTION	QTY.
1	T PLATE	SS304 -117.5X156X3 MM THK	1
2	2D DRAWING SALAVI MAM rivet_iso_15977_4_x_16_0	RIVET M4X16	10

Total Quantity - 12

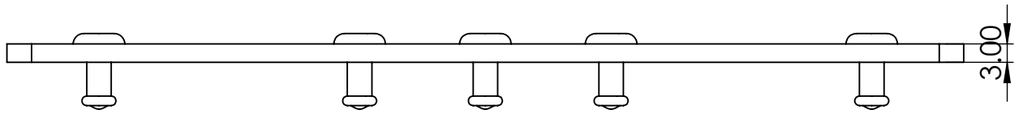


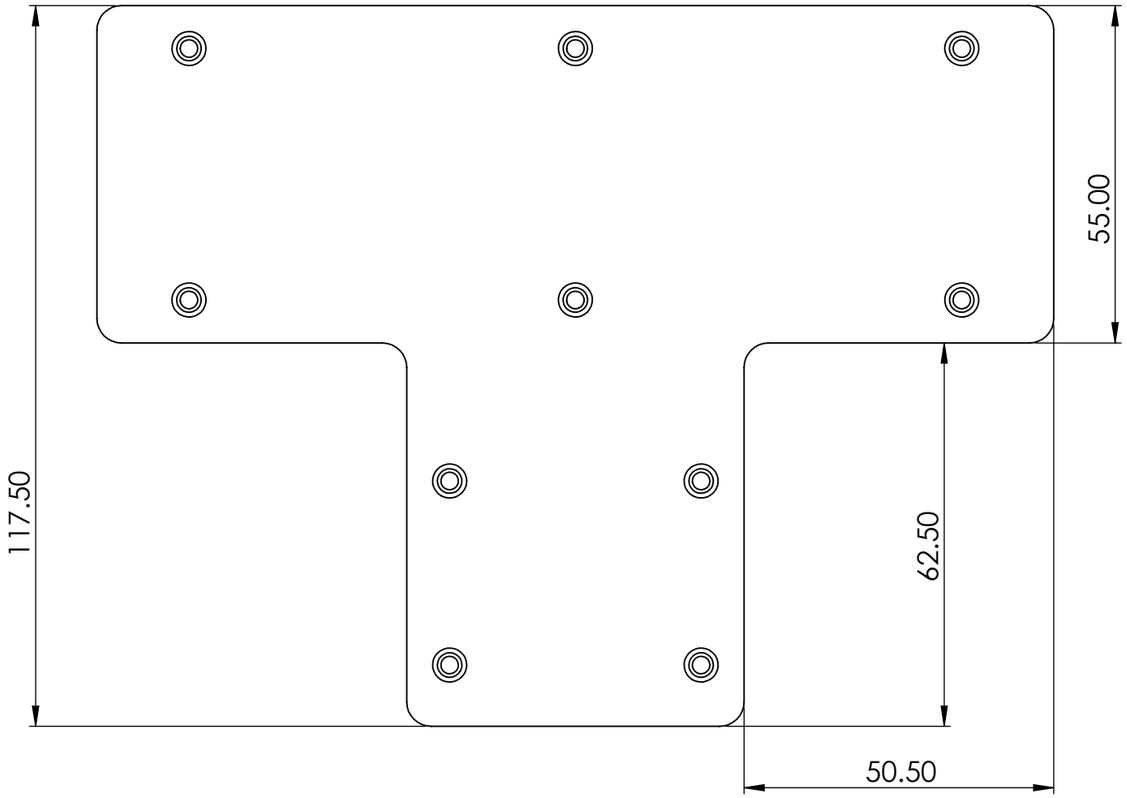


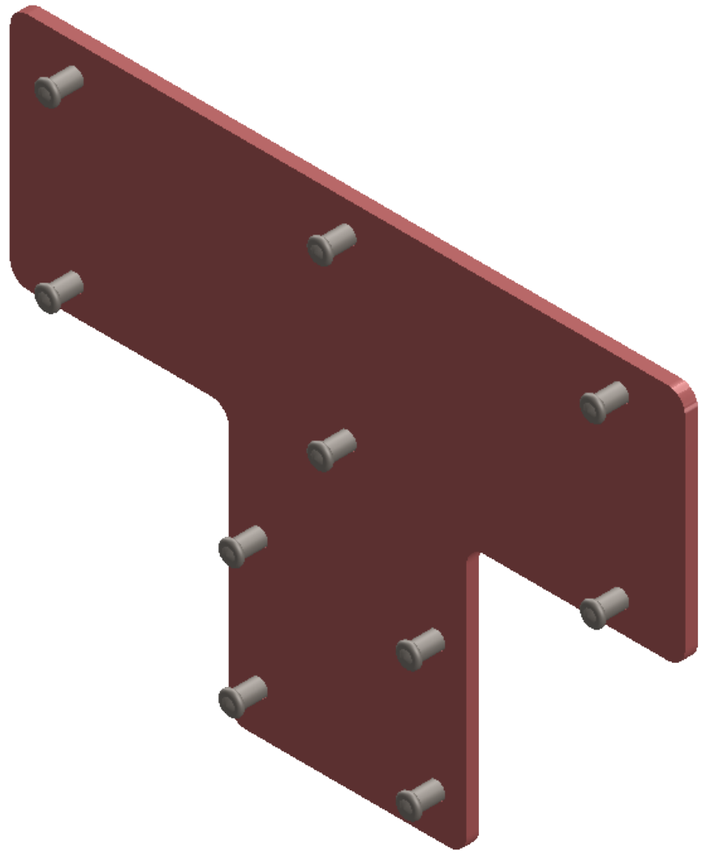


TITLE - RETRACTABLE ROOF				NIHVA TECHNOLOGIES PVT.LTD.PUNE
DWG NO - NTPL276-001-01-004-000				Website - www.nihva.com
	NAME	SIGNATURE	DATE	PROJECT NO - NTPL276-PM
DRAWN	S.W		28-03-2025	PRODUCT - RETRACTABLE ROOF
CHK'D	P.M.		28-03-2025	SITE LOCATION - GUJARAT
APPV'D	V.T.		28-03-2025	
if any queries contact - supportautomation@nihva.com				REVISION - QTY - 1
ALL DIMENSION ARE IN mm			A3	SCALE - SHEET 18 OF 36

ITEM NO.	PART NUMBER	DESCRIPTION	QTY.
1	T PLATE	SS304 -117.5X156X3 MM THK	12

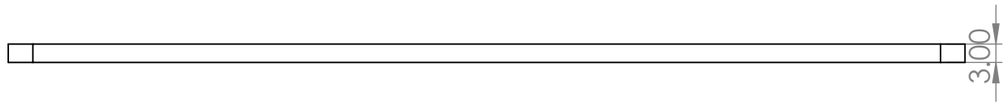


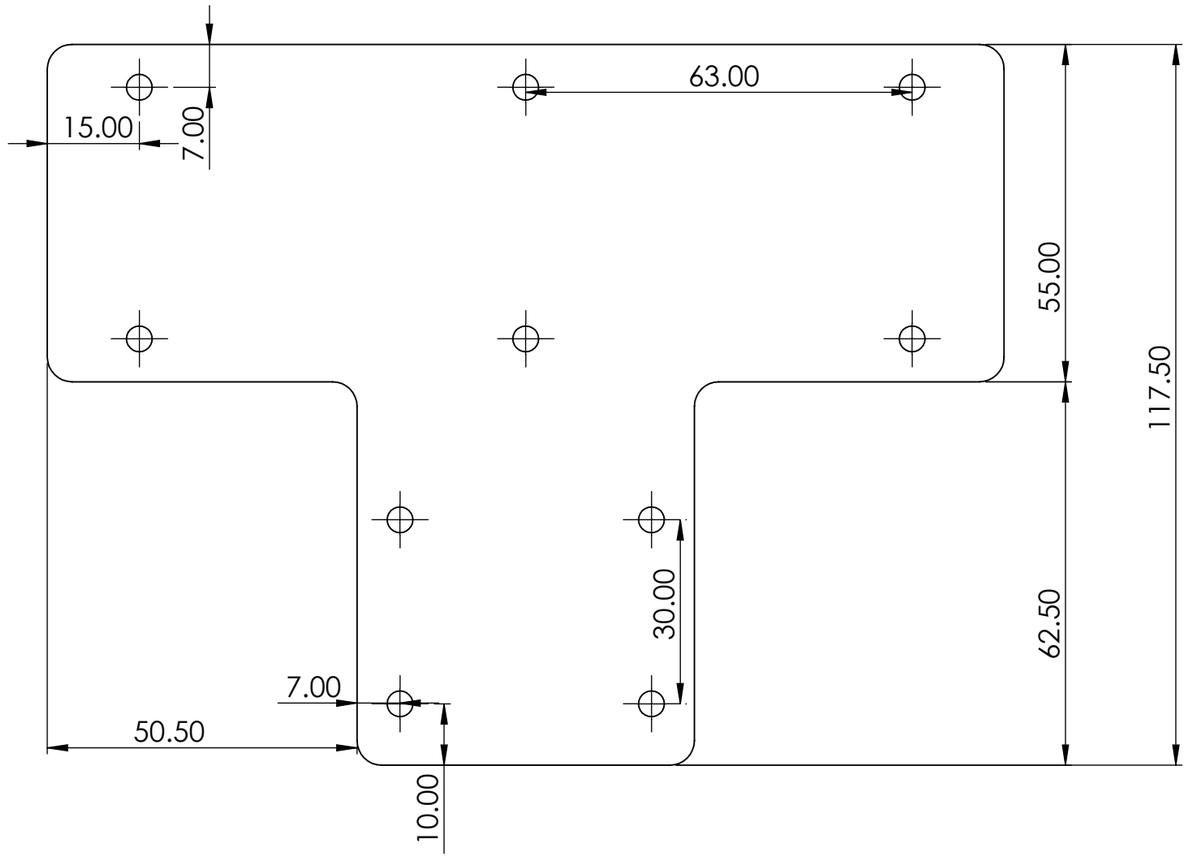


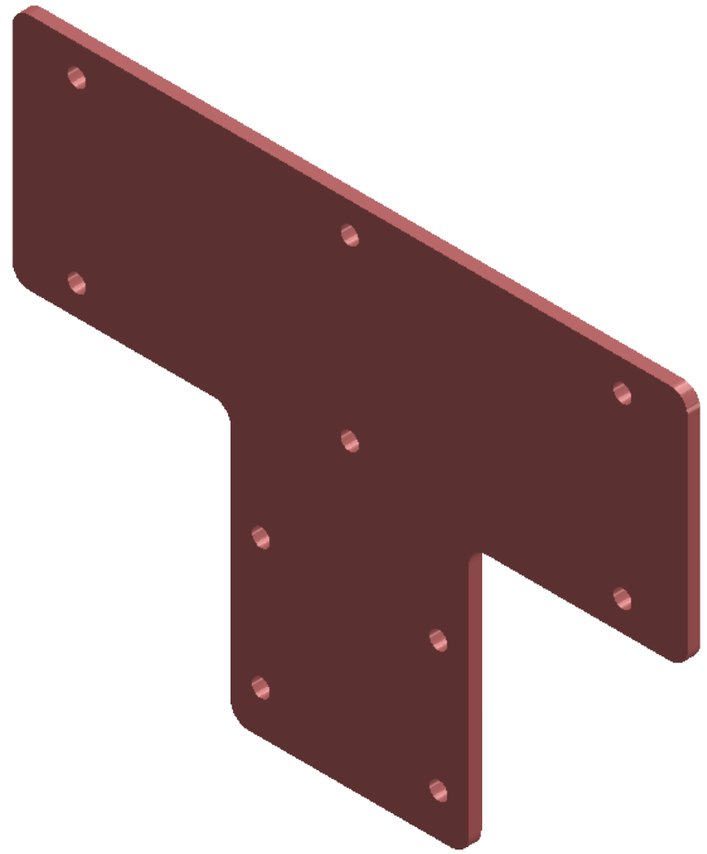


TITLE - RETRACTABLE ROOF				NIHVA TECHNOLOGIES PVT.LTD.PUNE
DWG NO - NTPL276-001-01-004-001				Website - www.nihva.com
	NAME	SIGNATURE	DATE	PROJECT NO - NTPL276-PM
DRAWN	S.W		28-03-2025	PRODUCT - RETRACTABLE ROOF
CHK'D	P.M.		28-03-2025	SITE LOCATION - GUJARAT
APPV'D	V.T.		28-03-2025	
if any queries contact - supportautomation@nihva.com				REVISION - / QTY - 1
ALL DIMENSION ARE IN mm		A3		SCALE - / SHEET 19 OF 36


ITEM NO.	PART NUMBER	DESCRIPTION	QTY.
1	2D DRAWING SALAVI MAM PROFILE L ANGLE WELDING PLATE	JOINING PLATE Al metal	1
		Sheet	1

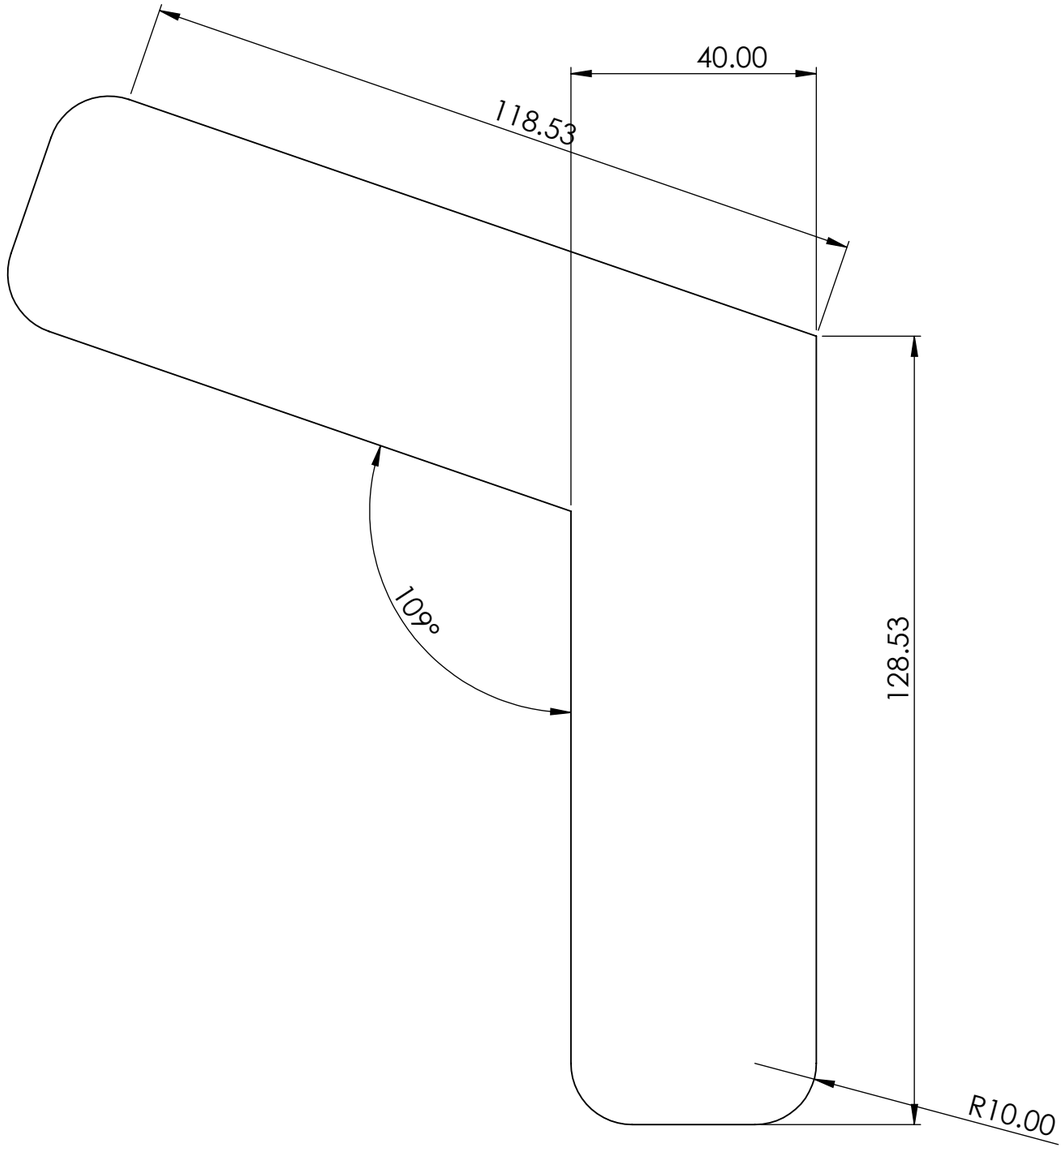


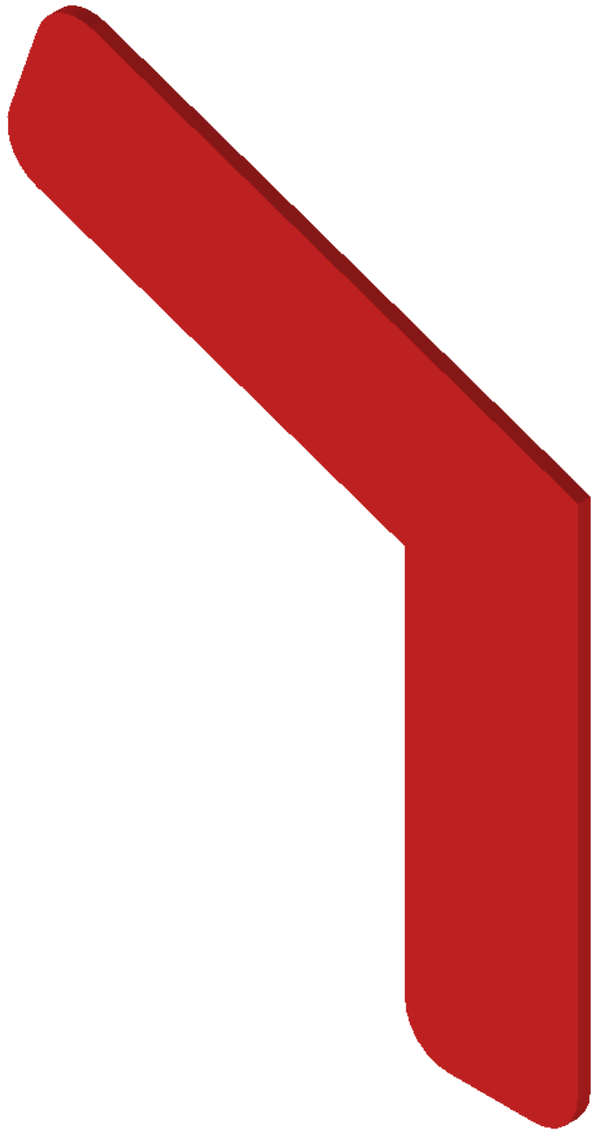


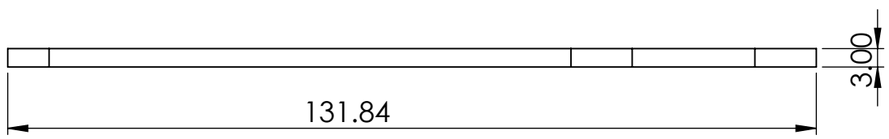


TITLE - RETRACTABLE ROOF				NIHVA TECHNOLOGIES PVT.LTD.PUNE
DWG NO - NTPL276-001-01-000-001				Website - www.nihva.com
	NAME	SIGNATURE	DATE	PROJECT NO - NTPL276-PM
DRAWN	S.W		28-03-2025	PRODUCT - RETRACTABLE ROOF
CHK'D	P.M.		28-03-2025	SITE LOCATION - GUJARAT
APPV'D	V.T.		28-03-2025	
if any queries contact - supportautomation@nihva.com				REVISION - QTY - 1
ALL DIMENSION ARE IN mm		A3		SCALE - SHEET 20 OF 36

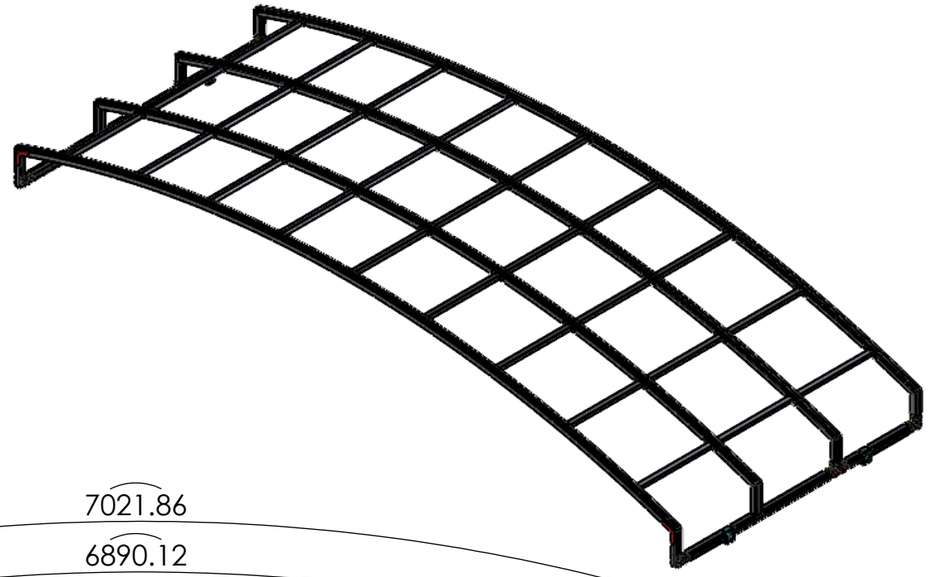

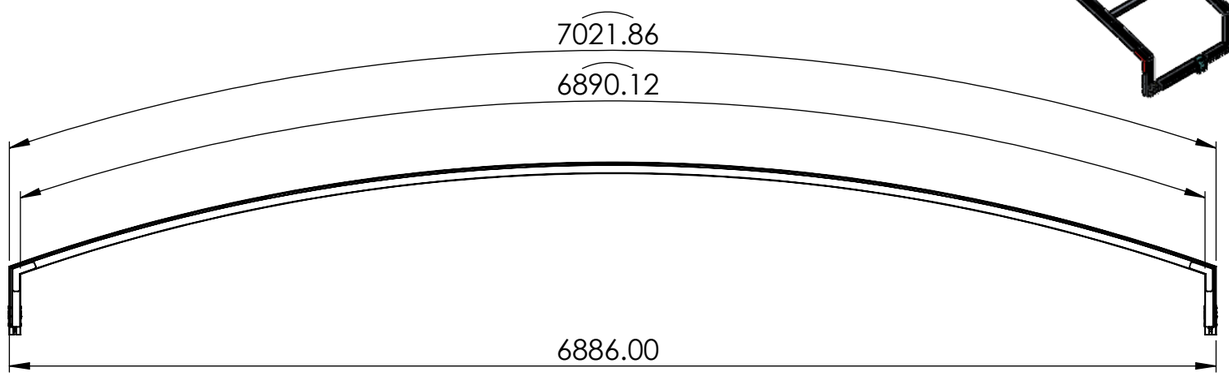

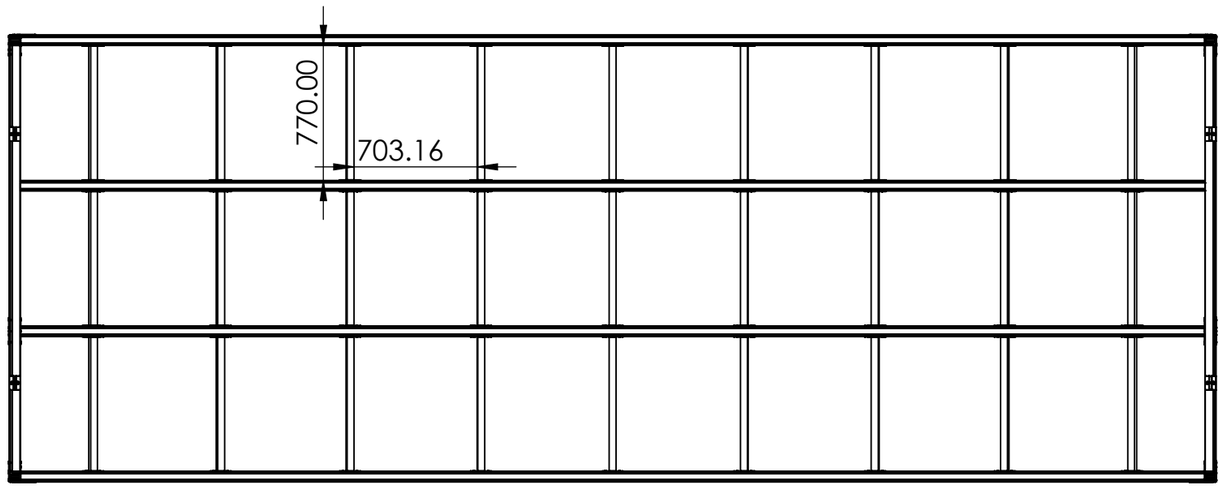

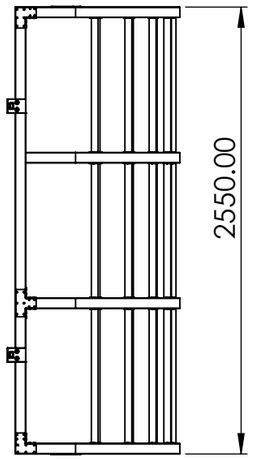

ITEM NO.	PART NUMBER	DESCRIPTION	QTY.
1	2D DRAWING SALAVI MAM NTPL-268-PM-PANEL_02	PANEL_02 FRAME	1
2	AL Support tube SQ TUBE 40X40X1.5 MM L-734 MM	AL INTERMEDIAT SUPPORT TUBE	27
3	2D DRAWING SALAVI MAM rivet_iso_15977_4_x_16_0	RIVET M4X16	79
4	T PLATE	JOINING PLATE	4
5	L PALTE	JOINING PLATE	8
6	L ANGLE PLATE	JOINING PLATE	8
7	2D DRAWING SALAVI MAM PROFILE L ANGLE WELDING PLATE	JOINING PLATE Al metal	4
8	2D DRAWING SALAVI MAM BEARING BLOCK ASM WITH SHOULDER BOLT	SLIDING BLOCK	4

PANEL-2

TITLE - RETRACTABLE ROOF

DWG NO - NTPL276-001-02-000-000

NIHVA TECHNOLOGIES PVT.LTD.PUNE

Website - www.nihva.com

	NAME	SIGNATURE	DATE
DRAWN	S.W		28-03-2025
CHK'D	P.M.		28-03-2025
APPV'D	V.T.		28-03-2025

PROJECT NO - NTPL276-PM

PRODUCT - RETRACTABLE ROOF

SITE LOCATION - GUJARAT

if any queries contact - supportautomation@nihva.com

REVISION -


QTY - 1

ALL DIMENSION ARE IN mm

A3


SCALE -


ITEM NO.	PART NUMBER	DESCRIPTION	QTY.
1	2D DRAWING SALAVI MAM NTPL-268-PM-PANEL_02	PANEL_02 FRAME	1

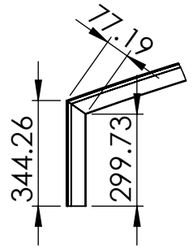



DETAIL P

SCALE 1 : 20

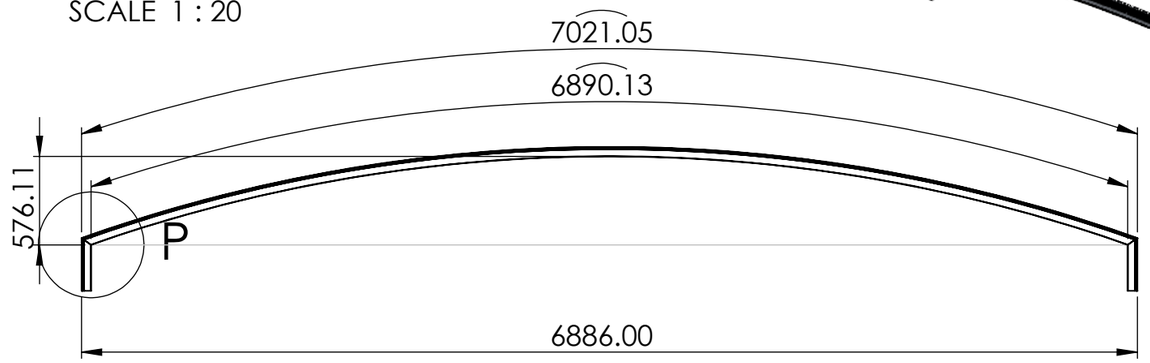


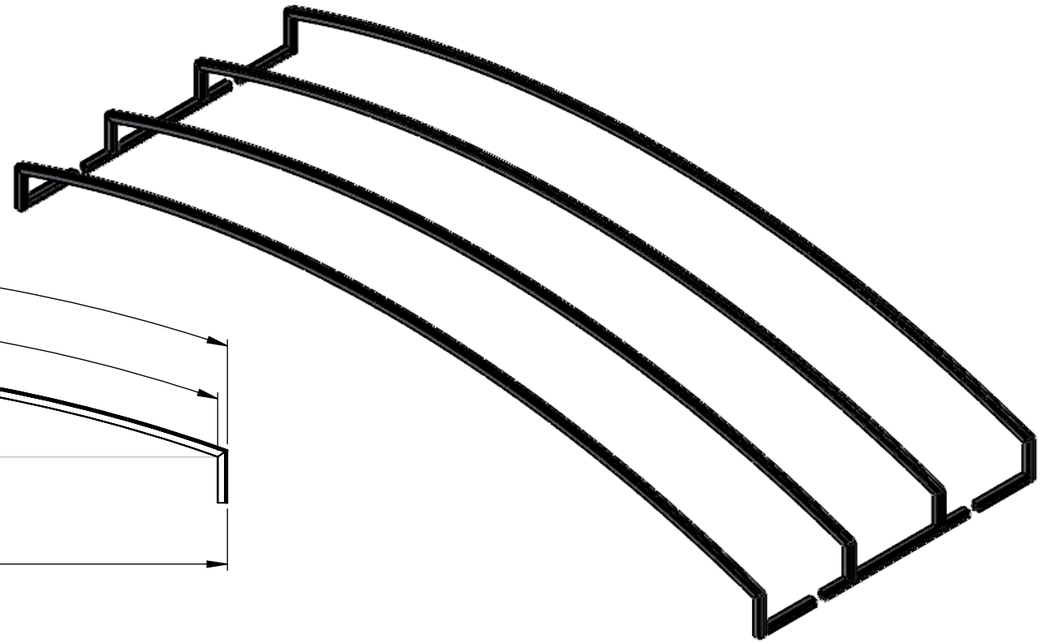


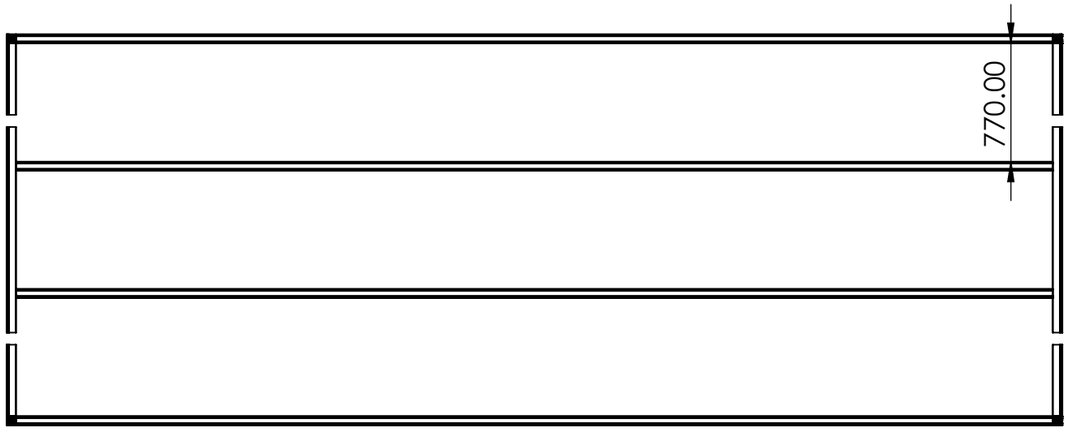


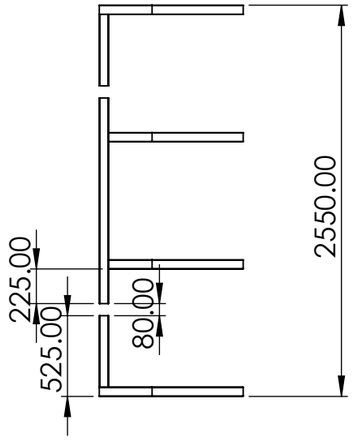


TITLE - RETRACTABLE ROOF				NIHVA TECHNOLOGIES PVT.LTD.PUNE
DWG NO - NTPL276-001-02-000-001				Website - www.nihva.com
	NAME	SIGNATURE	DATE	PROJECT NO - NTPL276-PM
DRAWN	S.W		28-03-2025	PRODUCT - RETRACTABLE ROOF
CHK'D	P.M.		28-03-2025	SITE LOCATION - GUJARAT
APPV'D	V.T.		28-03-2025	
if any queries contact - supportautomation@nihva.com				REVISION - QTY - 1
ALL DIMENSION ARE IN mm			A3	SCALE - SHEET 22 OF 36

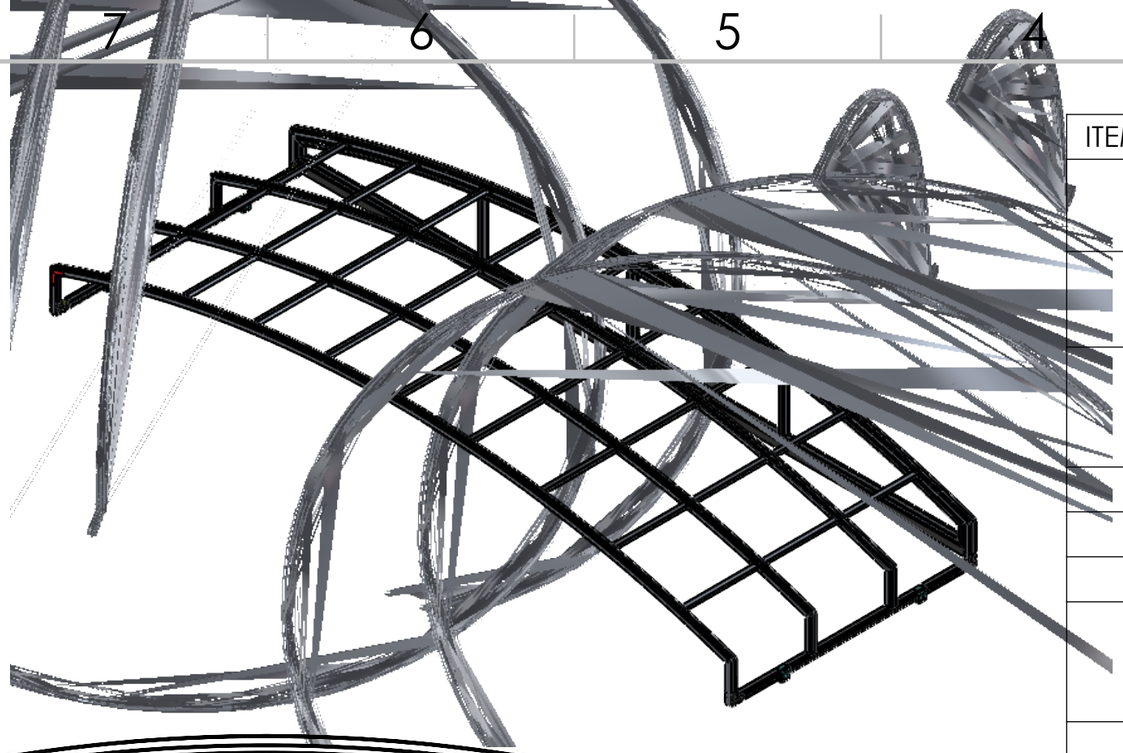

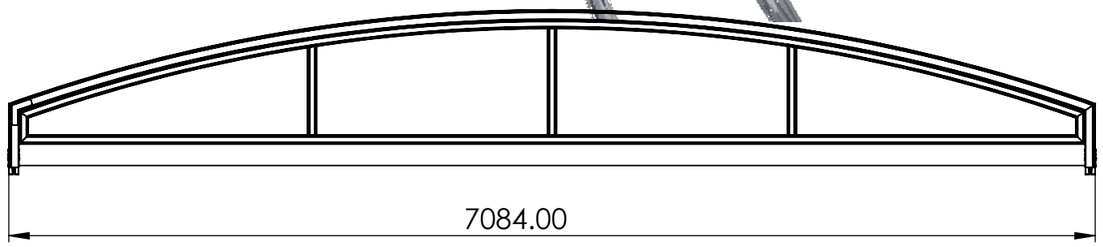

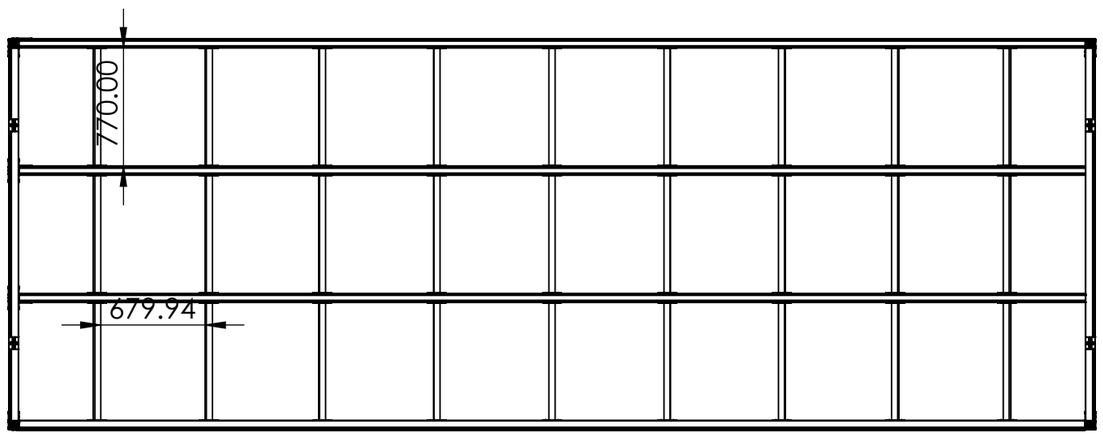

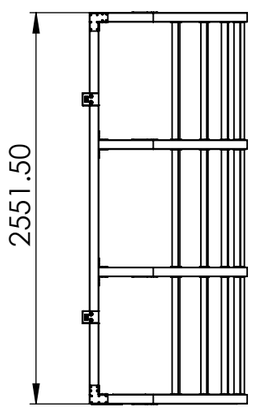

ITEM NO.	PART NUMBER	DESCRIPTION	QTY.
1	2D DRAWING SALAVI MAM NTPL-268-PM-PANEL_03	PANEL_03 FRAME	1
2	AL Support tube SQ TUBE 40X40X1.5 MM L-734 MM	AL INTERMEDIAT SUPPORT TUBE	27
3	2D DRAWING SALAVI MAM rivet_iso_15977_4_x_16_0	RIVET M4X16	79
4	T PLATE	JOINING PLATE	4
5	L PALTE	JOINING PLATE	8
6	L ANGLE PLATE	JOINING PLATE	8
7	2D DRAWING SALAVI MAM PROFILE L ANGLE WELDING PLATE	JOINING PLATE Al metal	4
8	2D DRAWING SALAVI MAM BEARING BLOCK ASM WITH SHOULDER BOLT	SLIDING BLOCK	4
9	2D DRAWING SALAVI MAM ENCLOSURE NTPL-268-PM-PANEL_03	ENCLOSURE _03	1
10	2D DRAWING EPDM RUBBER_BIG PANEL		1

PANEL-3

TITLE - RETRACTABLE ROOF

DWG NO - NTPL276-001-03-000-000

NIHVA Technologies Pvt. Ltd.

NIHVA TECHNOLOGIES PVT.LTD.PUNE

Website - www.nihva.com

	NAME	SIGNATURE	DATE
DRAWN	S.W		28-03-2025
CHK'D	P.M.		28-03-2025
APPV'D	V.T.		28-03-2025

PROJECT NO - NTPL276-PM

PRODUCT - RETRACTABLE ROOF

SITE LOCATION - GUJARAT

if any queries contact - supportautomation@nihva.com

REVISION -


QTY - 1


ALL DIMENSION ARE IN mm


A3


SCALE -

ITEM NO.	PART NUMBER	DESCRIPTION	QTY.
1	2D DRAWING SALAVI MAM ENCLOSURE NTPL-268-PM-PANEL_03	ENCLOSURE _03	1

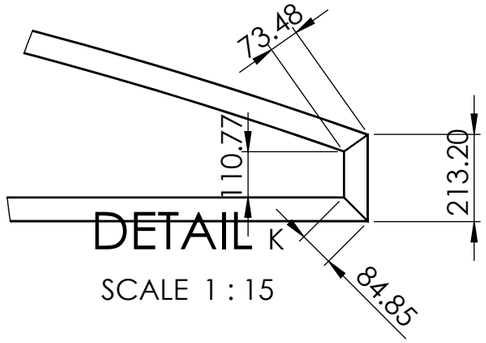

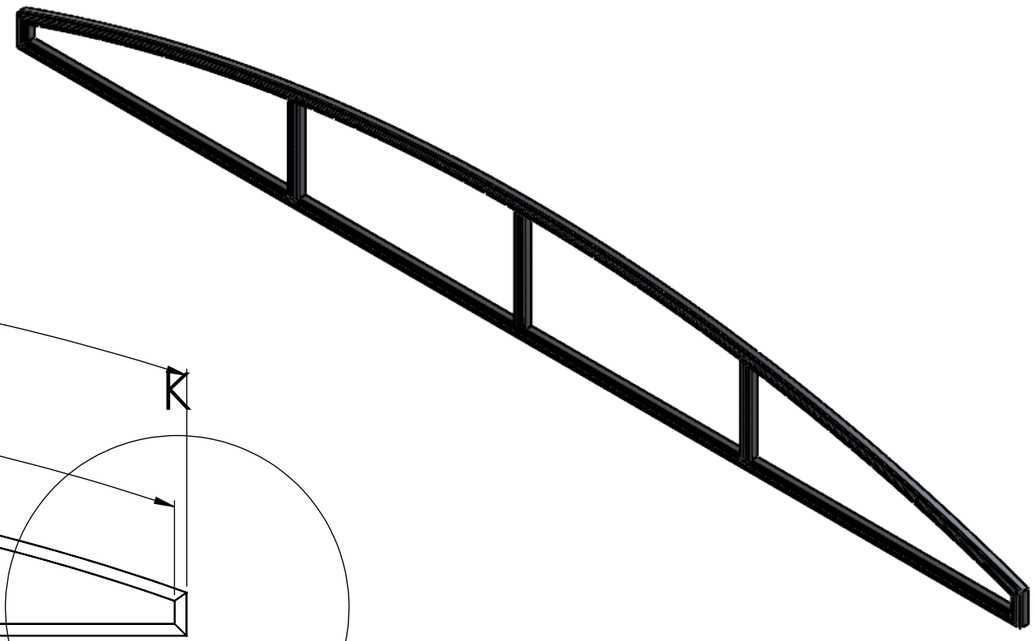

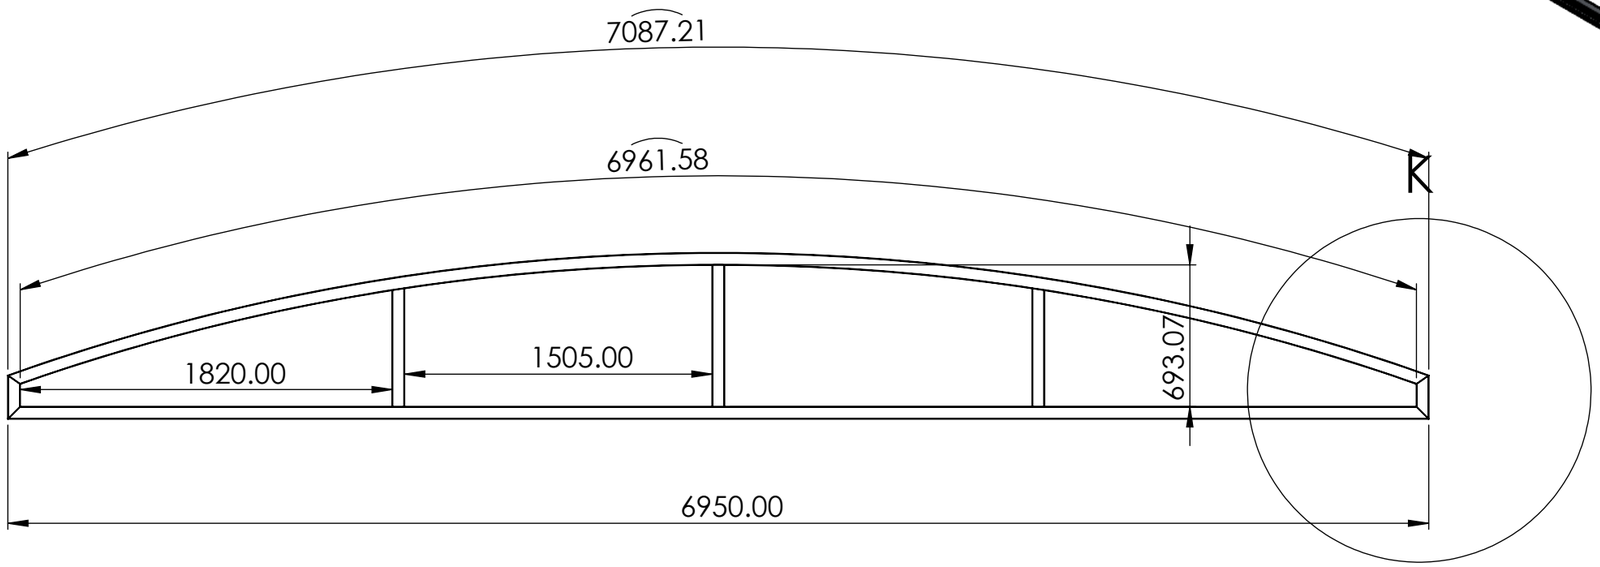


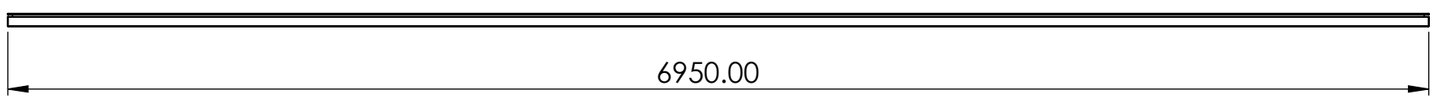




TITLE - RETRACTABLE ROOF				NIHVA TECHNOLOGIES PVT.LTD.PUNE
DWG NO - NTPL276-001-03-000-001				Website - www.nihva.com
	NAME	SIGNATURE	DATE	PROJECT NO - NTPL276-PM
DRAWN	S.W		28-03-2025	PRODUCT - RETRACTABLE ROOF
CHK'D	P.M.		28-03-2025	SITE LOCATION - GUJARAT
APPV'D	V.T.		28-03-2025	
if any queries contact - supportautomation@nihva.com				REVISION - / QTY - 1
ALL DIMENSION ARE IN mm			A3	SCALE - / SHEET 24 OF 36


ITEM NO.	PART NUMBER	DESCRIPTION	QTY.
1	2D DRAWING SALAVI MAM NTPL-268-PM-PANEL_03	PANEL_03 FRAME	1

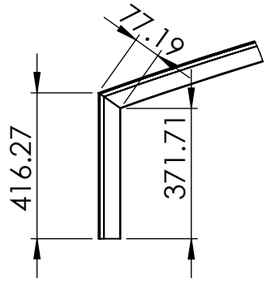


DETAIL Q

SCALE 2 : 35

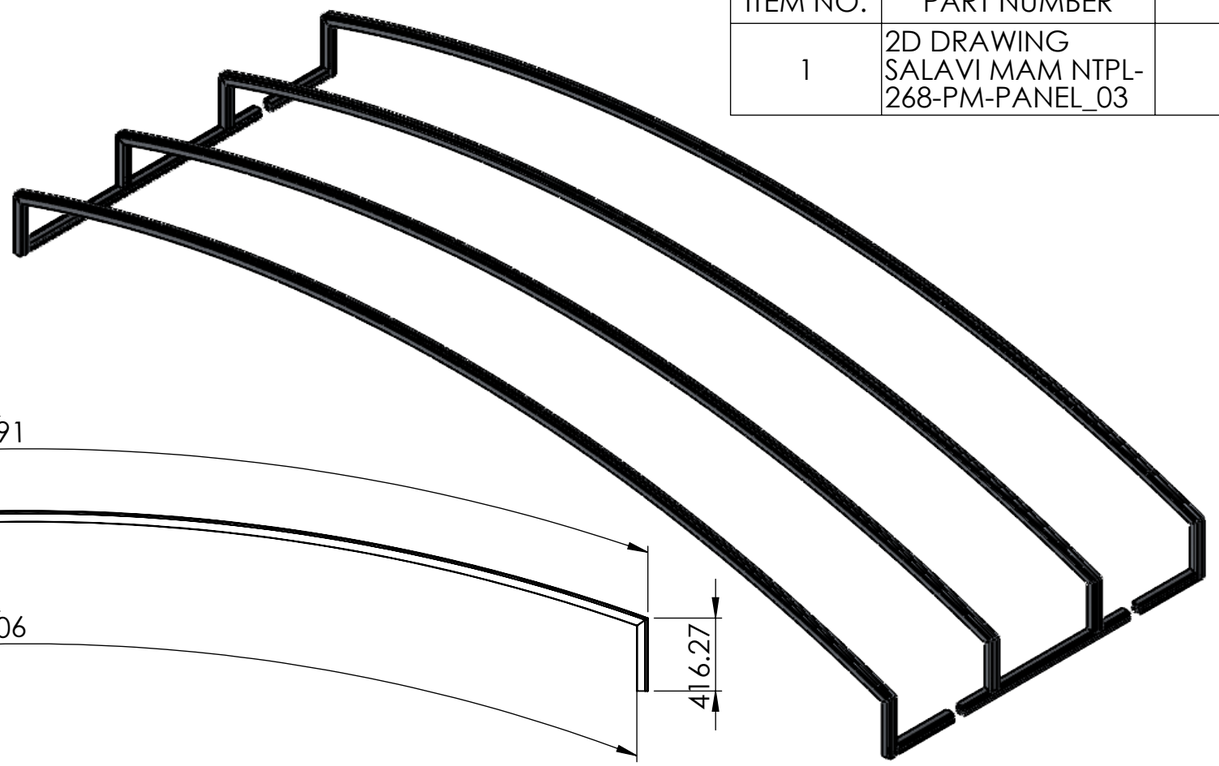

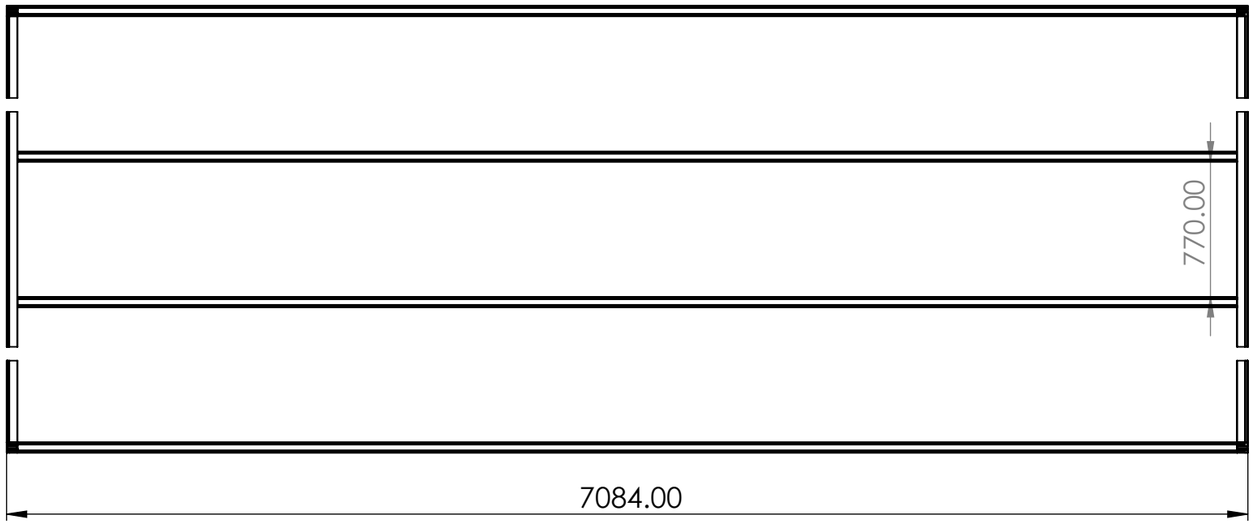


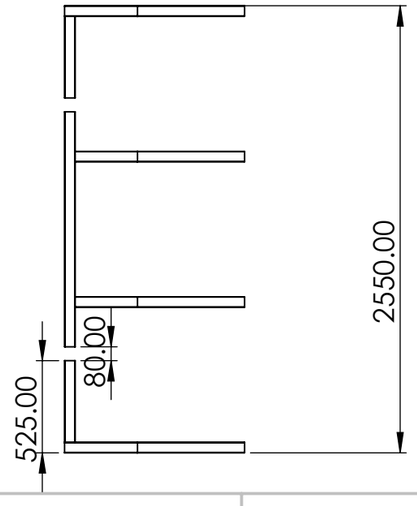



TITLE - RETRACTABLE ROOF				NIHVA TECHNOLOGIES PVT.LTD.PUNE Website - www.nihva.com
DWG NO - NTPL276-001-03-000-002				
	NAME	SIGNATURE	DATE	PROJECT NO - NTPL276-PM
DRAWN	S.W		28-03-2025	PRODUCT - RETRACTABLE ROOF
CHK'D	P.M.		28-03-2025	SITE LOCATION - GUJARAT
APPV'D	V.T.		28-03-2025	
if any queries contact - supportautomation@nihva.com				REVISION - / QTY - 1
ALL DIMENSION ARE IN mm			A3	SCALE - / SHEET 25 OF 36


ITEM NO.	PART NUMBER	DESCRIPTION	QTY.
1	C- CHANEL MTG BASE PLATE	320X50X10MM THK	1
2	C - CHANEL	70X30X575	2
3	C- CHANEL JOINING PLATE	35X40X10MM THK	2
4	2D DRAWING SALAVI MAM BUSBAR MTG PLATE		2

Total Quantity - 22

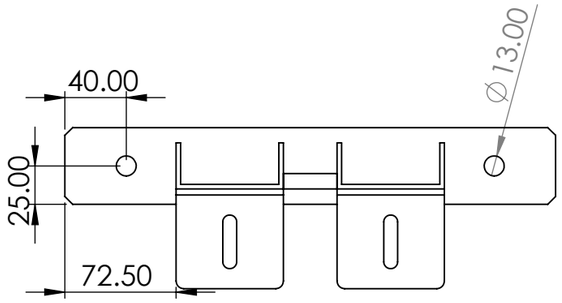

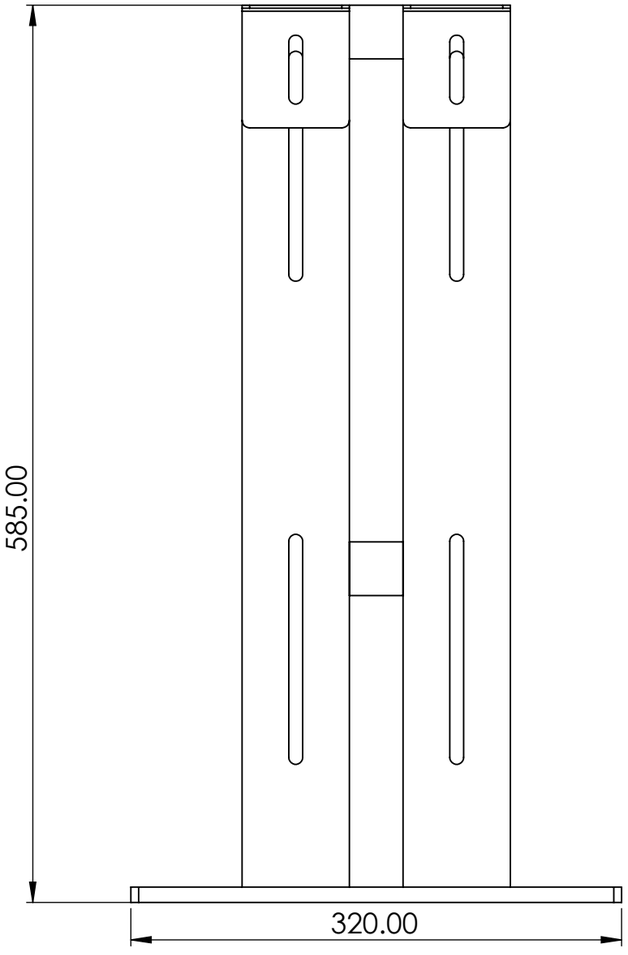


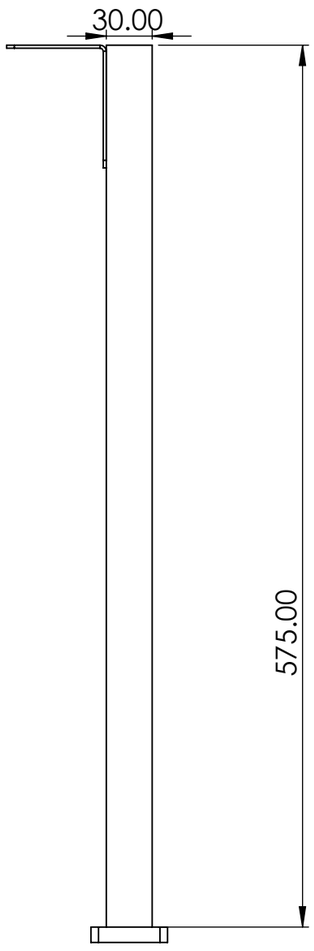


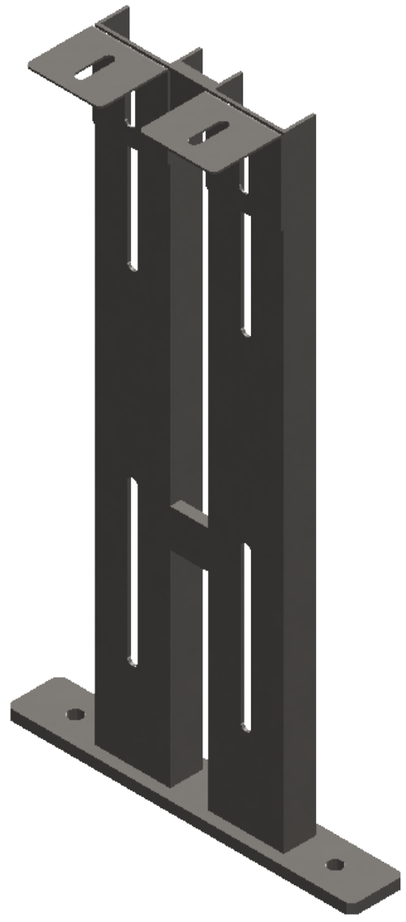

TITLE - RETRACTABLE ROOF				NIHVA TECHNOLOGIES PVT.LTD.PUNE
DWG NO - NTPL276-001-04-000-000				Website - www.nihva.com
	NAME	SIGNATURE	DATE	PROJECT NO - NTPL276-PM
DRAWN	S.W		28-03-2025	PRODUCT - RETRACTABLE ROOF
CHK'D	P.M.		28-03-2025	SITE LOCATION - GUJARAT
APPV'D	V.T.		28-03-2025	
if any queries contact - supportautomation@nihva.com				REVISION - QTY - 1
ALL DIMENSION ARE IN mm			A3	SCALE - SHEET 26 OF 36

ITEM NO.	PART NUMBER	DESCRIPTION	QTY.
1	C - CHANEL	70X30X575	22

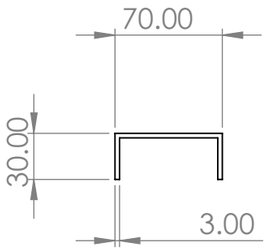


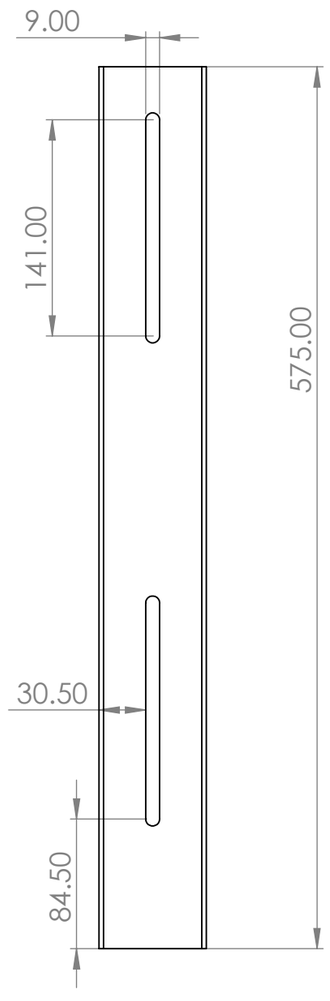






TITLE - RETRACTABLE ROOF				NIHVA TECHNOLOGIES PVT.LTD.PUNE
DWG NO - NTPL276-001-04-000-001				Website - www.nihva.com
	NAME	SIGNATURE	DATE	PROJECT NO - NTPL276-PM
DRAWN	S.W		28-03-2025	PRODUCT - RETRACTABLE ROOF
CHK'D	P.M.		28-03-2025	SITE LOCATION - GUJARAT
APPV'D	V.T.		28-03-2025	
if any queries contact - supportautomation@nihva.com				REVISION - QTY - 1
ALL DIMENSION ARE IN mm			A3	SCALE - SHEET 27 OF 36

ITEM NO.	PART NUMBER	DESCRIPTION	QTY.
1	BUSBAR FLASHER MTG L PLATE	70X142X2 MM THK	22

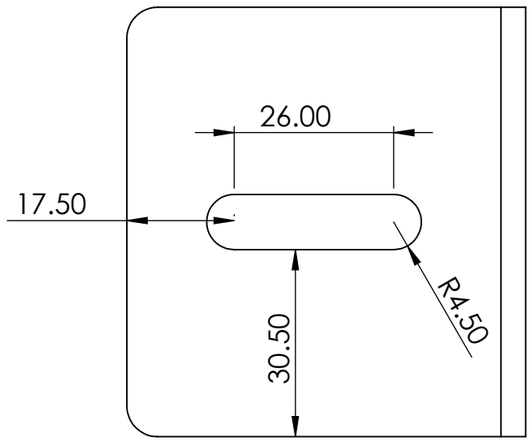

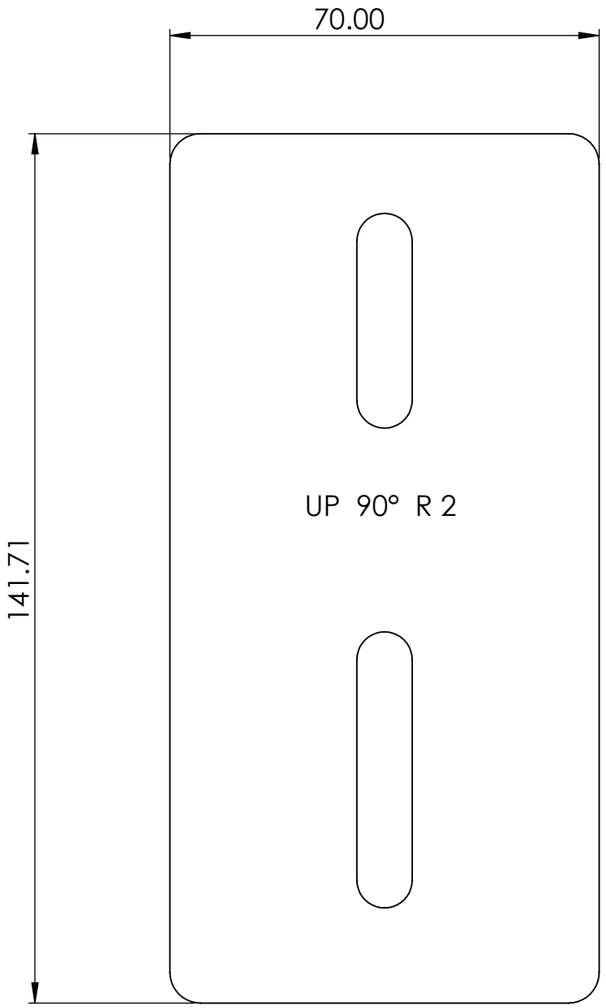


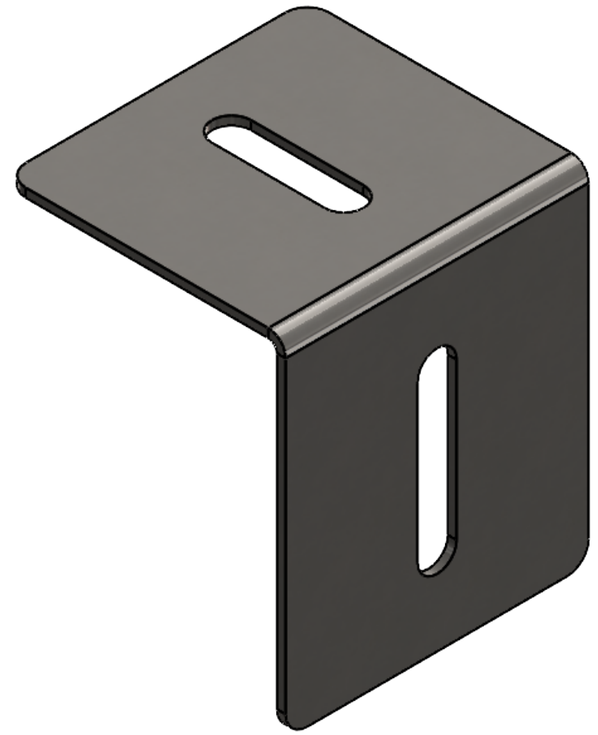


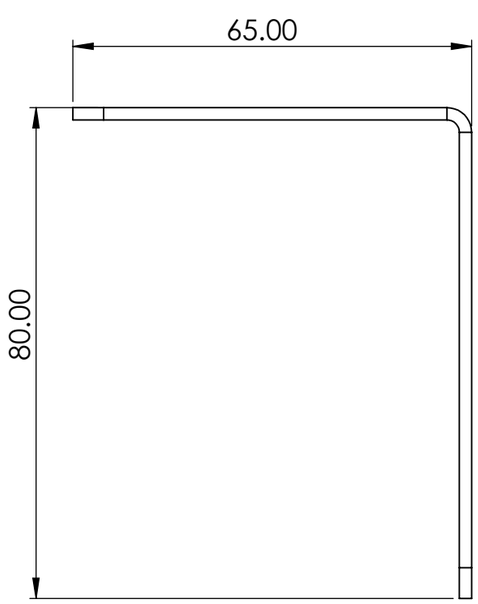

TITLE - RETRACTABLE ROOF				NIHVA TECHNOLOGIES PVT.LTD.PUNE
DWG NO - NTPL276-001-04-000-002				Website - www.nihva.com
	NAME	SIGNATURE	DATE	PROJECT NO - NTPL276-PM
DRAWN	S.W		28-03-2025	PRODUCT - RETRACTABLE ROOF
CHK'D	P.M.		28-03-2025	SITE LOCATION - GUJARAT
APPV'D	V.T.		28-03-2025	
if any queries contact - supportautomation@nihva.com				REVISION - QTY - 1
ALL DIMENSION ARE IN mm			A3	SCALE - SHEET 28 OF 36


ITEM NO.	PART NUMBER	DESCRIPTION	QTY.
1	C- CHANEL JOINING PLATE	35X40X10MM THK	22

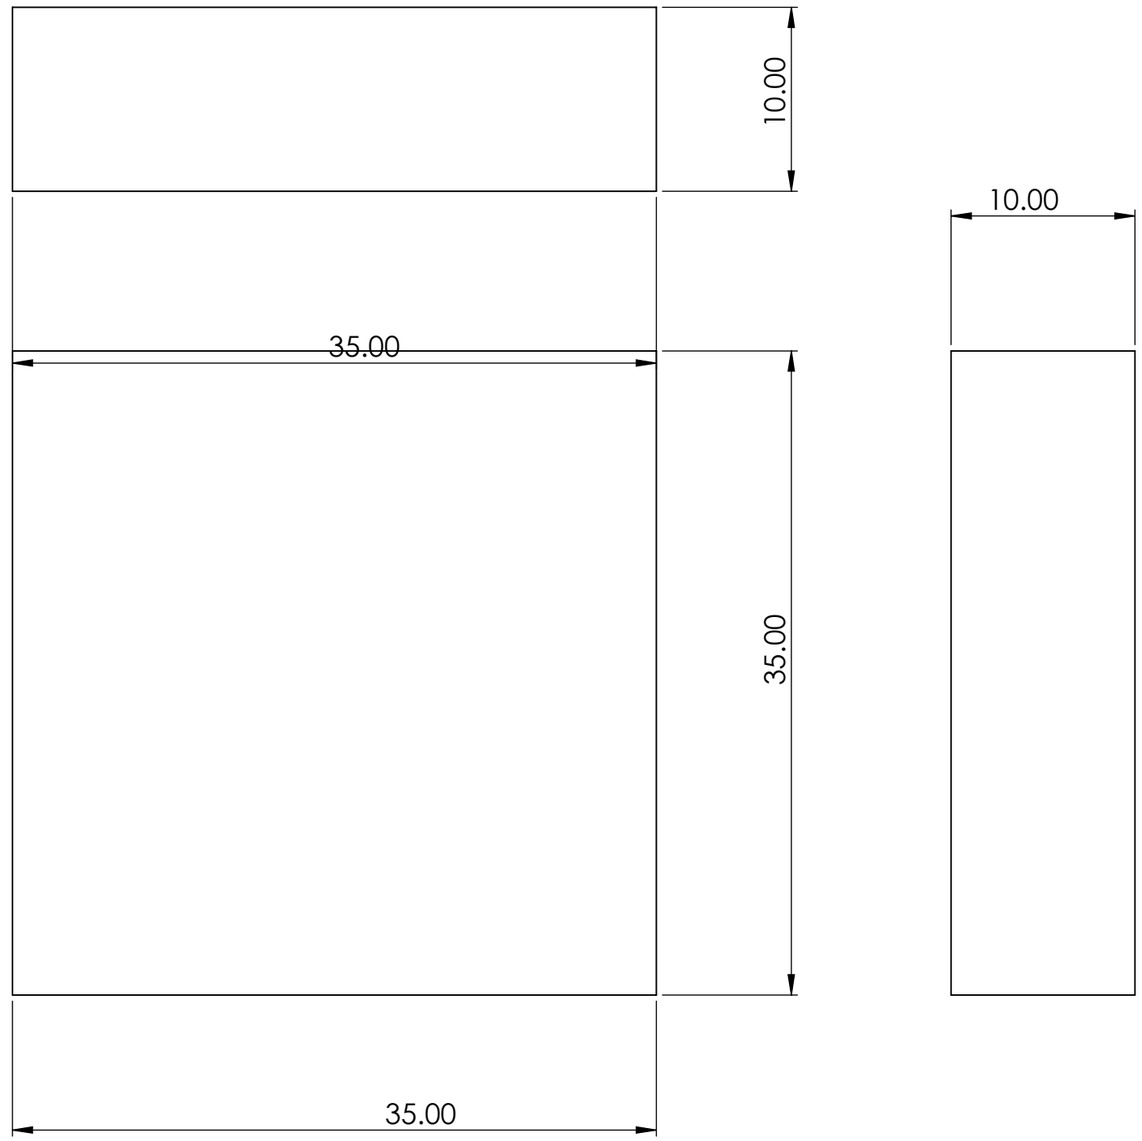


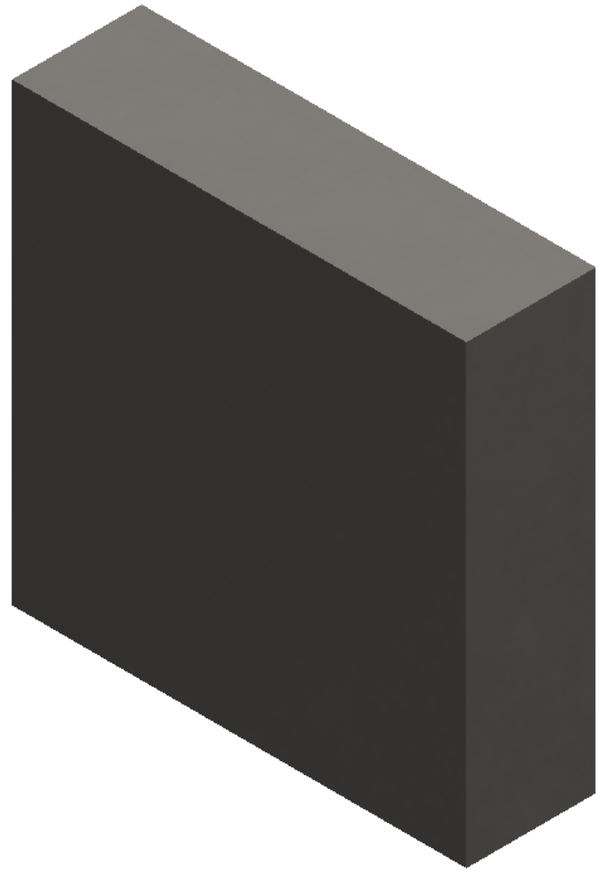



TITLE - RETRACTABLE ROOF				NIHVA TECHNOLOGIES PVT.LTD.PUNE
DWG NO - NTPL276-001-04-000-003				Website - www.nihva.com
	NAME	SIGNATURE	DATE	PROJECT NO - NTPL276-PM
DRAWN	S.W		28-03-2025	PRODUCT - RETRACTABLE ROOF
CHK'D	P.M.		28-03-2025	SITE LOCATION - GUJARAT
APPV'D	V.T.		28-03-2025	
if any queries contact - supportautomation@nihva.com				REVISION - QTY - 1
ALL DIMENSION ARE IN mm			A3	SCALE - SHEET 29 OF 36

ITEM NO.	PART NUMBER	DESCRIPTION	QTY.
1	MOTOR MTG BRACKET NICE 1T	MS	1
2	2D DRAWING SALAVI MAM NICE RB 1T		1

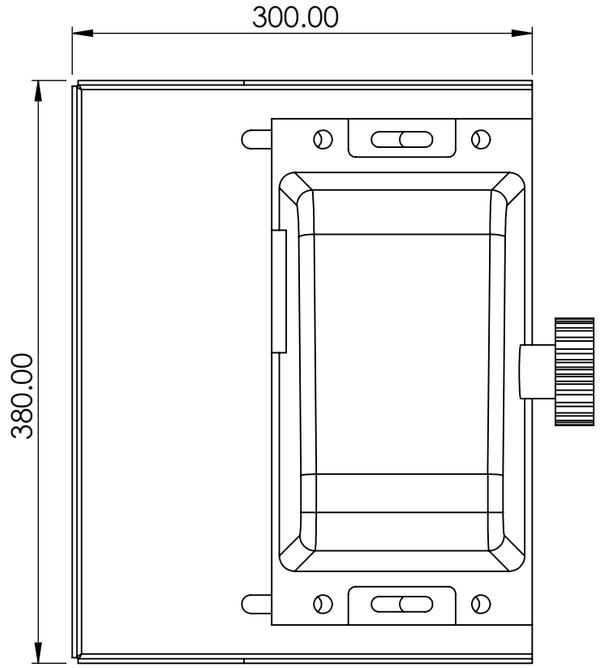

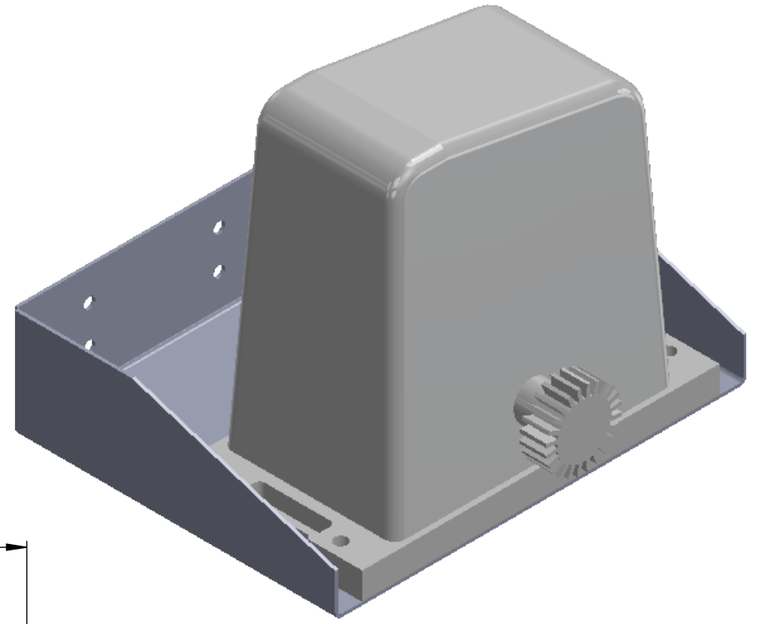


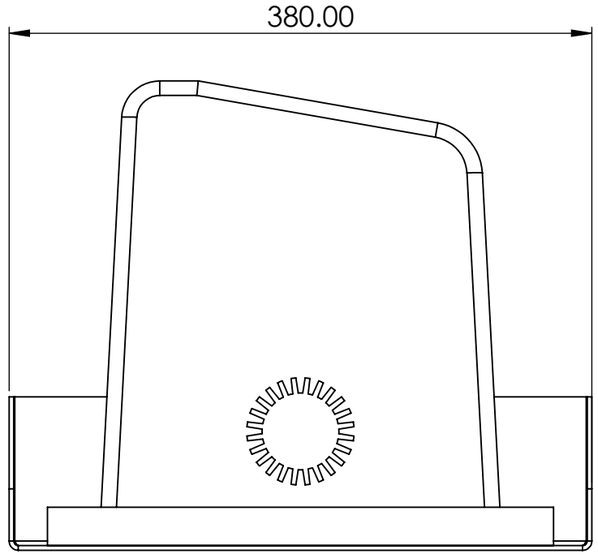


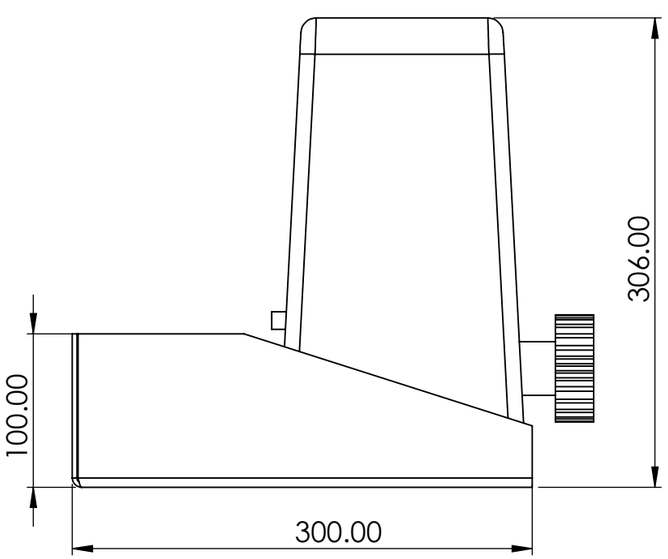



TITLE - RETRACTABLE ROOF				NIHVA TECHNOLOGIES PVT.LTD.PUNE
DWG NO - NTPL276-001-05-000-000				Website - www.nihva.com
	NAME	SIGNATURE	DATE	PROJECT NO - NTPL276-PM
DRAWN	S.W		28-03-2025	PRODUCT - RETRACTABLE ROOF
CHK'D	P.M.		28-03-2025	SITE LOCATION - GUJARAT
APPV'D	V.T.		28-03-2025	
if any queries contact - supportautomation@nihva.com				REVISION - QTY - 1
ALL DIMENSION ARE IN mm		A3		SCALE - SHEET 30 OF 36


ITEM NO.	PART NUMBER	DESCRIPTION	QTY.
1	MOTOR MTG BRACKET NICE 1T	MS	1
		Sheet	1

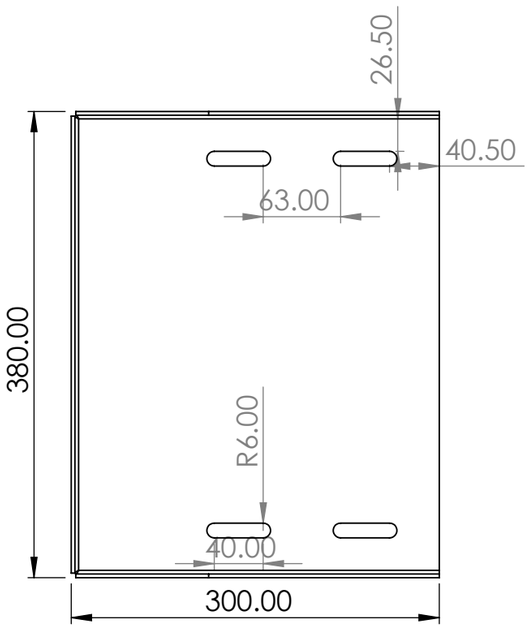

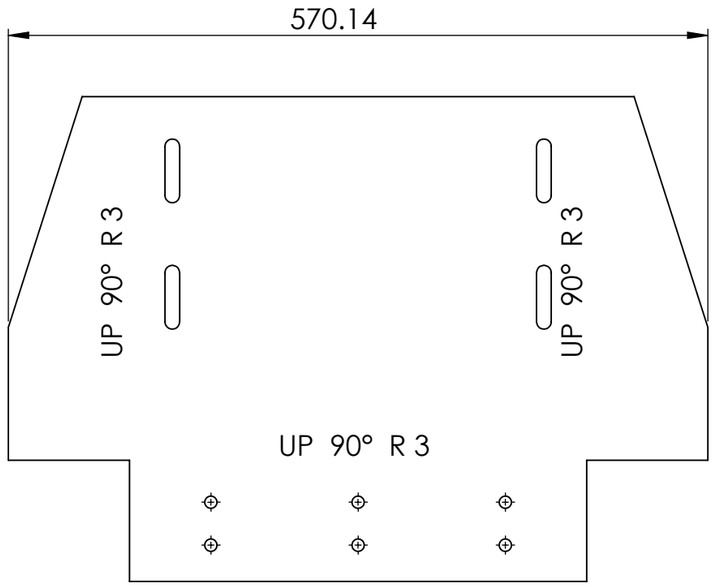

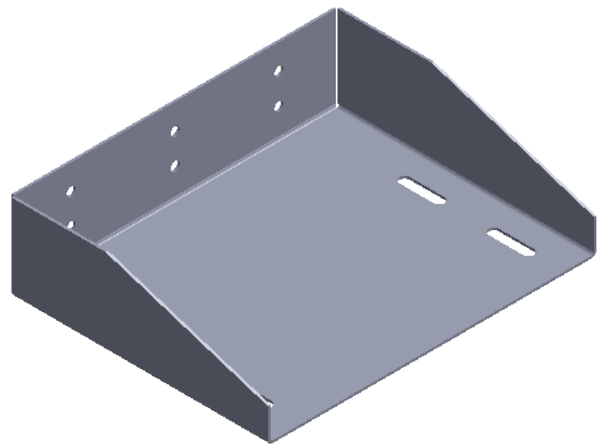


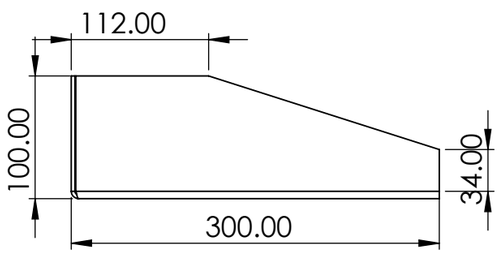


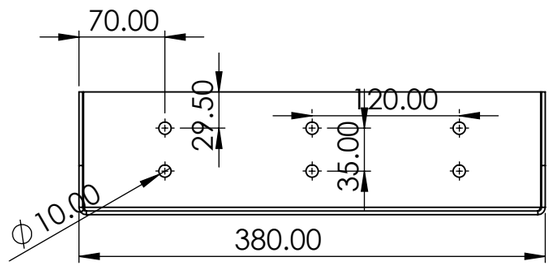



TITLE - RETRACTABLE ROOF				NIHVA TECHNOLOGIES PVT.LTD.PUNE
DWG NO - NTPL276-001-05-000-001				Website - www.nihva.com
	NAME	SIGNATURE	DATE	PROJECT NO - NTPL276-PM
DRAWN	S.W		28-03-2025	PRODUCT - RETRACTABLE ROOF
CHK'D	P.M.		28-03-2025	SITE LOCATION - GUJARAT
APPV'D	V.T.		28-03-2025	
if any queries contact - supportautomation@nihva.com				REVISION - QTY - 1
ALL DIMENSION ARE IN mm		A3		SCALE - SHEET 31 OF 36

ITEM NO.	PART NUMBER	DESCRIPTION	QTY.
1	2D DRAWING SALAVI MAM NICE RB 1T		1

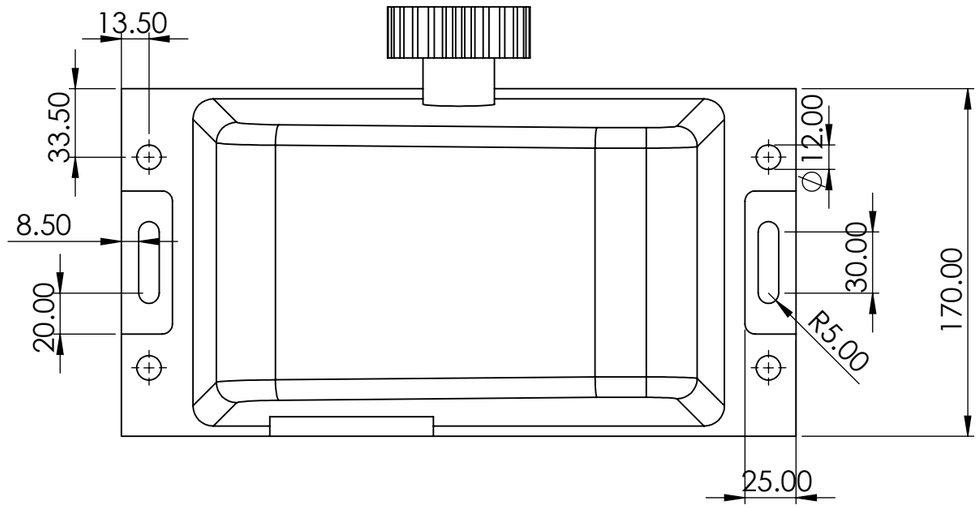


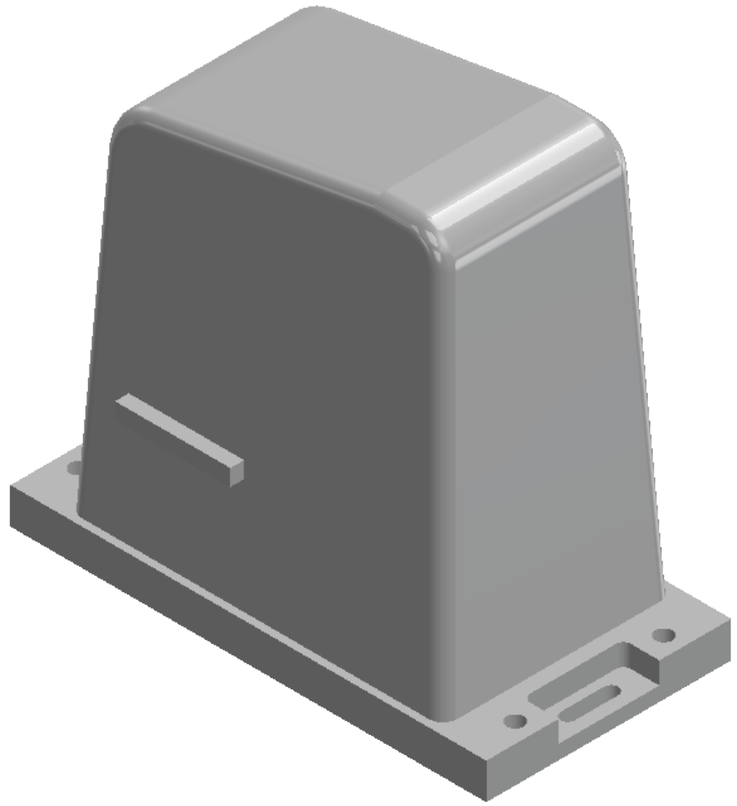


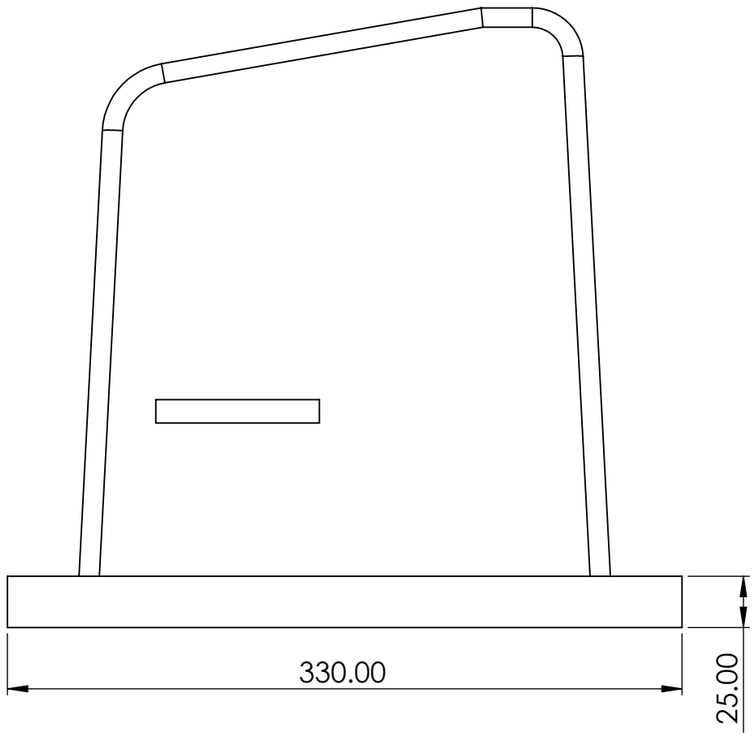


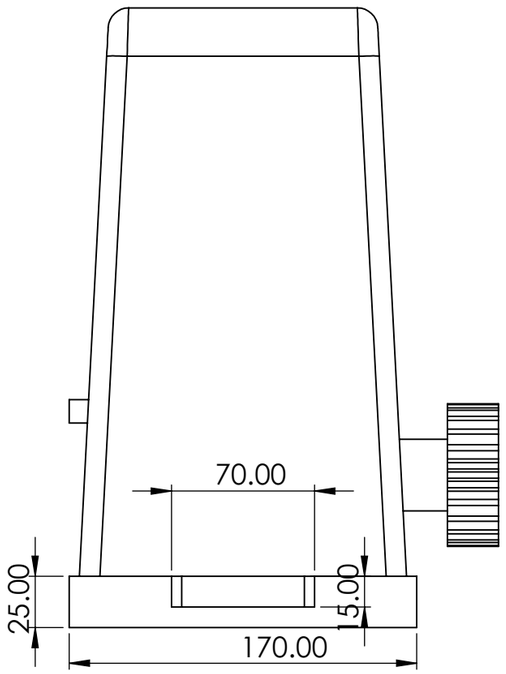

TITLE - RETRACTABLE ROOF				NIHVA TECHNOLOGIES PVT.LTD.PUNE
DWG NO - NTPL276-001-05-000-002				Website - www.nihva.com
	NAME	SIGNATURE	DATE	PROJECT NO - NTPL276-PM
DRAWN	S.W		28-03-2025	PRODUCT - RETRACTABLE ROOF
CHK'D	P.M.		28-03-2025	SITE LOCATION - GUJARAT
APPV'D	V.T.		28-03-2025	
if any queries contact - supportautomation@nihva.com				REVISION - QTY - 1
ALL DIMENSION ARE IN mm			A3	SCALE - SHEET 32 OF 36

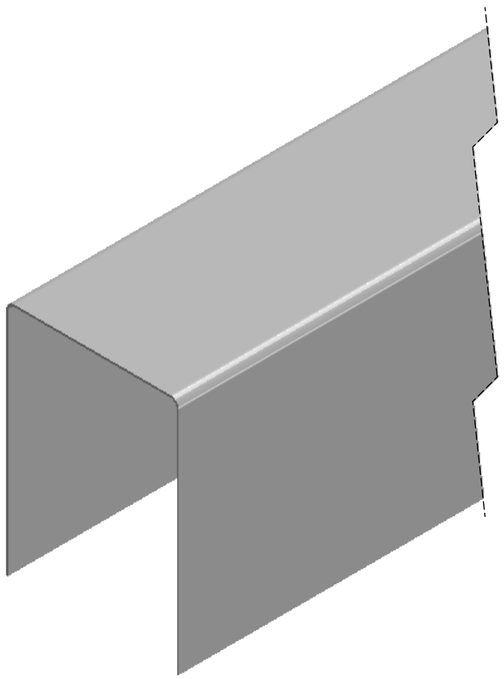


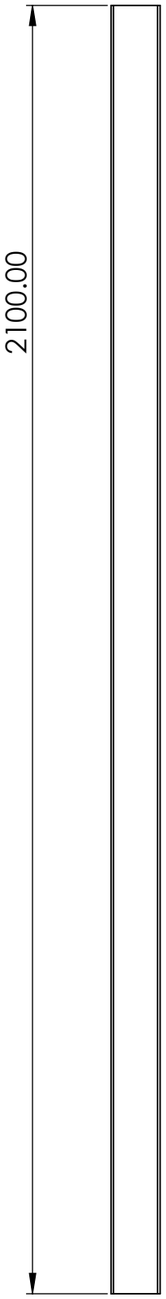

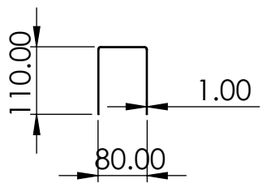



ITEM NO.	PART NUMBER	DESCRIPTION	QTY.
1	2D DRAWING SALAVI MAM BUSBAR FLASHER	STD (LOOSE PART)	1
		Sheet	1

TITLE - RETRACTABLE ROOF				NIHVA TECHNOLOGIES PVT.LTD.PUNE Website - www.nihva.com
DWG NO - NTPL276-001-00-000-001				
	NAME	SIGNATURE	DATE	PROJECT NO - NTPL276-PM
DRAWN	S.W		28-03-2025	PRODUCT - RETRACTABLE ROOF
CHK'D	P.M.		28-03-2025	SITE LOCATION - GUJARAT
APPV'D	V.T.		28-03-2025	
if any queries contact - supportautomation@nihva.com				REVISION - QTY - 1
ALL DIMENSION ARE IN mm		A3		SCALE - SHEET 33 OF 36

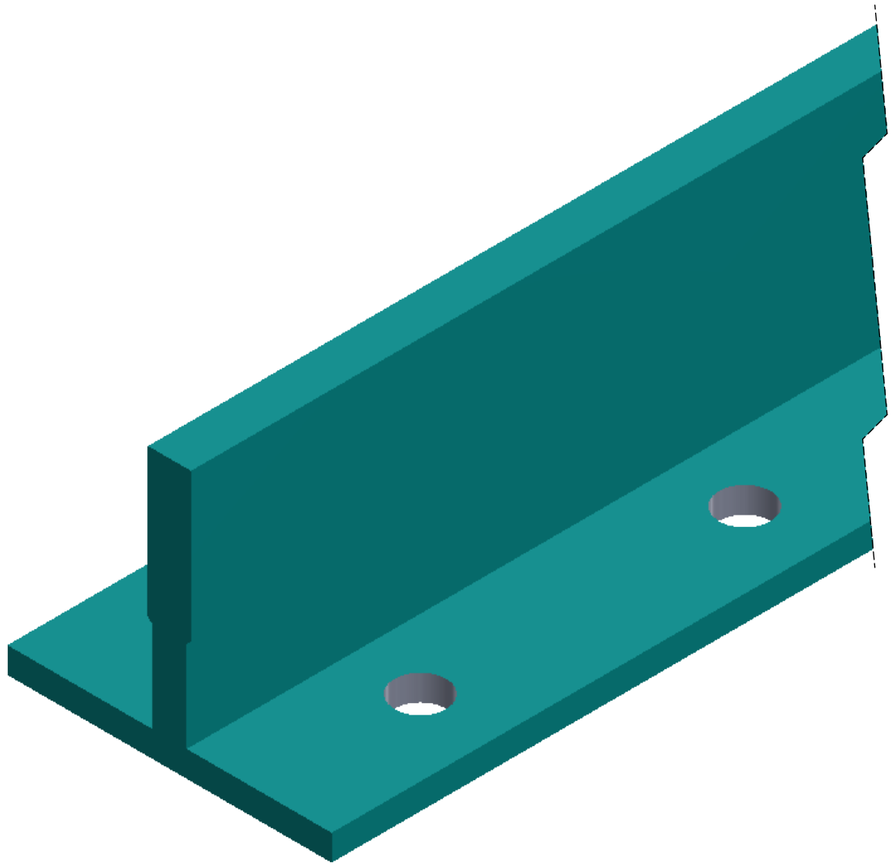


ITEM NO.	PART NUMBER	DESCRIPTION	QTY.
1	GUIDE RAILS-T75-1B	STD (10060 mm)	1

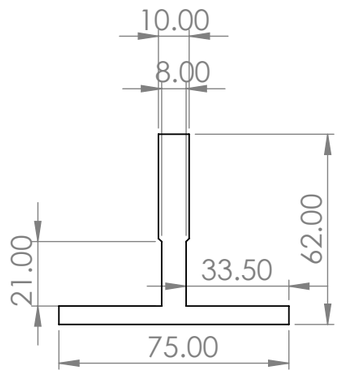

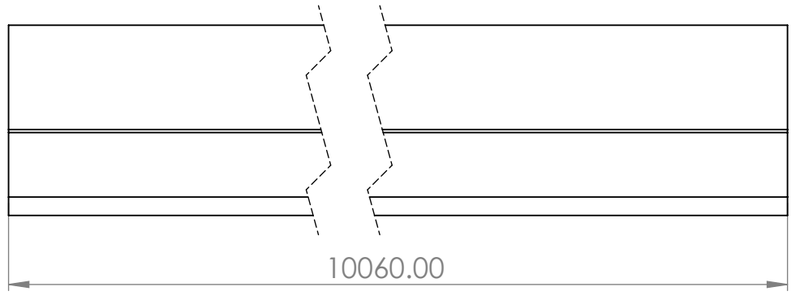


TITLE - RETRACTABLE ROOF				NIHVA TECHNOLOGIES PVT.LTD.PUNE
DWG NO - NTPL276-001-00-000-002				Website - www.nihva.com
	NAME	SIGNATURE	DATE	PROJECT NO - NTPL276-PM
DRAWN	S.W		28-03-2025	PRODUCT - RETRACTABLE ROOF
CHK'D	P.M.		28-03-2025	SITE LOCATION - GUJARAT
APPV'D	V.T.		28-03-2025	
if any queries contact - supportautomation@nihva.com				REVISION - / QTY - 1
ALL DIMENSION ARE IN mm			A3	SCALE - / SHEET 34 OF 36

ITEM NO.	PART NUMBER	DESCRIPTION	QTY.
1	2D DRAWING EPDM RUBBER_BIG PANEL		1

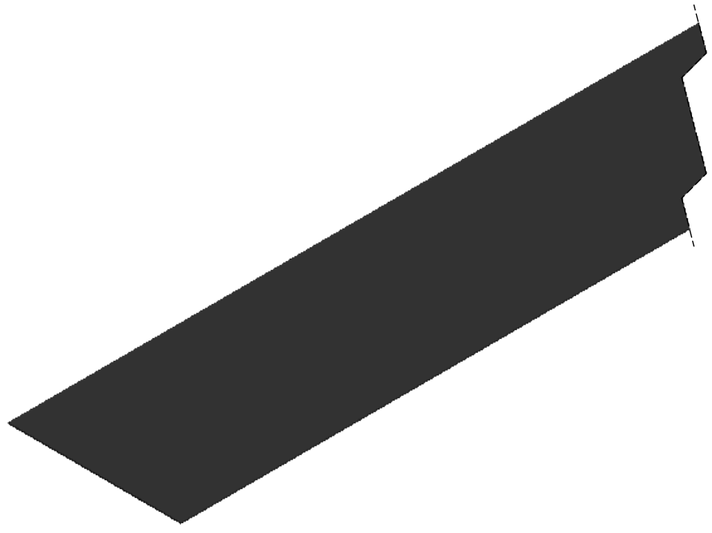

TITLE - RETRACTABLE ROOF				NIHVA TECHNOLOGIES PVT.LTD.PUNE
DWG NO - NTPL276-001-00-000-003				Website - www.nihva.com
	NAME	SIGNATURE	DATE	PROJECT NO - NTPL276-PM
DRAWN	S.W		28-03-2025	PRODUCT - RETRACTABLE ROOF
CHK'D	P.M.		28-03-2025	SITE LOCATION - GUJARAT
APPV'D	V.T.		28-03-2025	
if any queries contact - supportautomation@nihva.com				REVISION - QTY - 1
ALL DIMENSION ARE IN mm			A3	SCALE - SHEET 35 OF 36

ITEM NO.	PART NUMBER	DESCRIPTION	QTY.
1	2D DRAWING SALAVI MAM RACK	STD (M4 RACK, 30x8x1000 mm, ZINC COATED WITH SPACERS AND SCREWS.)	1

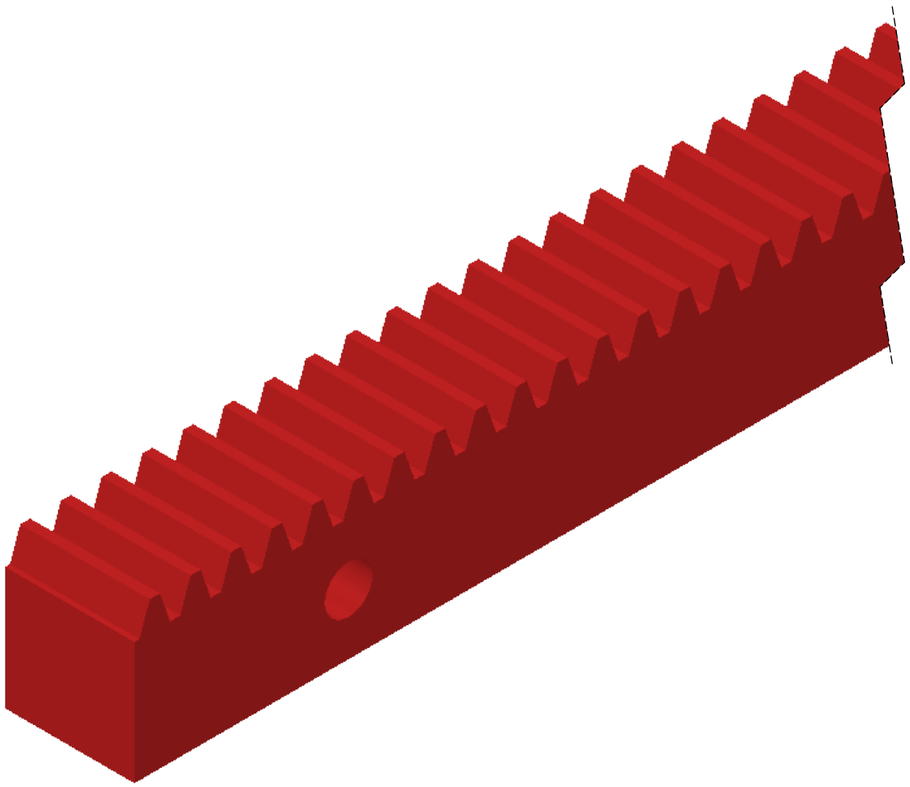

TITLE - RETRACTABLE ROOF

DWG NO - NTPL276-001-00-000-004

NIHVA TECHNOLOGIES PVT.LTD.PUNE

Website - www.nihva.com

	NAME	SIGNATURE	DATE
DRAWN	S.W		28-03-2025
CHK'D	P.M.		28-03-2025
APPV'D	V.T.		28-03-2025

PROJECT NO - NTPL276-PM

PRODUCT - RETRACTABLE ROOF

SITE LOCATION - GUJARAT

if any queries contact - supportautomation@nihva.com

REVISION -

QTY - 1

ALL DIMENSION ARE IN mm

A3

SCALE -