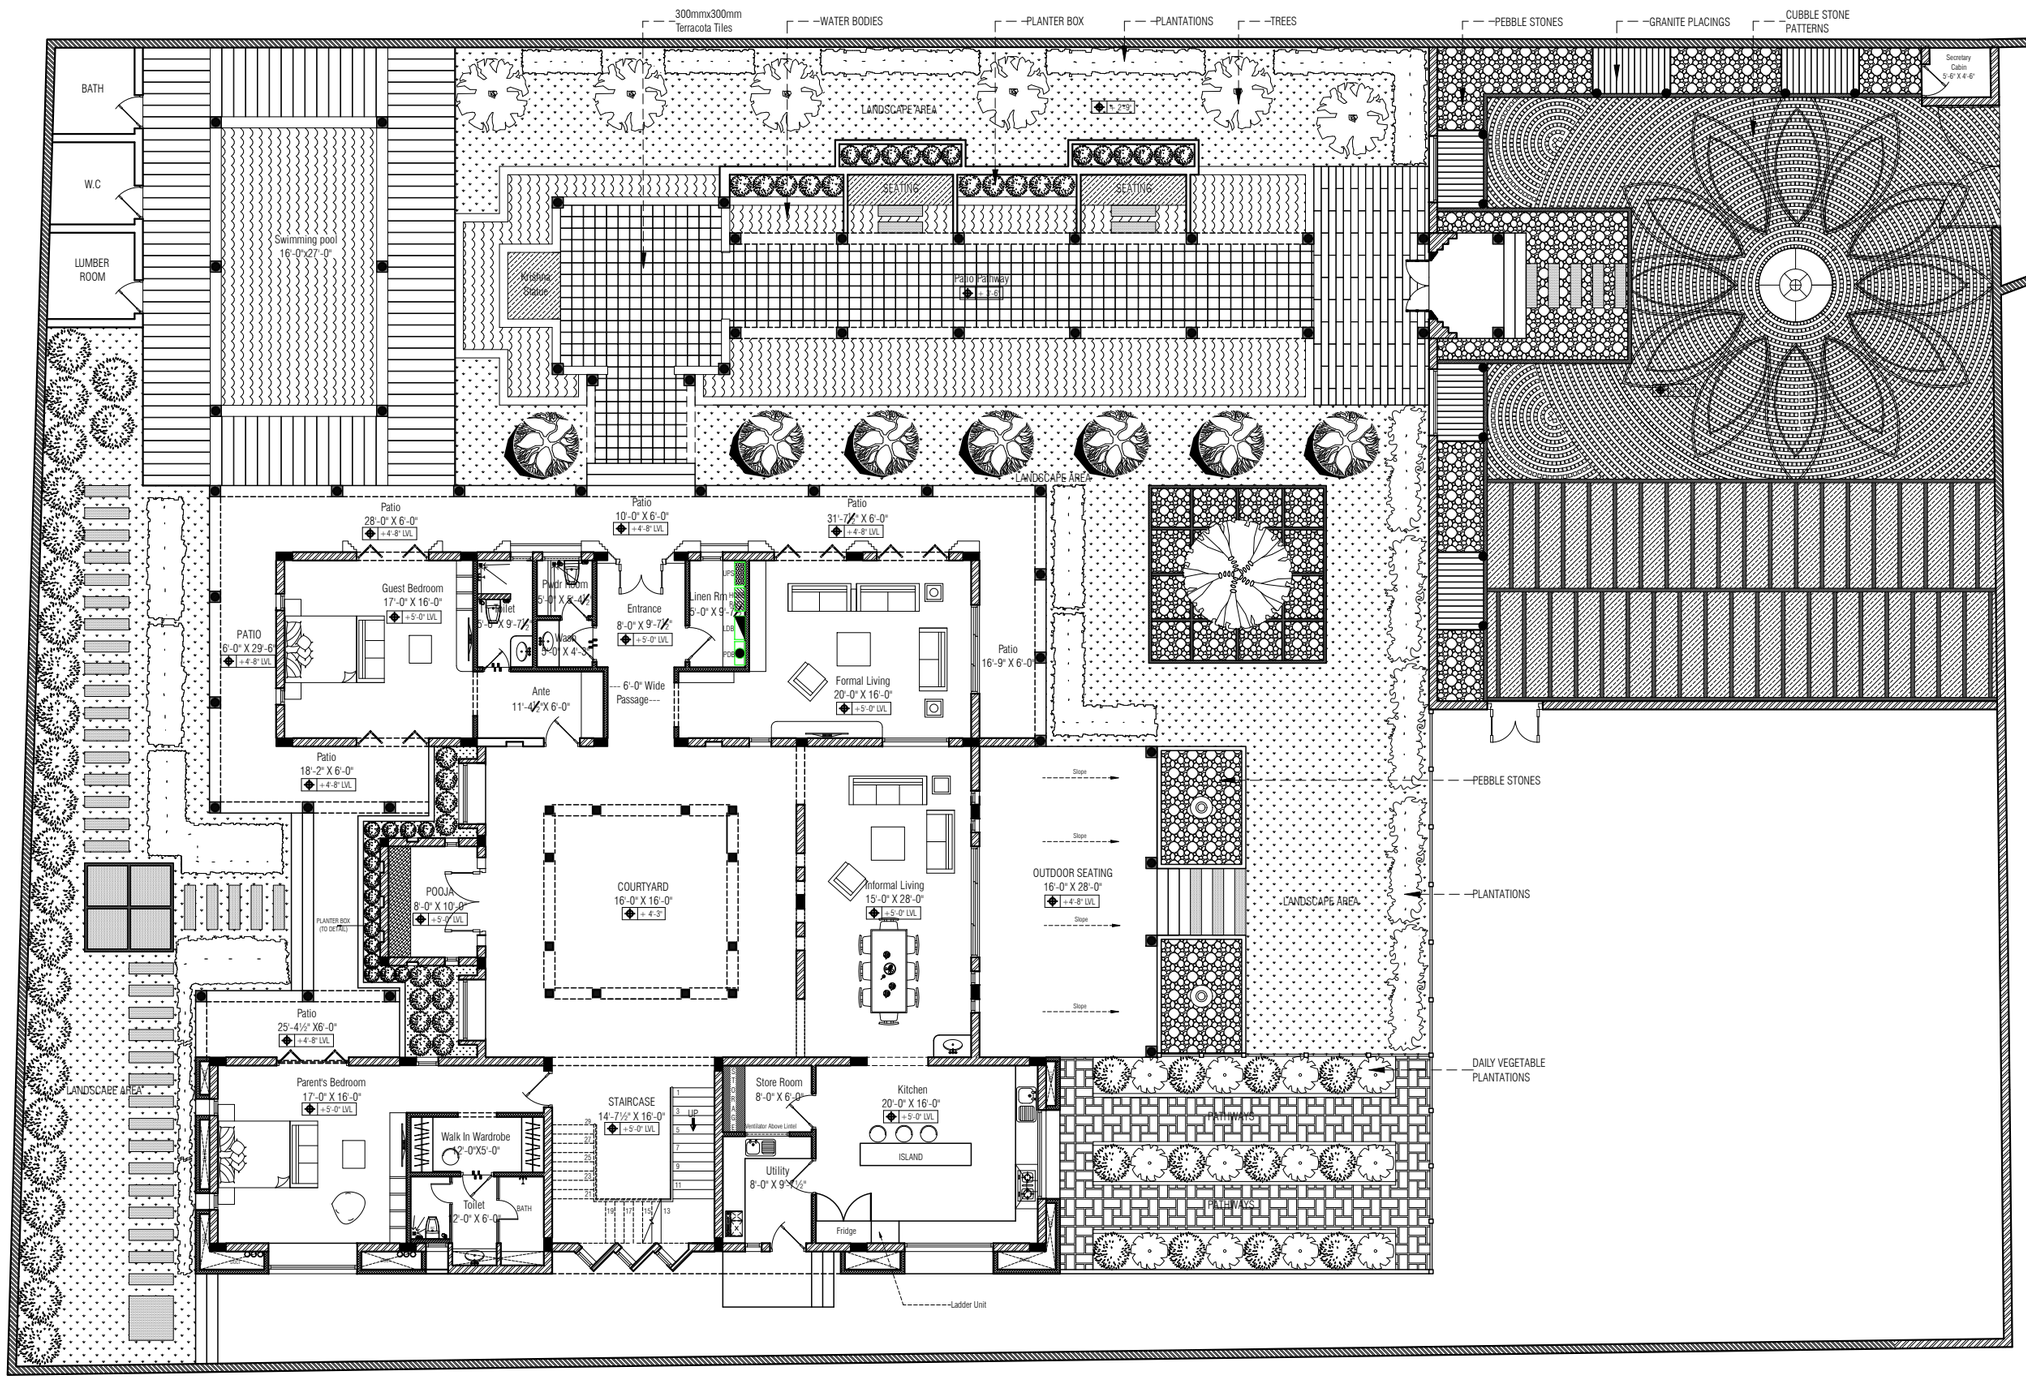


KRISHNA AISHWARYAM SITE LANDSCAPE PLAN

COPYRIGHT :
THIS DRAWING IS A COPYRIGHT. IT IS NOT TO BE REPRODUCED, COPIED, HANDED OVER TO A THIRD PARTY OR USED FOR ANY OTHER PURPOSE OTHER THAN FOR THE PROJECT INVOLVED WITHOUT THE KNOWLEDGE OF THE ARCHITECT.

NOTES:
ALL DIMENSIONS TO BE CHECKED AT SITE.
DO NOT SCALE THE DRAWING
IN THE EVENT OF ANY DISCREPANCIES OR DIFFERENCES BETWEEN ARCHITECTURAL DRAWINGS,STRUCTURAL DRAWINGS AND SITE CONDITIONS, IMMEDIATE REFERENCE IS TO BE MADE TO THE ARCHITECT PRIOR TO THE EXECUTION OF WORK AT THE SITE.

REV	REVISION DESCRIPTION	DATE

STRUCTURAL CONSULTANT:
Team 3 Associates
Architecture | Engineering | Interior | Landscape
JKR Towers,Door No: 5/6,
Moonlight Gardens,
Sitra-Kalapatti Rl,Kalapatti,
Coimbatore - 641048, India.
E-mail : drafting@t3associates.in
Phone : +91-0422-4206657

ARCHITECT:
Team 3 Associates
Architecture | Engineering | Interior | Landscape
JKR Towers,Door No: 5/6,
Moonlight Gardens,
Sitra-Kalapatti Rl,Kalapatti,
Coimbatore - 641048, India.
E-mail : drafting@t3associates.in
Phone : +91-0422-4206657

CLIENT:
KRISHNA AISHWARYAM COIMBATORE.


PROJECT:
PROPOSED RESIDENTIAL BUILDING AT COIMBATORE.

DRAWING TITLE:
SITE LANSCAPE PLAN

	INITIALS:	SIGNED BY:	DATE:
DRAWN BY:	S.K	S.KARTHIKEYAN	31-08-2022
CHECKED BY:	S.P	S.PRABHAKAR	31-08-2022
APPROVED BY:	S.P	S.PRABHAKAR	31-08-2022

SCALE: NTS | JOB NO: 23 | REV: 00

DRAWING NUMBER:

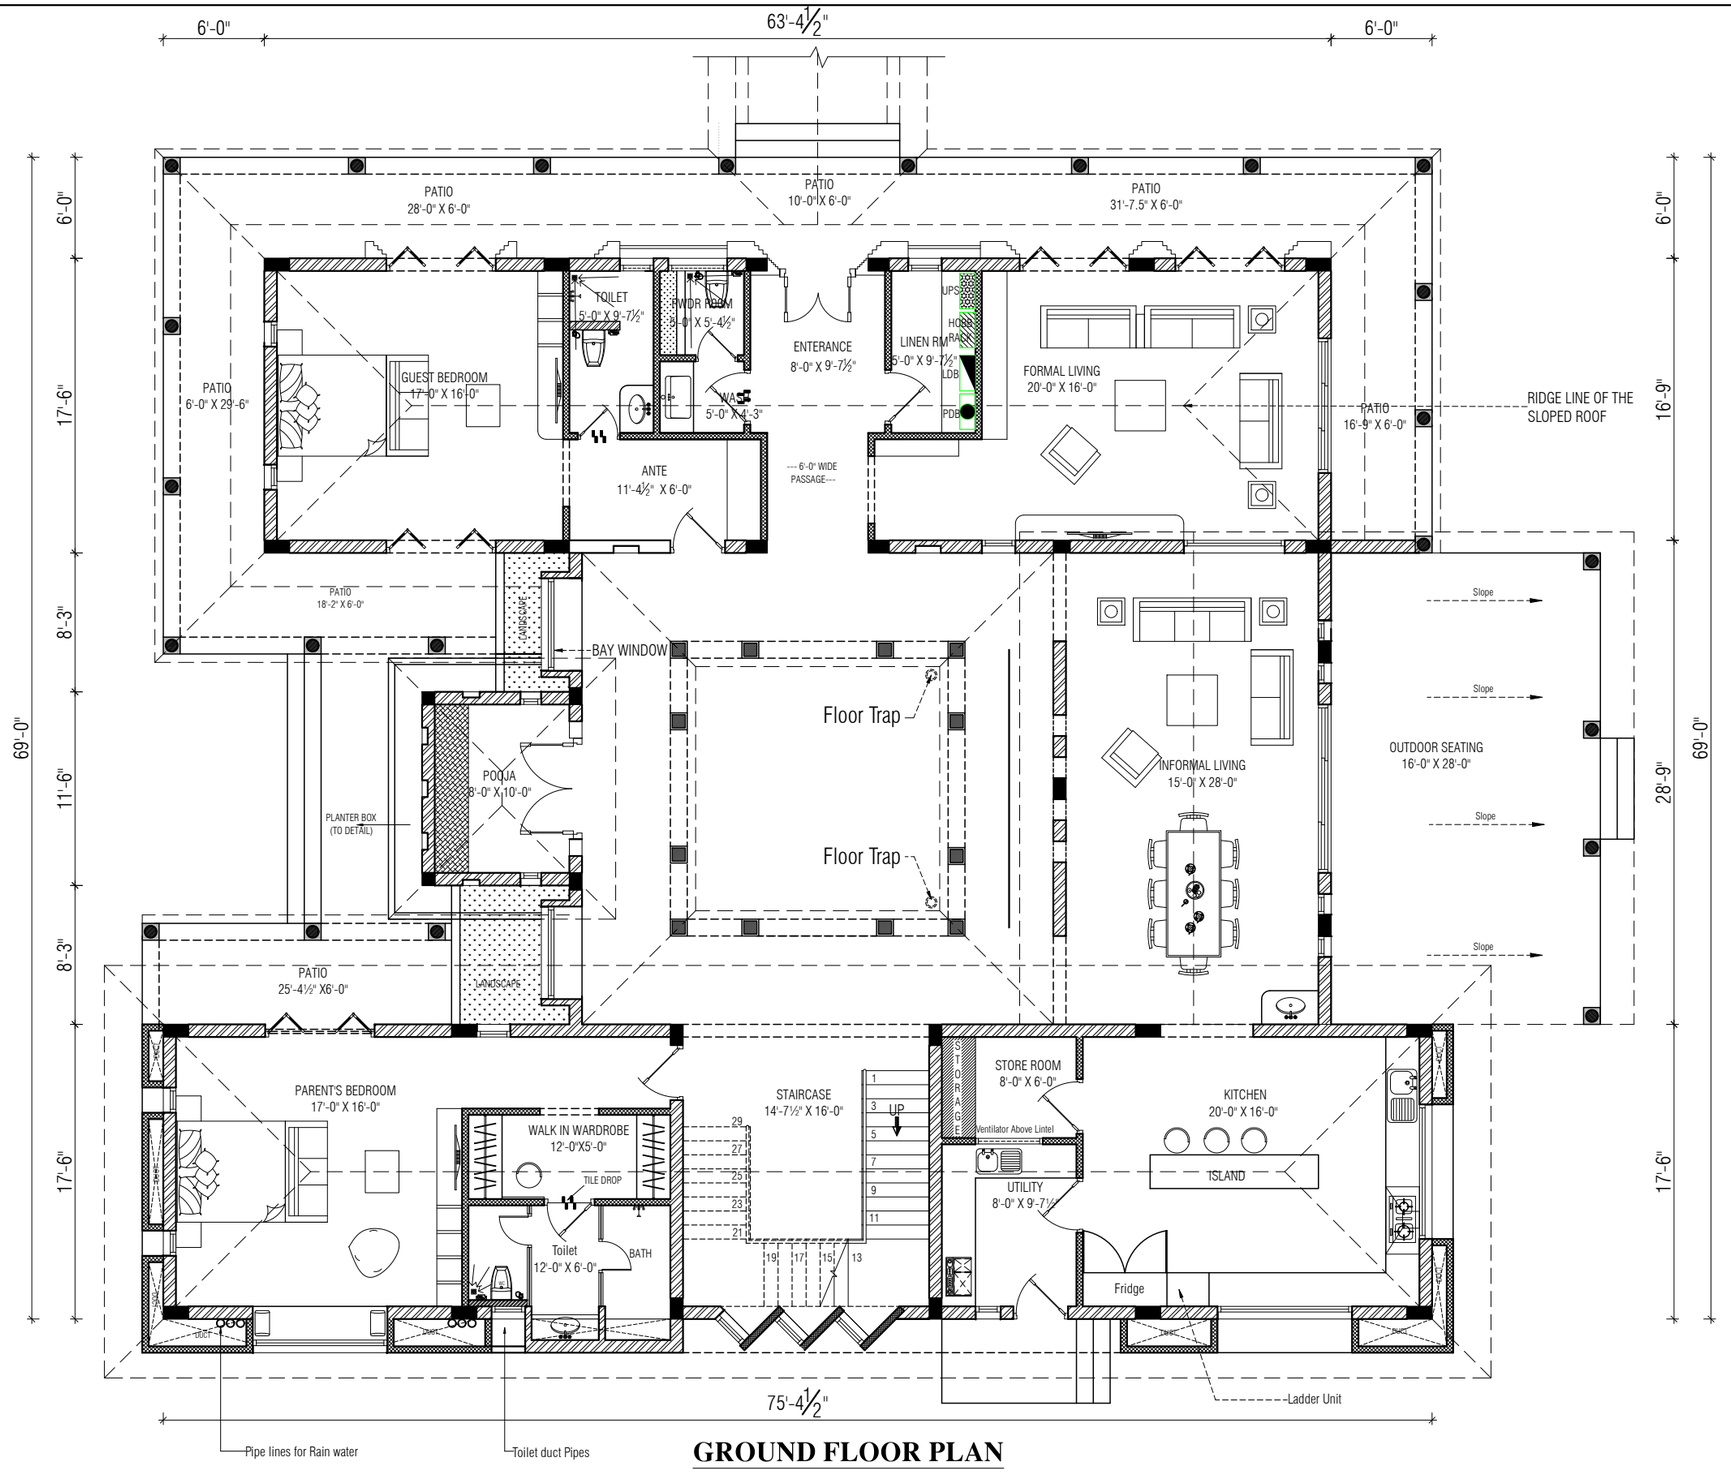

GROUND FLOOR PLAN

COPYRIGHT :
THIS DRAWING IS A COPYRIGHT. IT IS NOT TO BE REPRODUCED, COPIED, HANDED OVER TO A THIRD PARTY OR USED FOR ANY OTHER PURPOSE OTHER THAN FOR THE PROJECT INVOLVED WITHOUT THE KNOWLEDGE OF THE ARCHITECT.

NOTES:
ALL DIMENSIONS TO BE CHECKED AT SITE.
DO NOT SCALE THE DRAWING
IN THE EVENT OF ANY DISCREPANCIES OR DIFFERENCES BETWEEN ARCHITECTURAL DRAWINGS,STRUCTURAL DRAWINGS AND SITE CONDITIONS, IMMEDIATE REFERENCE IS TO BE MADE TO THE ARCHITECT PRIOR TO THE EXECUTION OF WORK AT THE SITE.

REV	REVISION DESCRIPTION	DATE

STRUCTURAL CONSULTANT:
Team3 Associates
Architecture | Engineering | Interior | Landscape
JKR Towers,Door No: 5/6,
Moonlight Gardens,
Sitra-Kalapatti Rl,Kalapatti,
Coimbatore - 641048, India.
E-mail : drafting@t3associates.in
Phone : +91-0422-4206657

ARCHITECT:
Team3 Associates
Architecture | Engineering | Interior | Landscape
JKR Towers,Door No: 5/6,
Moonlight Gardens,
Sitra-Kalapatti Rl,Kalapatti,
Coimbatore - 641048, India.
E-mail : drafting@t3associates.in
Phone : +91-0422-4206657

CLIENT:
KRISHNA AISHWARYAM COIMBATORE.


PROJECT:
PROPOSED RESIDENTIAL BUILDING AT COIMBATORE.

DRAWING TITLE:
GROUND FLOOR - SCHEME PLAN

	INITIALS:	SIGNED BY:	DATE:
DRAWN BY:	M.S	M.SURAMANIAN	31-08-2022
CHECKED BY:	S.P	S.PRABHAKAR	31-08-2022
APPROVED BY:	S.P	S.PRABHAKAR	31-08-2022

SCALE: NTS | JOB NO: 23 | REV: 00

DRAWING NUMBER:

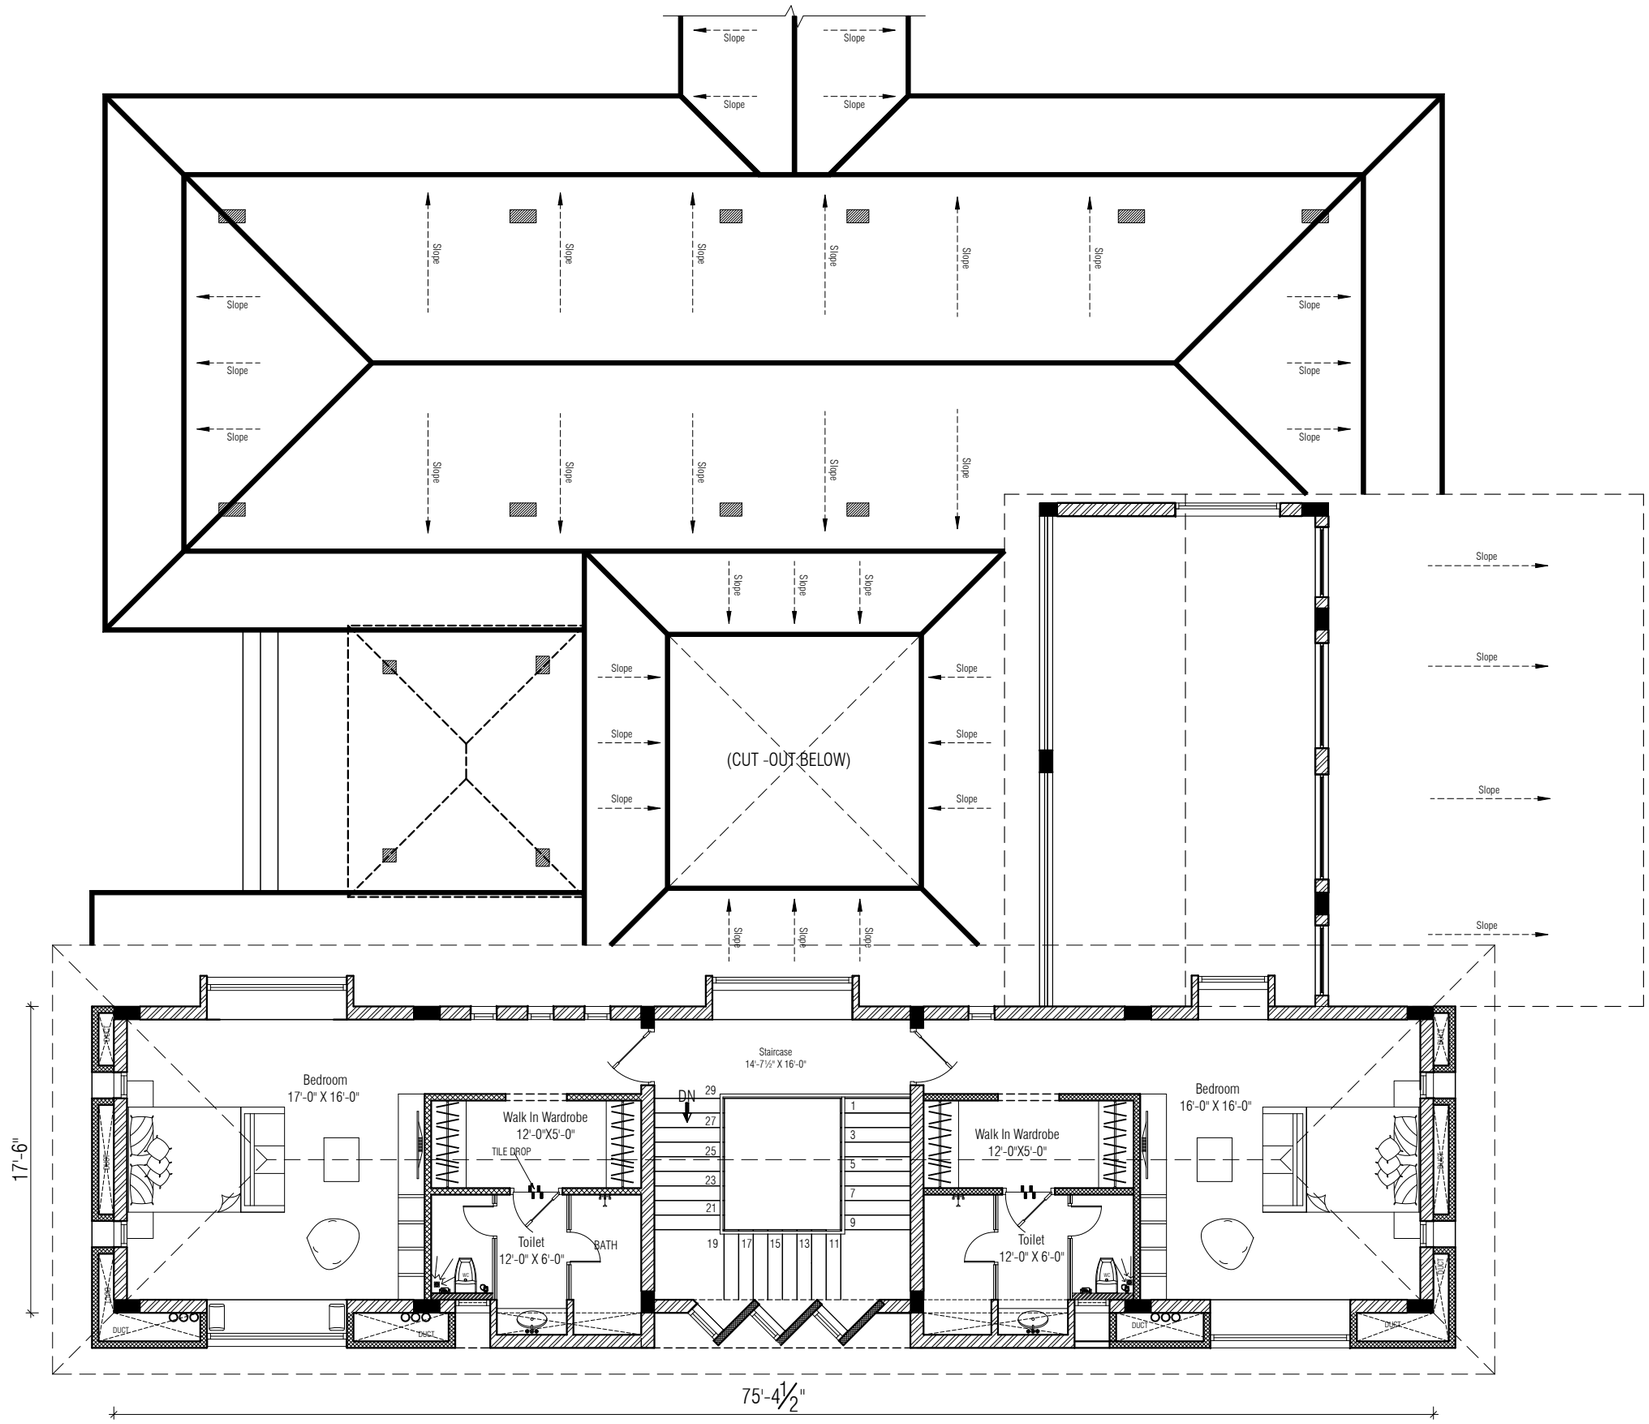

FIRST FLOOR PLAN

COPYRIGHT :
THIS DRAWING IS A COPYRIGHT. IT IS NOT TO BE REPRODUCED, COPIED, HANDED OVER TO A THIRD PARTY OR USED FOR ANY OTHER PURPOSE OTHER THAN FOR THE PROJECT INVOLVED WITHOUT THE KNOWLEDGE OF THE ARCHITECT.

NOTES:
ALL DIMENSIONS TO BE CHECKED AT SITE.
DO NOT SCALE THE DRAWING
IN THE EVENT OF ANY DISCREPANCIES OR DIFFERENCES BETWEEN ARCHITECTURAL DRAWINGS,STRUCTURAL DRAWINGS AND SITE CONDITIONS, IMMEDIATE REFERENCE IS TO BE MADE TO THE ARCHITECT PRIOR TO THE EXECUTION OF WORK AT THE SITE.

REV	REVISION DESCRIPTION	DATE

STRUCTURAL CONSULTANT:
Team 3 Associates
Architecture | Engineering | Interior | Landscape
JKR Towers,Door No: 5/6,
Moonlight Gardens,
Sitra-Kalapatti Rl,Kalapatti,
Coimbatore - 641048, India.
E-mail : drafting@t3associates.in
Phone : +91-0422-4206657

ARCHITECT:
Team 3 Associates
Architecture | Engineering | Interior | Landscape
JKR Towers,Door No: 5/6,
Moonlight Gardens,
Sitra-Kalapatti Rl,Kalapatti,
Coimbatore - 641048, India.
E-mail : drafting@t3associates.in
Phone : +91-0422-4206657

CLIENT:
KRISHNA AISHWARYAM COIMBATORE.


PROJECT:
PROPOSED RESIDENTIAL BUILDING AT COIMBATORE.

DRAWING TITLE:
FIRST FLOOR - SCHEME PLAN

	INITIALS:	SIGNED BY:	DATE:
DRAWN BY:	S.K	M.SUBRAMANIAN	31-08-2022
CHECKED BY:	S.P	S.PRABHAKAR	31-08-2022
APPROVED BY:	S.P	S.PRABHAKAR	31-08-2022

SCALE: NTS | JOB NO: 23 | REV: 00

DRAWING NUMBER:

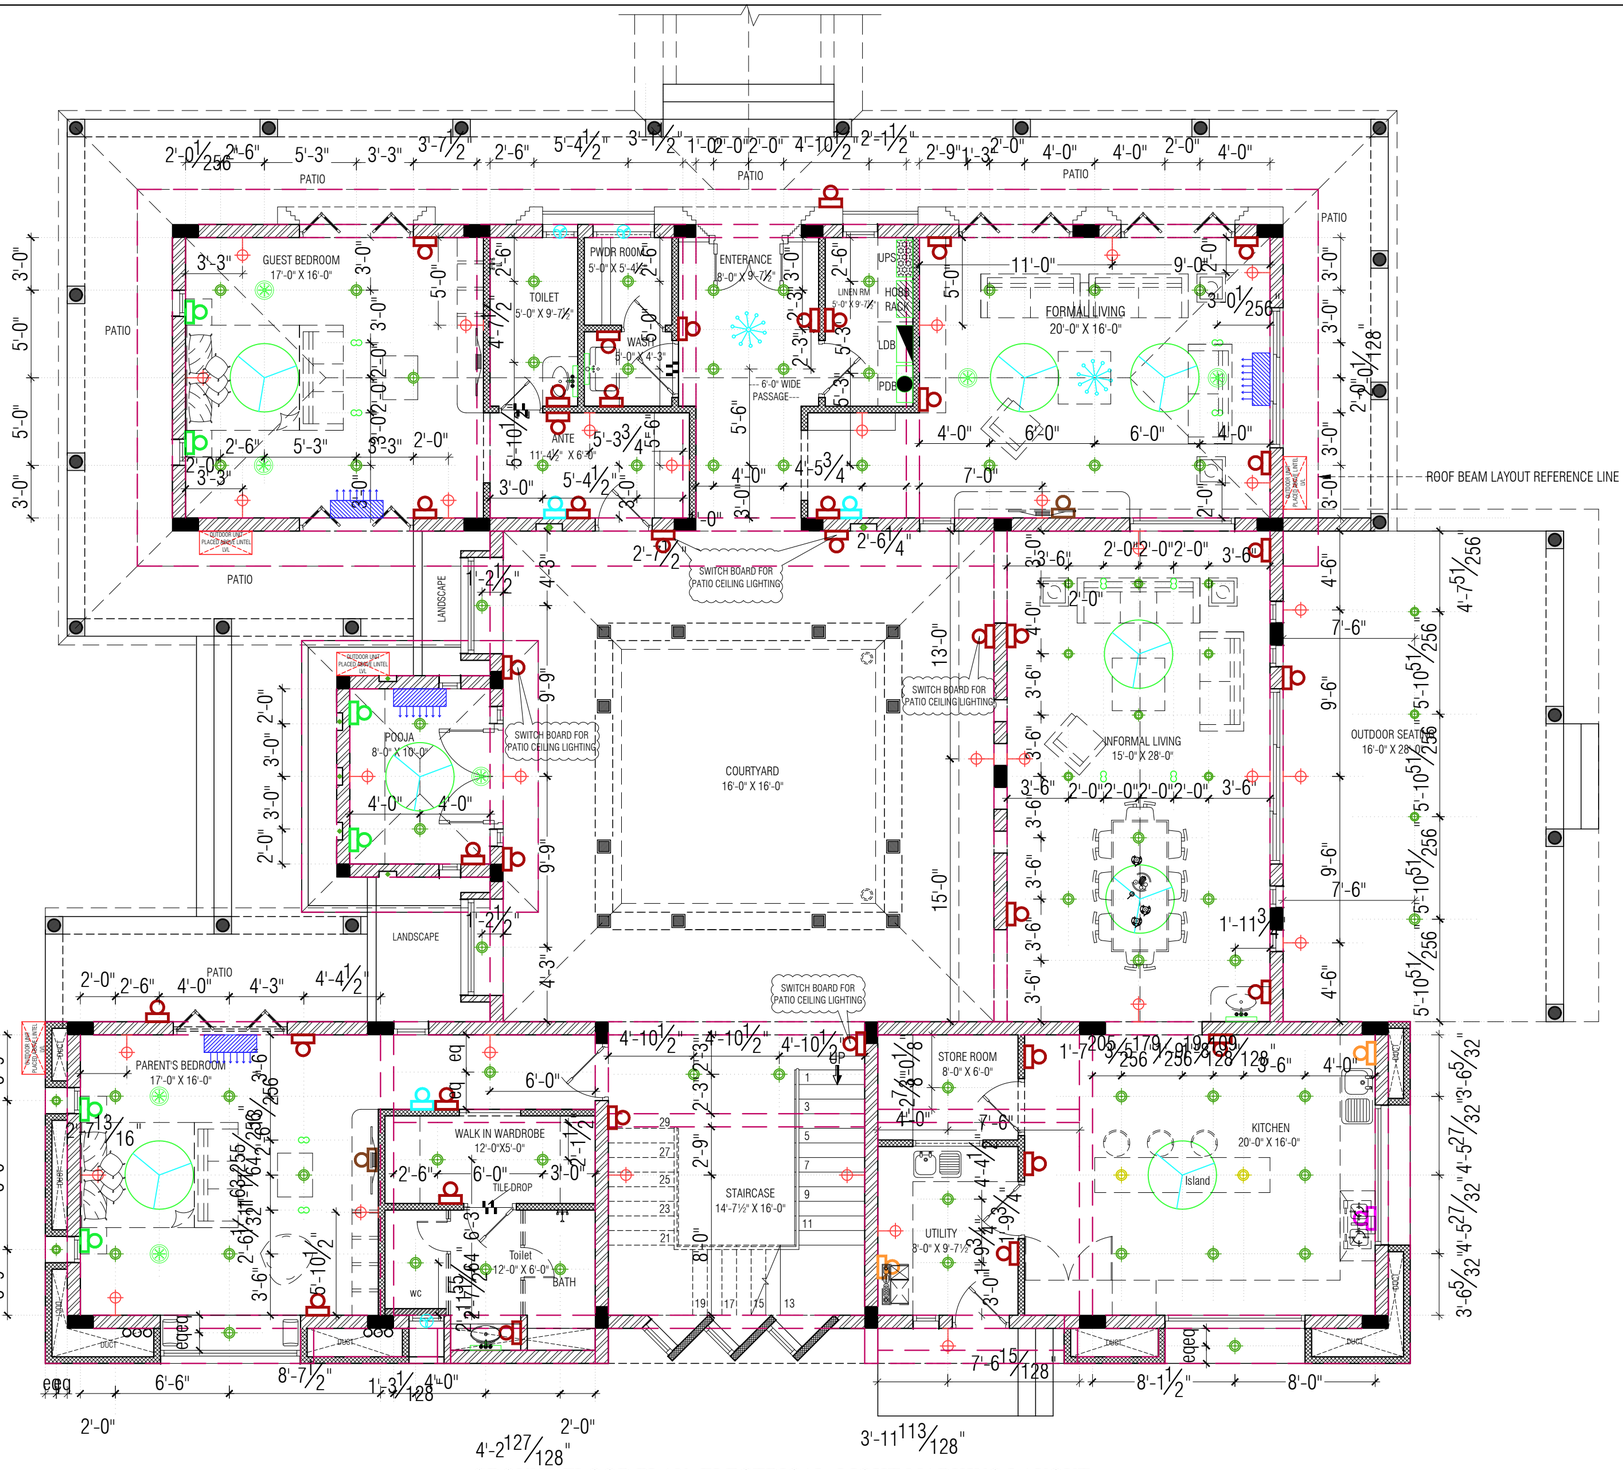

GROUND FLOOR PLAN- ELECTRICAL LIGHT MARKING LAYOUT

ELECTRICAL POINTS LEGENDS

SYMBOL	LEGEND	HT FROM FFL
	CEILING POINT	ROOF
	WALL BRACKET	8'-0"
	SPLIT AC	To Be Specified
	AC OUTDOOR UNIT	To Be Specified
	UPS & BATTERIES	---
	TELEPHONE+CCTV+ INTERNET HOBB BOX	---
	LDB	---
	PDB	---
	HOOK	ROOF
	MIRROR LIGHT	7'-0"
	EXHAUST FAN	Ventilator
	CHANDELLER	ROOF
	CEILING FAN	ROOF
	SPEAKERS	ROOF
SB	LIGHTING SWITCH BOARD	4'-6"
SB	LIGHTING SWITCH BOARD	1'-6"
SB	LIGHTING SWITCH BOARD	2'-6"
SB	LIGHTING SWITCH BOARD	3'-3"
SB	POWER SWITCH BOARD	4'-6"

COPYRIGHT :
THIS DRAWING IS A COPYRIGHT. IT IS NOT TO BE REPRODUCED, COPIED, HANDED OVER TO A THIRD PARTY OR USED FOR ANY OTHER PURPOSE OTHER THAN FOR THE PROJECT INVOLVED WITHOUT THE KNOWLEDGE OF THE ARCHITECT.

NOTES:
ALL DIMENSIONS TO BE CHECKED AT SITE.
DO NOT SCALE THE DRAWING
IN THE EVENT OF ANY DISCREPANCIES OR DIFFERENCES BETWEEN ARCHITECTURAL DRAWINGS,STRUCTURAL DRAWINGS AND SITE CONDITIONS, IMMEDIATE REFERENCE IS TO BE MADE TO THE ARCHITECT PRIOR TO THE EXECUTION OF WORK AT THE SITE.

REV	REVISION DESCRIPTION	DATE

STRUCTURAL CONSULTANT:
Team3 Associates
Architecture | Engineering | Interior | Landscape
JKR Towers,Door No: 5/6, Moonlight Gardens, Sitra-Kalapatti Rl,Kalapatti, Coimbatore - 641048, India.
E-mail : drafting@t3associates.in
Phone : +91-0422-4206657

ARCHITECT:
Team3 Associates
Architecture | Engineering | Interior | Landscape
JKR Towers,Door No: 5/6, Moonlight Gardens, Sitra-Kalapatti Rl,Kalapatti, Coimbatore - 641048, India.
E-mail : drafting@t3associates.in
Phone : +91-0422-4206657

CLIENT:
KRISHNA AISHWARYAM COIMBATORE.


PROJECT:
PROPOSED RESIDENTIAL BUILDING AT COIMBATORE.

DRAWING TITLE:
GROUND FLOOR - ELECTRICAL LIGHT MARKING LAYOUT

	INITIALS:	SIGNED BY:	DATE:
DRAWN BY:	S.K	S.KARTHIKEYAN	31-08-2022
CHECKED BY:	S.P	S.PRABHAKAR	31-08-2022
APPROVED BY:	S.P	S.PRABHAKAR	31-08-2022

SCALE: NTS | JOB NO: 23 | REV: 00

DRAWING NUMBER:

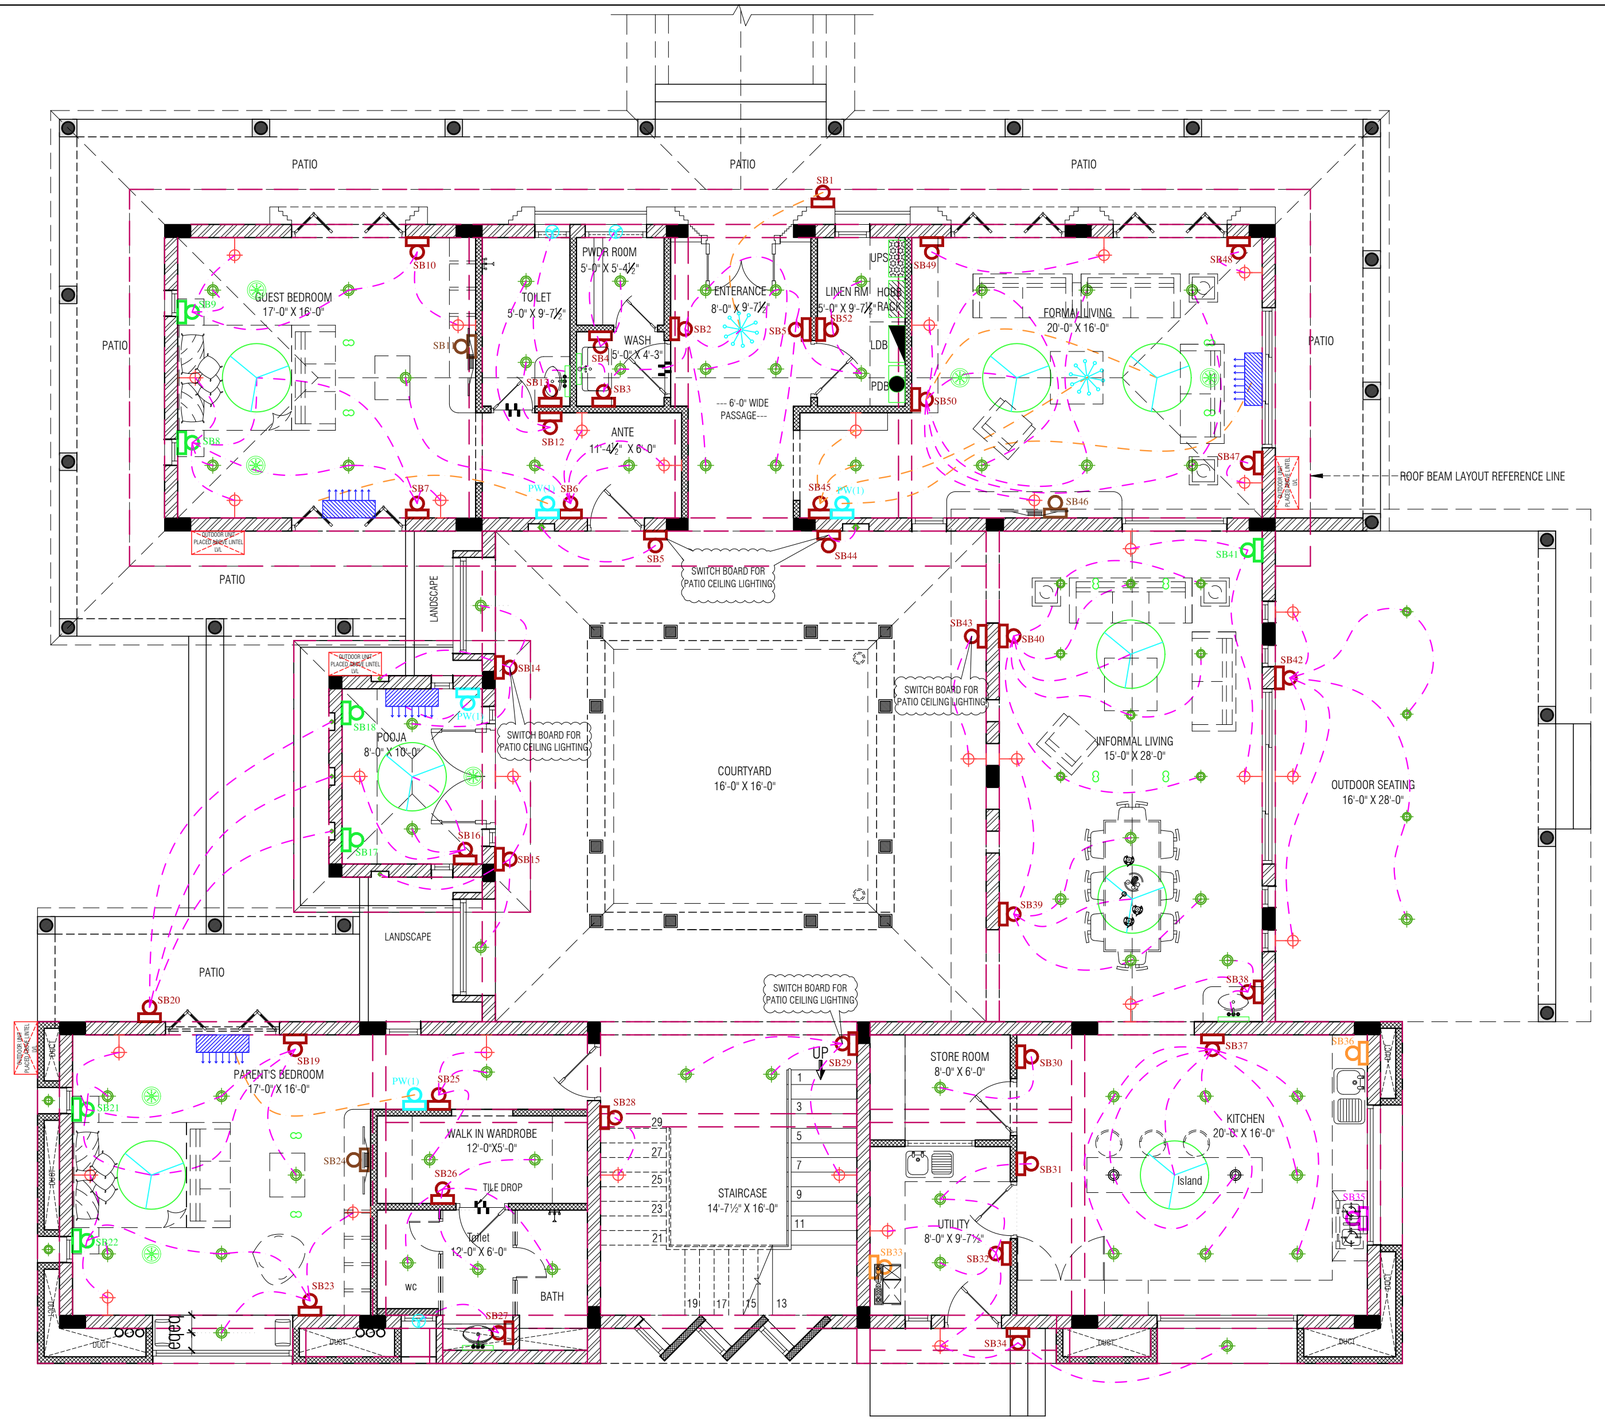

GROUND FLOOR PLAN- ELECTRICAL WIRING LAYOUT

SWITCH POINT CONNECTIONS

S.point	DESCRIPTION	SWITCH BOARD BOTTOM HEIGHT FROM FFL	SYMBOLS (SOCKETS AND SWITCHES)
SB1	1 X Two Way Switch For Chandeller	4'-6"	
SB2	2 X Two Way Switch For Light 1 X Single Way Switch For Light 1 X Two Way Switch For Chandeller	4'-6"	
SB3	1 X Two Way Switch For Light 1 X Single Way Switch For Mirror light 1 X 5 AMP Shuttered Socket and Switch	4'-6"	
SB4	1 X Single Way Switch For Light 1 X Single Way Switch For Exhaust Fan	4'-6"	
SB5	1 X Single Way Switch For Light Switch Board For Lights in Patio	4'-6"	--------
SB6	3 X Single Way Switch For Light 2 X Single Way Switch For Wall Bracket	4'-6"	
SB7	1 X Two Way Switch For Light 1 X Two Way Fan regulator and Switch Control 1 X Single Way Switch For Wall Bracket	4'-6"	
SB8	1 X Two Way Switch For Light 1 X Single Way Switch For Light 1 X Two Way Fan regulator and Switch Control 1 X 5 AMP Shuttered Socket and Switch 2 X Single Way Switch For Wall Bracket	2'-0"	
SB9	1 X Two Way Switch For Light 1 X Single Way Switch For Light 1 X Single Way Switch For Wall Bracket 1 X 5 AMP Shuttered Socket and Switch	2'-0"	
	A Telephone Point	2'-0"	
SB10	1 X Two Way Switch For Light 1 X Single Way Switch For Wall Bracket	4'-6"	
SB11	3 X 5 AMP Shuttered Socket and Switch	4'-6"	
	A Telephone Point , Internet point Socket For CCTV DVR	1'-6"	
	B Control Switch	2'-6"	
	C 1 X 5 AMP Shuttered Socket	4'-6"	
SB12	2 X Single Way Switch For Light	4'-6"	
SB13	1 X Single Way Switch For Mirror light 1 X Single Way Switch For Exhaust Fan 1 X 5 AMP Shuttered Socket and Switch	4'-6"	
SB14	3 X Single Way Switch For light Switch Board For Lights in Patio	4'-6"	--------
SB15	2 X Single Way Switch For light 1 X Single Way Switch For Wall Bracket Switch Board For Lights in Patio	4'-6"	--------
SB16	1 X Single Way Fan regulator and Switch Control 1 X Single Way Switch For light 1 X Single Way Switch For Wall Bracket	4'-6"	
SB17	2 X 5 AMP Shuttered Socket and Switch	2'-0"	
SB18	2 X 5 AMP Shuttered Socket and Switch	2'-0"	
SB19	1 X Two Way Fan regulator and Switch Control 1X Single Way Switch For light 1X Two Way Switch For light	4'-6"	
SB20	Switch Board For Lights in Patio 3 X Single Way Switch For light	4'-6"	--------
SB21	1 X Two Way Switch For Light 1 X Two Way Fan regulator and Switch Control 1 X 5 AMP Shuttered Socket and Switch 1 X Single Way Switch For Wall Bracket 1 X Single Way Way Switch For Light	2'-0"	
SB22	1 X Two Way Switch For Light 1 X 5 AMP Shuttered Socket and Switch 2 X Single Way Switch For Wall Bracket 1 X Single Way Way Switch For Light	2'-0"	
	A Telephone Point	2'-0"	
SB23	1X Single Way Switch For light 1X Two Way Switch For light 1 X Single Way Switch For Wall Bracket 1 X 5 AMP Shuttered Socket and Switch	4'-6"	
SB24	3 X 5 AMP Shuttered Socket and Switch	4'-6"	
	A Telephone Point , Internet point Socket For CCTV DVR	1'-6"	
	B Control Switch	2'-6"	
	C 1 X 5 AMP Shuttered Socket	4'-6"	
SB25	2 X Single Way Switch For Light 1 X Single Way Switch For Wall Bracket	4'-6"	
SB26	4 X Single Way Switch For Light	4'-6"	
SB27	1 X Single Way Switch For Mirror Light 1 X Single Way Switch For Exhaust Fan 1 X 5 AMP Shuttered Socket and Switch	4'-6"	

SWITCH POINT CONNECTIONS

S.point	DESCRIPTION	SWITCH BOARD BOTTOM HEIGHT FROM FFL	SYMBOLS (SOCKETS AND SWITCHES)
SB28	1 X Single Way Switch For Wall Bracket	4'-6"	
SB29	1 X Single Way Switch For Wall Bracket 2 X Single Way Switch For Light Switch Board for lights in patio	4'-6"	--------
SB30	1 X Single Way Switch For Light	4'-6"	
SB31	1 X Two Way Switch For Light	4'-6"	
SB32	1 X Single Way Switch For Light 1 X Two Way Switch For Light 1 X Single Way Switch For Wall Bracket 1 X Two Way Switch For Wall Bracket	4'-6"	
SB33	1 X15 AMP Shuttered Socket and Switch	3'-3"	
SB34	1 X Two Way Switch For Wall Bracket 1 X Single Way Switch For Light	4'-6"	
SB35	1 X15 AMP Shuttered Socket and Switch For Electric Hobb	2'-6"	
SB36	1 X 5 AMP Shuttered Socket and Switch For Water Purifier	3'-3"	
SB37	4 X Two Way Switch For Light 1 X Single Way Switch For Light 1 X Single Way Fan regulator and Switch Control	4'-6"	
SB38	1 X Single Way Switch For Mirror Light 1 X Single Way Switch For Wall Bracket 1 X Single Way Switch For Light 1 X 5 AMP Shuttered Socket and Switch	4'-6"	
SB39	2 X Two Way Switch For Light 1 X Single Way Fan regulator and Switch Control 1 X Single Way Switch For Light 1 X Single Way Switch For Wall Bracket	4'-6"	
SB40	4 X Two Way Switch For Light 1 X Single Way Fan regulator and Switch Control 1 X 5 AMP Shuttered Socket and Switch	4'-6"	
SB41	2 X Single Way Switch For Wall Bracket 1 X 5 AMP Shuttered Socket and Switch	1'-6"	
SB42	3 X Single Way Switch For Wall Bracket 2 X Two Way Switch For Light 1 X 5 AMP Shuttered Socket and Switch	4'-6"	
SB43	Switch Board For Lights in Patio 1 X Single Way Switch For Wall Bracket	4'-6"	----
SB44	1 X Single Way Switch For Light Switch Board For Lights in Patio	4'-6"	----
SB45	1 X Single Way Switch For Light 1 X Single Way Switch For Wall Bracket 1 X Single Way Switch For Chandeller	4'-6"	
SB46	3 X 5 AMP Shuttered Socket and Switch	4'-6"	
	A Telephone Point , Internet point Socket For CCTV DVR	1'-6"	
	B Control Switch	2'-6"	
	C 1 X 5 AMP Shuttered Socket	4'-6"	
SB47	1 X Single Way Switch For Wall Bracket 1 X 5 AMP Shuttered Socket and Switch	4'-6"	
SB48	1 X Single Way Switch For Wall Bracket 1 X 5 AMP Shuttered Socket and Switch	4'-6"	
SB49	1 X Single Way Switch For Wall Bracket 1 X 5 AMP Shuttered Socket and Switch	4'-6"	
SB50	3 X Two Way Switch For Light 2 X Single Way Switch For Wall Bracket 2 X Single Way Fan regulator and Switch Control 1 X 5 AMP Shuttered Socket and Switch	4'-6"	
SB51	1 X Two Way Switch For Light	4'-6"	
SB52	2 X Single Way Switch For Light 1 X 5 AMP Shuttered Socket and Switch	4'-6"	
PW(1)	1 X Single Way Switch For Split AC	4'-6"	

ELECTRICAL POINTS LEGENDS

SYMBOL	LEGEND	HT FROM FFL
	CEILING POINT	ROOF
	WALL BRACKET	8'-0"
	SPLIT AC	To Be Specified
	AC OUTDOOR UNIT	To Be Specified
	UPS & BATTERIES	---
	TELEPHONE+CCTV+ INTERNET HOBB BOX	---
	LDB	---
	PDB	---
	HOOK	ROOF

SYMBOL	LEGEND	HT FROM FFL
	MIRROR LIGHT	7'-0"
	EXHAUST FAN	Ventilator
	CHANDELLER	ROOF
	CEILING FAN	ROOF
	SPEAKERS	ROOF
	LIGHTING SWITCH BOARD	4'-6"
	LIGHTING SWITCH BOARD	2'-0"
	LIGHTING SWITCH BOARD	3'-3"
	LIGHTING SWITCH BOARD	2'-6"
	POWER SWITCH BOARD	4'-6"

FOR REFERENCE

ELECTRICAL WIRING CONNECTION LINES

COPYRIGHT :
THIS DRAWING IS A COPYRIGHT. IT IS NOT TO BE REPRODUCED, COPIED, HANDED OVER TO A THIRD PARTY OR USED FOR ANY OTHER PURPOSE OTHER THAN FOR THE PROJECT INVOLVED WITHOUT THE KNOWLEDGE OF THE ARCHITECT.

NOTES:
ALL DIMENSIONS TO BE CHECKED AT SITE.
DO NOT SCALE THE DRAWING
IN THE EVENT OF ANY DISCREPANCIES OR DIFFERENCES BETWEEN ARCHITECTURAL DRAWINGS,STRUCTURAL DRAWINGS AND SITE CONDITIONS, IMMEDIATE REFERENCE IS TO BE MADE TO THE ARCHITECT PRIOR TO THE EXECUTION OF WORK AT THE SITE.

STRUCTURAL CONSULTANT:
Team3 Associates
Architecture | Engineering | Interior | Landscape
JKR Towers,Door No: 5/6,
Moonlight Gardens,
Sitra-Kalapatti Rl,Kalapatti,
Coimbatore - 641048, India.
E-mail : drafting@t3associates.in
Phone : +91-0422-4206657

ARCHITECT:
Team3 Associates
Architecture | Engineering | Interior | Landscape
JKR Towers,Door No: 5/6,
Moonlight Gardens,
Sitra-Kalapatti Rl,Kalapatti,
Coimbatore - 641048, India.
E-mail : drafting@t3associates.in
Phone : +91-0422-4206657

CLIENT:
KRISHNA AISHWARYAM COIMBATORE.

PROJECT:
PROPOSED RESIDENTIAL BUILDING AT COIMBATORE.

DRAWING TITLE:
GROUND FLOOR - ELECTRICAL WIRING LAYOUT

	INITIALS:	SIGNED BY:	DATE:
DRAWN BY:	S.K	S.KARTHIKEYAN	31-08-2022
CHECKED BY:	S.P	S.PRABHAKAR	31-08-2022
APPROVED BY:	S.P	S.PRABHAKAR	31-08-2022

SCALE: NTS | JOB NO: 23 | REV: 00

DRAWING NUMBER: