
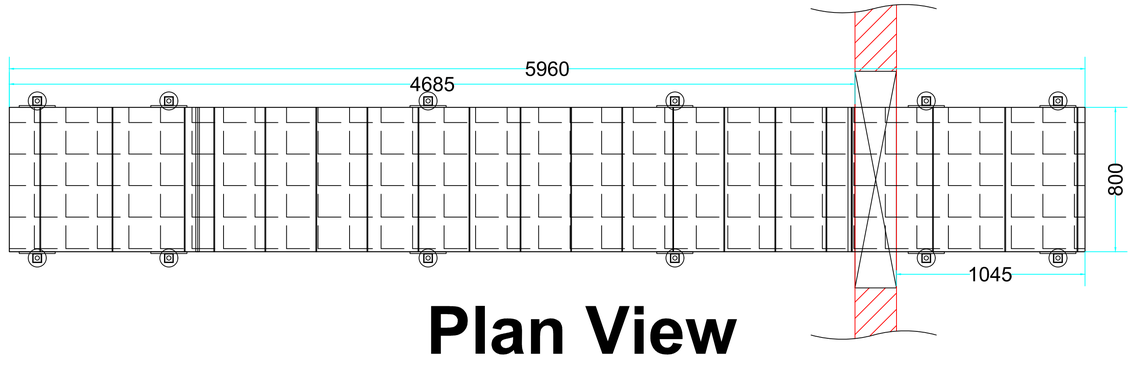


Plan View

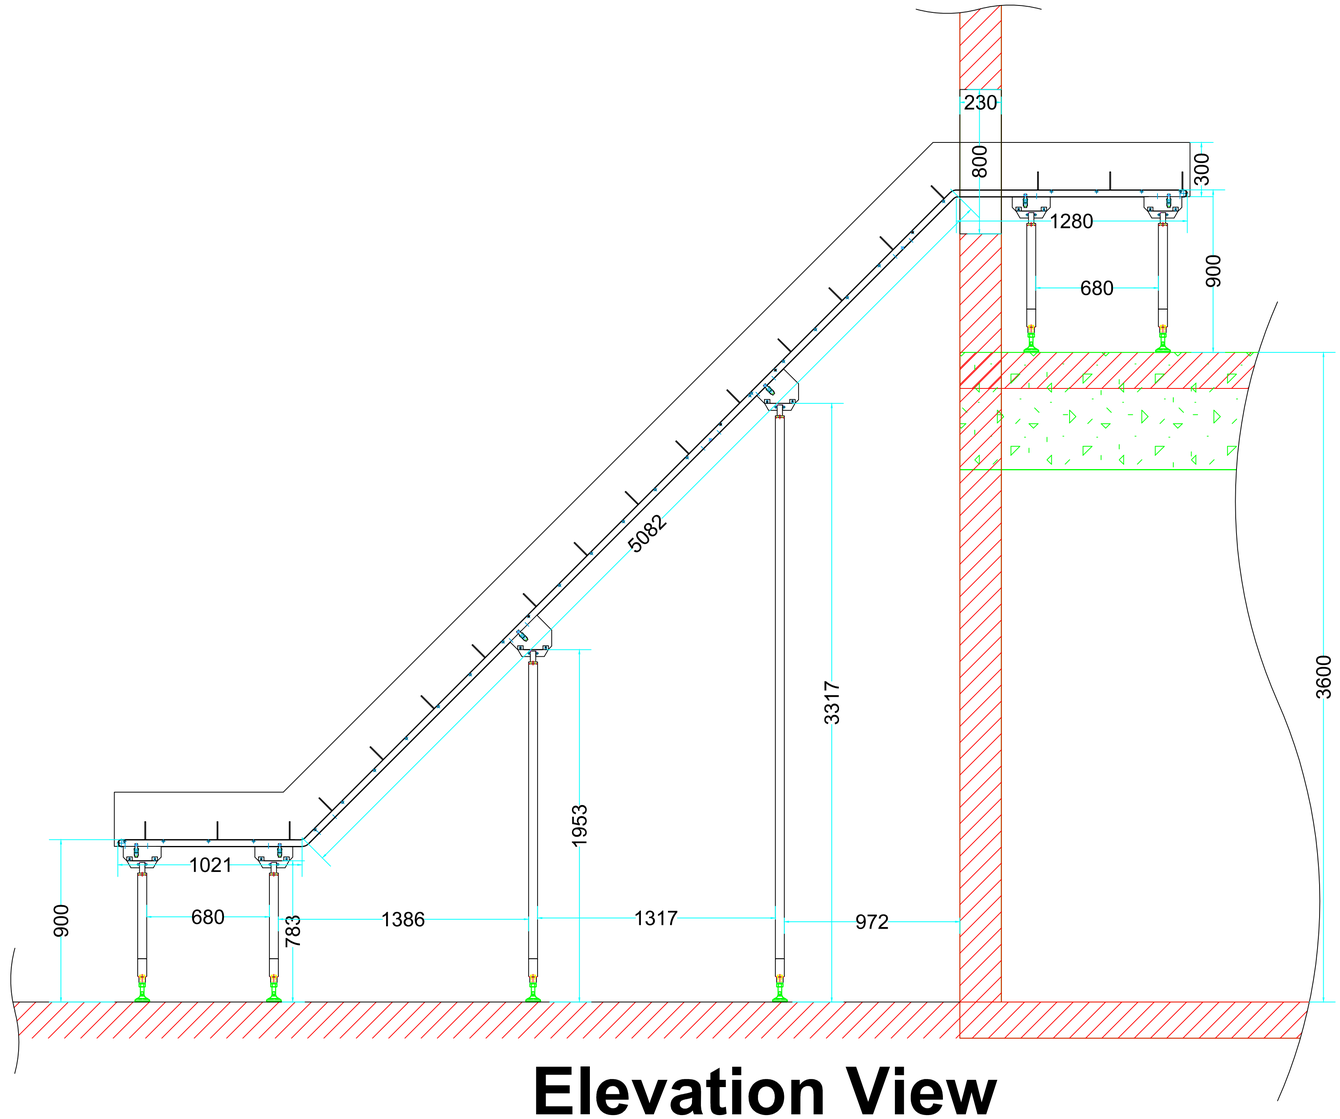

Elevation View

NOTES:-

-All dimension in mm
-This drawing is only for general size and detail of converyor
-Motor, gear, chain, shaft, bearing etc. detail is not given in drawing
-SS304 material is used

REV. No.	DESCRIPTION	DRAWN	CHECKED	APPROVED	DATE

PMG ENGINEERING PRIVATE LIMITED - NOIDA
A-224, A BLOCK, SECTOR 83, NOIDA, UTTAR PRADESH, 201305
TEL. No. 1800 212 9929, WWW.PMG.ENGINEERING

CLIENT:	Bhole Baba Milk Foods			JOB NUMBER	-		
DRAWN	SA	07.03.2022	TITLE: GA Drawing for Conveying system				
CHECKED	SA	07.03.2022					
APPROVED	AP	07.03.2022					
SCALE	NTS	DRG. No.	BBML2101-PMG-ST-2D-2007	REV No.	00	SIZE	A1

RELEASED FOR ☑ INFORMATION ☐ REVIEW ☐ CONSTRUCTION ☐ APPROVAL ☐ AS-BUILT

FILE NAME: BBML2101-PMG-ST-2D-2007-R0