




SECTION A-A'

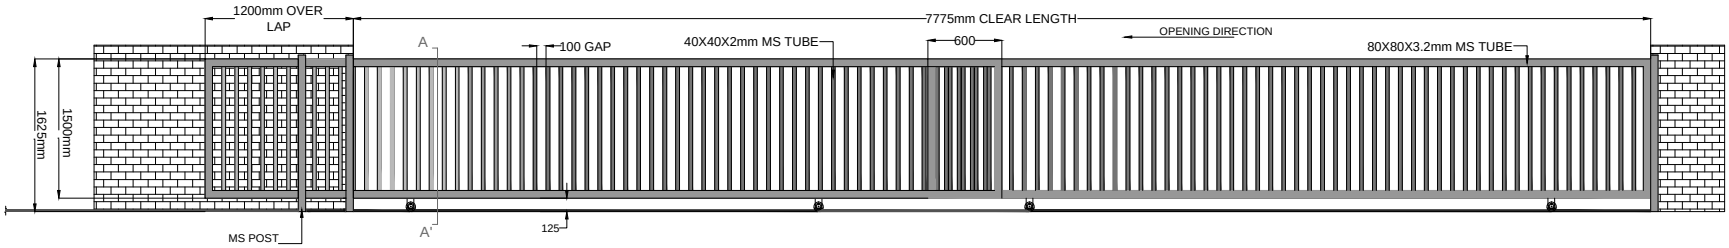


INSIDE ELEVATION

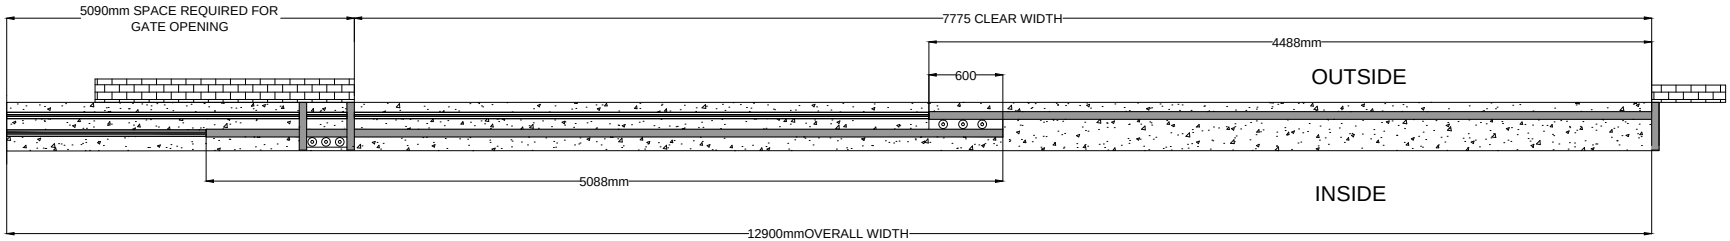

PLAN

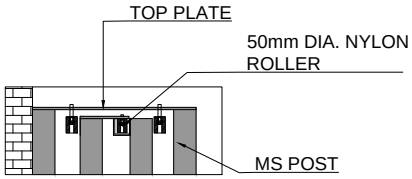

DETAIL VIEW OF B

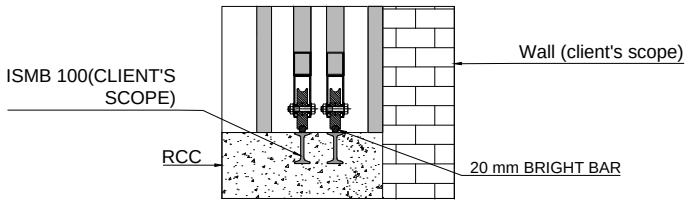

DETAIL VIEW OF A

NOTE:-
1.ALL REQUIRED CIVIL WORK BE IN CLIENTS SCOPE.
2.ONE COAT OF RED OXIDE & TWO COAT OF APPROVED RAL SHADE WILL BE GIVEN TO THE GATE.

CLEAR WIDTH	CLEAR HEIGHT	QUANTITY.
7775mm	1625mm	01 NOS

This drawing & designing is the property of NIHVA TECHNOLOGIES. Not to be sold or copied to any other concern.

TITLE: MANUAL DOUBLE LEAF TELESCOPIC GATE

		SIGN	DATE
DRAWN	SURAJ		26/06/18
CHECK	PRADEEP		26/06/18
APPROVAL	R.D		26/06/18

If any queries contact : design@nihva.com

ALL DIMENSION ARE IN mm

NIHVA TECHNOLOGIES PVT. LTD. PUNE
Tel : 020 66304033
Email:- info@nihva.com
Website:- www.nihva.com

CLIENT - **SHAPOORJI**

PROJECT -

SITE -

DWG. NO. : NIHVA/18-19/0070 | REV.

SCALE: NTS | WT: | SHEET: 01 OF 01