CRAINE DOOR

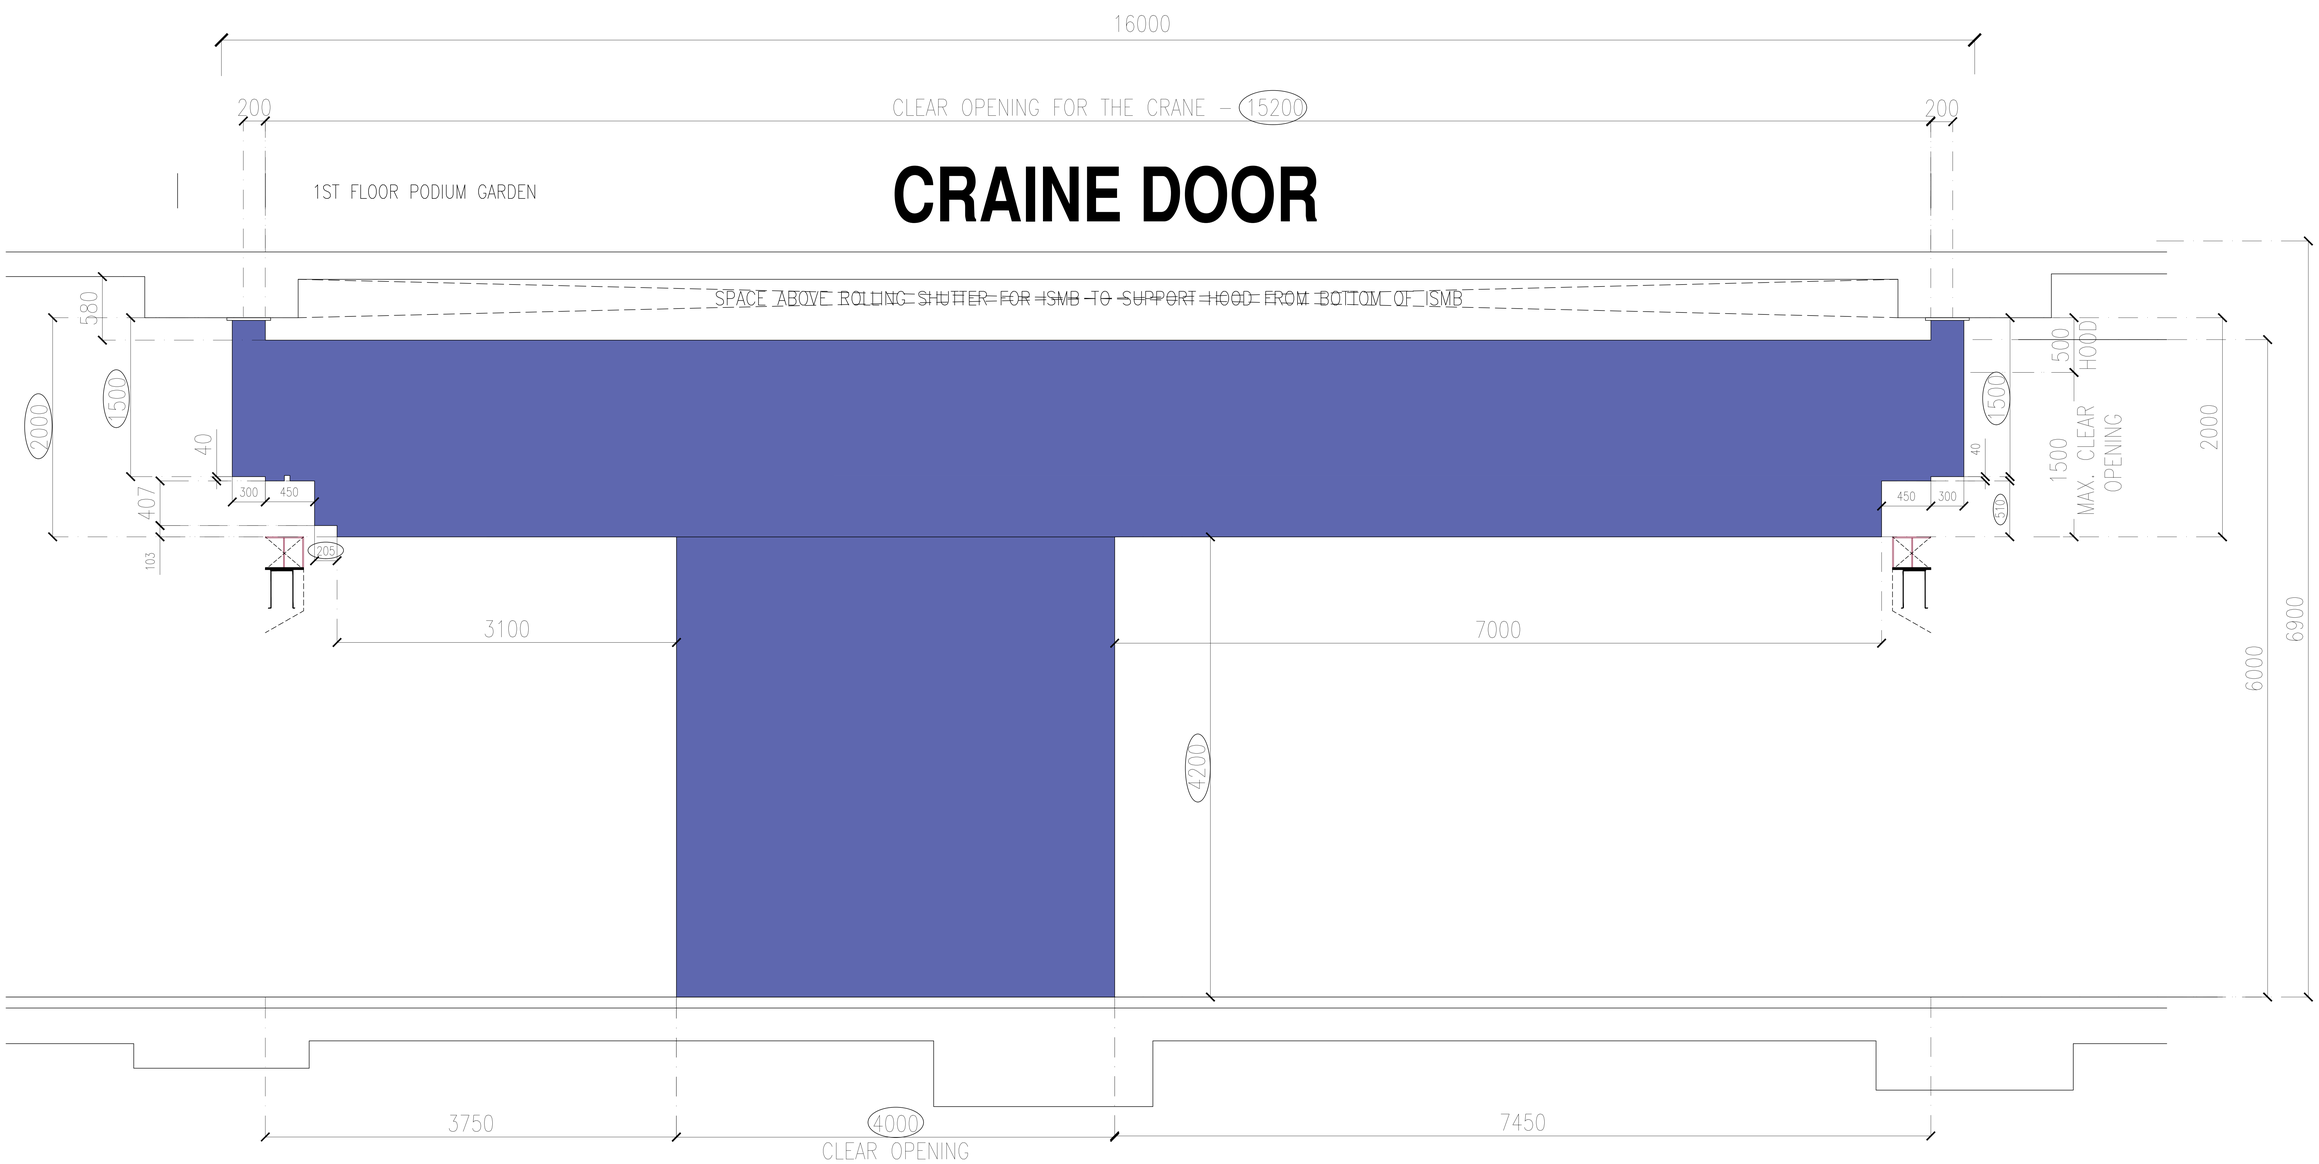
16000
200
CLEAR OPENING FOR THE CRANE – 15200
200
1ST FLOOR PODIUM GARDEN
SPACE ABOVE ROLLING SHUTTER FOR ISMB TO SUPPORT HOOD FROM BOTTOM OF ISMB
580
1500
2000
40
407
103
300
450
1205
1500
40
450
300
610
500
HOOD
1500
MAX. CLEAR OPENING
2000
6900
6000
3100
7000
4200
3750
4000
CLEAR OPENING
7450