
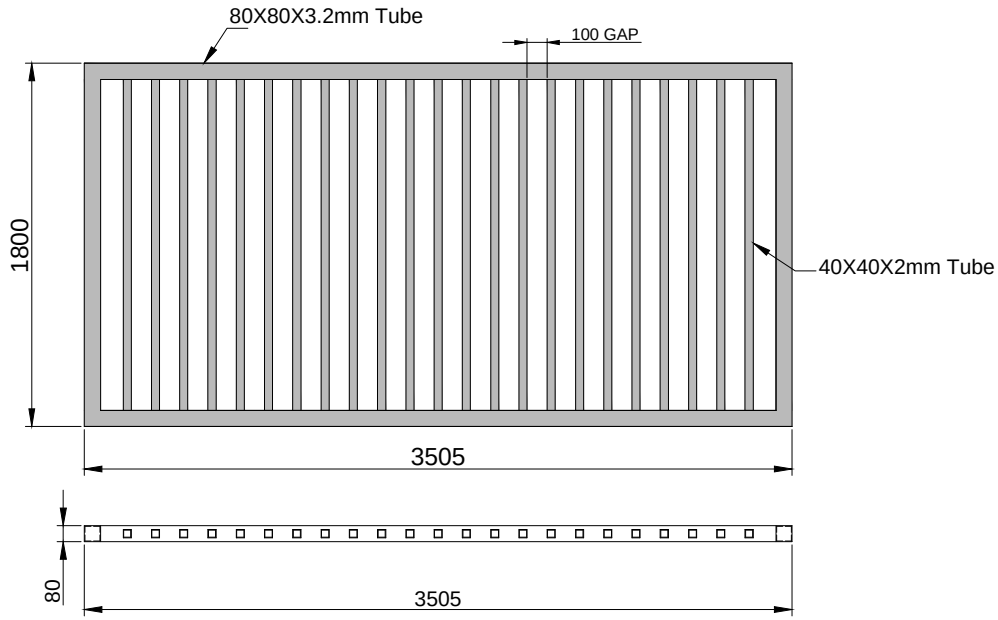


SR NO	TUBE SPECIFICATION	
1	80X80X3.2mm	OUTER TUBE
2	40X40X2mm	INNER TUBE
3	GAP B/W INNER TUBES	100mm


LEAF QTY- 2 NOS

NOTE- MAKE LOCKING ARRANGEMENT TO THE LEAFS. REFER ASSEMBLY DRG.

FIXING PLATE

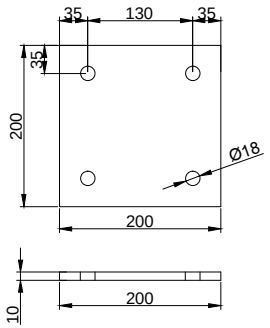

MATERIAL -MILD STEEL
THICKNESS- 10mm
QTY- 04nos

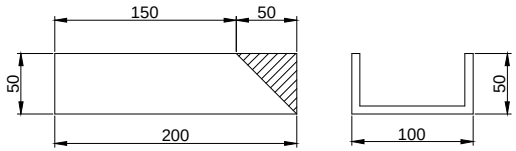

MATERIAL -MILD STEEL
ISMC100
QTY- 04nos

NOTE-
1. ALL REQUIRED CIVIL WORK WILL BE IN CLIENTS SCOPE.
2. ONE COAT OF RED OXIDE & TWO COAT OF APPROVED RAL SHADE WILL BE GIVEN TO THE GATE.
3.IF REQUIRED GATE LEAF WILL BE IN TWO PARTS FOR TRANSPORTATION & WILL BE WELD TOGETHER ON SITE.

TOLERANCE- ±10mm

This drawing & designing is the property of NIHVA TECHNOLOGIES. Not to be sold or copied to any other concern.

TITLE: GATE NO 7. SWING GATES

NIHVA TECHNOLOGIES PVT. LTD. PUNE
Tel : 020 66304033
Email:- info@nihva.com
Website:- www.nihva.com

	SIGN	DATE
DRAWN	SURAJ	05/06/17
CHECK	SHEKHAR	05/06/17
APPROVAL	SHEKHAR	05/06/17

If any queries contact : projects@nihva.com

ALL DIMENSION ARE IN mm

CLIENT -

PROJECT -

SITE LOCATION -

DWG. NO. : NIHVA/18-19/VDR/035 | REV-0

SCALE: NTS | WT: | SHEET: 01 OF 01