


0 KEY PLAN

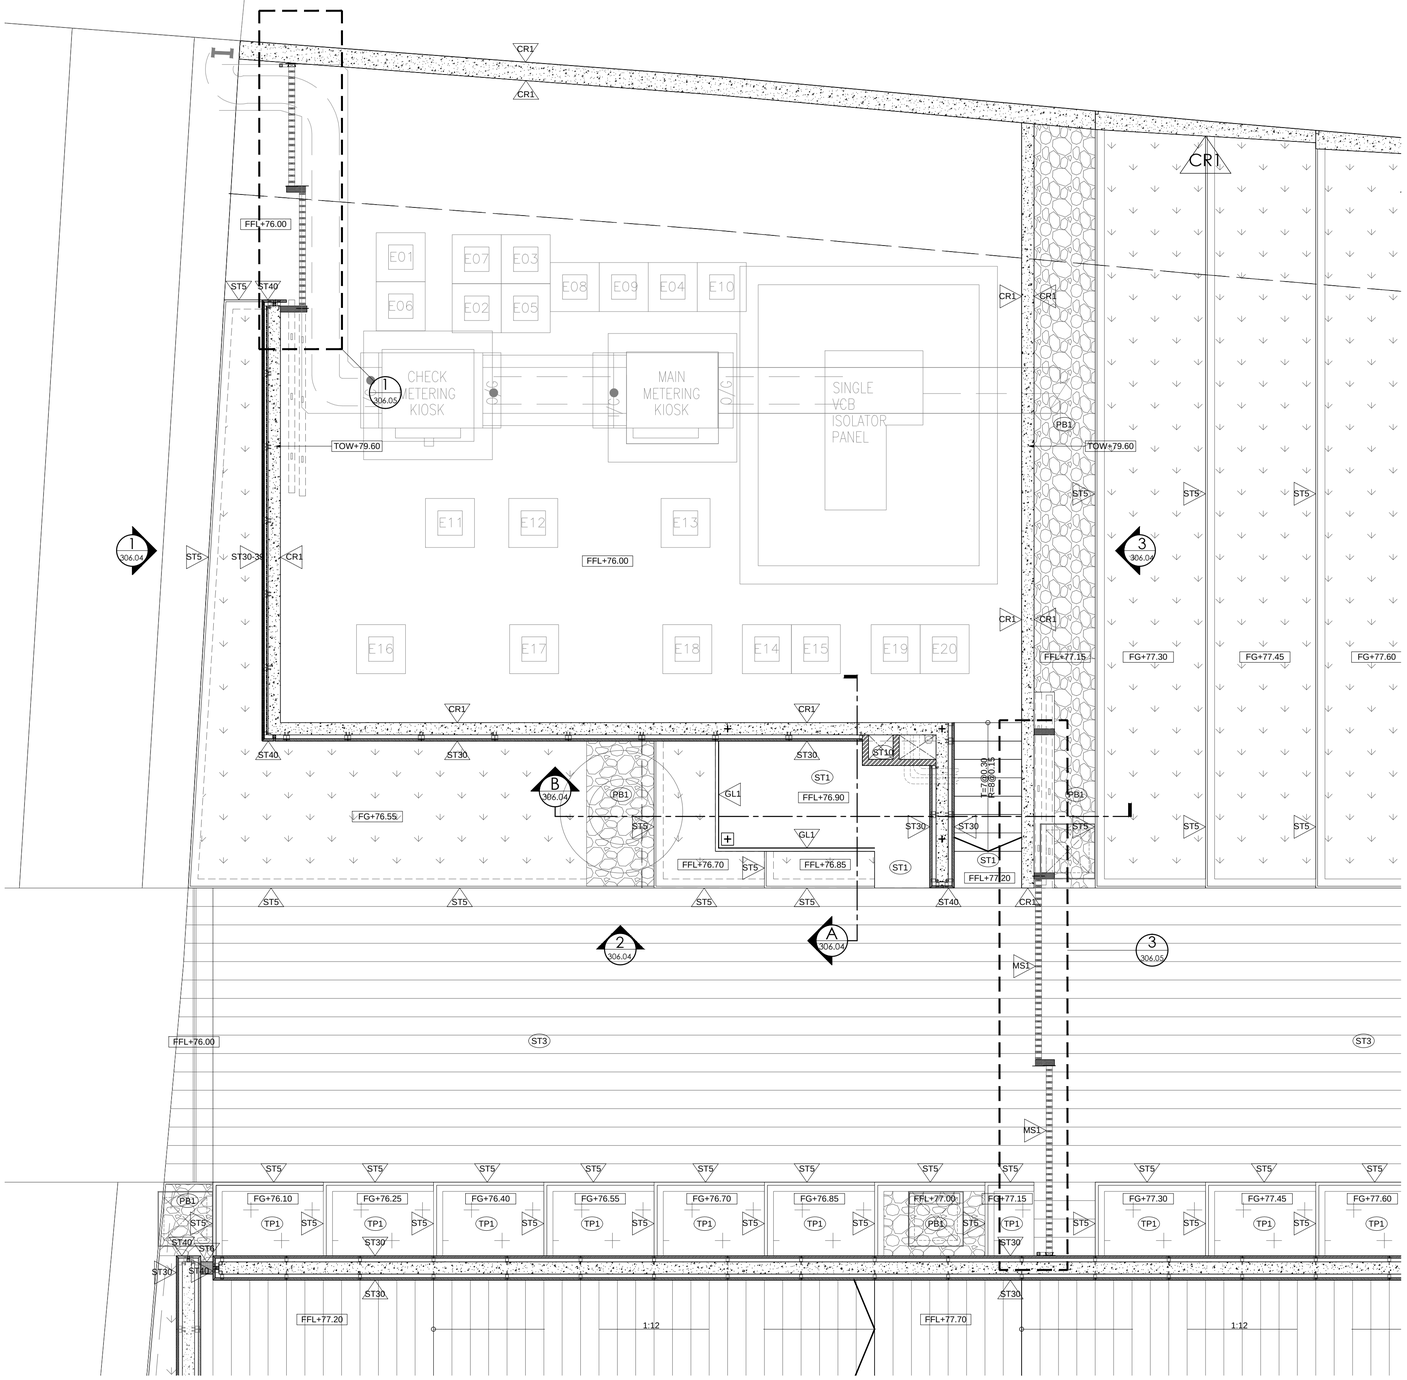

6 111.01 BLOW-UP 06 : MEP AND GUARD HOUSE DETAIL PLAN
1:50

NOTES

1. Shma Co., Ltd. All rights reserved. No copy is allowed without written permission from Shma.
2. All dimensions are to be carefully checked by the contractor. All adjustments must be made before commencement of works or frabrication of fittings.

LANDSCAPE ARCHITECT

shma

Shma Co., Ltd.
93/2 Ekkamai 3 Sukhumvit 63 Rd.
Klongton Nuer Vadhana
Bangkok Thailand 10110
TEL:662 390 1977 Fax:662 390 1974
Email: admin@shmadesigns.com

CLIENT / OWNER


LUPIN LIMITED
MUMBAI


ARCHITECT

Venkataramanan Associates
ARCHITECTURE - URBAN DESIGN
10/2 , O'SHAUGHNESSY ROAD, LANGFORD GARDENS, BANGALORE– 560 025

PROJECT TITLE : LUPIN RESEARCH PARK, PUNE, INDIA

JOB NO.	315	**DATE**	17.08.15	**PROJECT LA**	**DRAWING NAME**	**DRAWING NO.**	**ISSUED FOR**	**STAGE**	**REV**	**DESCRIPTION**	**NORTH**
SCALE	**A0** -	**CHECKED BY**	PRAPAN	PRAPAN NAPAWONGDEE	*BLOW-UP 06*	*306.01*	CONSTRUCTION	GFC			
	A1 *1:50*	**DRAWN BY**	KATAVET	KATAVET SITTIKIT	*MEP AND GUARD HOUSE DETAILPLAN*						
	A3 -			KRITTAYA and PAT							

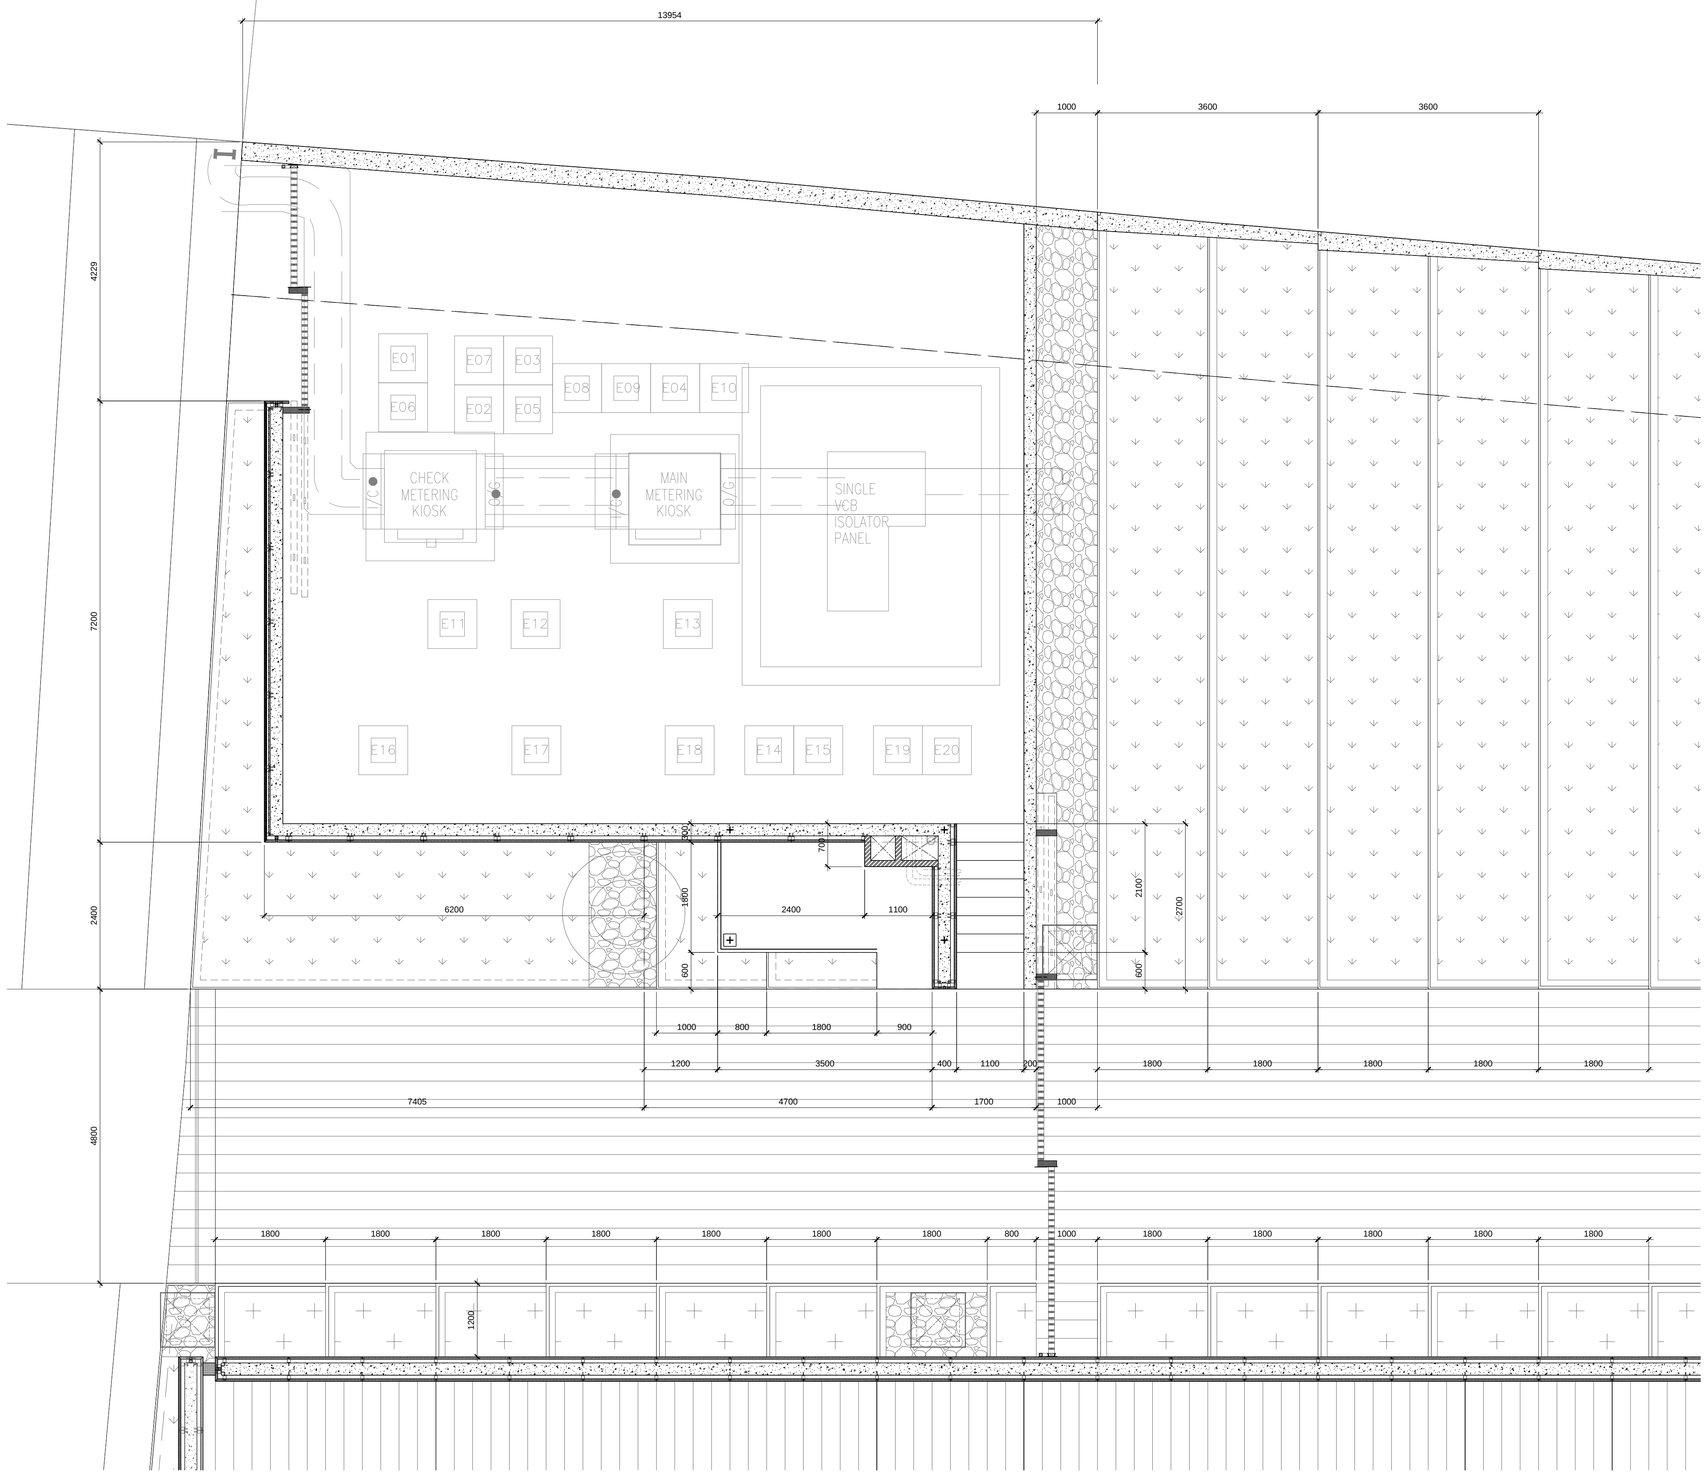

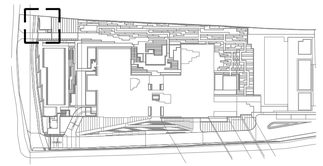

0 KEY PLAN

6 (11.01) BLOW-UP 06 : MEP AND GUARD HOUSE SETTING-OUT PLAN
1:50

NOTES

1. Shma Co., Ltd. All rights reserved.
   No copy is allowed without written permission from Shma.
2. All dimensions are to be carefully checked by the contractor.
   All adjustments must be made before commencement of works or frabrication of fittings.

LANDSCAPE ARCHITECT

Shma Co., Ltd.
93/2 Ekkamai 3 Sukhumvit 63 Rd.
Klongton Nuer Vadhana
Bangkok Thailand 10110
TEL:662 390 1977 Fax:662 390 1974
Email: admin@shmadesigns.com

CLIENT / OWNER


LUPIN LIMITED
MUMBAI

ARCHITECT


Venkataramanan Associates
ARCHITECTURE - URBAN DESIGN
10/2 , O'SHAUGHNESSY ROAD, LANGFORD GARDENS, BANGALORE– 560 025

PROJECT TITLE : LUPIN RESEARCH PARK, PUNE, INDIA


JOB NO.	315	**DATE**	17.08.15	**PROJECT LA**	**DRAWING NAME**	**DRAWING NO.**	**ISSUED FOR**	**STAGE**	**REV**	**DESCRIPTION**	**NORTH**
SCALE	**A0** -	**CHECKED BY**	PRAPAN	PRAPAN NAPAWONGDEE	*BLOW-UP 06*	*306.02*	CONSTRUCTION	GFC			
	A1 *1:50*	**DRAWN BY**	KATAVET	KATAVET SITTIKIT	*MEP AND GUARD HOUSE*						
	A3 -			KRITTAYA and PAT	*SETTING-OUT PLAN*						

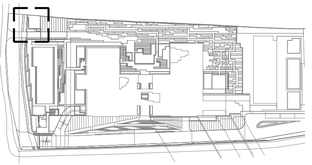

0 KEY PLAN

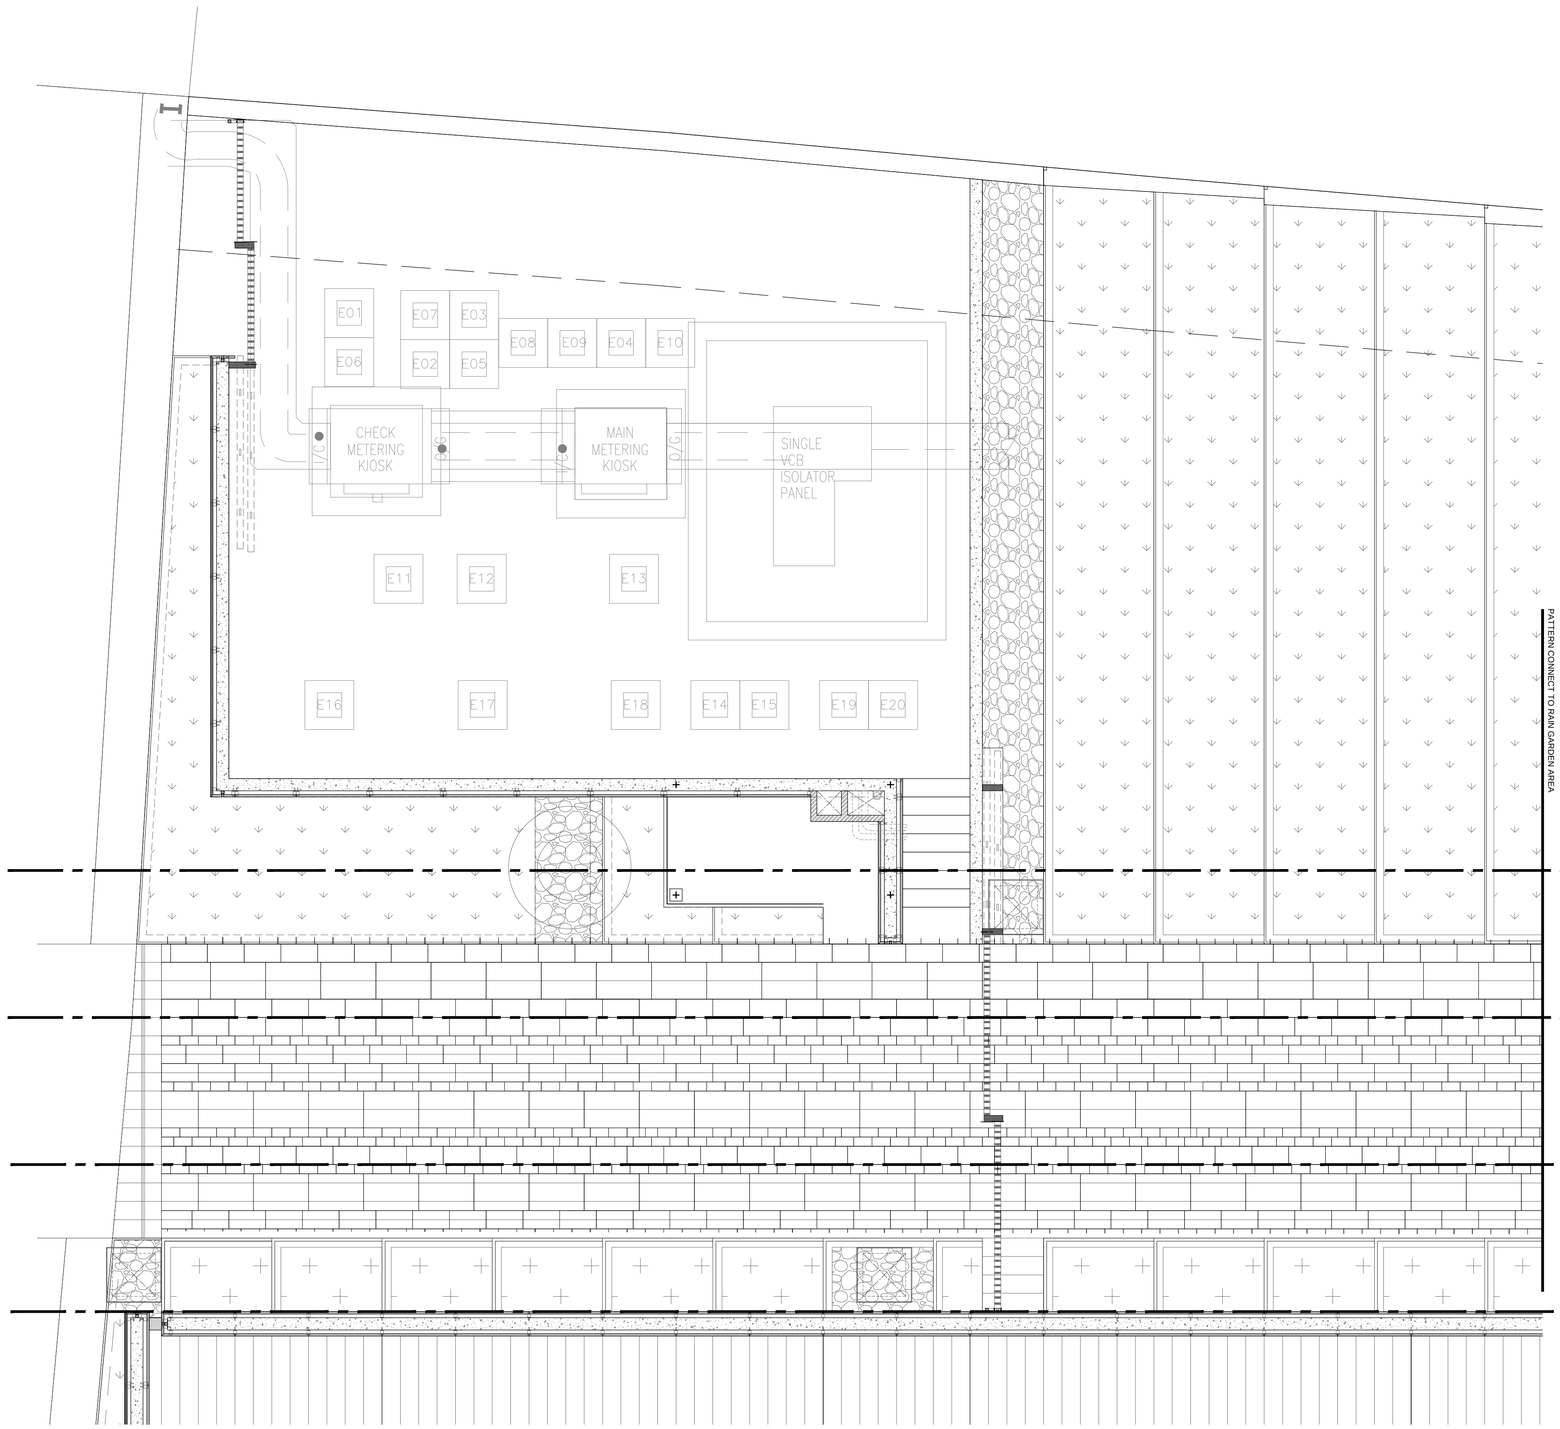

6 111.01 BLOW-UP 06 : MEP AND GUARD HOUSE PATTERN PLAN
1:50

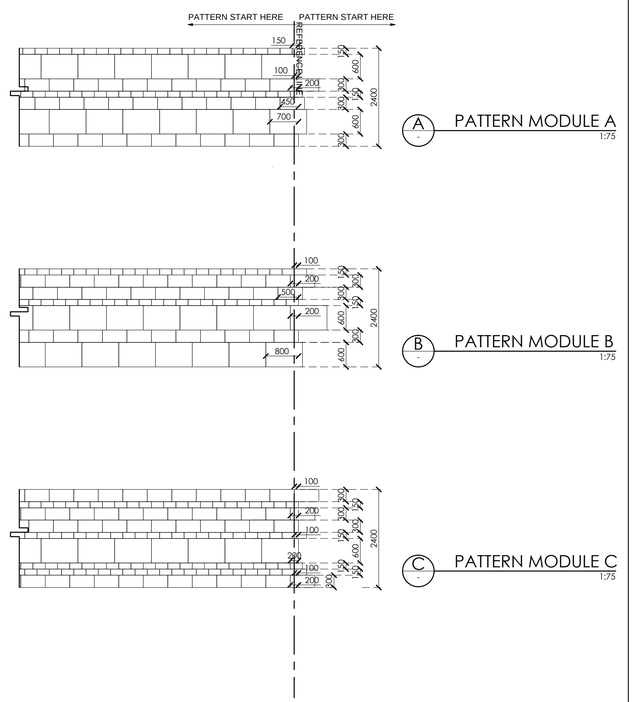

NOTES

1. Shma Co., Ltd. All rights reserved.
   No copy is allowed without written permission from Shma.
2. All dimensions are to be carefully checked by the contractor.
   All adjustments must be made before commencement of works or frabrication of fittings.

LANDSCAPE ARCHITECT

shma

Shma Co., Ltd.
93/2 Ekkamai 3 Sukhumvit 63 Rd.
Klongton Nuer Vadhana
Bangkok Thailand 10110
TEL:662 390 1977 Fax:662 390 1974
Email: admin@shmadesigns.com

CLIENT / OWNER

LUPIN LIMITED
MUMBAI


ARCHITECT

Venkataramanan Associates
ARCHITECTURE - URBAN DESIGN
10/2 , O'SHAUGHNESSY ROAD, LANGFORD GARDENS, BANGALORE– 560 025


PROJECT TITLE : LUPIN RESEARCH PARK, PUNE, INDIA

JOB NO.	315	**DATE**	17.08.15	**PROJECT LA**	**DRAWING NAME**	**DRAWING NO.**	**ISSUED FOR**	**STAGE**	**REV**	**DESCRIPTION**
SCALE	**A0** -	**CHECKED BY**	PRAPAN	PRAPAN NAPAWONGDEE	*BLOW-UP 06*	*306.03*	CONSTRUCTION	GFC		
	A1 *1:50*	**DRAWN BY**	KATAVET	KATAVET SITTIKIT	*MEP AND GUARD HOUSE*					
	A3 -			KRITTAYA and PAT	*PATTERN PLAN*					


NORTH

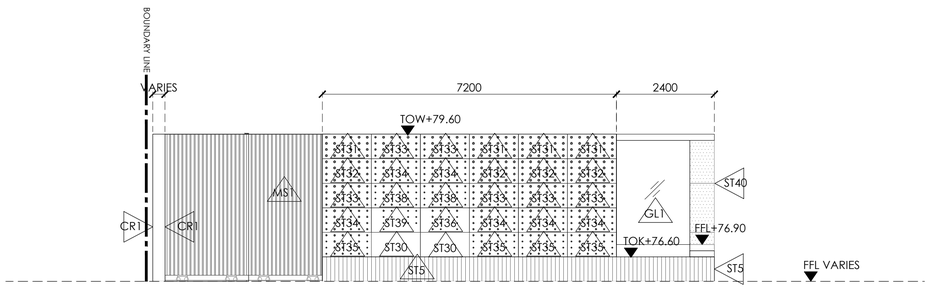


1 306.01 BLOW-UP 06 : MEP AND GUARD HOUSE ELEVATION 1
1:75

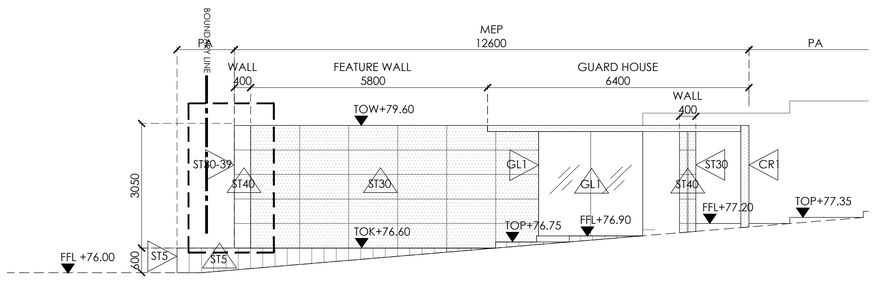


2 306.01 BLOW-UP 06 : MEP AND GUARD HOUSE ELEVATION 2
1:75

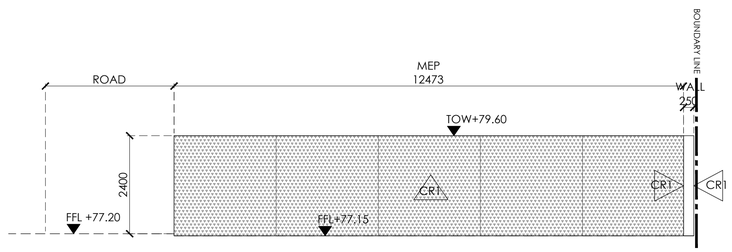


3 306.01 BLOW-UP 06 : MEP AND GUARD HOUSE ELEVATION 3
1:75

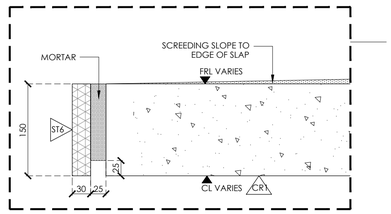

1 ROOF EDGE TYPICAL DETAIL
1:5

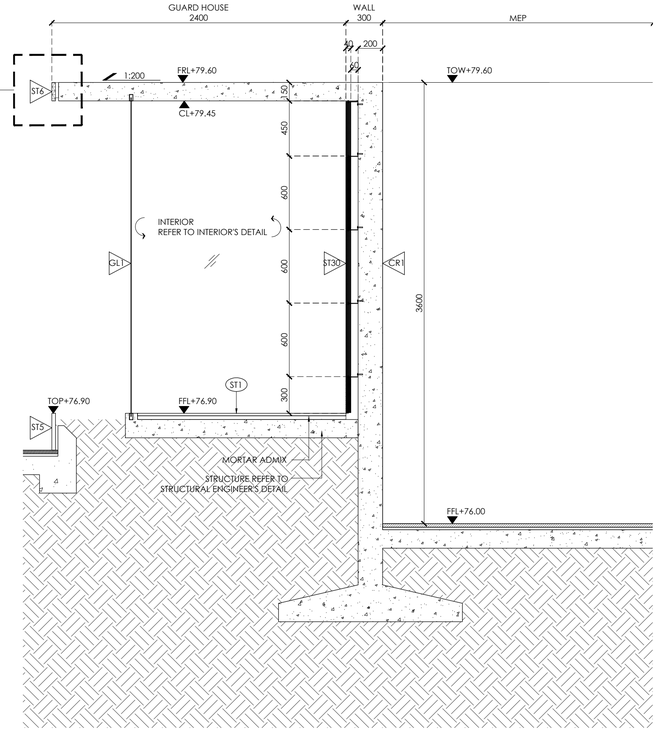

A 306.01 BLOW-UP 06 : MEP AND GUARD HOUSE SECTION A
1:25

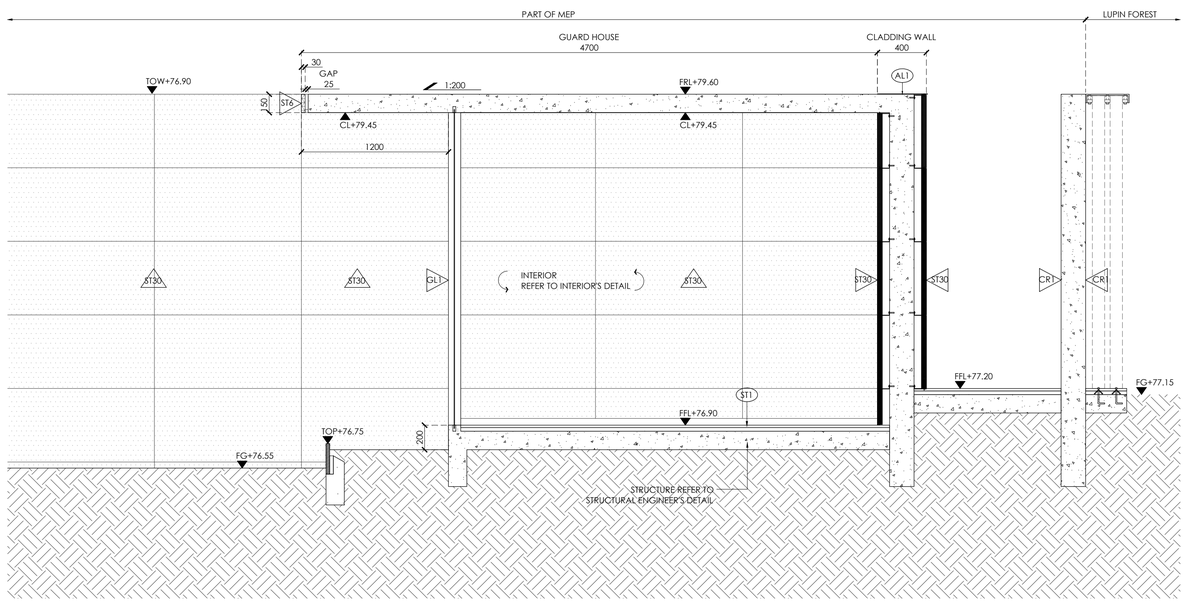

B 306.01 BLOW-UP 06 : MEP AND GUARD HOUSE SECTION B
1:25

NOTES

1. Shma Co., Ltd. All rights reserved.
   No copy is allowed without written permission from Shma.
2. All dimensions are to be carefully checked by the contractor.
   All adjustments must be made before
   commencement of works or frabrication of fittings.

LANDSCAPE ARCHITECT

shma

Shma Co., Ltd.
93/2 Ekkamai 3 Sukhumvit 63 Rd.
Klongton Nuer Vadhana
Bangkok Thailand 10110
TEL:662 390 1977 Fax:662 390 1974
Email: admin@shmadesigns.com

CLIENT / OWNER


LUPIN LIMITED
MUMBAI

ARCHITECT


Venkataramanan Associates
ARCHITECTURE - URBAN DESIGN
10/2 , O'SHAUGHNESSY ROAD, LANGFORD GARDENS, BANGALORE– 560 025

PROJECT TITLE : LUPIN RESEARCH PARK, PUNE, INDIA


JOB NO.	315	**DATE**	17.08.15	**PROJECT LA**	**DRAWING NAME**	**DRAWING NO.**	**ISSUED FOR**	**STAGE**	**REV**	**DESCRIPTION**	**NORTH**
SCALE	**A0** -	**CHECKED BY**	PRAPAN	PRAPAN NAPAWONGDEE	*BLOW-UP 06*						
	A1 *AS SHOWN*	**DRAWN BY**	KATAVET	KATAVET SITTIKIT	*MEP AND GUARD HOUSE*	*306.04*	CONSTRUCTION	GFC			
	A3 -			KRITTAYA and PAT	*SECTION & ELEVATION*						

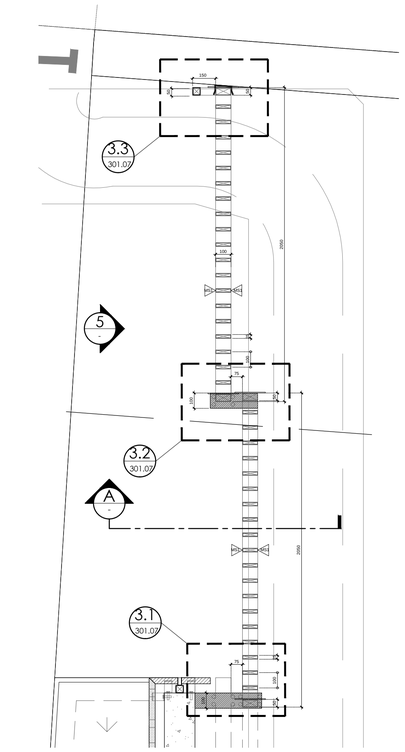


1 306.01 SLIDING DOOR PLAN @MEP AREA (CLOSE) 1:10

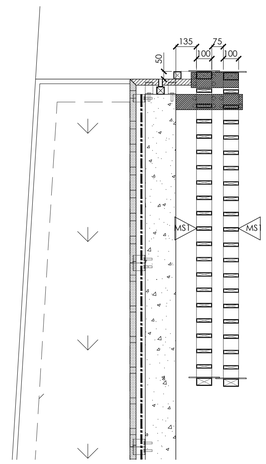


2 - SLIDING DOOR PLAN @MEP AREA (OPEN) 1:20

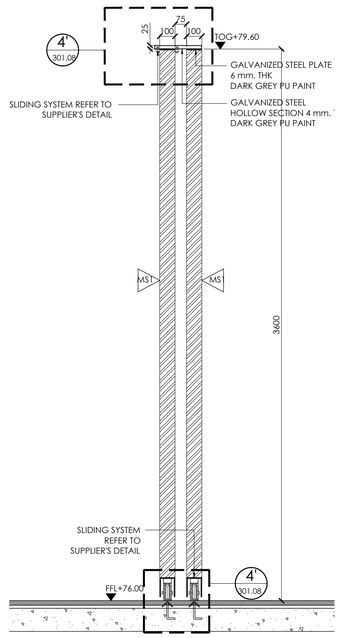


A - SECTION A 1:20

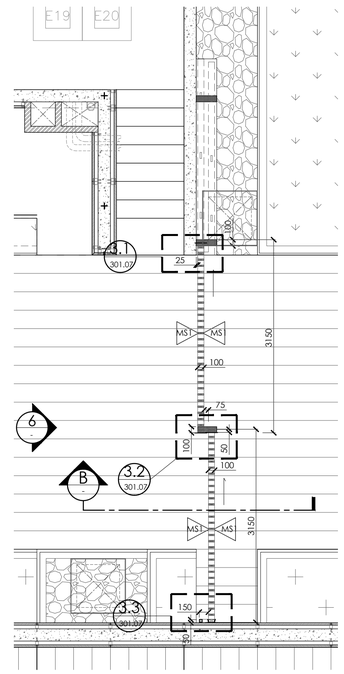


3 306.01 SLIDING GATE @VIP ENTRANCE (CLOSE) 1:50

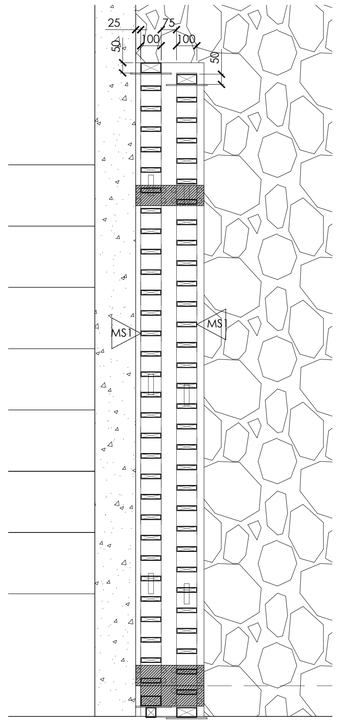


4 - SLIDING GATE @VIP ENTRANCE (OPEN) 1:15

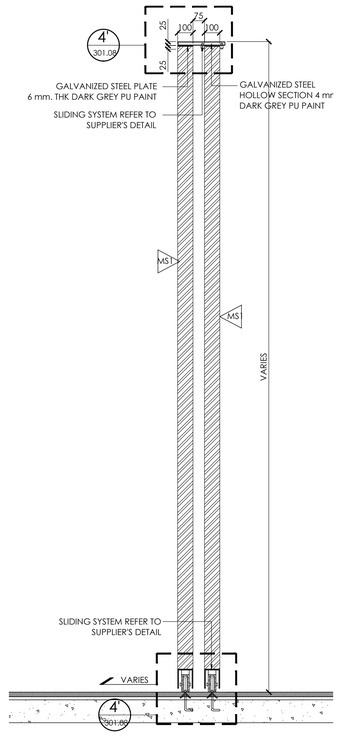

B - SECTION B 1:20

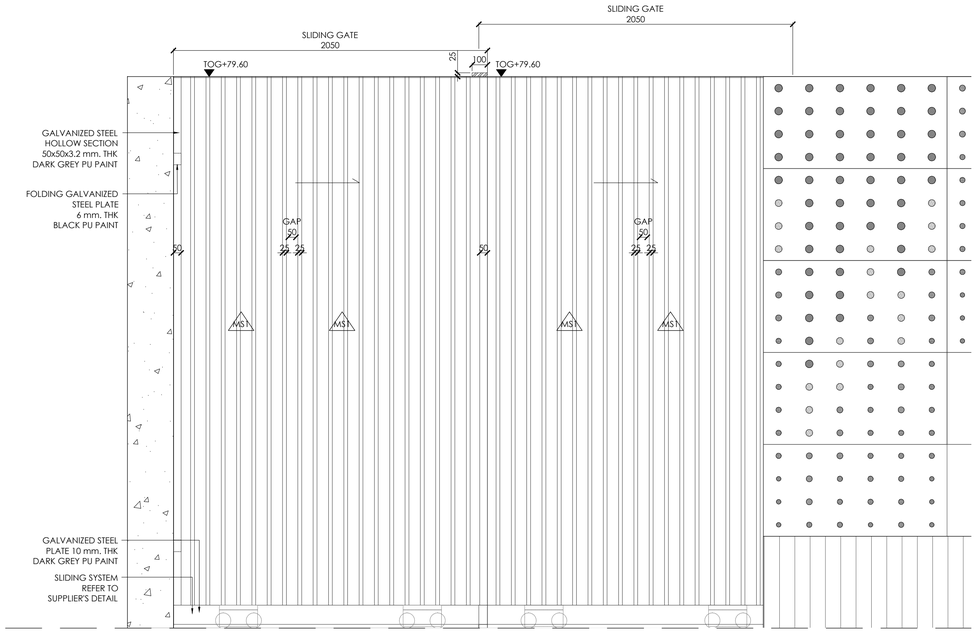

5 - SLIDING DOOR ELEVATION @MEP AREA 1:20

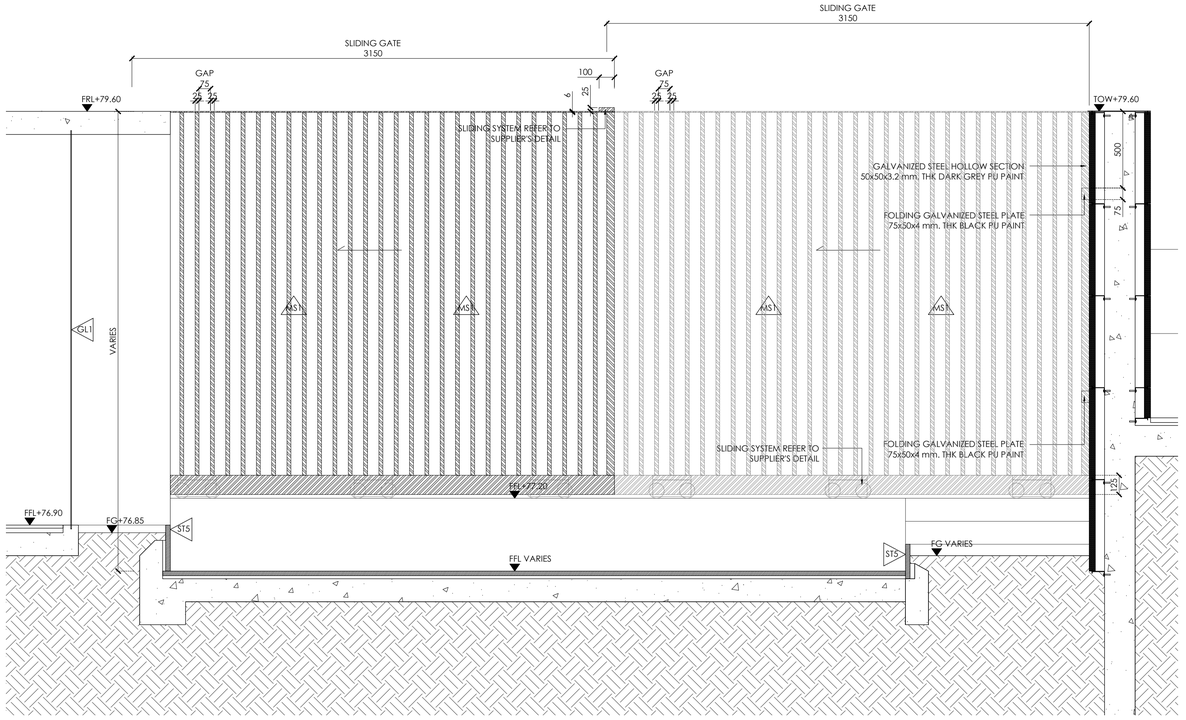

6 - SLIDING GATE ELEVATION @VIP ENTRANCE 1:20

NOTES

1. Shma Co., Ltd. All rights reserved.
   No copy is allowed without written permission from Shma.
2. All dimensions are to be carefully checked by the contractor.
   All adjustments must be made before
   commencement of works or frabrication of fittings.

LANDSCAPE ARCHITECT

Shma Co., Ltd.
93/2 Ekkamai 3 Sukhumvit 63 Rd.
Klongton Nuer Vadhana
Bangkok Thailand 10110
TEL:662 390 1977 Fax:662 390 1974
Email: admin@shmadesigns.com

CLIENT / OWNER

LUPIN LIMITED
MUMBAI

ARCHITECT

Venkataramanan Associates
ARCHITECTURE - URBAN DESIGN
10/2 , O'SHAUGHNESSY ROAD, LANGFORD GARDENS, BANGALORE– 560 025

PROJECT TITLE : LUPIN RESEARCH PARK, PUNE, INDIA

JOB NO.	315	**DATE**	17.08.15	**PROJECT LA**	**DRAWING NAME**	**DRAWING NO.**	**ISSUED FOR**	**STAGE**	**REV**	**DESCRIPTION**	**NORTH**
SCALE	**A0** -	**CHECKED BY**	PRAPAN	PRAPAN NAPAWONGDEE	*BLOW-UP 06*	*306.05*	CONSTRUCTION	GFC			
	A1 *AS SHOWN*	**DRAWN BY**	KATAVET	KATAVET SITTIKIT	*VIP ENTRANCE*						
	A3 -			KRITTAYA and PAT	*SLIDING DOOR DETAIL*						