
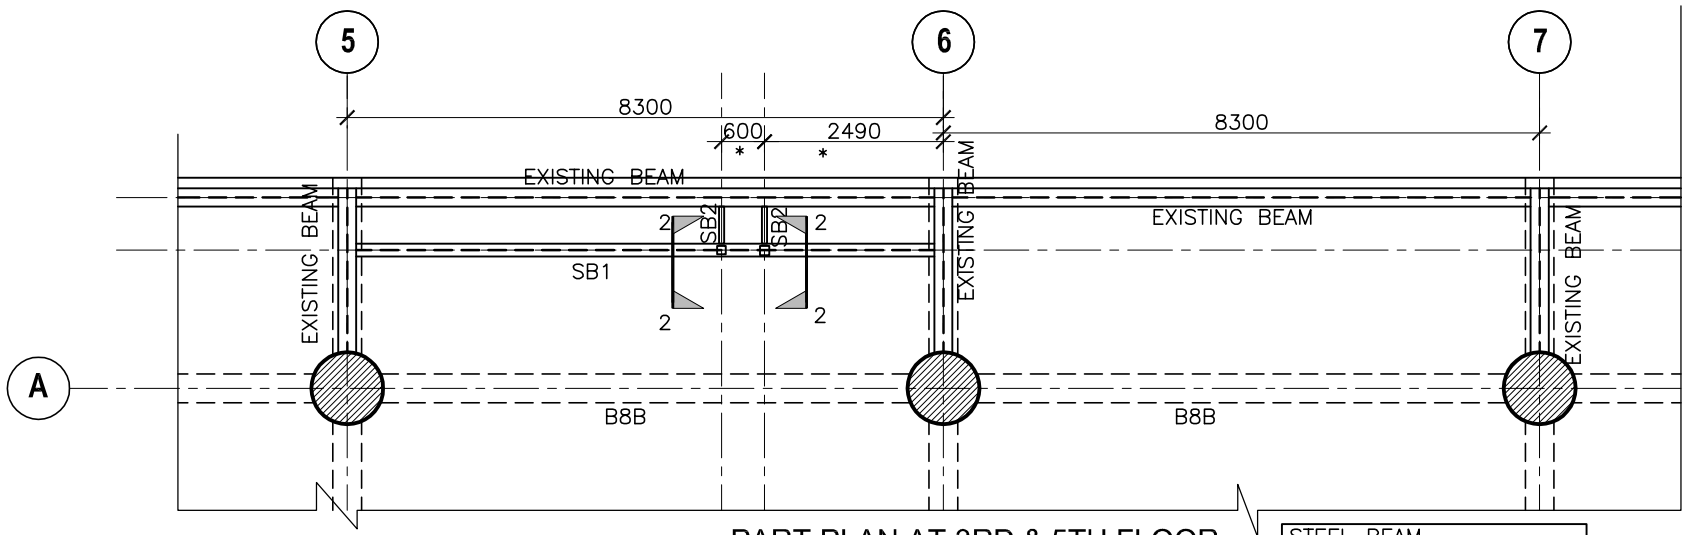



PART PLAN AT 3RD & 5TH FLOOR
(SCALE 1:100)

NOTE:– *DISTANCE SHALL BE VERIFY BY DOOR VENDOR DRAWING


STEEL BEAM
SB2–TUBE 70x70x4THK.

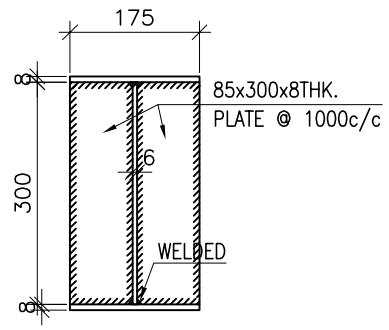


SB1 DETAILS
(SCALE 1:10)

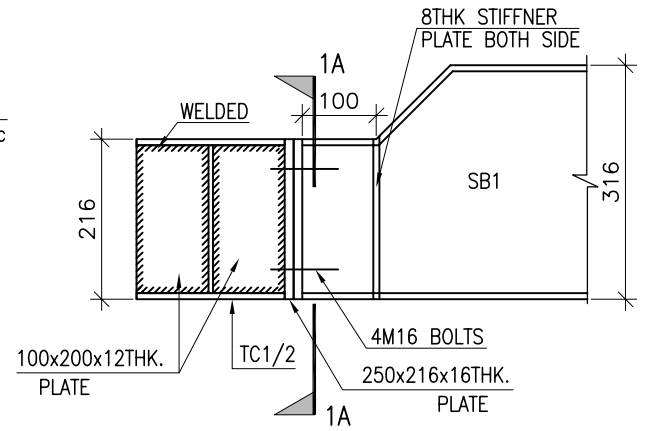


TC1/TC2–SB1 CONNECTION DETAILS
(SCALE 1:10)

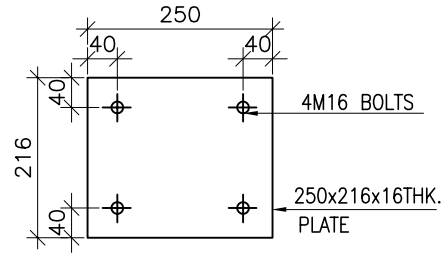

VIEW 1A–1A
(SCALE 1:10)

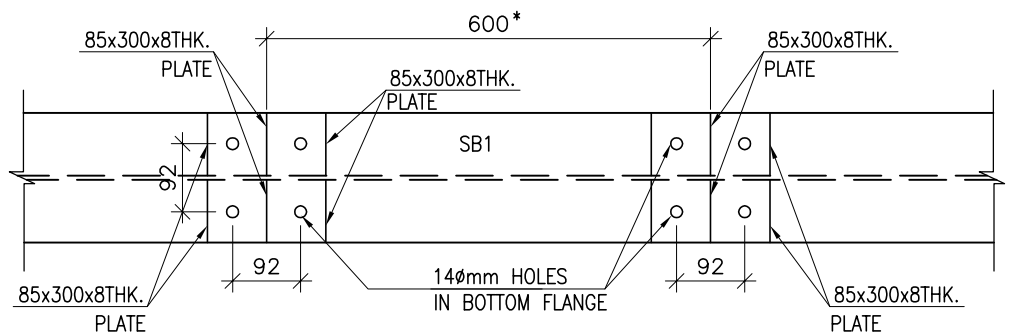

VIEW 2A–2A
(SCALE 1:10)

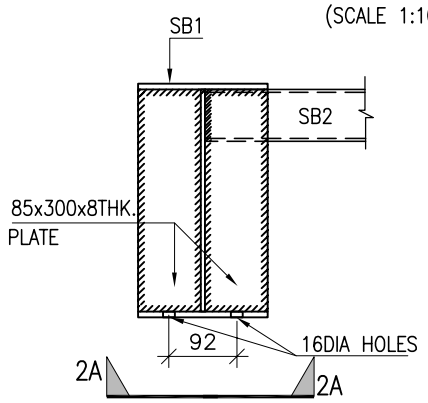

VIEW 2–2
(SCALE 1:10)

NOTE:–
1) ALL STEELWORK TO BE OF FY=250MPA
2) ALL BOLTS GRADE 8:8
3) ALL WELDED TO BE 6MM FILLET, UNO.
4) ACTUAL SITE DIMENSIONS TO BE TAKEN PRIOR FABRICATION.
5) SHOP DRAWINGS TO BE MADE FOR ENGINEERS APPROVAL.
6) INCASE OF NON–AVAILABILITY OF MATERIAL, NEXT HIGHER SIZE TO BE PROPOSED. SECTION MODULUS, AREA & MOMENT OF INERTIA OF PROPOSED SECTION MUST BE EQUAL TO OR HIGHER THAN SECTION SPECIFIED ON DRAWING.
7) COVER FOR TOP & BOTTOM IN SLAB TO BE 20MM.
8) ALL STEEL WORKS TO BE SAND/SHOT BLASTED, PRIMED WITH ZINC PHOSPHATE PRIMER & COATED WITH EPOXY PAINT HAVING A MINIMUM THICKNESS OF 150MICRONS
9) BUILT UP SECTION TO BE MADE USING FULL FILLET WELD(6MM) ON ONE SIDE AND RUNS OF 100MM @ EVERY 500MM C/C FOR OTHER SIDE

No	Description	By	Chk	Date
RO	GOOD FOR CONSTRUCTION	R.P.	R.M	29-12-2016

Drawn by : R.P.
Checked by : R.M
Approved by : R.M.
Date : 29-12-2016

Title : PART PLAN AT 3RD& 5TH FLOOR
Project : PROPOSED COMMERZONE, FOR K. RAHEJA CORP, AT YERWADA, PUNE.
Architect :
Client : Nvidia Graphics Private Limited

Structural consultant:
Design Werkz Engineering Pvt.LTD
Artha Vishwa 3rd Floor Lane 5,
Koregaon Park, Pune 411001.
Tel : +91-20-32900573 / 26052921
Fax : +91-20-66201389 web:www.designwerkzeng.com

Job no: -
Dwg. No: ST-104
Drg. Size: A3
Sheet No: 1
Rev. No: R0
Scale: AS SHOWN
Drawing status: GOOD FOR CONSTRUCTION

This drawing is the property of Design Werkz Engineering Pvt.LTD and shall not be reproduced or used without written permission.