

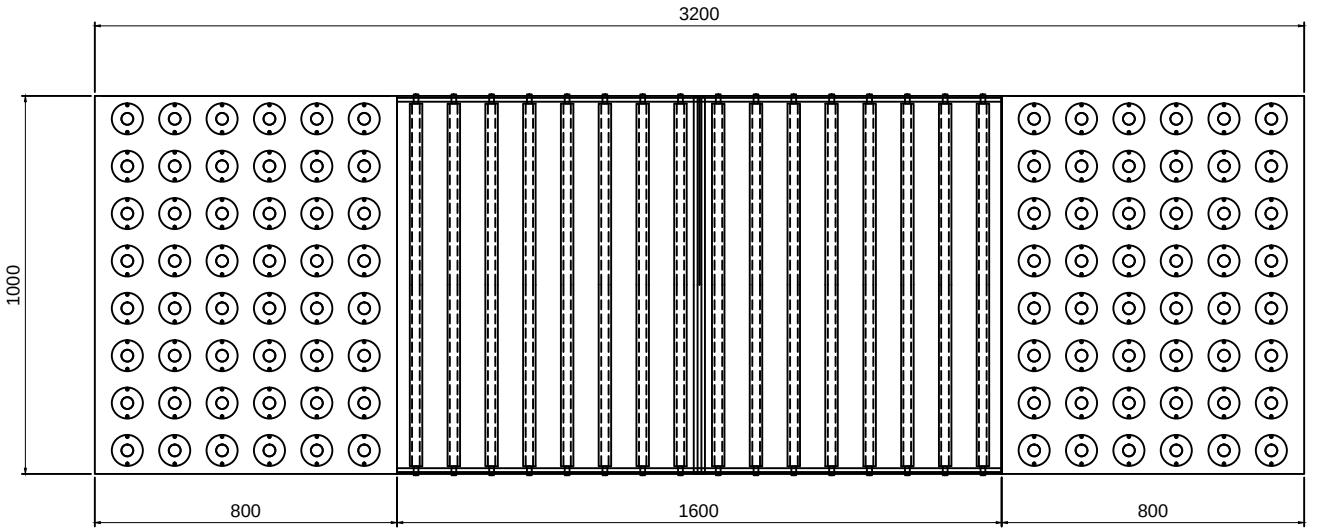


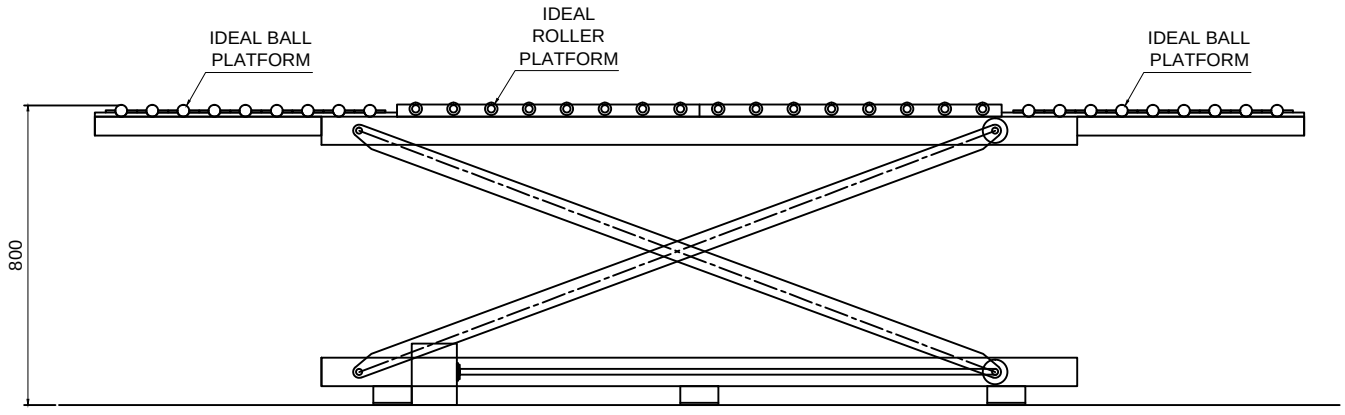

OPEN POSITION

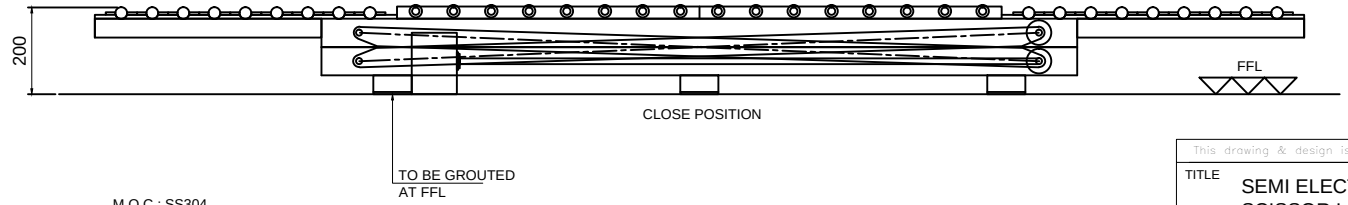

CLOSE POSITION

TO BE GROUTED AT FFL

M.O.C : SS304
(EXCLUDING DRIVE)

This drawing & design is the property of NIHVA TECHNOLOGIES. Not to be sold or copied to any other concern.

TITLE	SEMI ELECTRIC SCISSOR LIFT			NIHVA TECHNOLOGIES PVT. LTD. PUNE Tel : 020 66304033 Email:- info@nihva.com Website:- www.nihva.com
	NAME	SIGN	DATE	
DRAWN	P.A		24.08.2020	CLIENT - INFINITY AUTOMATED SOLUTION
CHECK	G.J		24.08.2020	PROJECT -
APPRD.				SITE LOCATION - PUNE
If any queries contact : design@nihva.com				DWG. NO. : NIHVA/20-21/0046
ALL DIMENSION ARE IN mm				SCALE: NTS / WT: / REV- 00