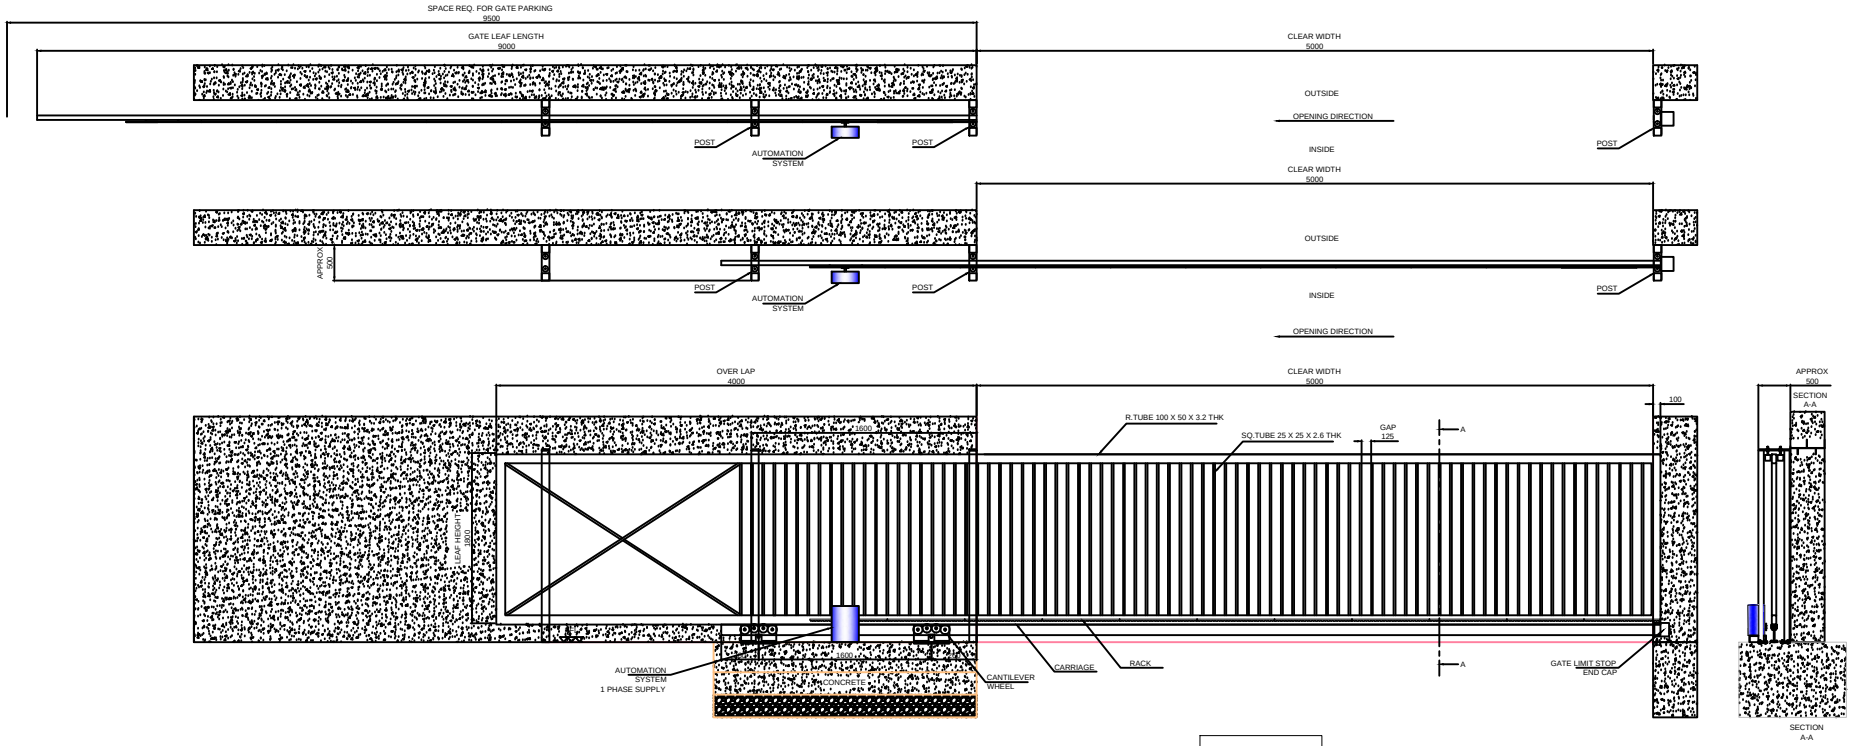


QTY : 2 NOS

TOLERANCE - ±10mm

NOTE-
1. ALL REQUIRED CIVIL WORK WILL BE IN CLIENTS SCOPE.
2. TWO COATS OF PRIMER AND TWO COATS OF SYNTHETIC ENAMEL PAINT OF APPROVE SHADE.
3. SAFETY ACCESSORIES : FLASHING LIGHT, SAFETY PHOTOCELL.
4. GATE LEAF WILL BE IN TWO/THREE PARTS FOR TRANSPORTATION & WILL BE WELD TOGETHER ON SITE.

This drawing & design is the property of NIHVA TECHNOLOGIES, not to be used or copied for any other purpose.

TITLE: AUTOMATIC CANTILEVER GATE	NIHVA TECHNOLOGIES PVT. LTD.		NIHVA TECHNOLOGIES PVT. LTD. PUNE Tel : 020 66304033 Email - info@nihva.com Website:- www.nihva.com
	NAME	SIGN	DATE
DRAWN	P.A		24.01.2020
CHECK	G.J		24.01.2020
APPRD.			
CLIENT -			
PROJECT -			
SITE LOCATION -			
If any queries contact : design@nihva.com	DWG. NO. : NIHVA/1 9-20/VDR/290		REV- R00
ALL DIMENSION ARE IN mm	SCALE: NTS	WT:	SHEET: 01 OF 01