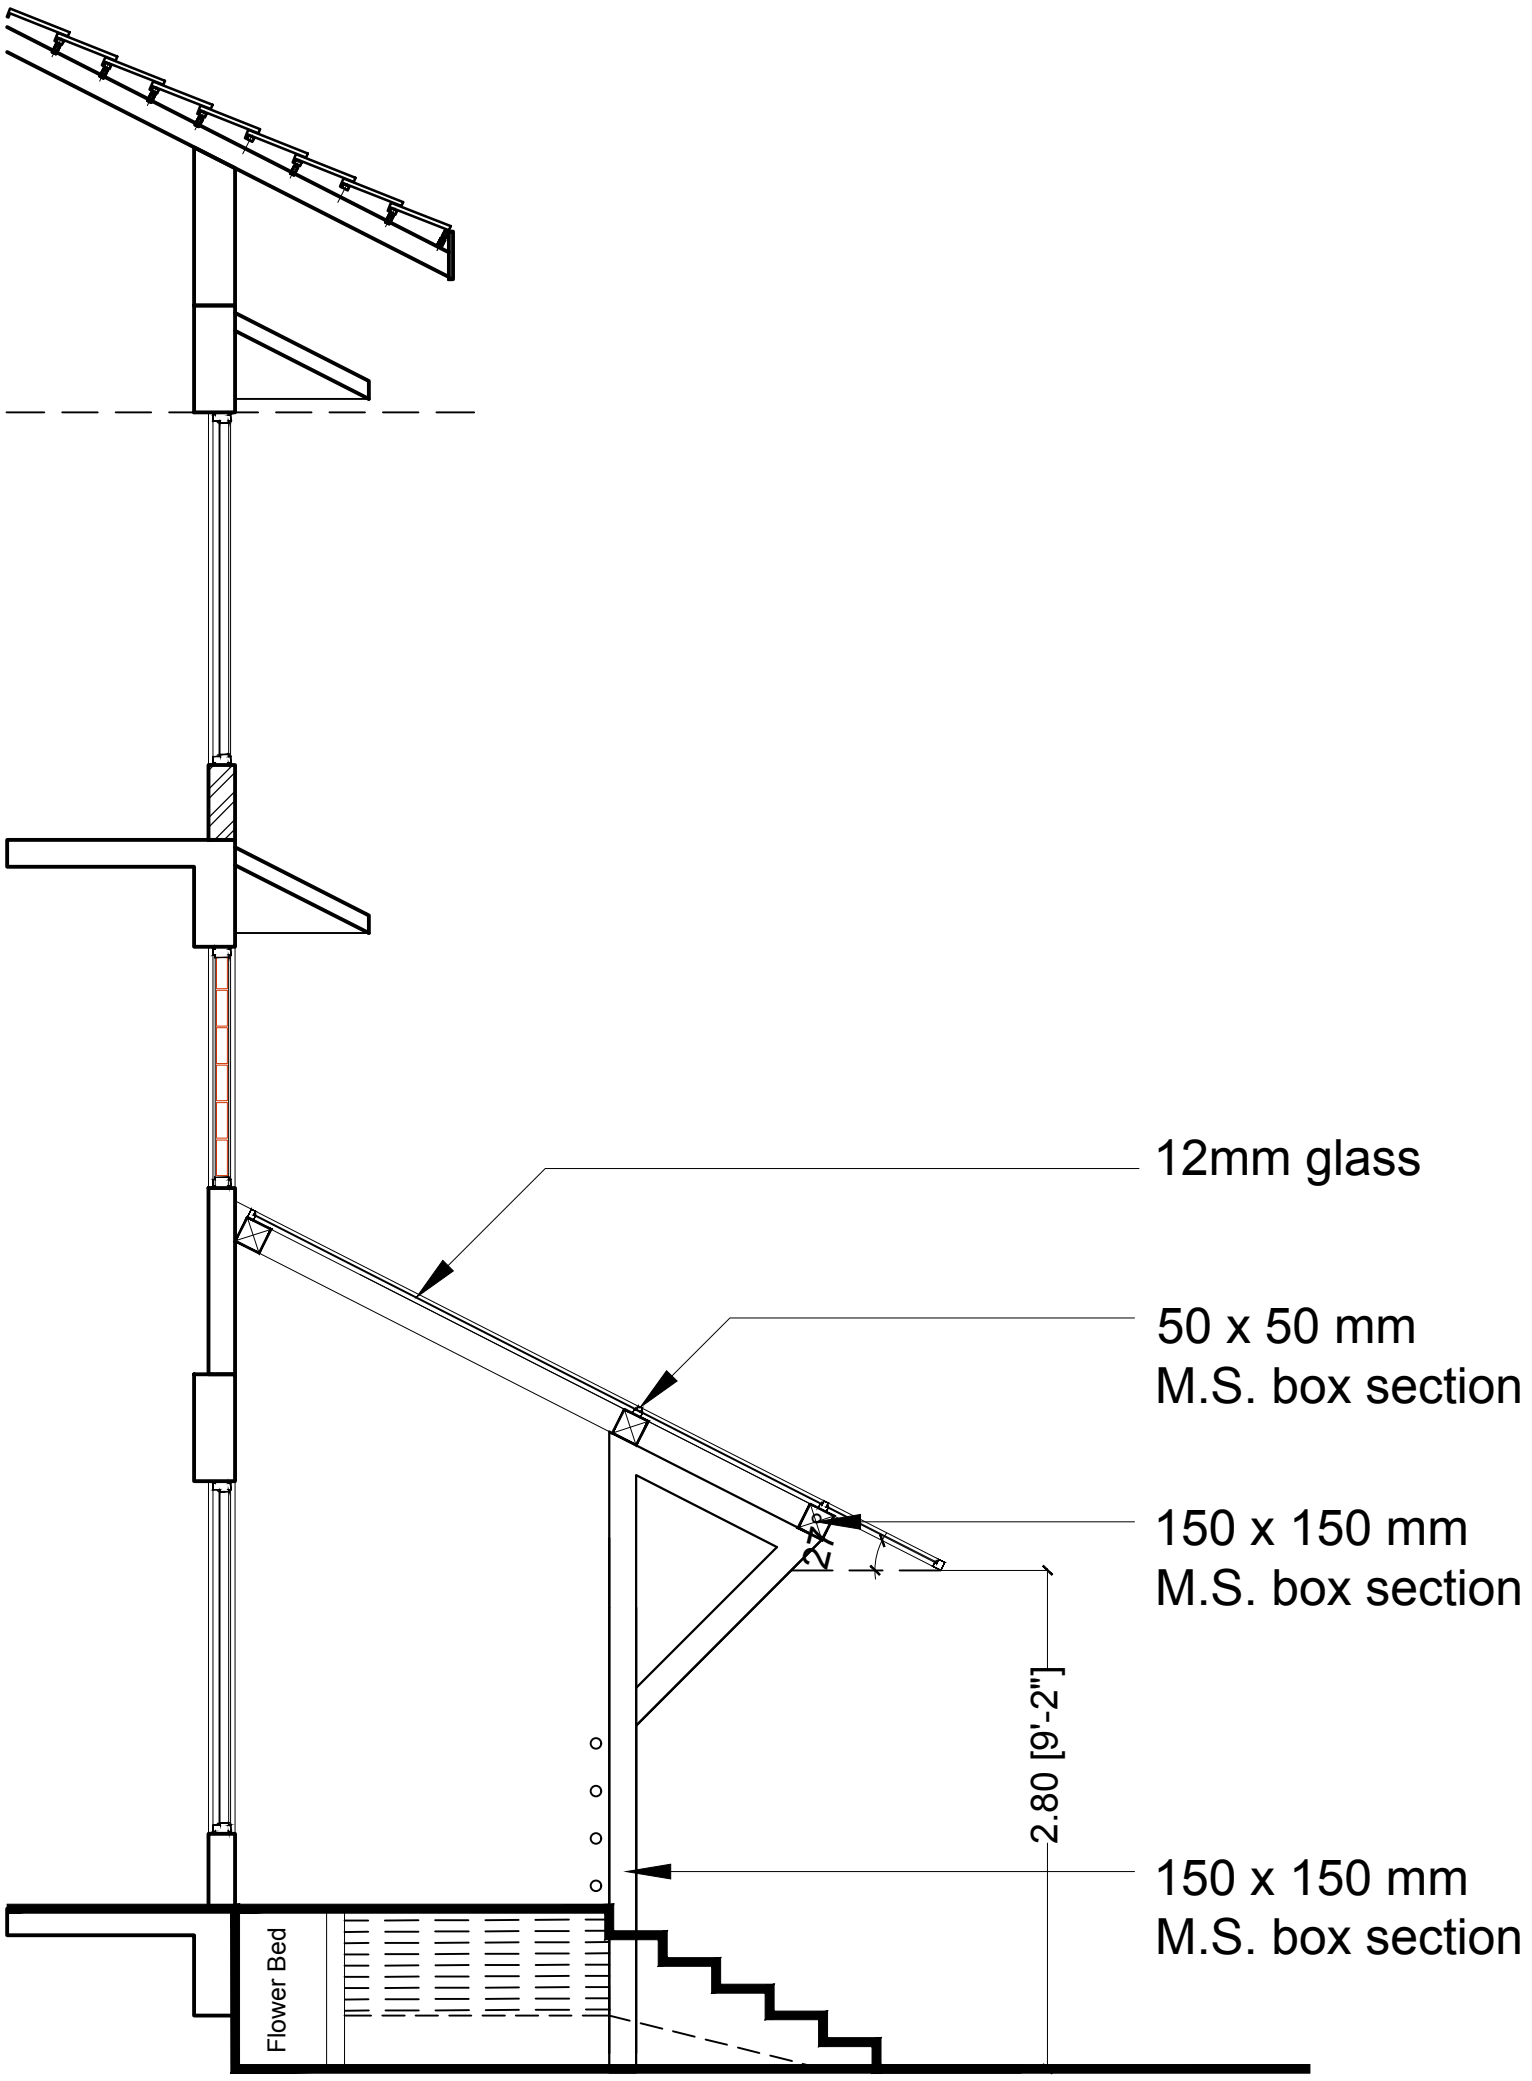


NOTES -
1.Do not scale the drawing.Work to figured dimensions only.
2.All dimensions are in millimetres(mm) unless noted otherwise & levels in metres(m).
3.This drawing to be read in conjunction with all relevant contract drawings and documentation.
4.This drawing is to be carefully checked by contractor against architects drawings,and any discrepancy reported to the engineer before construction commences.

FORESTA MULSHI

CLIENT - HIGHYIELD FORTUNE PVT. LTD

SCALE	DATE	DRAWN BY	JOB NO	STATUS
NTS	18.07.23	Ar. Akshat		G.F.C

Drawing Name - Suite Building entrance Canopy section
DRAWING NO -

ARCHITECT-

EPIC DESIGN PVT. LTD.