
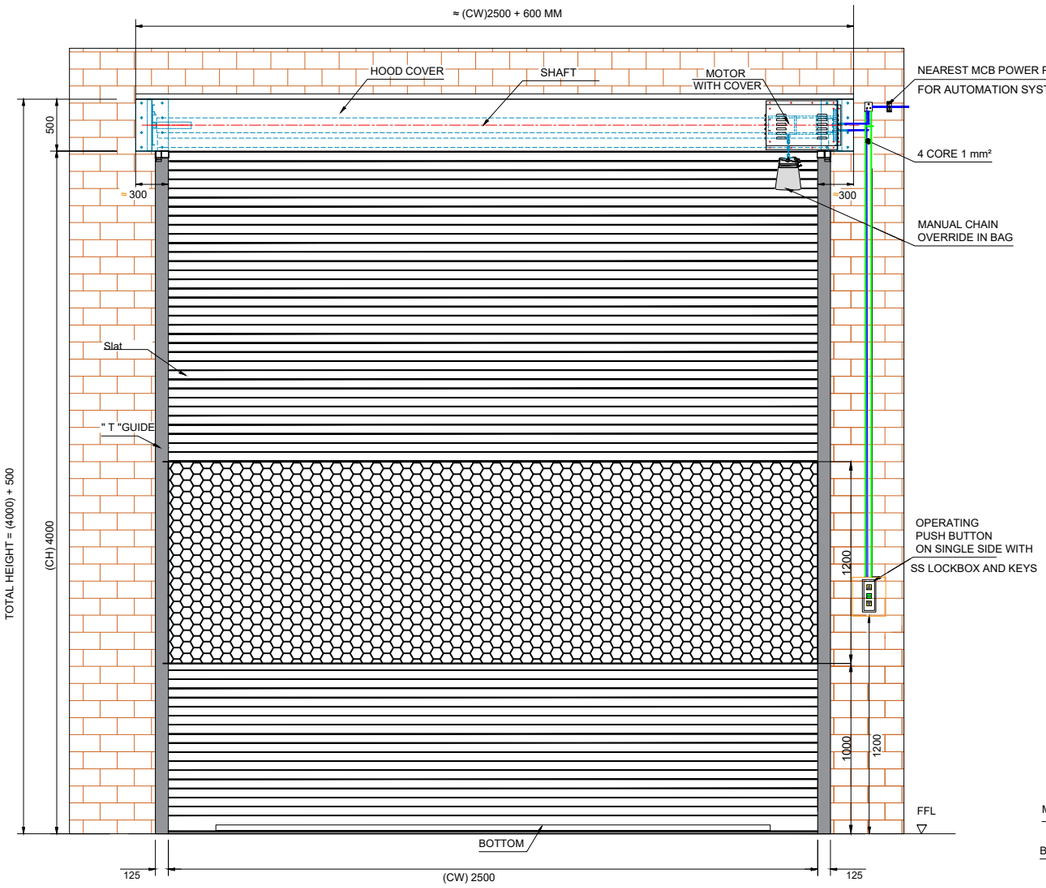



" T " TYPE GUIDE

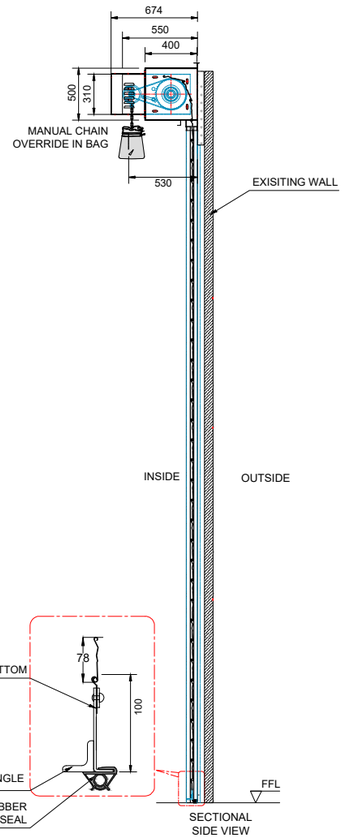


## TECHNICAL SPECIFICATION:-

| SR. | SPECIFICATION | DETAILS |
|---|---|---|
| 1. | DESCRIPTION & DRIVE | MOTORIZED ROLLING SHUTTER (INDIRECT DRIVE) SPROCKET CHAIN ARRANGEMENT. |
| 2. | LOCATION AREA | INSIDE |
| 3. | MOUNTING SURFACE | SIDE BRACKETS: OPTIONAL+ON CONCRETE/STEEL&SIDE |
| 4. | SLAT | CURVED 78 MM GI SHEET - 1.2 MM THICK |
| 5. | BOTTOM PROFILE | M.S. PLATE 100MMX2.5MM THICK WITH ANGULAR STIFFENER. |
| 6. | GUIDE PROFILE | M.S." T " SHAPE 65-150X3 MM THICK. |
| 7. | HOOD COVER & MOTOR COVER | MADE OF GI SHEET THICKNESS 0.9 MM. |
| 8. | COLOUR | TWO COATS OF EPOXY PAINT RAL9003 |
| 9. | PUSH BOTTON | 3 WAY PUSH BUTTON ON SINGLE SIDE |
| 10. | TYPE OF MOTOR | AC |
| 11. | POWER SUPPLY | 1Ø PHASE |
| 12. | RATED VOLTAGE FREQUENCY - (V/HZ) | 220/50 |
| 13. | RATED CURRENT - (A) | 3.3 |

## SHUTTER SIZES :-

| SR. | CLEAR WIDTH | CLEAR HEIGHT | QTY. |
|---|---|---|---|
| 01 | 2500 mm | 4000 mm | 01 |

## LOCATION :- ELECTRICAL SUB - STATION RS-01-2500X4000 MM

This drawing & designing is the property of NIHVA TECHNOLOGIES. Not to be sold or copied to any other concern.

TITLE :- MOTORISED ROLLING SHUTTER

NIHVA TECHNOLOGIES PVT. LTD. PUNE
Tel : 020 66304033
Email:- info@nihva.com
Website:- www.nihva.com

| | NAME | DATE |
|---|---|---|
| DRAWN | B.S. | 11/09/2025 |
| CHECK & APPROVAL | V.T. | 11/09/2025 |

CLIENT - SUROJ BUILDCON PVT LTD
PROJECT - MOTORISED ROLLING SHUTTER
FORMAT NO - NIHVA-DD-F-03
DWG. NO. : NIHVA/24-25/GB/1109001 | REV-00
SCALE: NTS | WT: | SHEET: 01 OF 01
ALL DIMENSION ARE IN mm
If any queries contact : design@nihva.com