


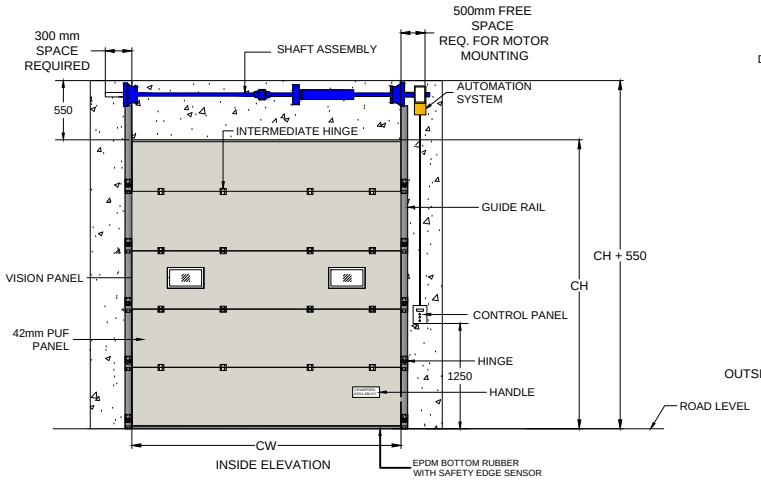


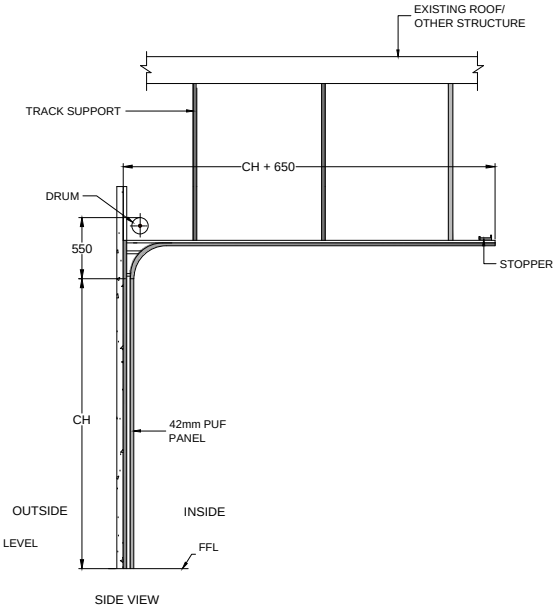

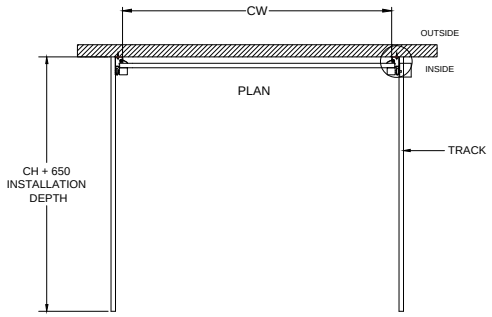

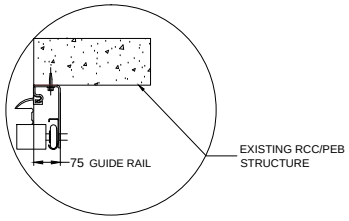

TRACK DETAILS

SR.NO	CLEAR WIDTH (CW)	CLEAR HEIGHT (CH)	QTY
5	2400	2800	7 NOS
4	2000	3000	1 NO
3	3000	4000	4 NOS
2	4000	4000	5 NOS
1	3500	3000	5 NOS

TOLERANCE - ±10mm

This drawing & design is the property of NIHVA TECHNOLOGIES. Not to be sold or copied to any other concern.

TITLE

SECTIONAL DOOR (SL)

NIHVA TECHNOLOGIES PVT. LTD.
NIHVA TECHNOLOGIES PVT. LTD. PUNE
Tel : 020 66304033
Email:- info@nihva.com
Website:- www.nihva.com

	NAME	SIGN	DATE
DRAWN	P.V.A		23.08.2019
CHECK	V.M.T		23.08.2019
APPRD.			

CLIENT - MHD LOGISTICS

PROJECT -GOVERNMENT POULTRY FARM

SITE LOCATION - OMAN

If any queries contact : design@nihva.com

DWG. NO. : NIHVA/19-20/0082 REV- 0

ALL DIMENSION ARE IN mm

SCALE: NTS WT: SHEET: 01 OF 01