


GA DRAWING

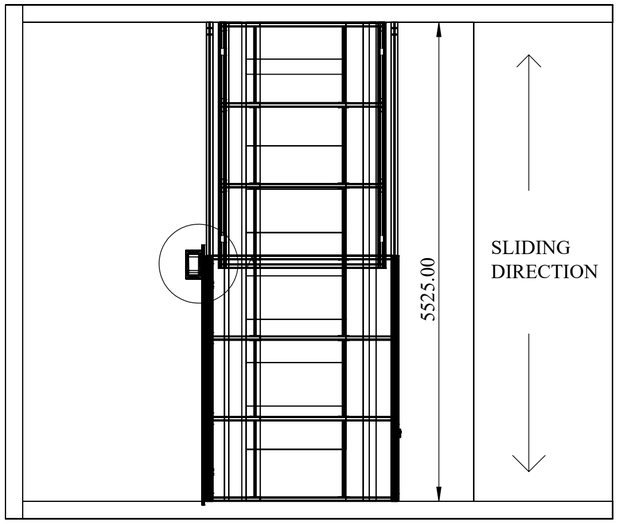


T.V

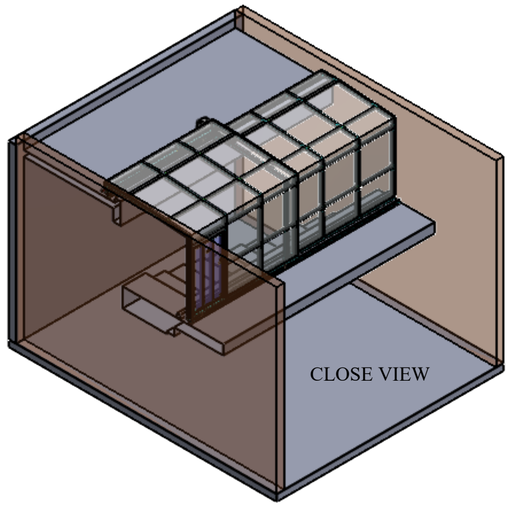

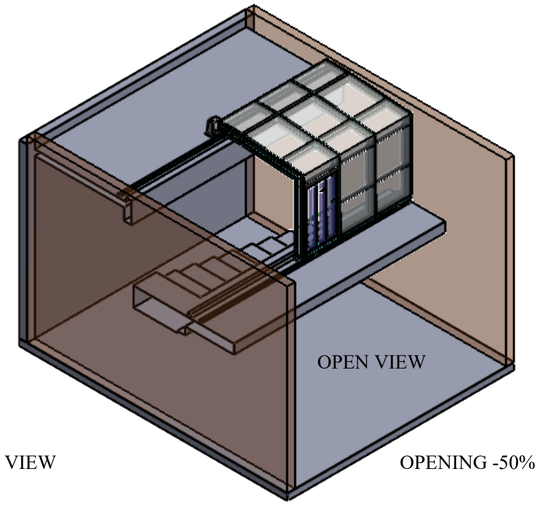


ISO VIEW


OPENING -50%

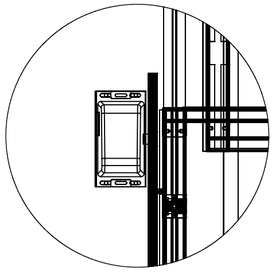


DETAIL A
SCALE 1 : 15

MOTOR
MOUNTING

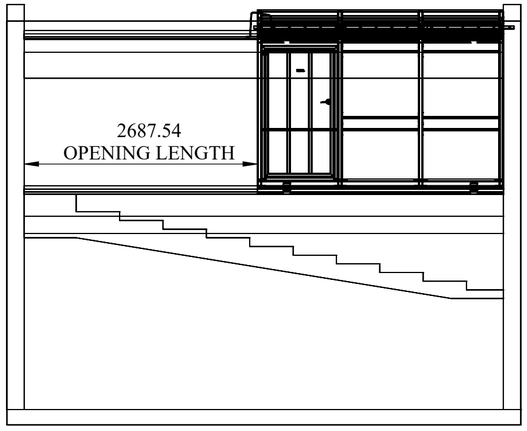


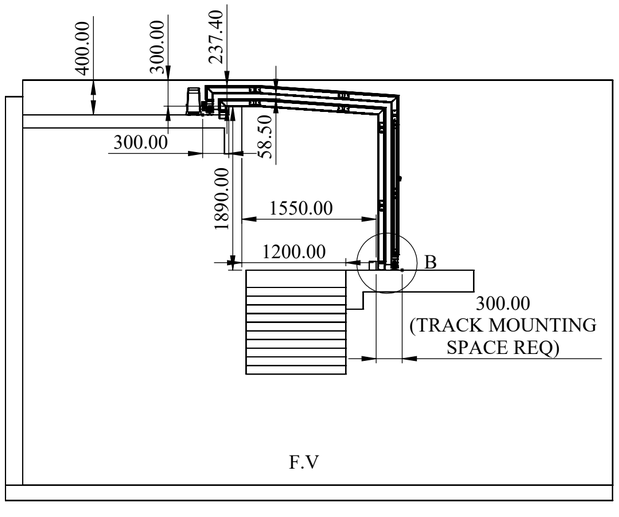

F.V

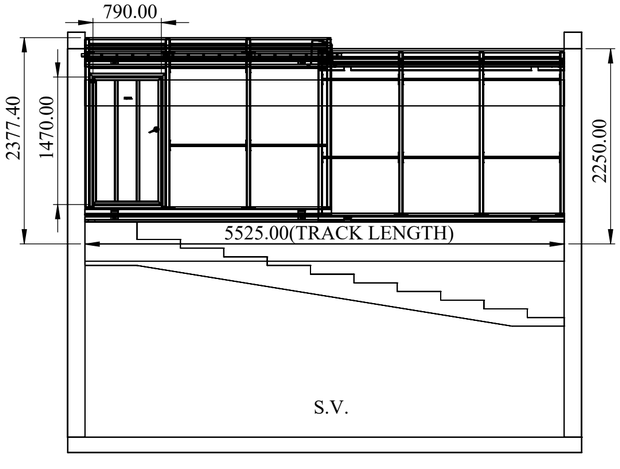

S.V.

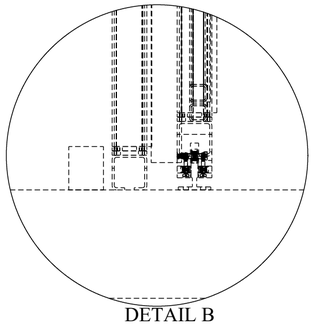

DETAIL B
SCALE 1 : 10

TRACK
MOUNTING

REV DESCRIPTION	DATE	REV NO
	10-07-2026	REV 00
1.		

NOTE :

THIS DRAWING IS FOR CLIENT APPROVAL
BASE STRUCTURE IN CLIENT SCOPE.

SPECIAL INSTRUCTION'S :

This drawing & design is the property of NIHVA TECHONOLOGIES PVT. LTD. Not to be sold or copied to any other concern

TITLE - BALCONY ENCLSOURE

DWG NO - NTPL-000-PM

NIHVA TECHNOLOGIES PVT.LTD.PUNE
Website - www.nihva.com

	NAME	SIGNATURE	DATE
DRAWN	V.W.		09-07-2026
CHK'D	S.P.		10-07-2026
APPV'D	V.T.		10-07-2026

PRODUCT - RETRACTABLE ROOF
CLIENT NAME - LODHA GROUP.
SITE LOCATION -
MATRIAL -
QTY - 1
If any queries contact - info@nihva.com
PROJECTION METHOD:
SCALE :
ALL DIMENSION ARE IN mm
A2
SHEET 1 OF 1