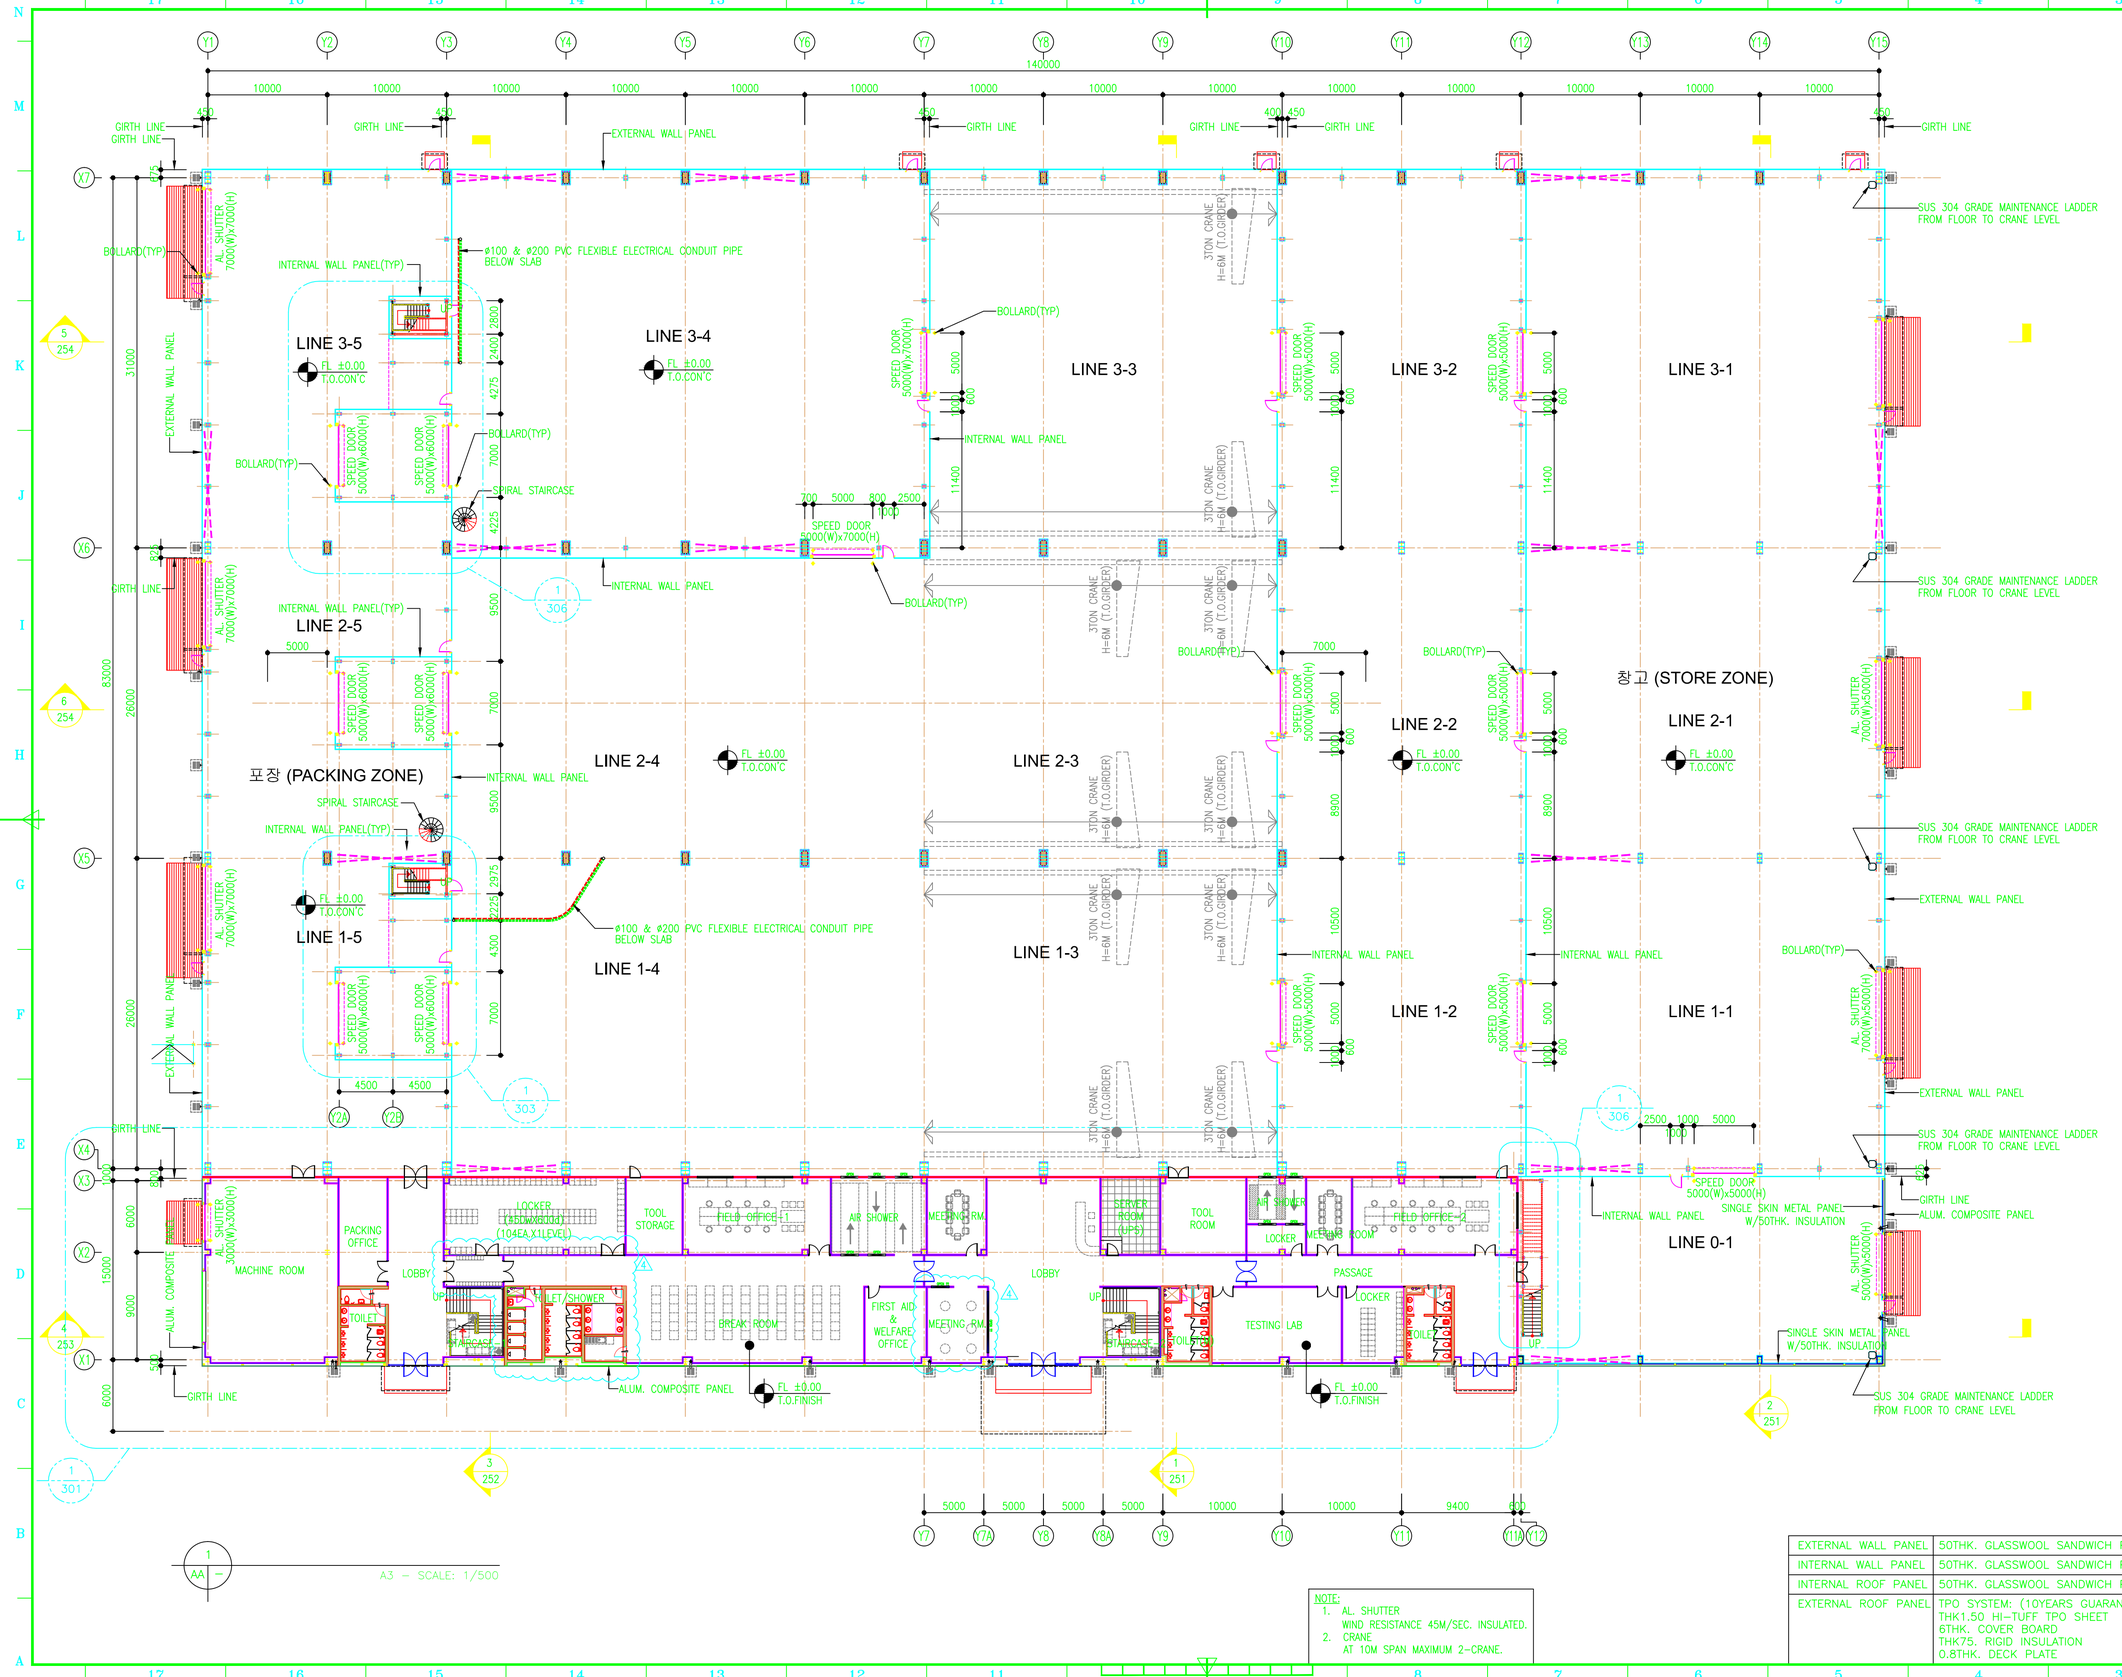


A3 — SCALE: 1/500

NOTE:
1. AL. SHUTTER WIND RESISTANCE 45M/SEC. INSULATED.
2. CRANE AT 10M SPAN MAXIMUM 2-CRANE.

EXTERNAL WALL PANEL	50THK. GLASSWOOL SANDWICH PANEL
INTERNAL WALL PANEL	50THK. GLASSWOOL SANDWICH PANEL
INTERNAL ROOF PANEL	50THK. GLASSWOOL SANDWICH PANEL
EXTERNAL ROOF PANEL	TPO SYSTEM: (10YEARS GUARANTEE) THK1.50 HI-TUFF TPO SHEET 6THK. COVER BOARD THK75. RIGID INSULATION 0.8THK. DECK PLATE

N

KEY PLAN

OFFICE LAYOUT REVISED AS PER CLIENT'S REQUIREMENT

REQUEST FOR REFERENCE ONLY

REV.	CONTENTS	NAME	DATE
3	OFFICE LAYOUT REVISED AS PER CLIENT'S REQUIREMENT	ANBU	08.DEC.2015
2	ISSUED FOR CONSTRUCTION	ANBU	16.OCT.2015
1	ISSUED FOR TENDER	ANBU	05.AUG.2015
0	FOR CLIENT CONFIRMATION AND ROUGH ESTIMATION DRAWING	ANBU	18.JUL.2015

CLIENT
HYOSUNG T&D
HYOSUNG CORPORATION INDIA PVT. LTD.

ARCHITECTS & ENGINEERS
HTI ENGINEERING PVT. LTD.
91.44.2252.3743 www.mapgroup.co.kr

PROJECT TITLE
HYOSUNG PUNE PLANT

DRAWING TITLE
GROUND FLOOR PLAN

SCALE	DRAWN BY	DESIGNED BY	CHECKED BY	APPROVED BY
A3:1/500 A1:1/250	ANBU	H.G.KIM	–	–
DATE	20.MAY.2015	20.MAY.2015	–	–

DRAWING NO.: HY-PU-FAC-AA-101 REV.: 3