

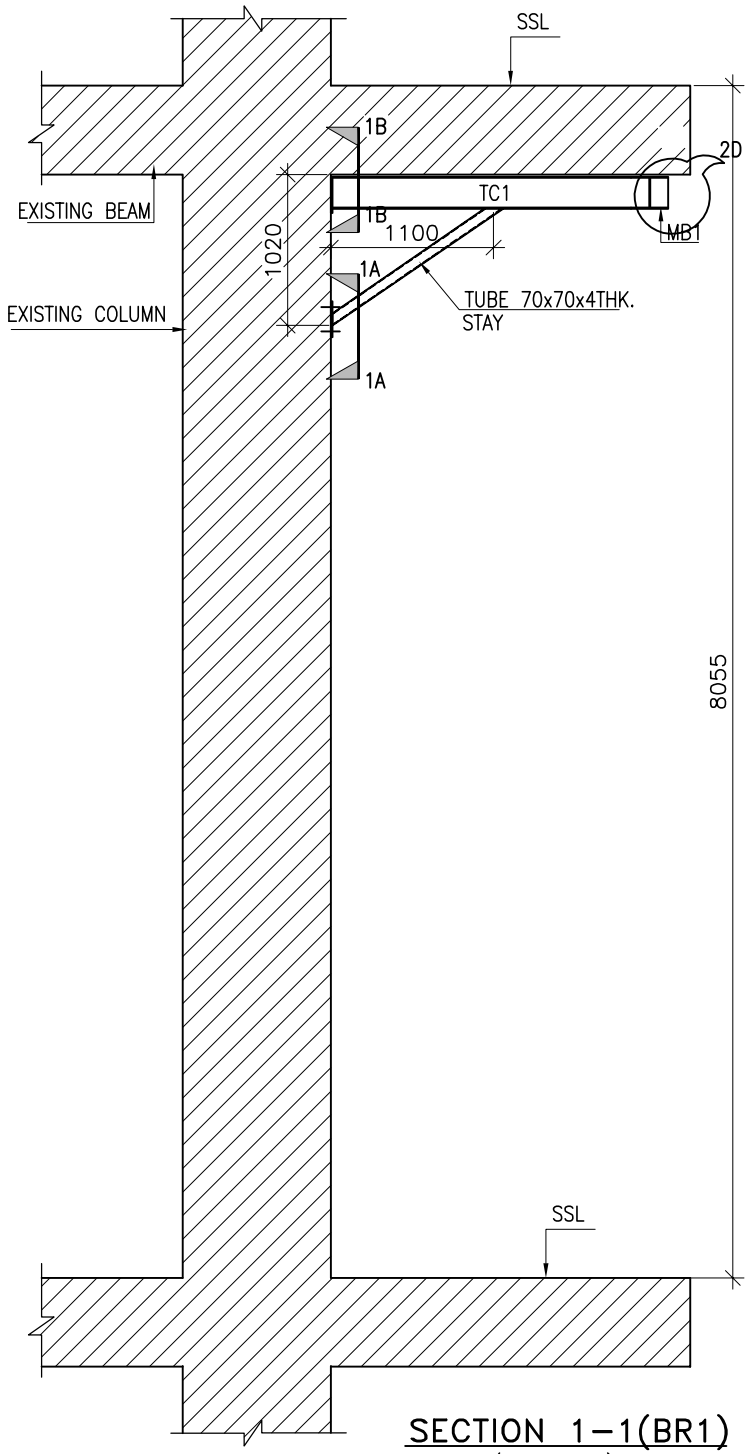



SECTION 1–1(BR1)
(SCALE 1:50)

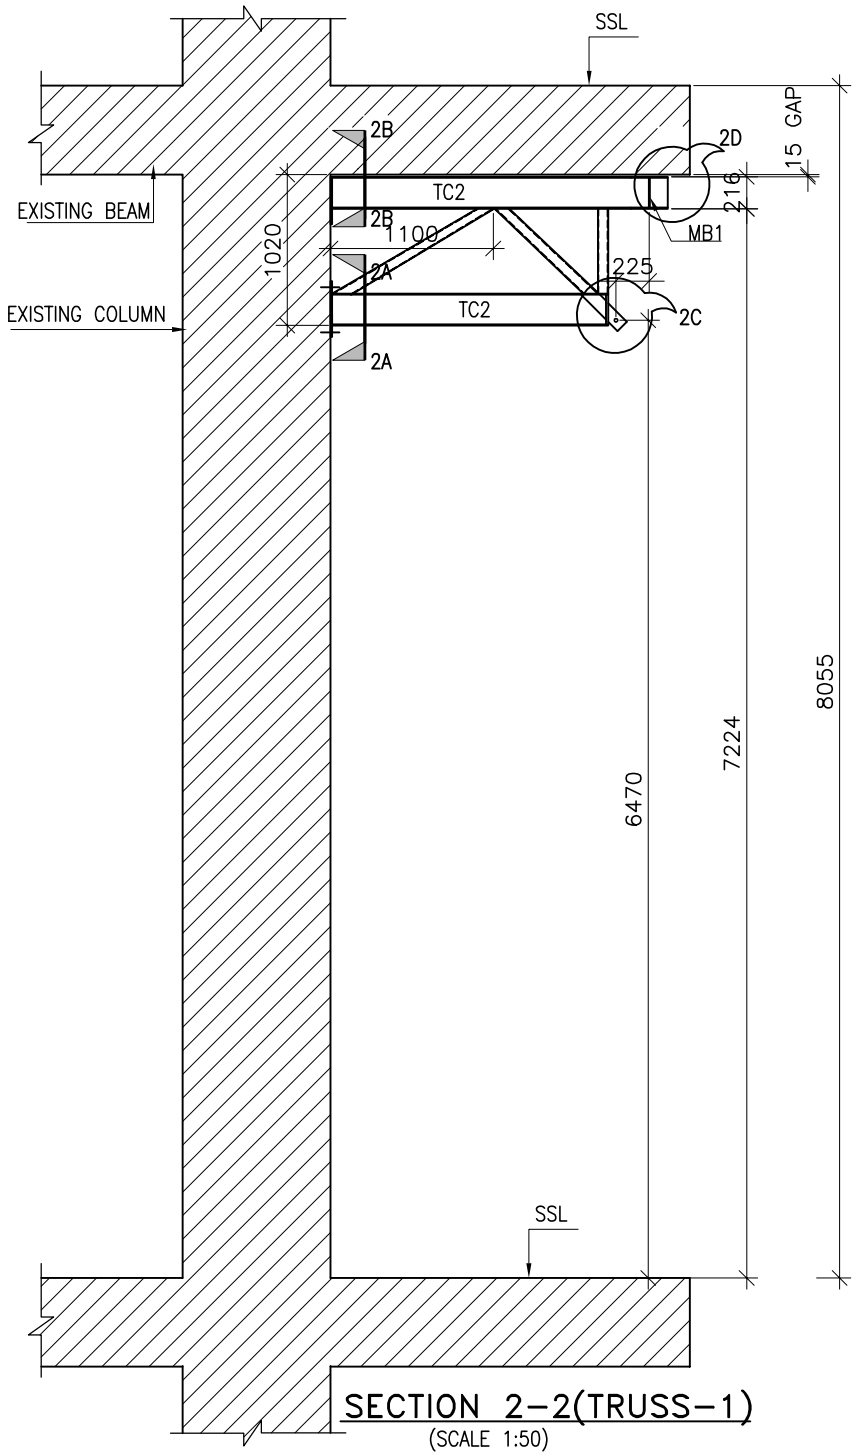


SECTION 2–2(TRUSS–1)
(SCALE 1:50)

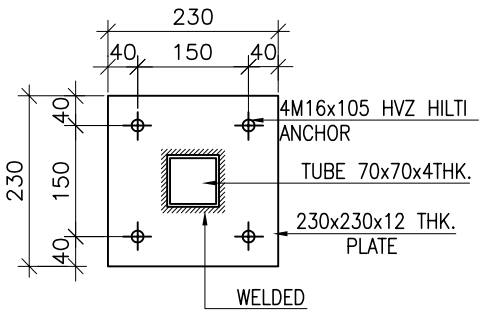


VIEW 1A–1A
(SCALE 1:10)

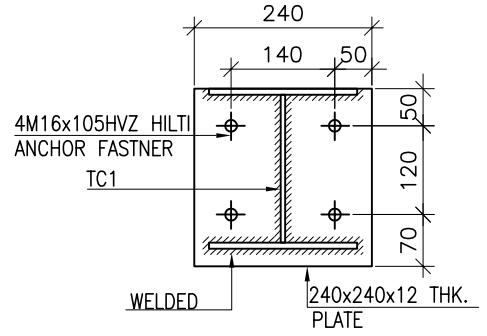


VIEW 1B–1B
(SCALE 1:10)

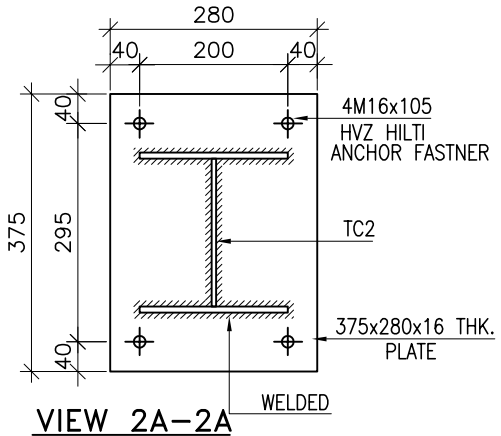


VIEW 2A–2A
(SCALE 1:10)

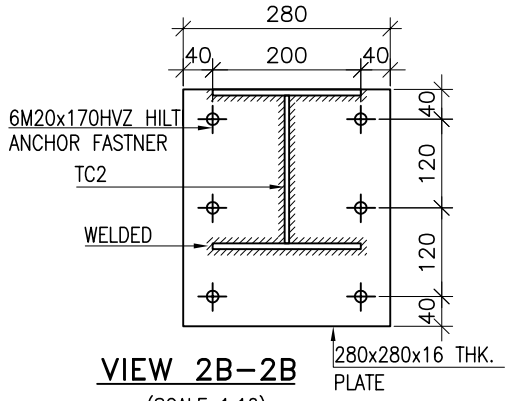

VIEW 2B–2B
(SCALE 1:10)

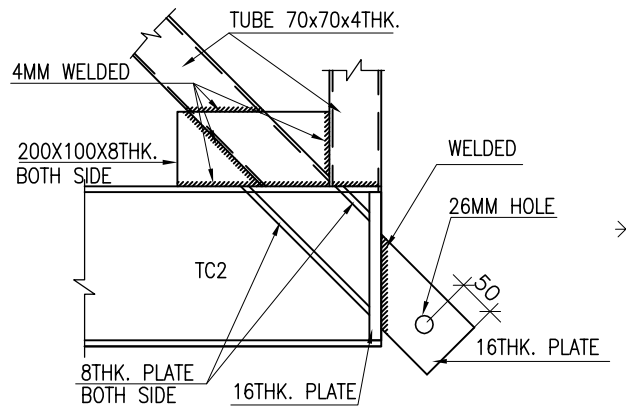

DETAILS AT '2C'
(SCALE 1:10)

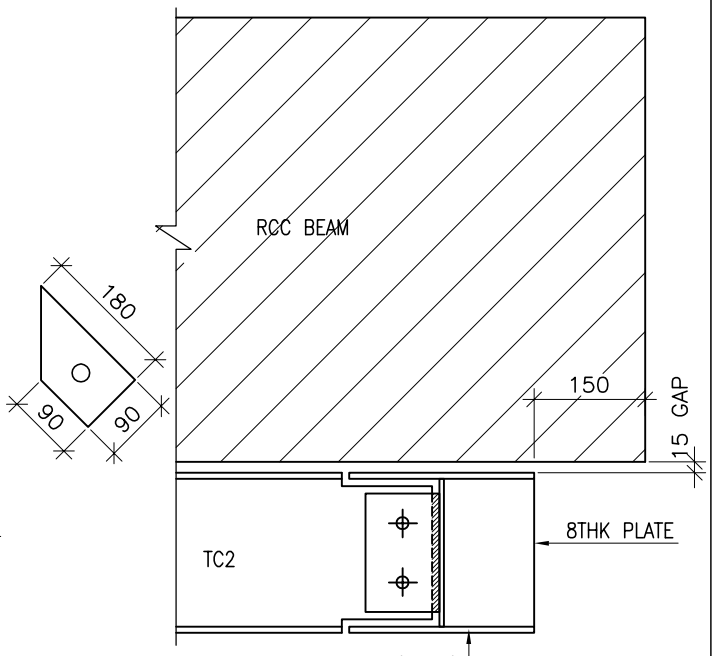

DETAILS AT '2D'
(SCALE 1:10)

No	Description	By	Chk	Date
RO	GOOD FOR CONSTRUCTION	R.P.	R.M	19-11-2016

Drawn by : R.P.
Checked by : R.M
Approved by : R.M.
Date : 19-11-2016

Title : PART PLAN AT 3RD& 5TH FLOOR
Project : PROPOSED COMMERZONE, FOR K. RAHEJA CORP, AT YERWADA, PUNE.
Architect :
Client : Nvidia Graphics Private Limited

Structural consultant:
Design Werkz Engineering Pvt.LTD
Artha Vishwa 3rd Floor Lane 5,
Koregaon Park, Pune 411001.
Tel : +91-20-32900573 / 26052921
Fax : +91-20-66201389 web:www.designwerkzeng.com

Job no: -
Dwg. No: ST-101
Drg. Size: A3
Sheet No: 2/3
Rev. No: R0
Scale: AS SHOWN
Drawing status: GOOD FOR CONSTRUCTION

This drawing is the property of Design Werkz Engineering Pvt.LTD and shall not be reproduced or used without written permission.