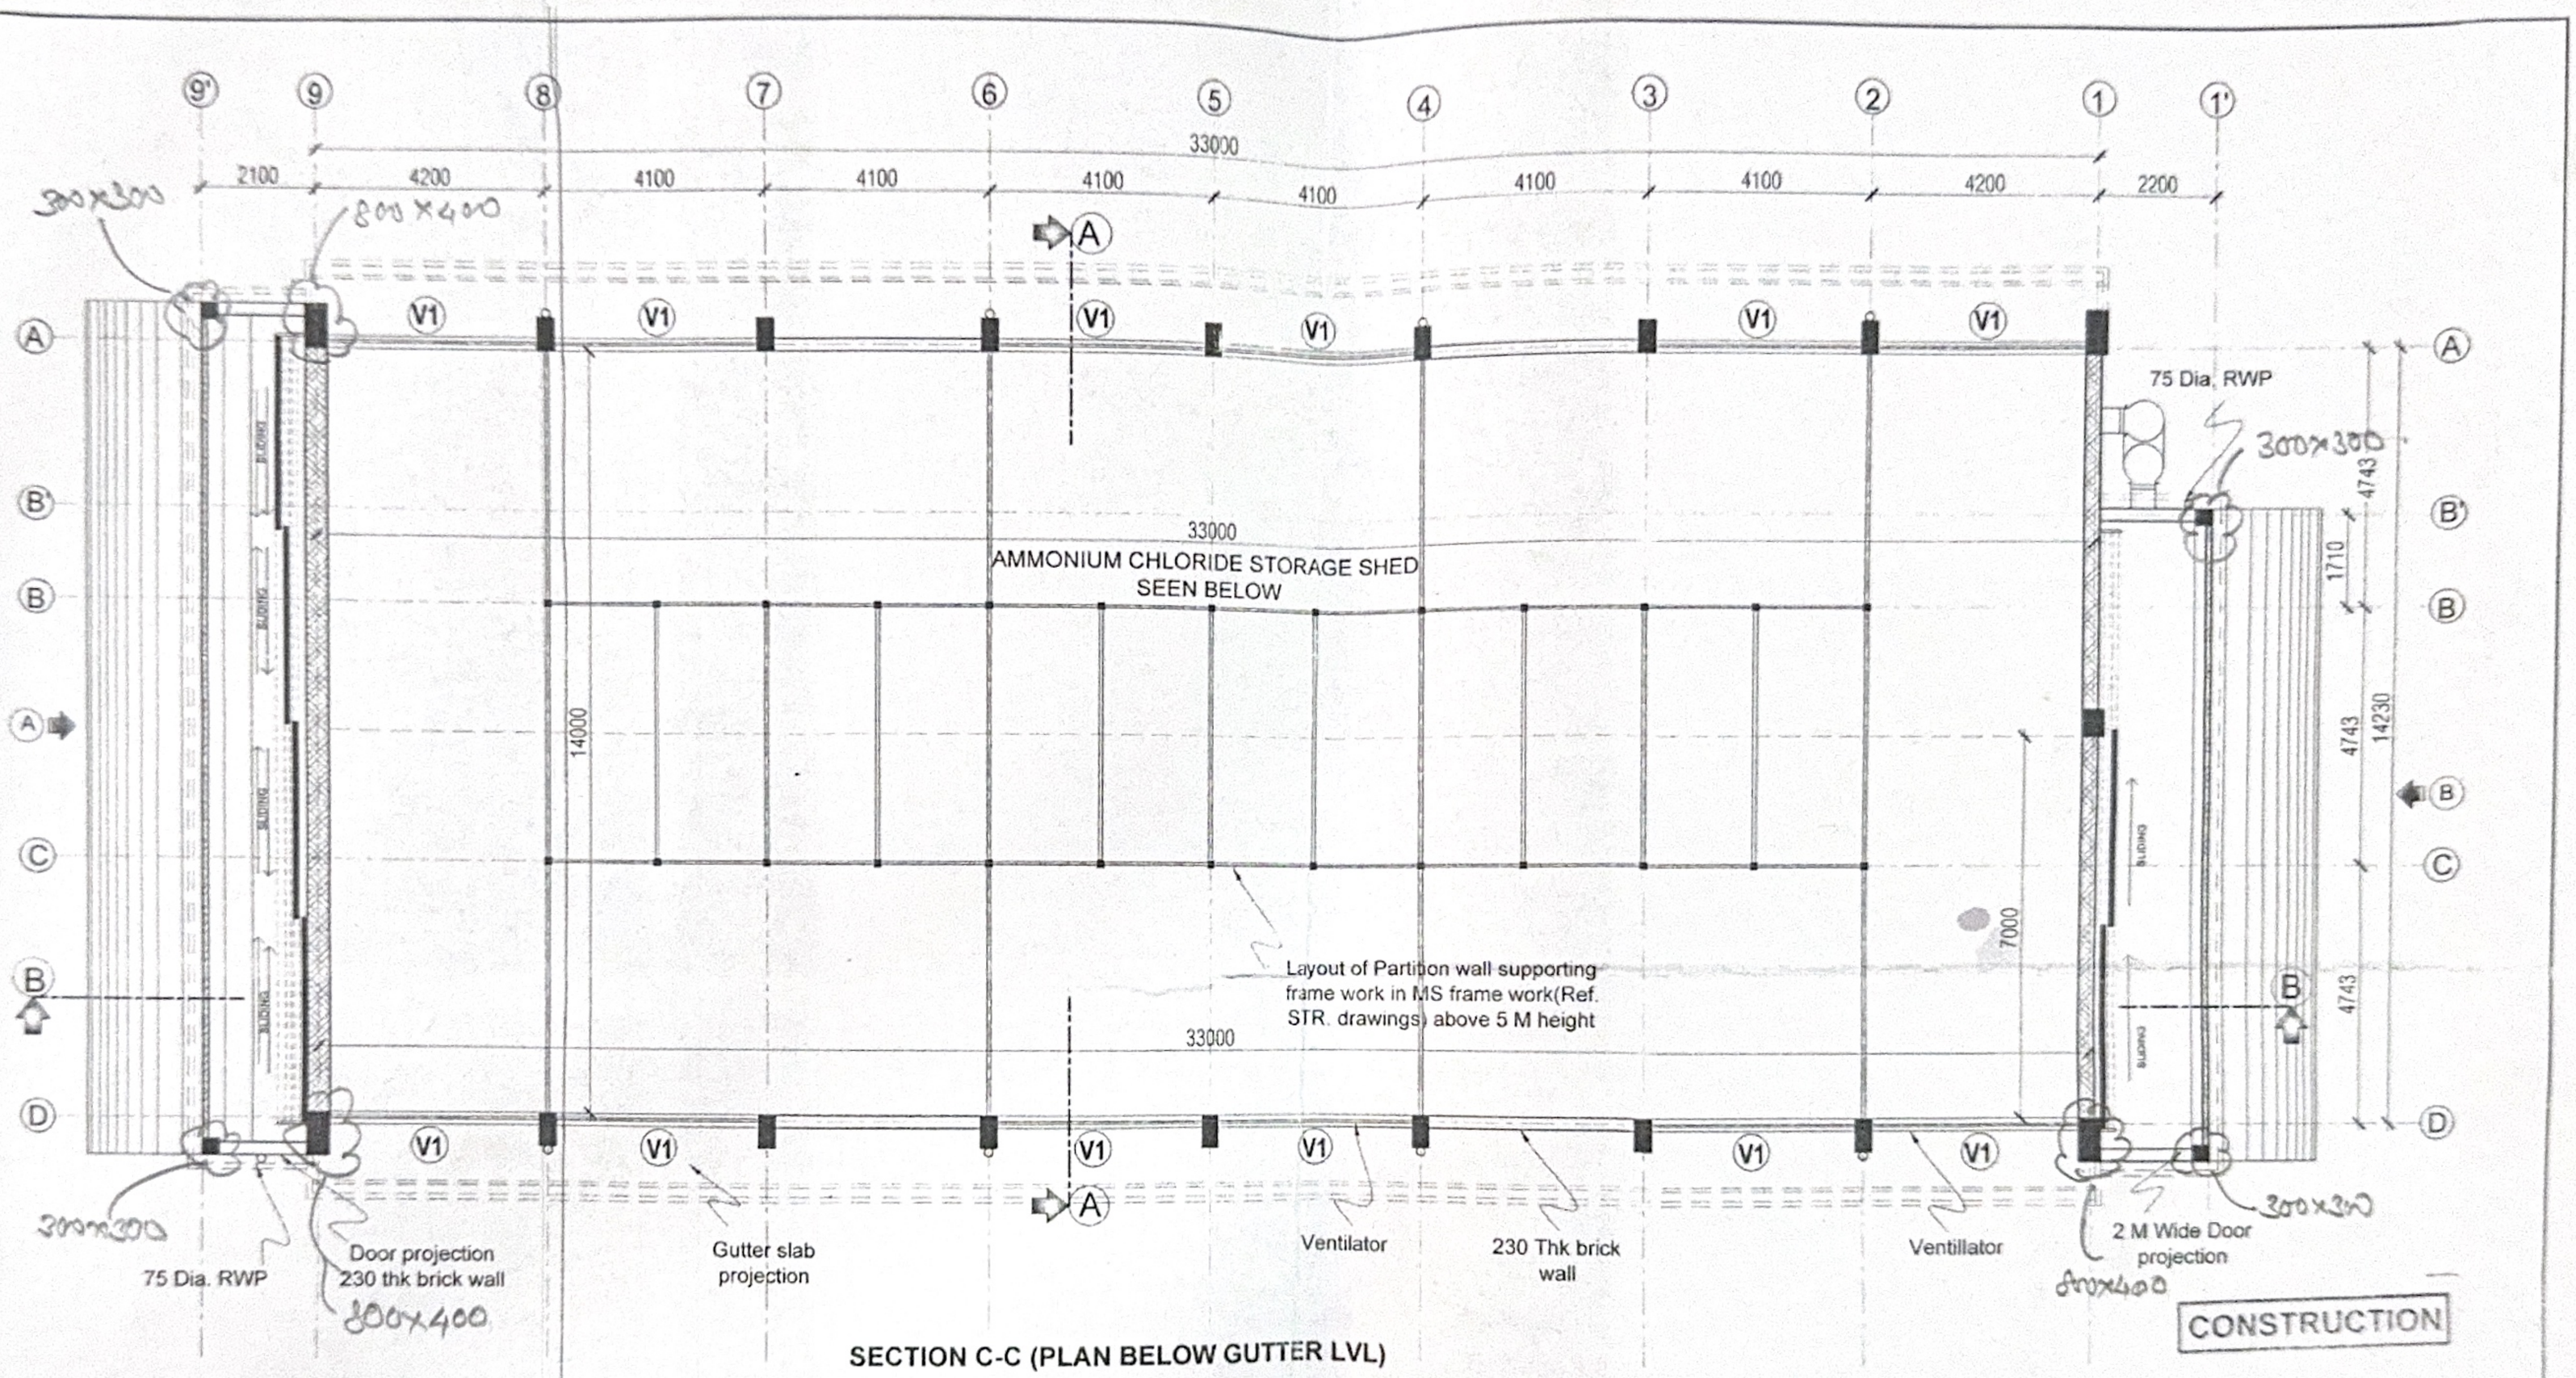


SECTION C-C (PLAN BELOW GUTTER LVL)

NOTE:1

1. ALL DIMENSIONS ARE IN MILLIMETERS UNLESS OTHERWISE SPECIFIED.
2. DRAWING SHOULD NOT BE SCALED.ONLY WRITTEN DIMENSION SHOULD BE FOLLOWED.
3. ALL DIMENSIONS ARE TO BE VERIFIED AT SITE.
4. ANY DISCREPANCY FOUND IN THE DRAWING SHALL BE BROUGHT TO THE NOTICE OF THE Dy HEAD PDC/CMG
5. ANY DEVIATIONS FROM THE DRAWING OR SPECIFICATIONS MENTIONED IN THE DRG.NEED TO BE GOT APPROVED BY THE Dy HEAD, PDC, CMG
6. THIS DRAWING IS TO BE READ IN CONJUCTION WITH ALL OTHER ARCH DRGS.
7. THIS DRAWING SUPERCEDES DRG. NO.

AREA DETAILS

PLINTH AREA

GROUND FLOOR (6.00m Ht.)	-	484.50 Sqm.
DOOR PROJECTION(3.00 m ht)	-	54.20sqm
TOTAL	-	538.70sqm

CARPET AREA

GROUND FLOOR = 453. 00 SQM

REVISION DATE	NO.	DESCRIPTION	CHECKED	APPROVED

ALL DIMENSIONS ARE IN MM

CMG VSSC

SCALE:- NTS | DATE: 20.03.2024

APPROVED BY	RECOMMENDED BY	DRG. NO.
ALAGARSAMY A, GROUP DIRECTOR, CMG	ANJU S DEV, Dy HEAD, PDC, CMG	VSSC/CMG/PDC/1-1/23-WD-04
CHECKED BY	DRAWN BY	Working Drawings
RAJENDRA KUMAR M, SR(QTY),PDC, CMG	BINI BHADRAN, DMAN - II, PDC, CMG	ARCHITECTURE DRAWING

DRAWING TITLE:
SECTION- CC (PLAN BELOW GUTTER LVL)

NAME OF WORK:
PROPOSED AMMONIUM CHLORIDE STORAGE SHED AT APEP