

Abbrevation's:
WOW-Wall Opening Width
WOH-Wall Opening Height
UC-Under Cut
FFL-Finished Floor Level

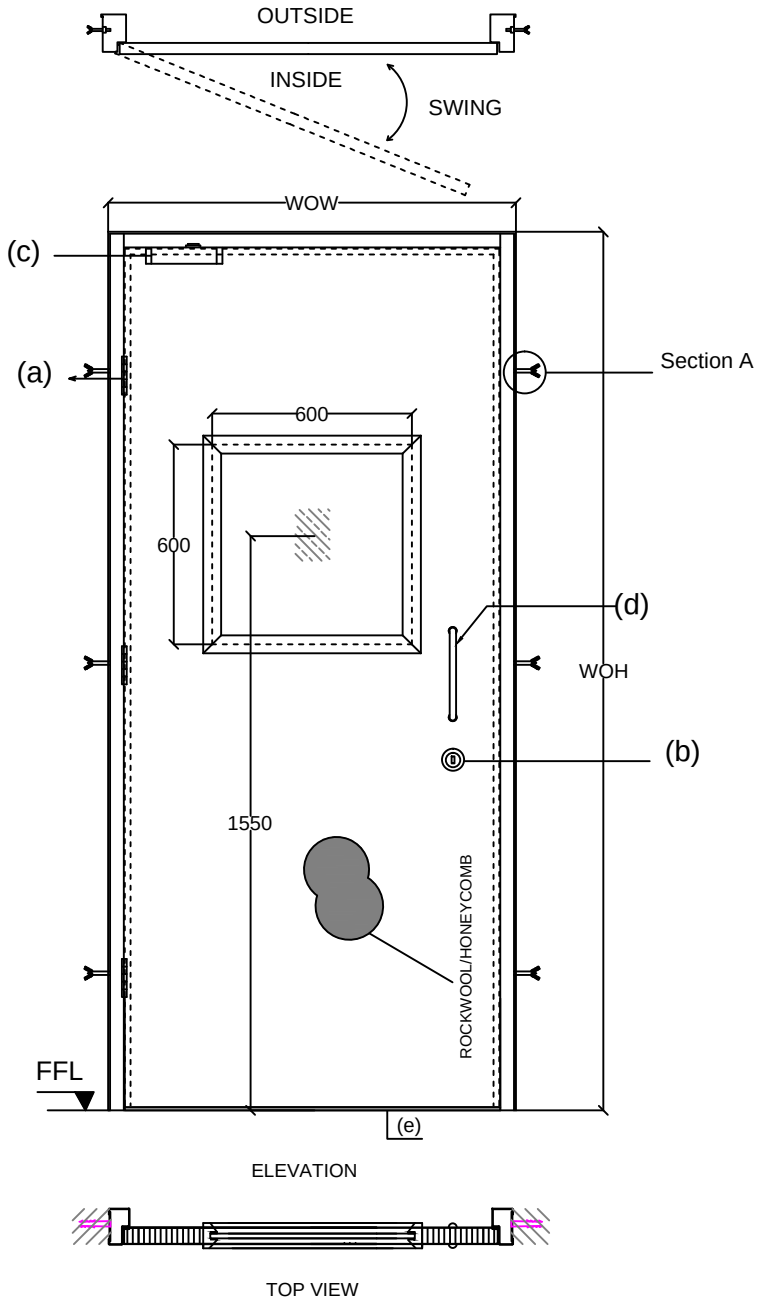

ELEVATION

TOP VIEW

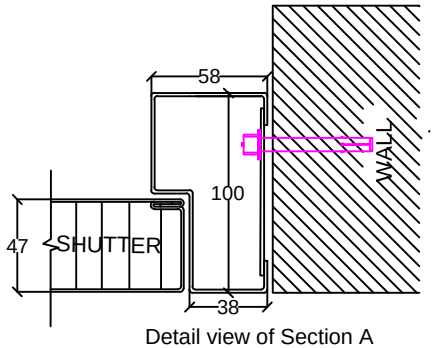

Detail view of Section A

ASSESORIES DETALES

(a) HINGES: SS Ball bearing butt hinges size 100x75x3mm

(b) LOCK : Mortise Dead lock,Cylinder(one side key & other side thumb turn) with Escutcheon

(c) DOOR CLOSER B4W

(d) HANDLE : D Handle

(e) Concealed Door Bottom

Shutter thickness : 47 mm
Frame Sheet thick : 1.20mm
Shutter sheet thick : 0.80mm
Fixing : On Soliid Brick plasterd wall with Anchors

NOTE:- *All Dimensions are in mm.
*Tolerance:-All Linear Dimensions ±3mm,Others ±0.5mm.
*The Drawing Is For Location of Hardware only. Drawing Does Not Represent The Hardware For More Clarity, Please Go Through Hardware Broucher.

Steel door size						
WOW	WOH	TYPE 1	TYPE 2	TYPE 3	TYPE 4	QUANTITY
1200	2100					2

NOTE- CLIENT SHOULD SELECT DOOR TYPE FROM DOOR HANDLING SHEET.

This drawing & design is the property of NIHVA TECHNOLOGIES. Not be sold or copy to any other concern.

STEEL DOOR (SINGLE LEAF)

CLIENT APPROVAL

ALL DIMENSION ARE IN mm

	NAME	DATE	SIGN.
DRAWN	SURAJ	26/04/17	
CHECK	SAGAR P.	26/04/17	
REV.			
APPRD.			
MFG			

NIHVA TECHNOLOGIES PVT. LTD.
NIHVA TECHNOLOGIES PVT. LTD. PUNE
Tel : 020 66304033
Email:- info@nihva.com
Website:-www.nihva.com

CLIENT - TATA PROJECTS
PROJECT -
SITE - HYDERABAD
DWG. NO. - NIHVA/17-18/0027
SCALE: NTS | WT: | SHEET: 01 OF 01
If any queries contact : projects@nihva.com