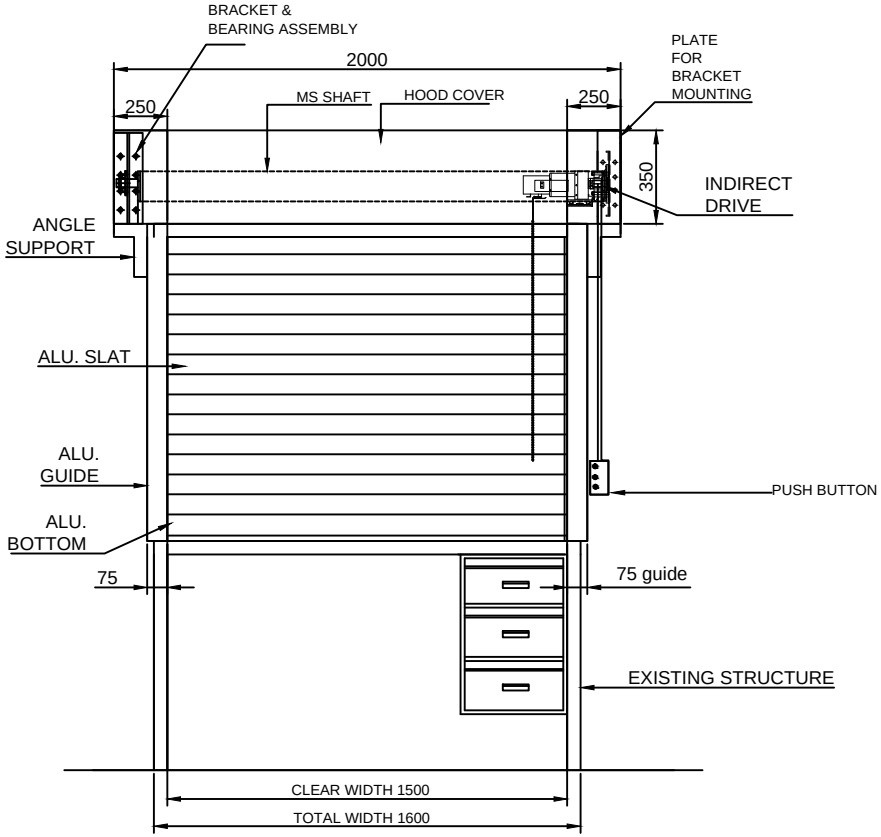

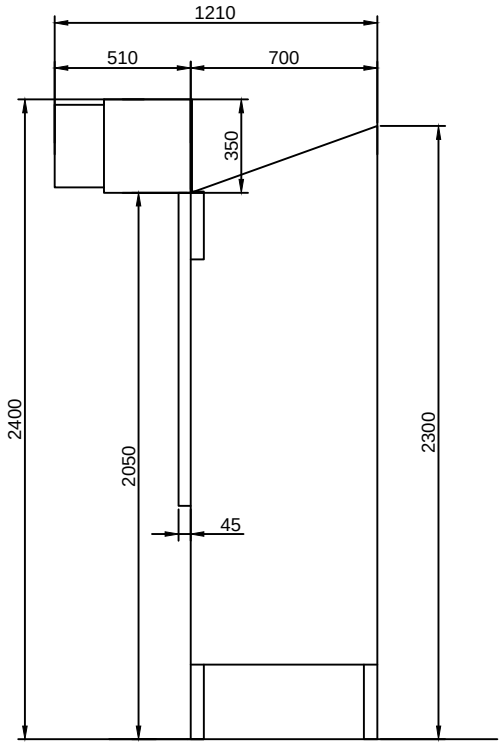

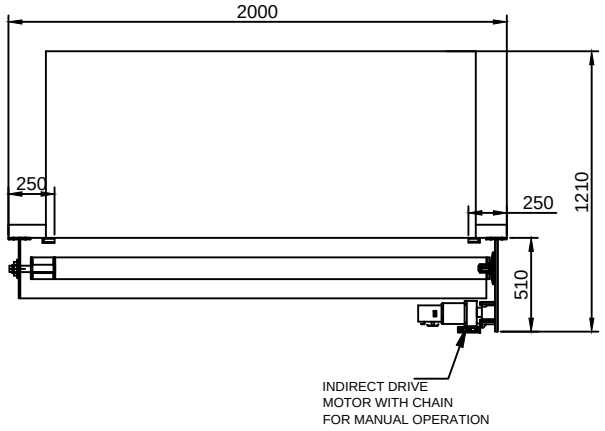

REV NO	DATE	DESCRIPTION
REV -0	26/10/17	INITIAL DRAWING
REV -1	13/11/17	DRAWING DRAWN AS PER ACTUAL FINAL DIM. OF SHUTTER

This drawing & design is the property of NIHVA TECHNOLOGIES. Not to be sold or copied to any other concern.

TITLE: ALUMINUM ROLLING SHUTTER

NIHVA TECHNOLOGIES PVT. LTD.
NIHVA TECHNOLOGIES PVT. LTD. PUNE
Tel : 020 66304033
Email:- info@nihva.com
Website:- www.nihva.com

	SIGN	DATE
DRAWN	OMKAR	26/10/17
CHECK	SHEKHAR	26/10/17
REV.		
APPROVAL	SHEKHAR	26/10/17

If any queries contact : design@nihva.com

ALL DIMENSION ARE IN mm

CLIENT - FERRERO INDIA PVT. LTD.

PROJECT -

SITE - BARAMATI

DWG. NO. : NIHVA/17-18/0250/R01 | REV-01

SCALE: NTS | WT: | SHEET: 01 OF 01