


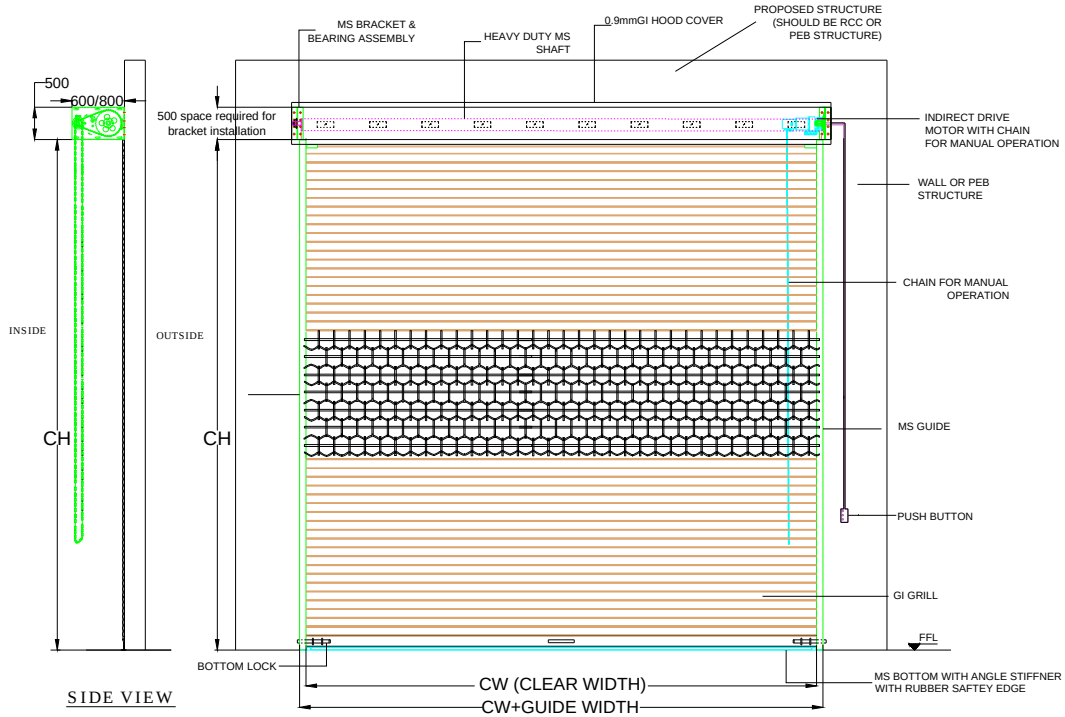


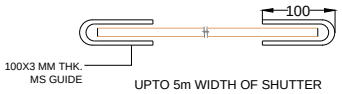


UPTO 5m WIDTH OF SHUTTER

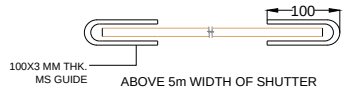


ABOVE 5m WIDTH OF SHUTTER

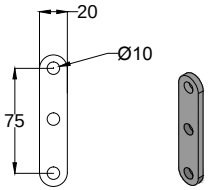

5 m m THK. LINK

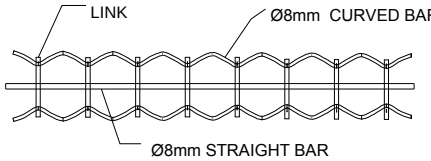

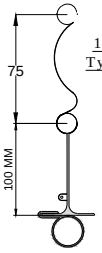

1 m m Thk.Curve Type MS Shutter lath AT TOP & BOTTOM

M.S. BOTTOM RAIL PROFILE 2.5MM THK WITH ANGLE STIFFNER & EPDM RUBBER

CLEAR WIDTH	CLEAR HEIGHT	QTY.
3000mm	3400mm	04 NOS
4500mm	3400mm	03 NOS
3000mm	3000mm	01 NOS

TOLERANCE - ±10mm

This drawing & design is the property of NIHVA TECHNOLOGIES. Not to be sold or copied to any other concern.

TITLE: MOTORISED ROLLING SHUTTER

	NAME	SIGN	DATE
DRAWN	SURAJ		17-08-2018
CHECK	PRADEEP		17-08-2018
APPRD.	R.D		17-08-2018

If any queries contact : design@nihva.com

ALL DIMENSION ARE IN mm

NIHVA TECHNOLOGIES PVT. LTD.

NIHVA TECHNOLOGIES PVT. LTD. PUNE
Tel : 020 66304033
Email:- info@nihva.com
Website:- www.nihva.com

CLIENT -DEVI CONSTRUCTION

PROJECT -

SITE LOCATION - PUNE.

DWG. NO. : NIHVA/18-19/0112 | REV- 0

SCALE: NTS | WT: | SHEET: 01 OF 01