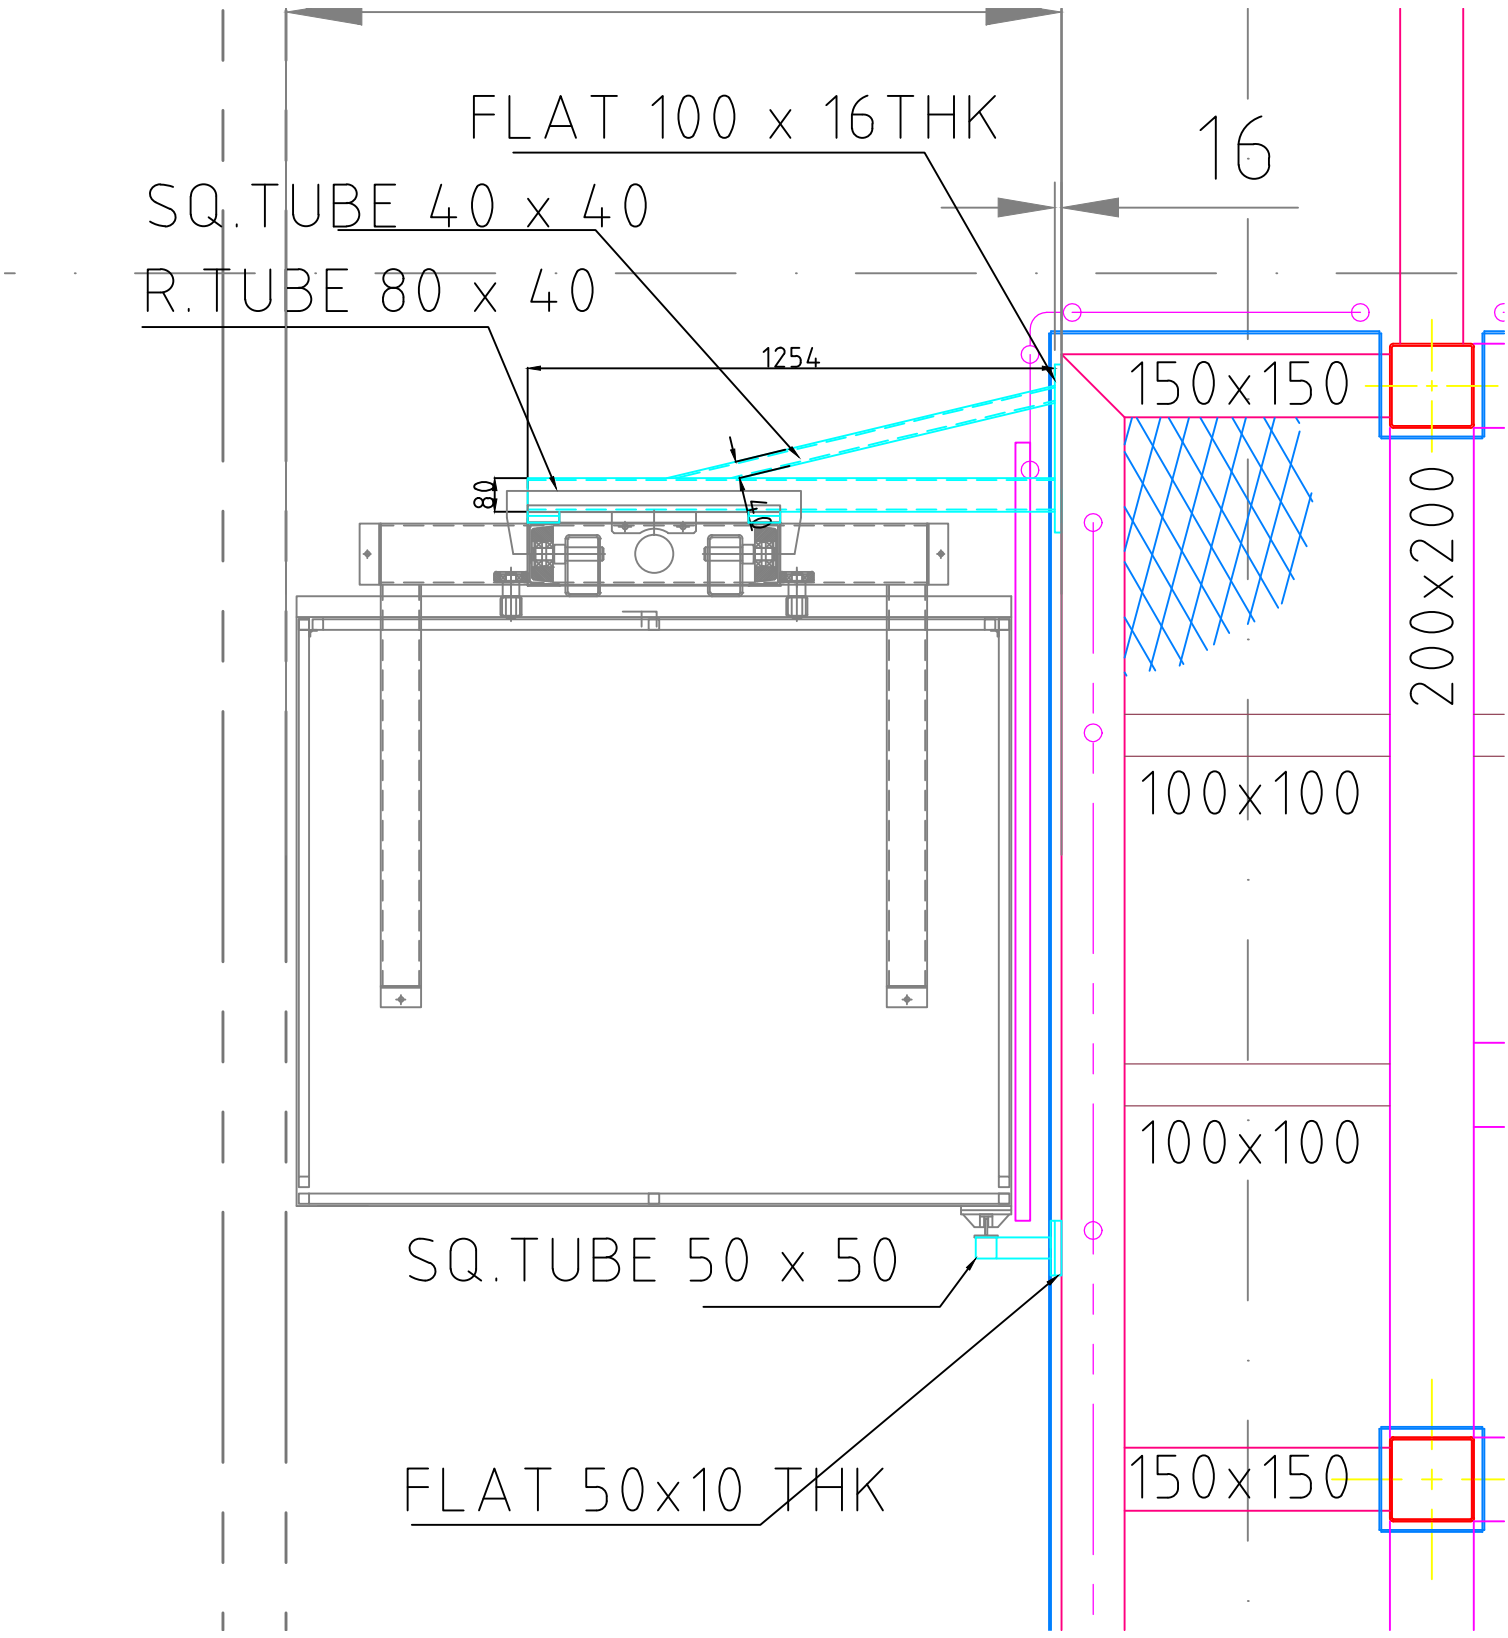
FLAT 100 x 16THK
16
SQ.TUBE 40 x 40
R.TUBE 80 x 40
1254
89
150x150
200x200
100x100
100x100
SQ.TUBE 50 x 50
FLAT 50x10 THK
150x150