
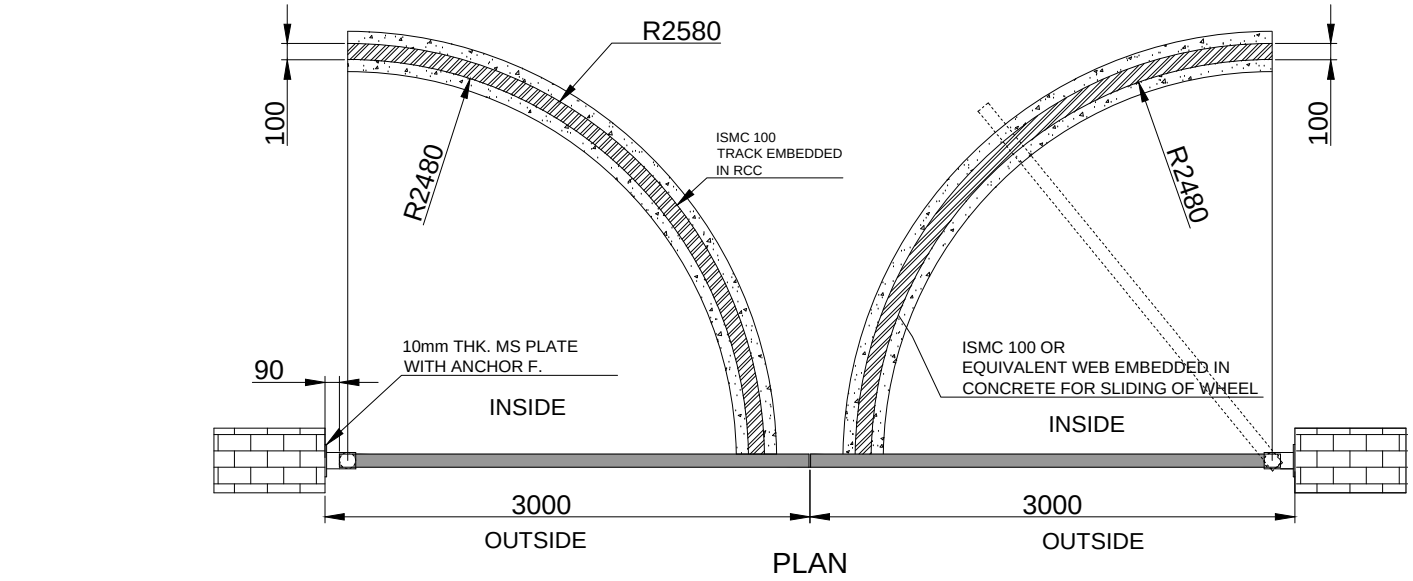


PLAN

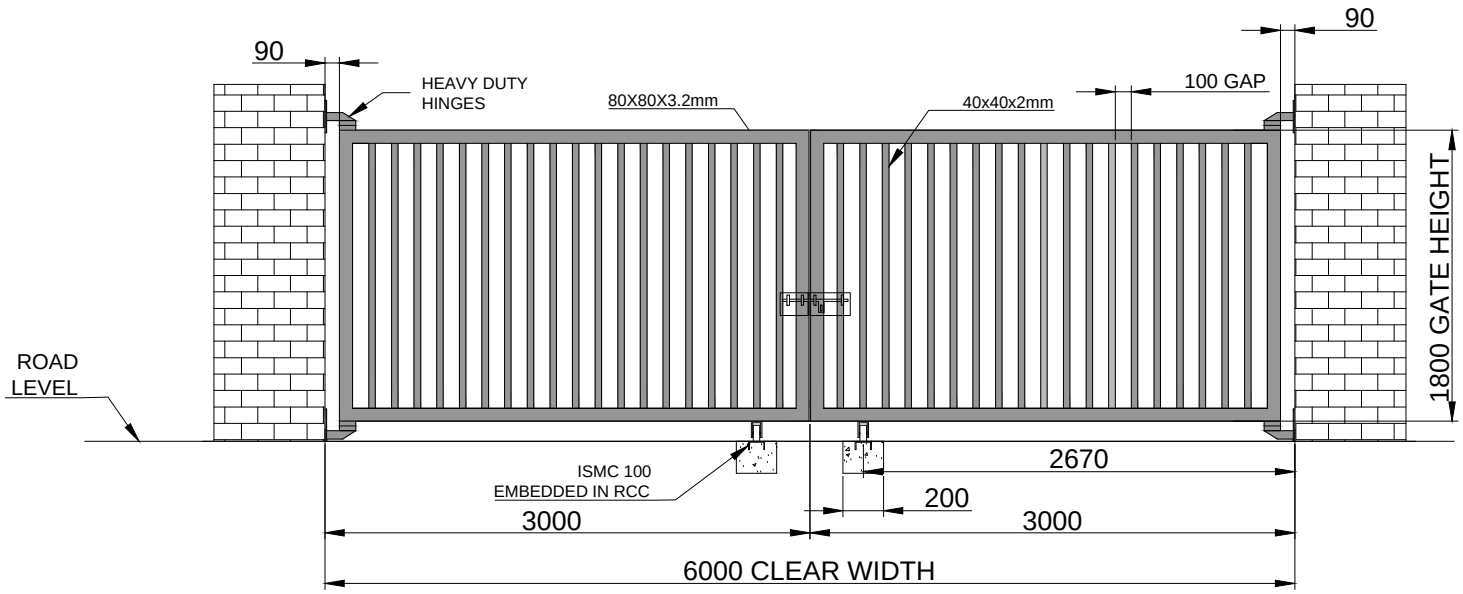

ELEVATION

TOLERANCE- ±10mm

DIMENSION :

CLEAR WIDTH	CLEAR HEIGHT	QUANTITY
6000mm	1800mm	1 NOS

MATERIAL:

SR NO	TUBE SPECIFICATION	
1	MS 80X80X3.2mm	OUTER FRAME
2	MS 40X40X2mm	INNER PATTERN

THICKNESS :

NOTE-
1. ALL REQUIRED CIVIL WORK WILL BE IN CLIENTS SCOPE.
2. ONE COAT OF RED OXIDE & TWO COAT OF APPROVED RAL SHADE WILL BE GIVEN TO THE GATE.

NIHVA
NIHVA TECHNOLOGIES PVT. LTD.
NIHVA TECHNOLOGIES PVT. LTD. PUNE
Email:- info@nihva.com
Website:- www.nihva.com

TITLE:

MANUAL SWING GATE 6X1.8m GATE NO 2

CLIENT'S APPROVAL :

CLIENT -

PROJECT -

SITE LOCATION -

DWG. NO. : NIHVA/17-18/VDR/0167 | REV-0

SCALE: NTS | WT: | SHEET:1 OF 1

NAME	SIGN	DATE
DRAWN: SURAJ		04-11-2017
CHECK : OMKAR		04-11-2017
APPD : SHEKHAR		04-11-2017

If any queries contact : projects@nihva.com

NOTE: ALL DIMENSIONS ARE IN mm

THIS DRAWING & DESIGN IS THE PROPERTY OF NIHVA TECHNOLOGIES. NOT TO BE SOLD OR COPIED TO ANY OTHER CONCERN.