

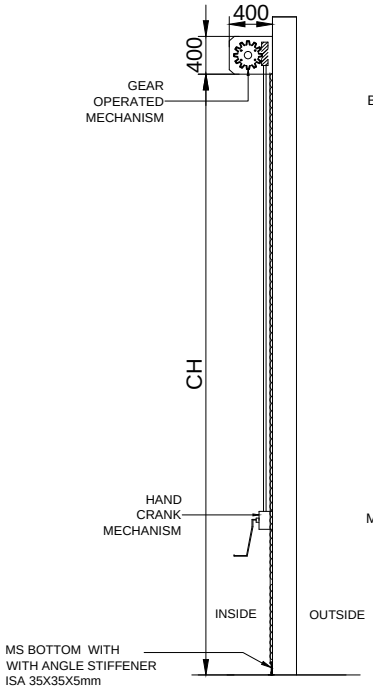



SIDE VIEW

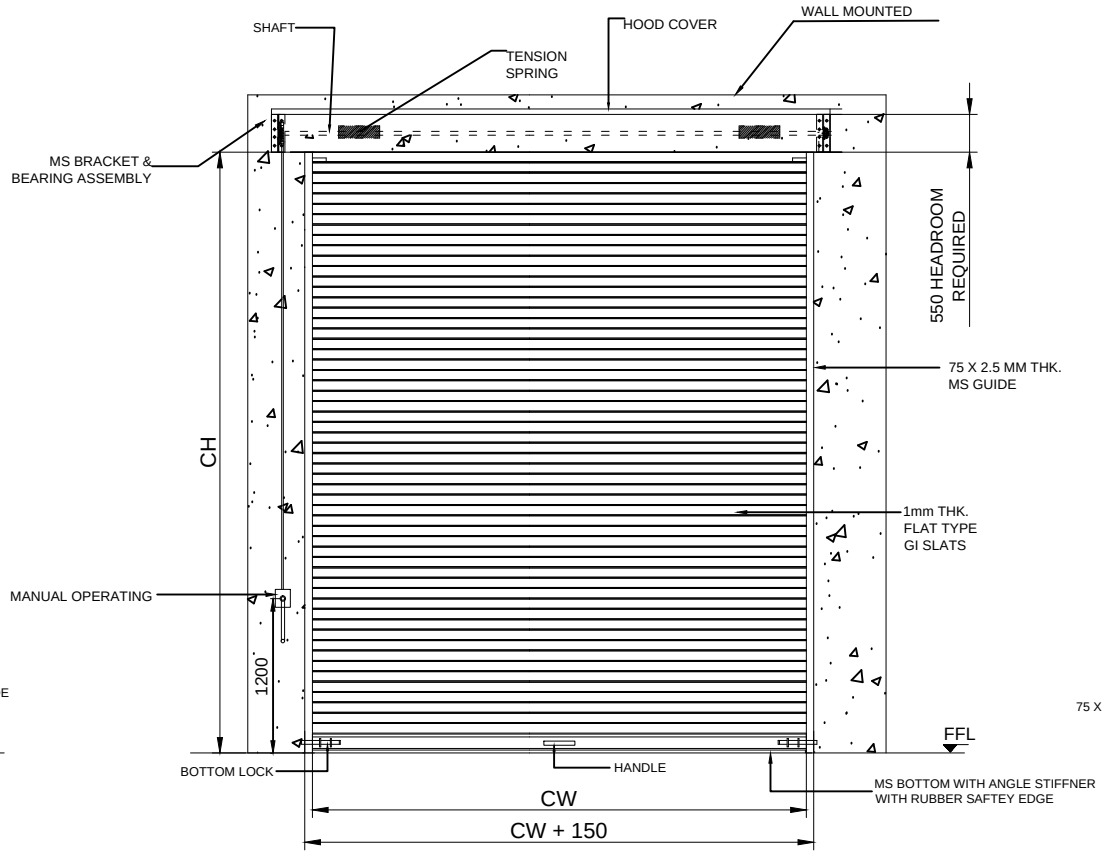


INSIDE ELEVATION

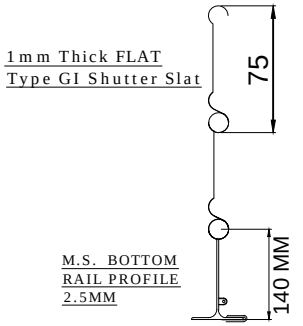

M.S. BOTTOM RAIL PROFILE 2.5MM

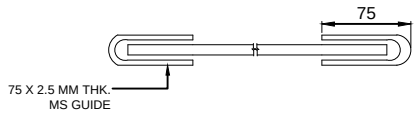

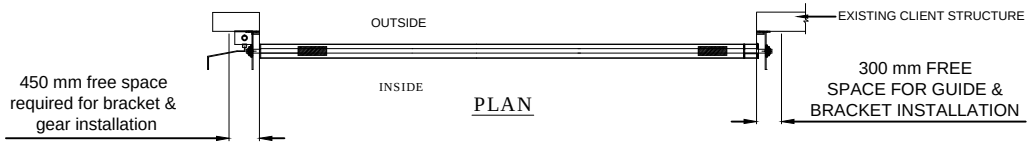

PLAN

TOLERANCE - ±10mm

SR.NO.	(CW) CLEAR WIDTH	(CH) CLEAR HEIGHT	QTY	RAL
01	2500	2500	1 NO	9010

NOTE-
1. ALL CIVIL WORK WILL BE CLIENT'S SCOPE.

This drawing & design is the property of NIHVA TECHNOLOGIES. Not to be sold or copied to any other concern.

TITLE
GEAR OPERATED ROLLING SHUTTER

NIHVA TECHNOLOGIES PVT. LTD.

NIHVA TECHNOLOGIES PVT. LTD. PUNE
Tel : 020 66304033
Email:- info@nihva.com
Website:- www.nihva.com

	NAME	SIGN	DATE
DRAWN	P.A		04.06.2020
CHECK	G.J		04.06.2020
APPRD.			

CLIENT - SYNERGY
PROJECT-EMBASSY INDUSTRIAL PARKS PVT. LTD.
SITE LOCATION - CHAKAN
If any queries contact : design@nihva.com
DWG. NO. : NIHVA/20-21/0013
REV- 00
ALL DIMENSION ARE IN mm
SCALE: NTS
WT:
SHEET: 01 OF 01