

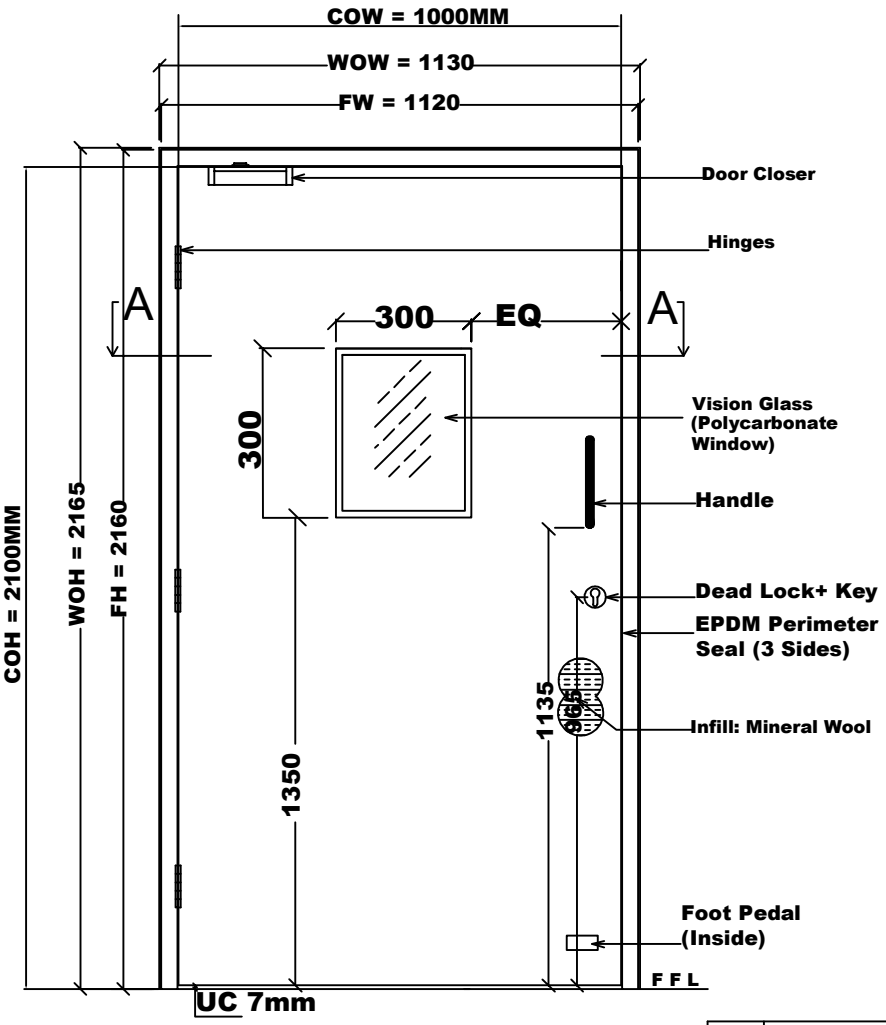


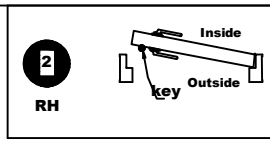

Frame Profile & Fixing Details
Not to scale

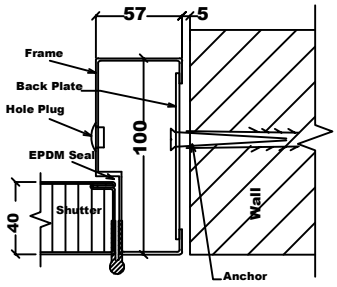

POS	Supply Description	Qty
1	HMPS Door Steel Set : 1,120.00 x 2,160.00 mm Single leaf door	06

Door Code :
Clear Opening (W x H) : 1000 mm x 2,100.00 mm

Material Specifications:
Frame : GI 1.20 mm
Shutter : GI 0.80 mm
Shutter Width / Active Shutter Width : 1,034.00 mm

Frame Profile (D x H): 100.00 mm x 57.00 mm
Frame Profile type : Kerf
Frame Joint Type: Bolting
Frame Rebate : Single
Under Cut: 7.00 mm
Door type : Single leaf door
Leaf type : NA.
Infill Material : Mineral Wool (Density 96 Kg/M3)
Handing : NA
Key Box: No
Fixing Shield: Universal Anchor
Shutter thickness : 40.0mm
Finish : Paint Finsih RAL 9002(Grey White)
Type of Fixing : On solid brick plastered wall with anchors

Frame Set:	1
Shutter: Single leaf door	1
Ball bearing butt hinge, SS304, of size 100 x 75 x 3mm with screws in SSS	3
Mortise dead lock, inc strike H4, 55mm BS, 20mm sq.forend SSS finish	1
Euro profile 5 pin cylinder 5701, 70mm Key x TT, NP finish	1
S.S. Handle D type back to back 19 x 200mm	2
Surface Heavy Door Closer with Standard Arm	1
Standard Clear Non Fire Polycarbonate Sheet 8mm - Size: 300 x 300mm	1
Foot Operated Door Pedal (Inside)	1
EPDM Perimeter Seal (3 Sides)	1

ABBRIVATIONS

WOW-Wall Opening Width
FW-Frame Width
WOH-Wall Opening Height
FH-Frame Height
UC-Under Cut
FFL-Finished Floor Level
COW-Clear opening width
COH-Clear opening height

NOTES:

1:All Dimensions are in mm

2:Tolerances - All linear dimensions +/- 3mm, others +/- 0.5mm

3:All civil work is in client scope

This drawing & design is the property of NIHVA TECHNOLOGIES. Not to be sold or copied to any other concern.

TITLE: SINGLE LEAF STEEL DOORS

NIHVA TECHNOLOGIES PVT. LTD.
NIHVA TECHNOLOGIES PVT. LTD, PUNE
Tel : 020 66304033
Email:- info@nihva.com
Website:- www.nihva.com

	NAME	DATE	SIGN
DRAWN	S.B	19/10/2021	
CHECK	G.P	19/10/2021	
APPRD.	A.K	19/10/2021	

If any queries contact : design@nihva.com

ALL DIMENSION ARE IN mm

CLIENT - FERRERO INDIA PVT PLD
LOCATION - BARAMATI
PRODUCT - SINGLE LEAF STEEL DOOR
DWG NO:-NIHVA\21-22\0240 REV-1
SCALE: NTS **SCALE :1:20** SHEET: 01 OF 02

Rev No.	Revision	Date	Revised By
1.	Outer dimension of the steel door has been changed & wall structure drawing to be added.	19/10/2021	Sujata. B