




A SIDE ELEVATION

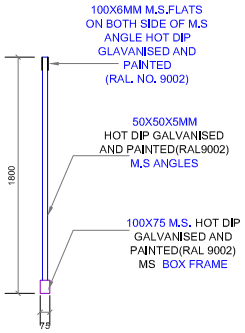


GATE SHUTTER SECTION

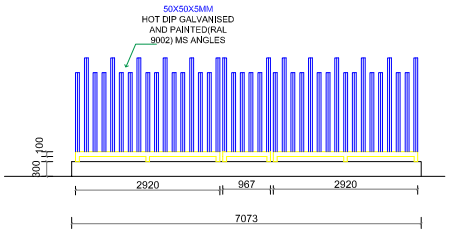

B SIDE ELEVATION

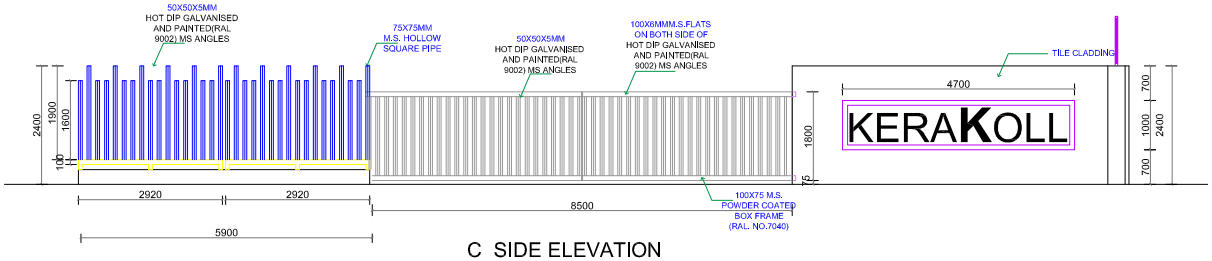

C SIDE ELEVATION

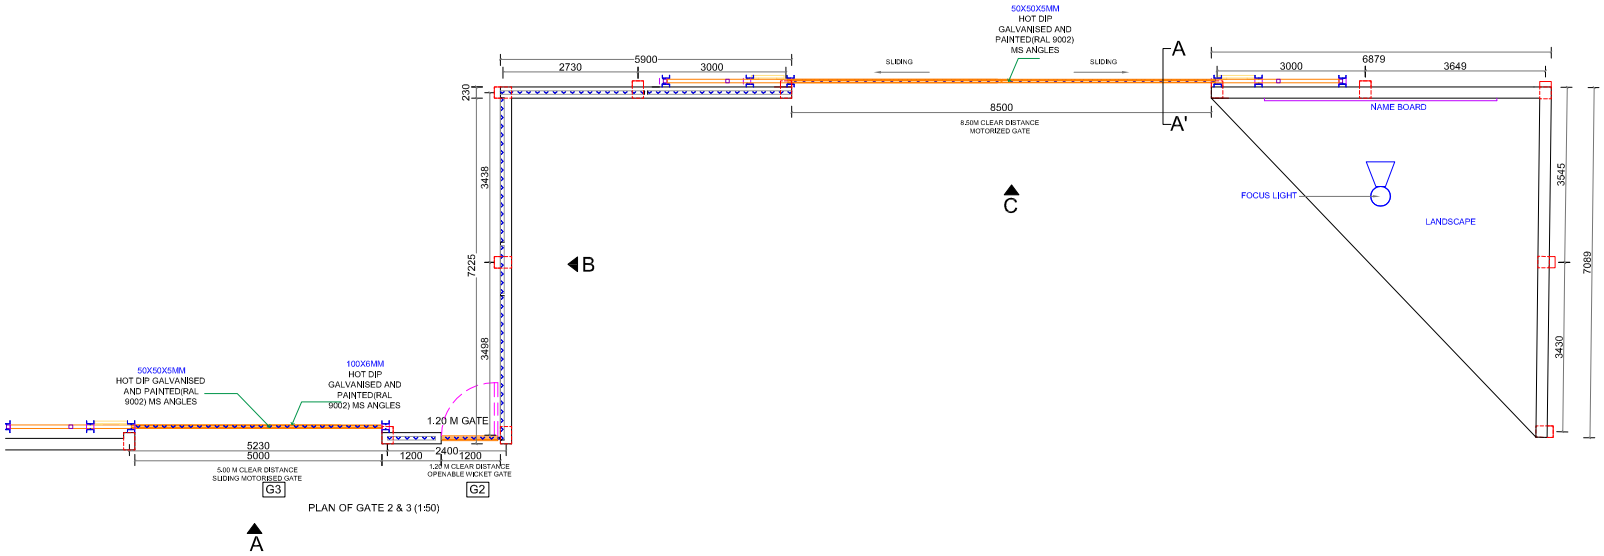

PLAN OF GATE 2 & 3 (1:50)

A

REEFER DRAWING NUMBER 1107/2013/24

NORTH

NOTES –

1.Do not scale the drawing.Work to figured dimensions only.
2.All dimensions are in millimetres(mm) unless noted otherwise & levels in metres(m).
3.This drawing to be read in conjunction with all relevant contract drawings and documentation.
4.This drawing is to be carefully checked by contractor against architects drawings,and any discrepancy reported to the engineer before construction commences.

DATE	REVISIONS	DRAWN BY	UPDATE

REVISIONS –

CONSULTANTS –

ARCHITECT –

ARCHITECTS UNITED
Address: 111/9,14Th lane prabhat road, Pune–411004.
Tel: 020–25441426, 020–25469176 Fax: 020–25448059.
E–mail: architectunited@vsnl.net
Wesite: www.architectsunited.com

PROJECT –
INDUSTRIAL SHED AT PLOT NO.630,
SAVLI INDUSTRIAL ESTATE,VADODARA,
GUJRAT,INDIA

CLIENT –
M/S KERAKOLL INDIA PVT. LTD

SCALE	DATE	DRAWN BY	JOB NO	STATUS
AS SPECIFIED	19.12.13	ASHWINI	10_15_K23	FOR CONSTRUCTION

DRG NAME :GATE DETAIL
FILE NAME :GATE_DETAIL_10_15_K23
DWG NO. : 11583

REVISIONS