



DOOR DIMENSION

CW: 24380 MM	CH: 4880 MM	QTY:01 NO

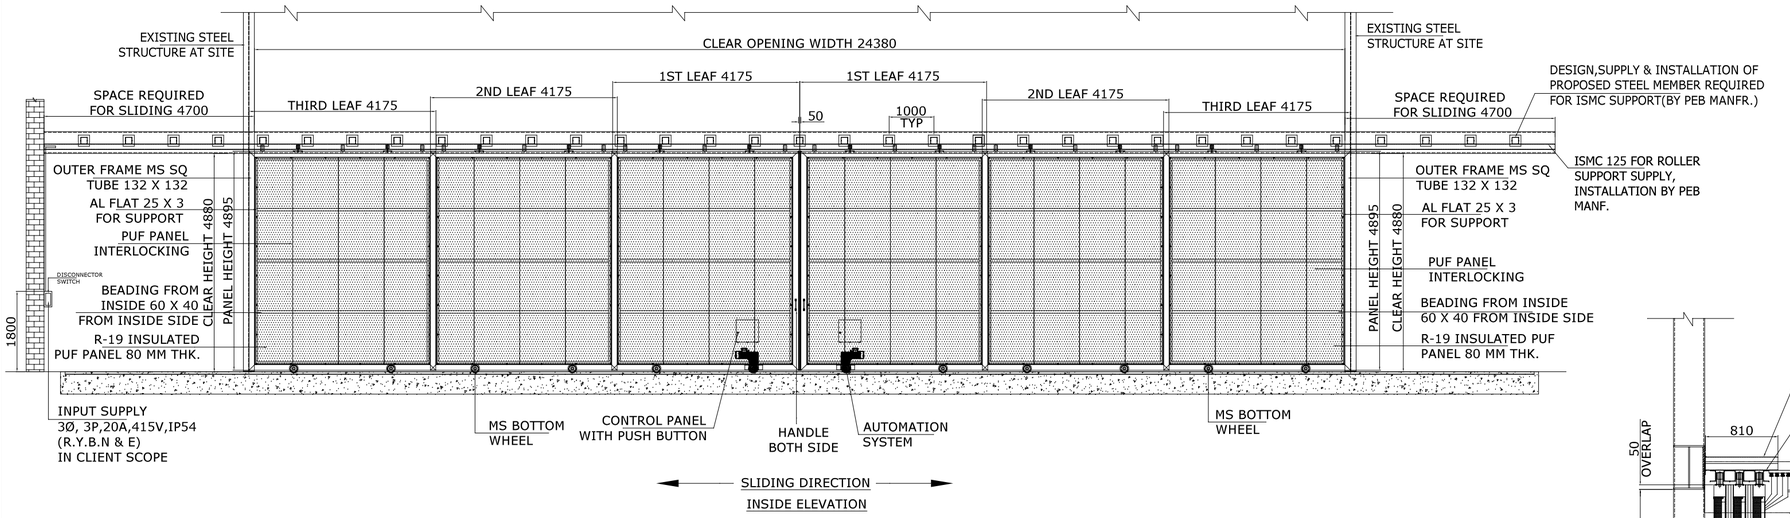

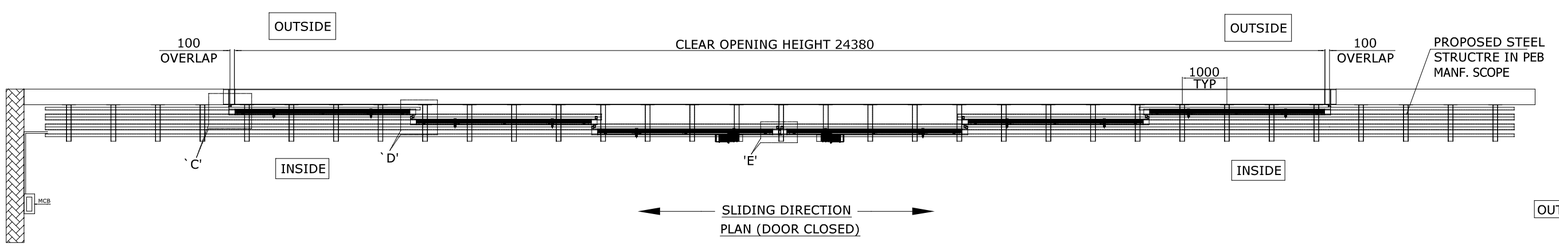

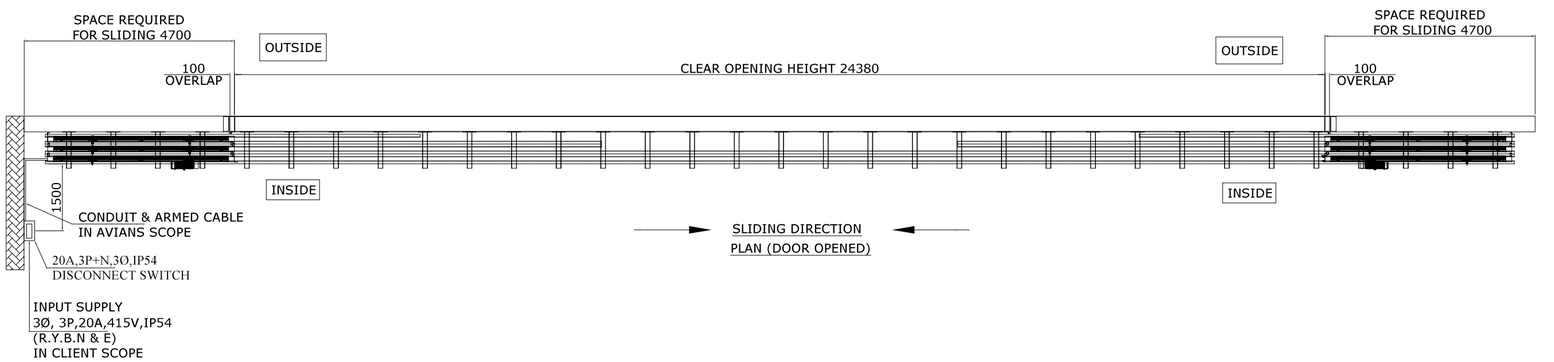

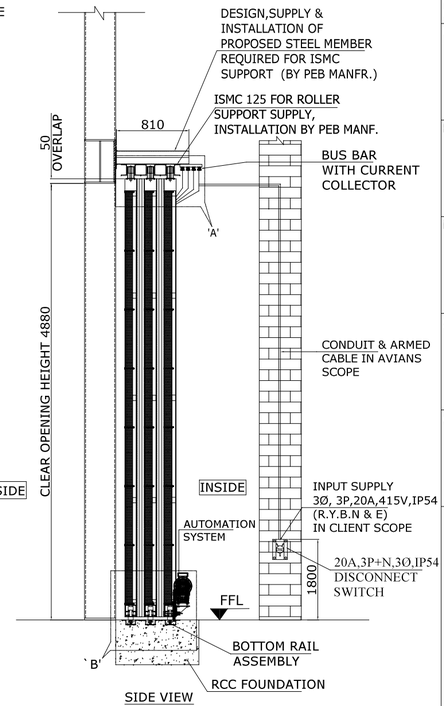

GENERAL NOTES & REMARKS :

THIS IS A COPYRIGHT DOCUMENT AND MUST NOT BE REPORDUCED WITHOUT WRITTEN PERMISSION.
THE BUILDER IS TO WORK ACCORDING TO FIGURED DIMENSIONS, AND MUST NOT SCALE THE DRAWING.
ALL DIMENSIONS ARE TO BE CHECKED ON SITE, ANY DISCREPANCIES TO BE REPORTED TO THE ENGINEER BEFORE ANY WORK IS CARRIED OUT.
ALL DIMENSIONS IN MILLIMETERS, UNLESS OTHER WISE STATED.
MEASUREMENTS ARE TO THE CLOSEST SITE DIMENSION.
VERIFY ALL DIMENSIONS ON SITE.

KEY PLAN :

REVISION :

NO.	DATE	DESCRIPTION	ACTION
R-0	14.10.20	DOOR SPECIFICATION & CLIENT COMMENTS ADDED	--

ACTION CODE :

A - APPROVED
B - APPROVED AS NOTED
C - NOT APPROVED
D - RETURNED WITH COMMENTS
E - FOR INFORMATION

CLIENT :

ALI AL SALEM AIR BASE
ALI AL SALEM AIR BASE, KUWAIT

PROJECT :

SEMI PERMANENT SMALL AIRCRAFT WEATHER SHELTER C-12

MAIN CONTRACTOR :

SUB CONTRACTOR:

AVIANS INNOVATIONS TECHNOLOGY PVT. LTD.
615 / 25, Pradhikaran, Nigdi, Pune-411044
Tel : 020 65112222, Fax : +91 20 27490570
www. avians.co.in sales@avians.co.in

VENDOR DESIGNER:

DRAWING TITLE :

MOTORIZED TELESCOPIC HANGER DOOR

REFERENCE DRAWING DETAILS :

DATE :	-	REVISION NO. :	-
DRAWING NO. :	- AIT/19-20/8027-1/MTSD-01/R1		
DRAWING DETAILS :	GENERAL ARRANGEMENT DRAWING		

DRAWN BY :	DESIGN BY :	CHECKED BY :	APPROVED BY :
CAK	CAK	MCP	MCP
DATE :	SCALE :	PAPER SIZE :	REVISION NO. :
30.09.2020	AS NOTED	A3	0
DRAWING NO. :			