



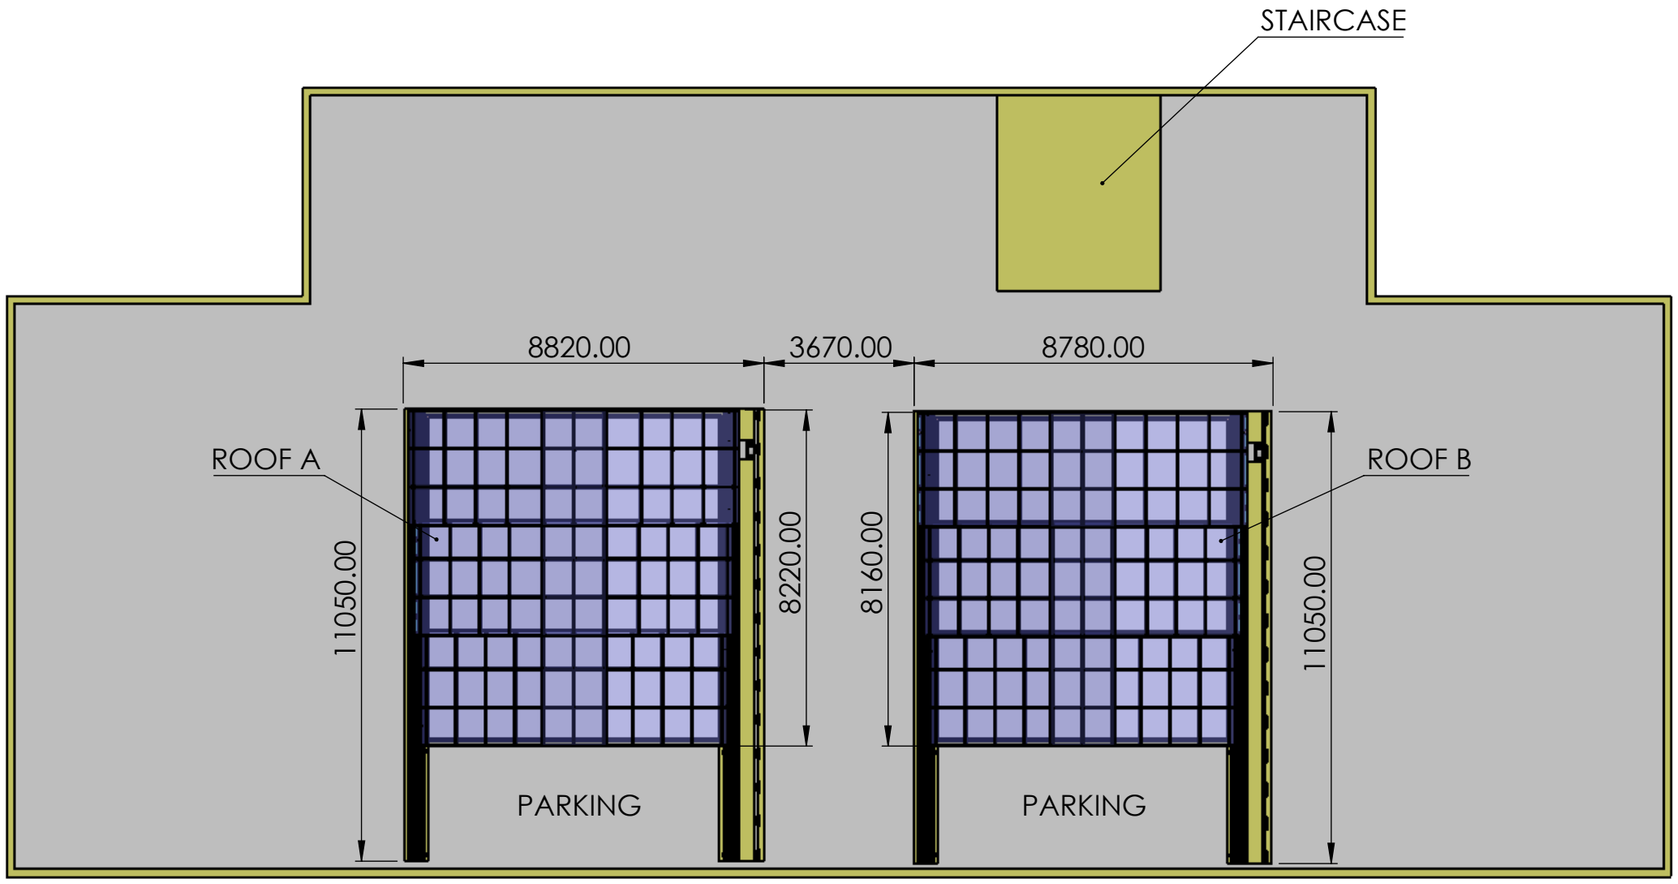


TITLE - ROOF AUTOMATION				NIHVA TECHNOLOGIES PVT.LTD.PUNE
DWG NO - NTPL-281-PM-001-00-00-00				Website - www.nihva.com
	NAME	SIGNATURE	DATE	PROJECT NO - NTPL-281-B-PM
DRAWN	V.G.		25-05-2025	PRODUCT - RETRACTABLE ROOF
CHK'D	S.W.		25-05-2025	SITE LOCATION - AKOLA
APPV'D	V.T.		25-05-2025	
if any queries contact - supportautomation@nihva.com				REVISION - QTY - 1
ALL DIMENSION ARE IN mm		A3		SCALE - SHEET 1 OF 41

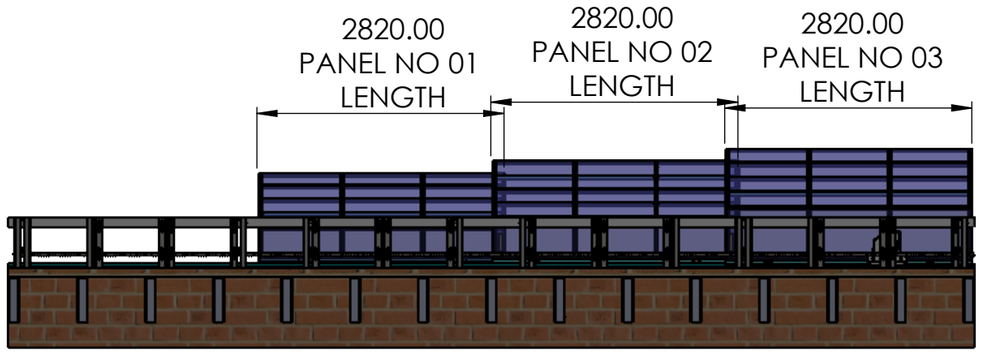

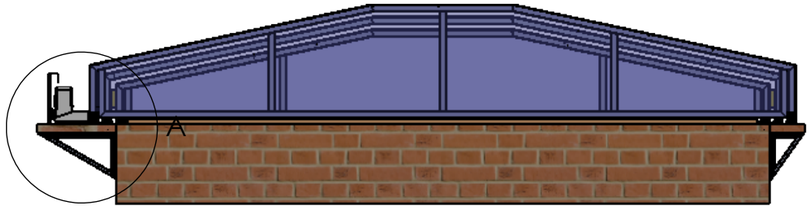

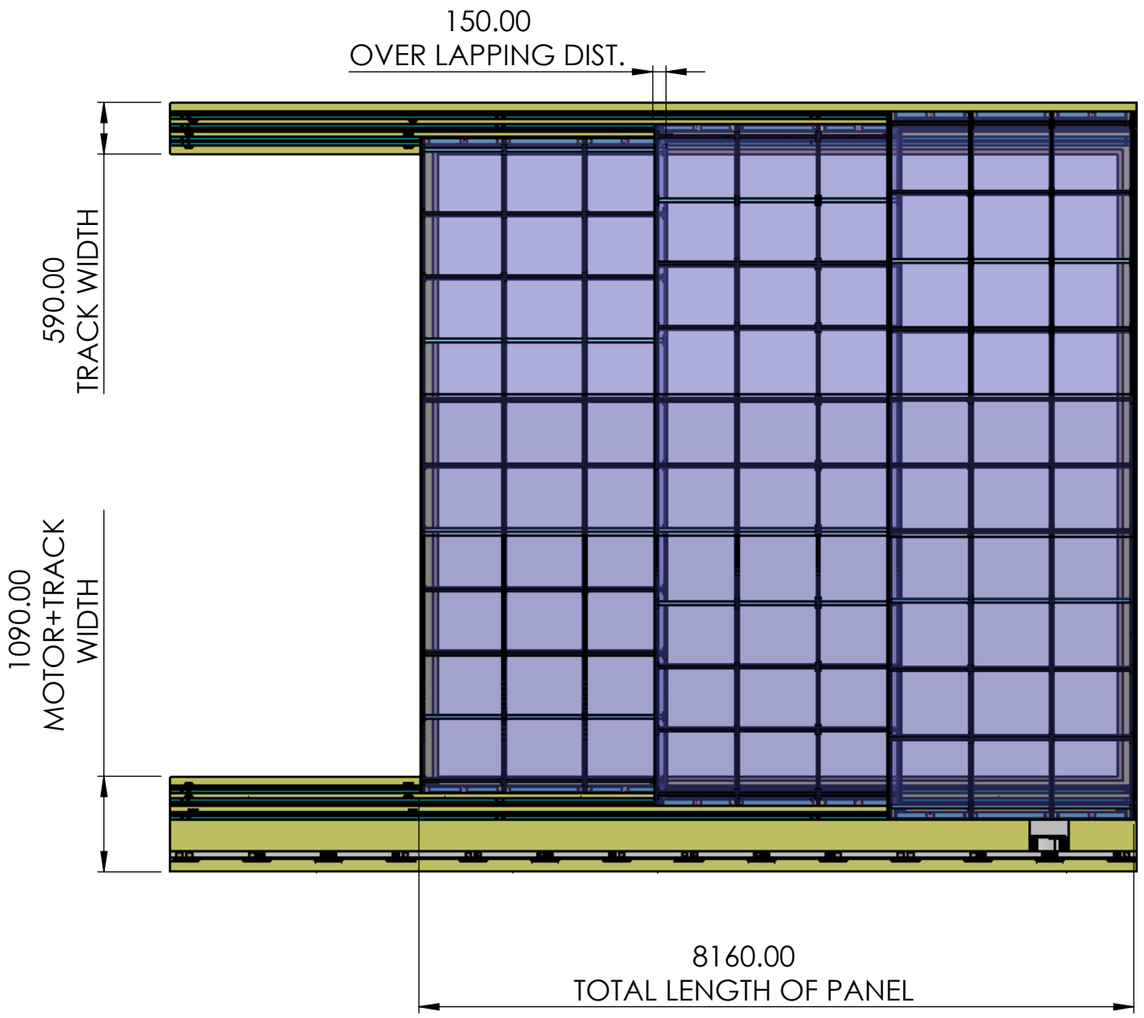


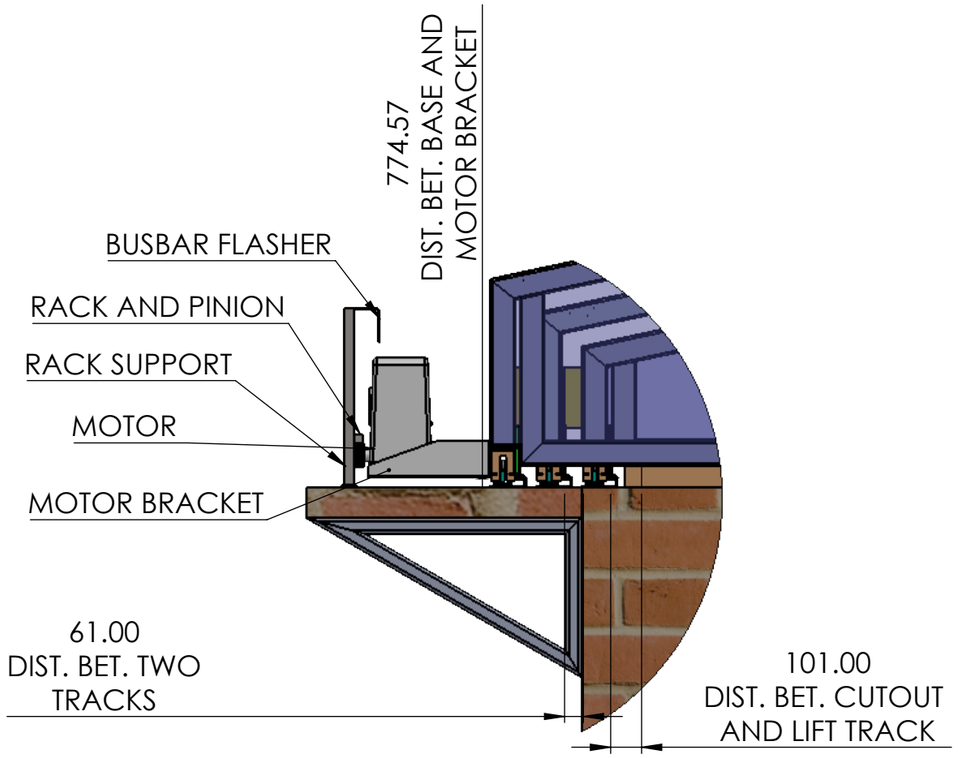

DETAIL A
SCALE 1 : 20

TITLE - ROOF AUTOMATION				NIHVA TECHNOLOGIES PVT.LTD.PUNE
DWG NO - NTPL-281-PM-001-00-00-00				Website - www.nihva.com
	NAME	SIGNATURE	DATE	PROJECT NO - NTPL-281-B-PM
DRAWN	V.G.		25-05-2025	PRODUCT - RETRACTABLE ROOF
CHK'D	S.W.		25-05-2025	SITE LOCATION - AKOLA
APPV'D	V.T.		25-05-2025	
if any queries contact - supportautomation@nihva.com				REVISION - / QTY - 1
ALL DIMENSION ARE IN mm			A3	SCALE - / SHEET 2 OF 41


ITEM NO.	PART NUMBER	DESCRIPTION	QTY.
1	R2_TRACK AND BOLT ASM		6
2	R2_PANEL 01 ASM.		1
3	R2_PANEL 02 ASM		1
4	R2_PANEL 03 ASM		1
5	R2_01PRACTICE Rack support_575	STD (LOOSE PART)	14
6	GUIDE RAILS-T89-1B	STD (5 M LENGTH)	12
7	MOTOR MTG BRT PLATE 1_NICE_1.8T	454X400X5MM THK	1
8	NICE RB 2.5T		1
9	ANCHOR BOLT M10 x 75 MM	STD	6
10	NYLON STOPPER SMALL		8
11	NYLON STOPPER BIG		2
12	LOCKING PLATE 1	78.85 X 90 X 6MM THK	24

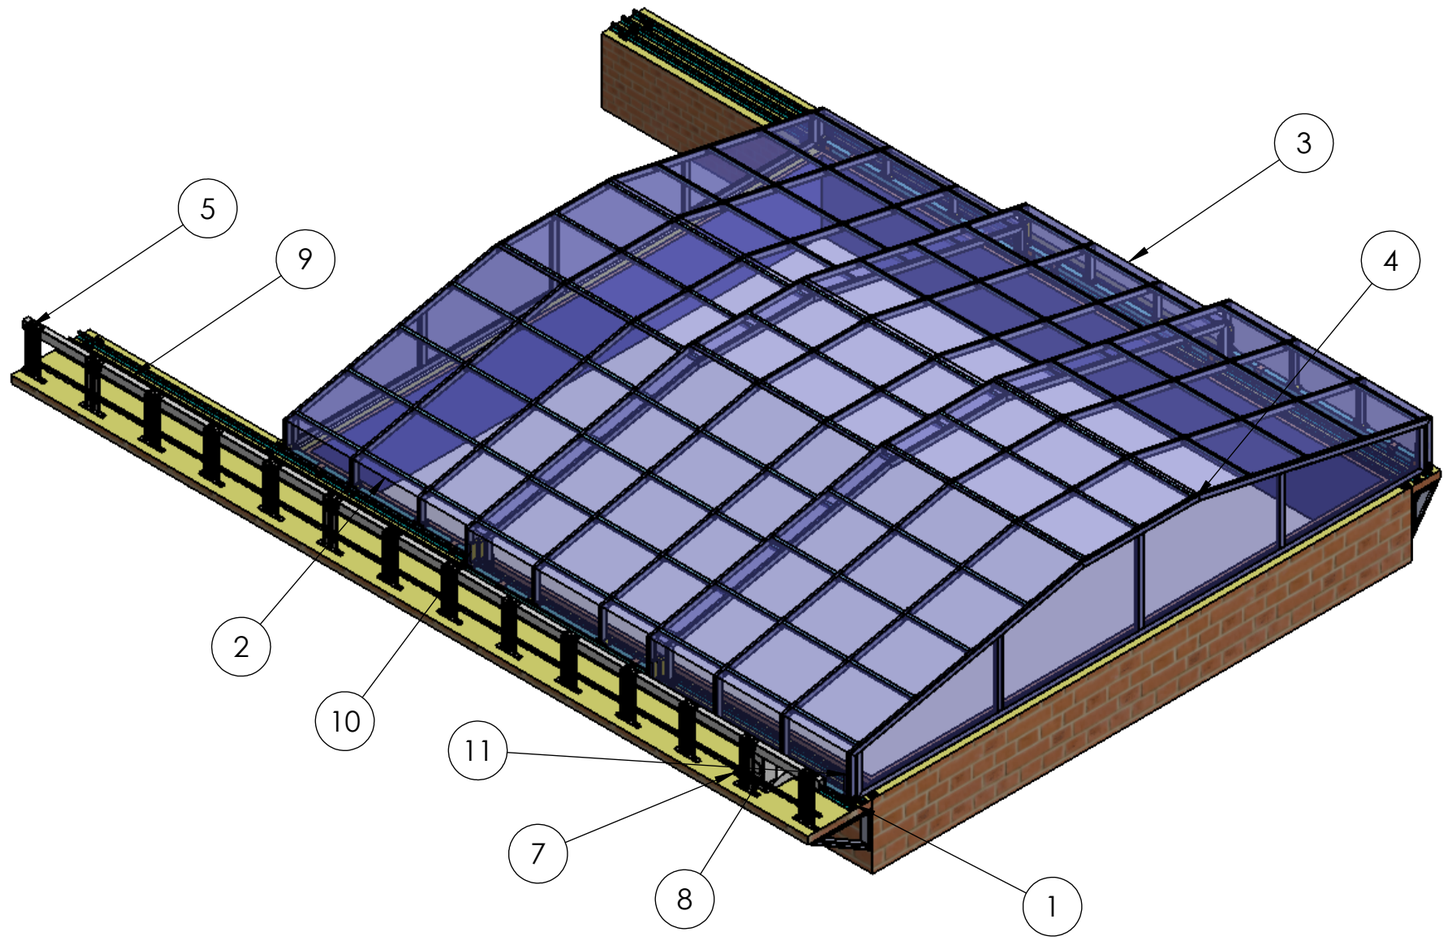



ISOMATRIC VIEW OF ROOF

TITLE - ROOF AUTOMATION				NIHVA TECHNOLOGIES PVT.LTD.PUNE
DWG NO - NTPL-281-PM-001-00-00-00				Website - www.nihva.com
	NAME	SIGNATURE	DATE	PROJECT NO - NTPL-281-B-PM
DRAWN	V.G.		25-05-2025	PRODUCT - RETRACTABLE ROOF
CHK'D	S.W.		25-05-2025	SITE LOCATION - AKOLA
APPV'D	V.T.		25-05-2025	
if any queries contact - supportautomation@nihva.com				REVISION - QTY - 1
ALL DIMENSION ARE IN mm			A3	SCALE - SHEET 3 OF 41

ITEM NO.	PART NUMBER	DESCRIPTION	QTY.
1	CUTOUT_1 BASE		1
2	GUIDE RAILS-T89-1B	STD (5 M LENGTH)	12
3	ANCHOR BOLT M10 x 75 MM	STD	130

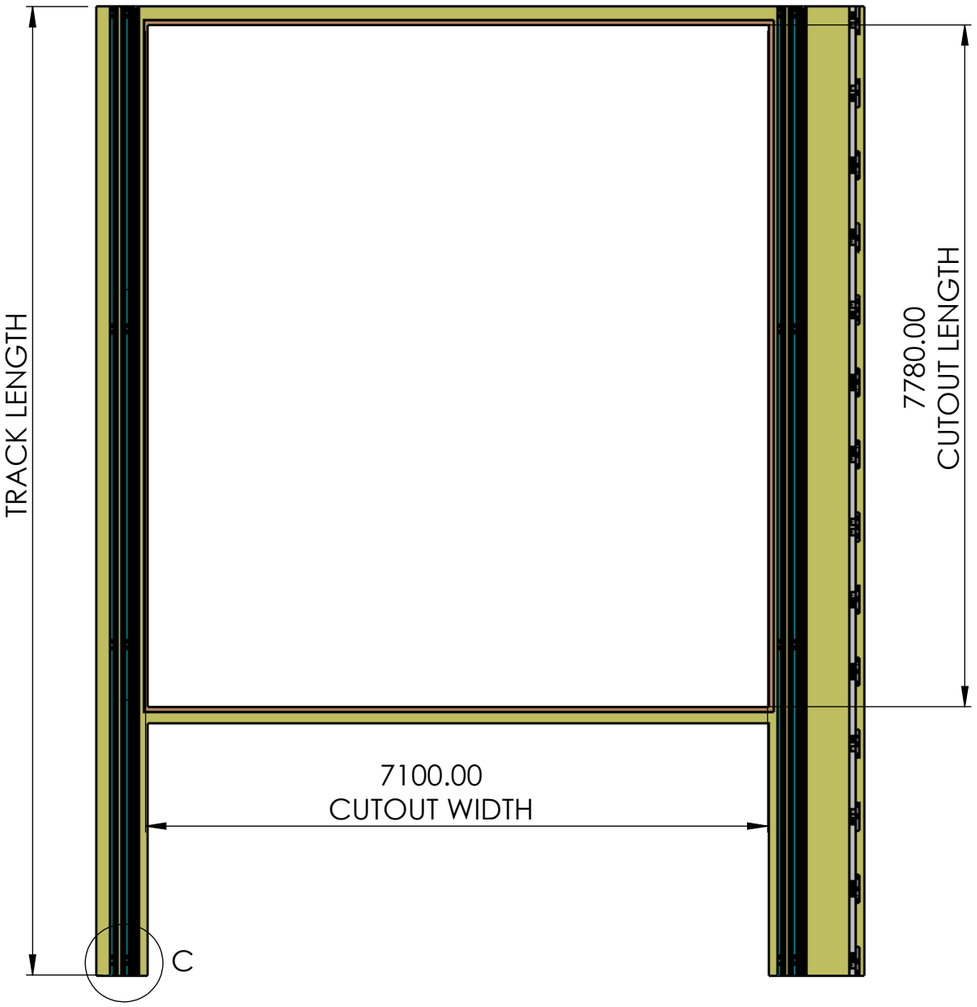


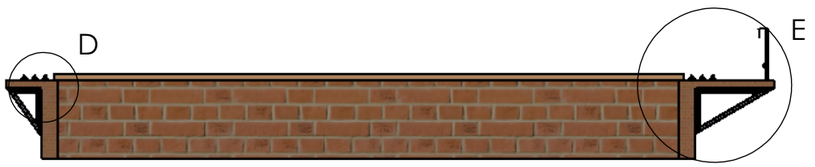

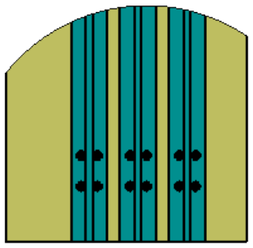


DETAIL C
SCALE 1 : 15

ANCHOR BOLT FASTENING

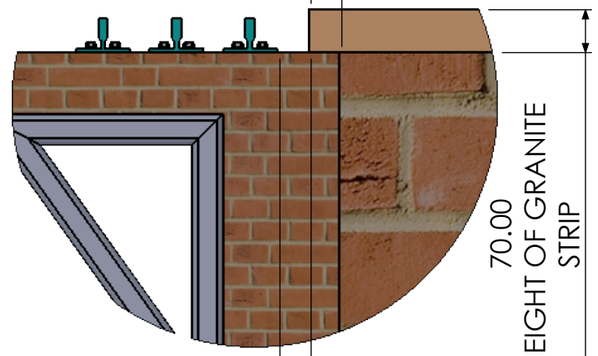

DETAIL D
SCALE 1 : 10

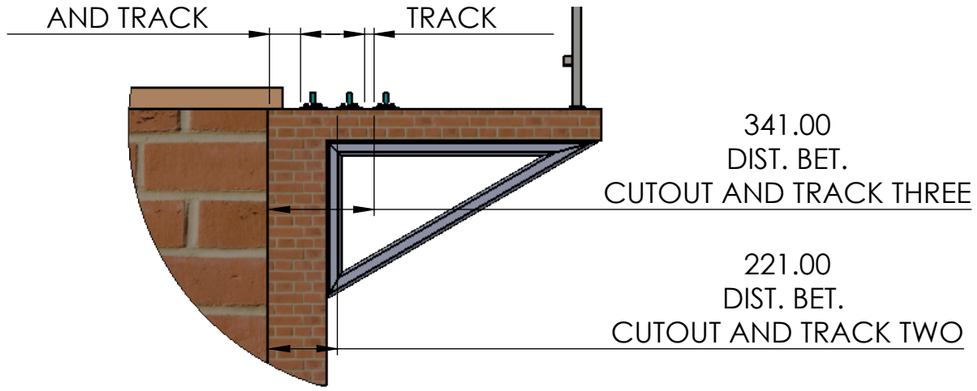



DETAIL E
SCALE 1 : 20


NOTE :- SUB ASM. NO 01
TRACK ASM.

TITLE - ROOF AUTOMATION				NIHVA TECHNOLOGIES PVT.LTD.PUNE
DWG NO - NTPL-281-PM-001-01-00-00				Website - www.nihva.com
	NAME	SIGNATURE	DATE	PROJECT NO - NTPL-281-B-PM
DRAWN	V.G.		25-05-2025	PRODUCT - RETRACTABLE ROOF
CHK'D	S.W.		25-05-2025	SITE LOCATION - AKOLA
APPV'D	V.T.		25-05-2025	
if any queries contact - supportautomation@nihva.com				REVISION - / QTY - 1
ALL DIMENSION ARE IN mm			A3	SCALE - / SHEET 4 OF 41

ITEM NO.	PART NUMBER	DESCRIPTION	QTY.
1	R2_GUIDE RAILS-T89-1B	STD	12

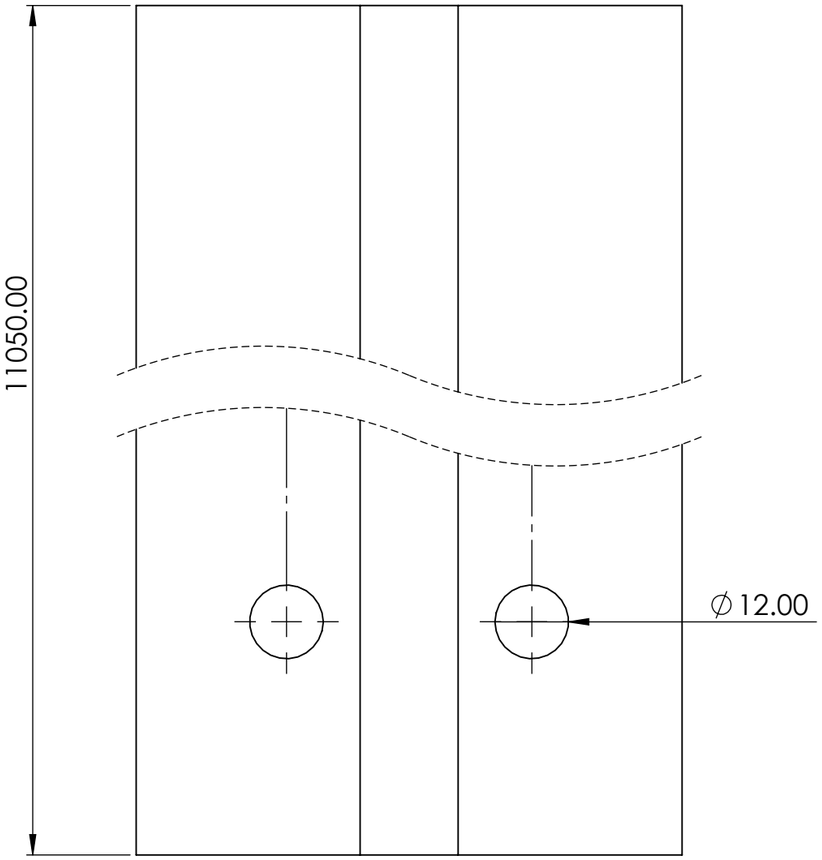


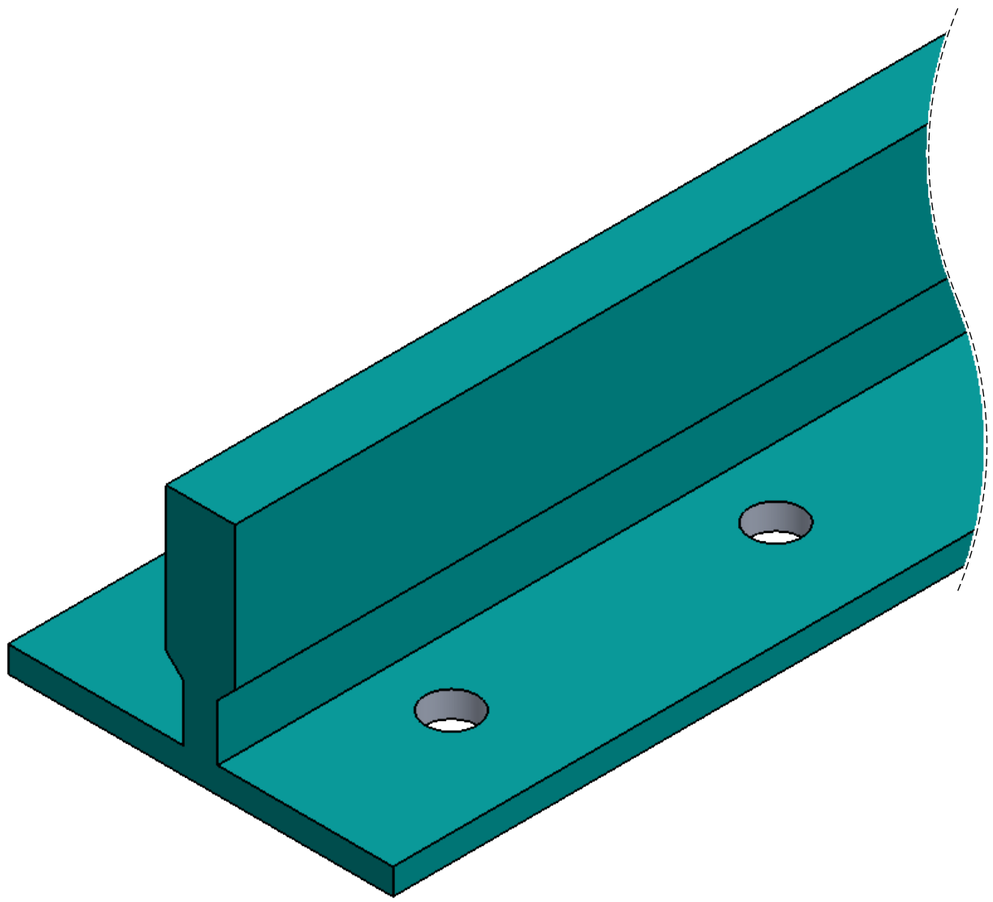


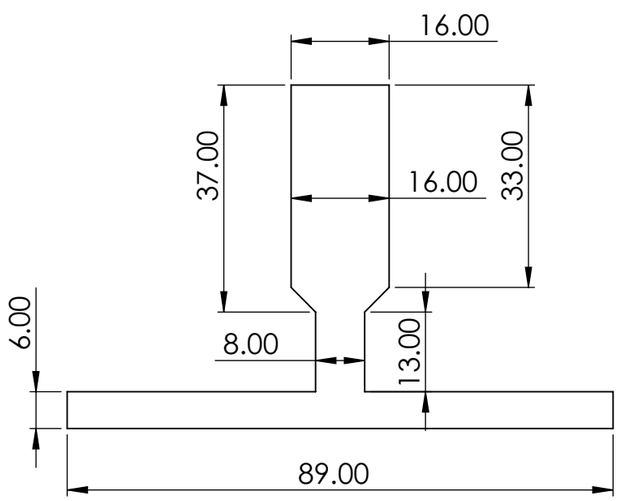


TITLE - ROOF AUTOMATION				NIHVA TECHNOLOGIES PVT.LTD.PUNE
DWG NO - NTPL-281-PM-001-01-01-01				Website - www.nihva.com
	NAME	SIGNATURE	DATE	PROJECT NO - NTPL-281-B-PM
DRAWN	V.G.		25-05-2025	PRODUCT - RETRACTABLE ROOF
CHK'D	S.W.		25-05-2025	SITE LOCATION - AKOLA
APPV'D	V.T.		25-05-2025	
if any queries contact - supportautomation@nihva.com				REVISION - / QTY - 1
ALL DIMENSION ARE IN mm		A3		SCALE - / SHEET 5 OF 41

ITEM NO.	PART NUMBER	DESCRIPTION	QTY.
1	R2_GUIDE RAILS-T89-1B	STD	6

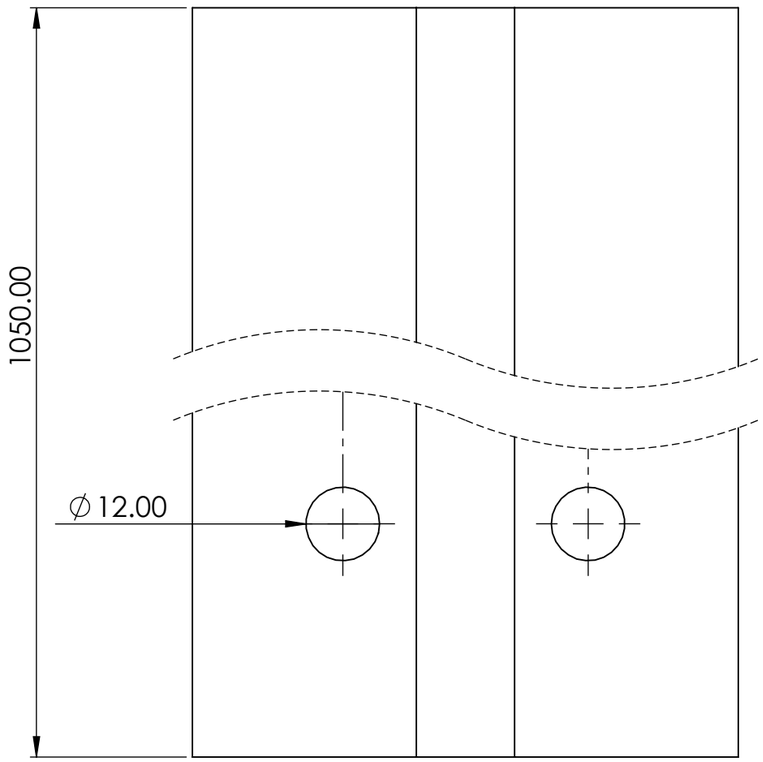

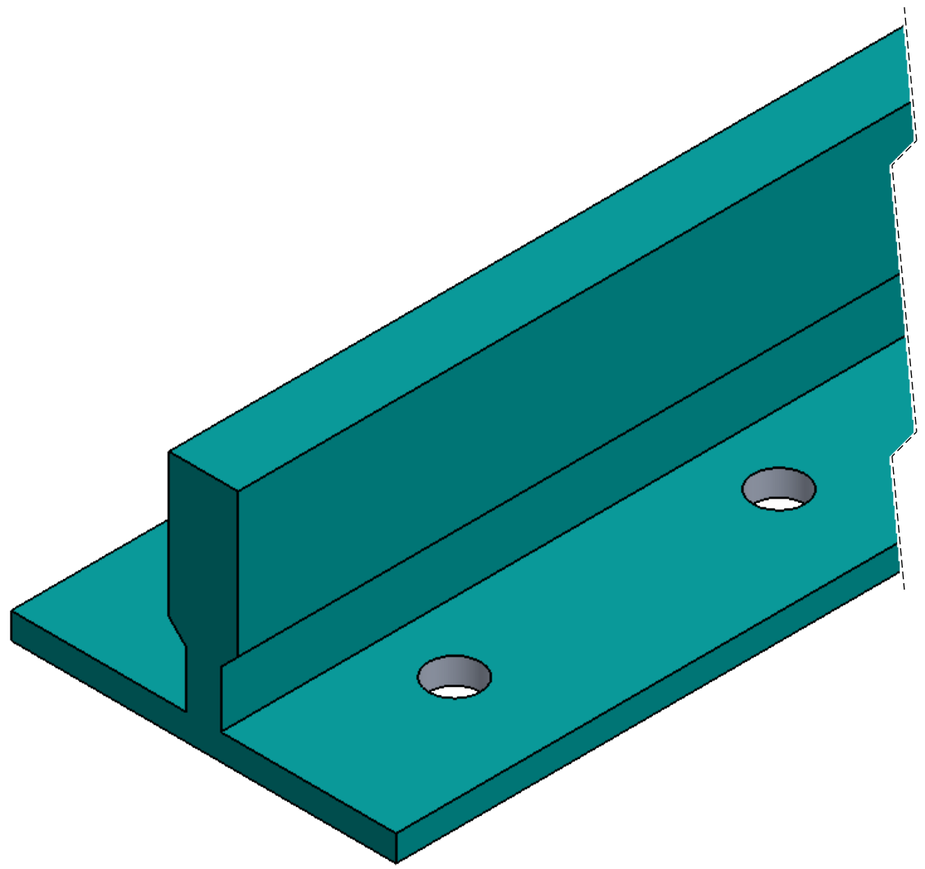


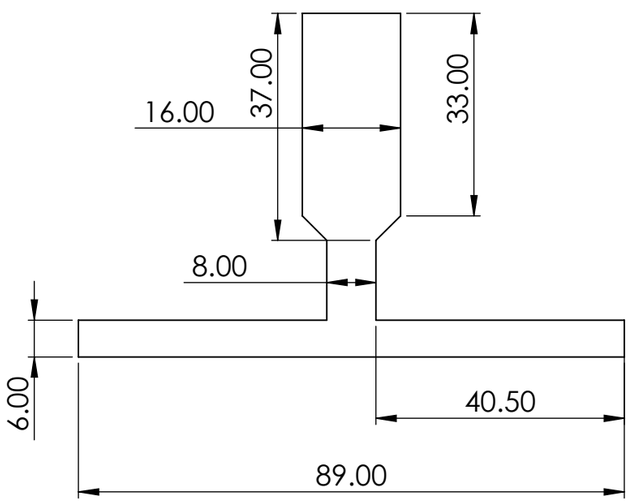



NOTE :- GUIDE RAILS-T89-1B
PART REQ. TO CUT-1050 MM LENGTH
QTY :- 6 No's

TITLE - ROOF AUTOMATION				NIHVA Technologies Pvt. Ltd.	NIHVA TECHNOLOGIES PVT.LTD.PUNE Website - www.nihva.com
DWG NO - NTPL-281-PM-001-01-01-01					
	NAME	SIGNATURE	DATE	PROJECT NO - NTPL-281-B-PM	
DRAWN	V.G.		25-05-2025	PRODUCT - RETRACTABLE ROOF	
CHK'D	S.W.		25-05-2025	SITE LOCATION - AKOLA	
APPV'D	V.T.		25-05-2025		
if any queries contact - supportautomation@nihva.com				REVISION -	QTY - 1
ALL DIMENSION ARE IN mm		A3		SCALE -	SHEET 6 OF 41


ITEM NO.	PART NUMBER	DESCRIPTION	QTY.
1	R2_TRACK Anchor Bolt M10x75	STD	130

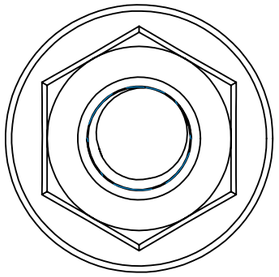

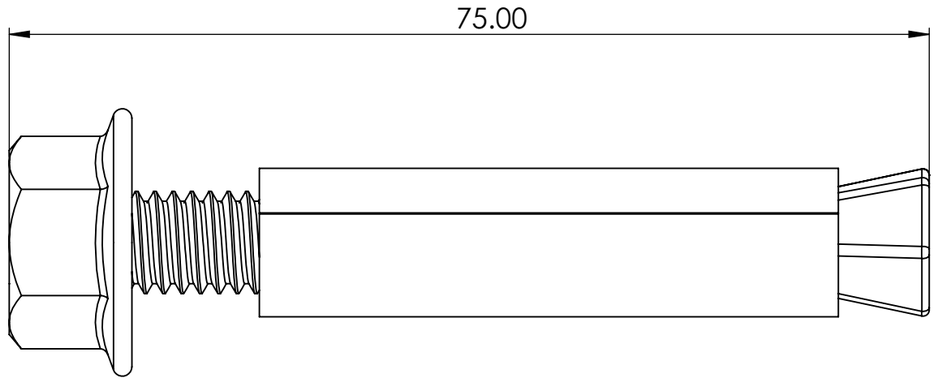


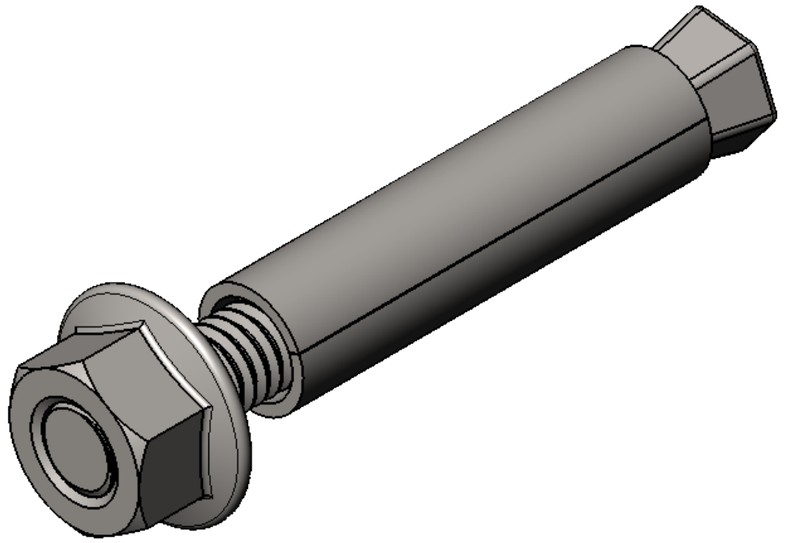

TITLE - ROOF AUTOMATION				NIHVA TECHNOLOGIES PVT.LTD.PUNE
DWG NO - NTPL-281-PM-001-01-01-02				Website - www.nihva.com
	NAME	SIGNATURE	DATE	PROJECT NO - NTPL-281-B-PM
DRAWN	V.G.		25-05-2025	PRODUCT - RETRACTABLE ROOF
CHK'D	S.W.		25-05-2025	SITE LOCATION - AKOLA
APPV'D	V.T.		25-05-2025	
if any queries contact - supportautomation@nihva.com				REVISION - / QTY - 1
ALL DIMENSION ARE IN mm			A3	SCALE - / SHEET 7 OF 41

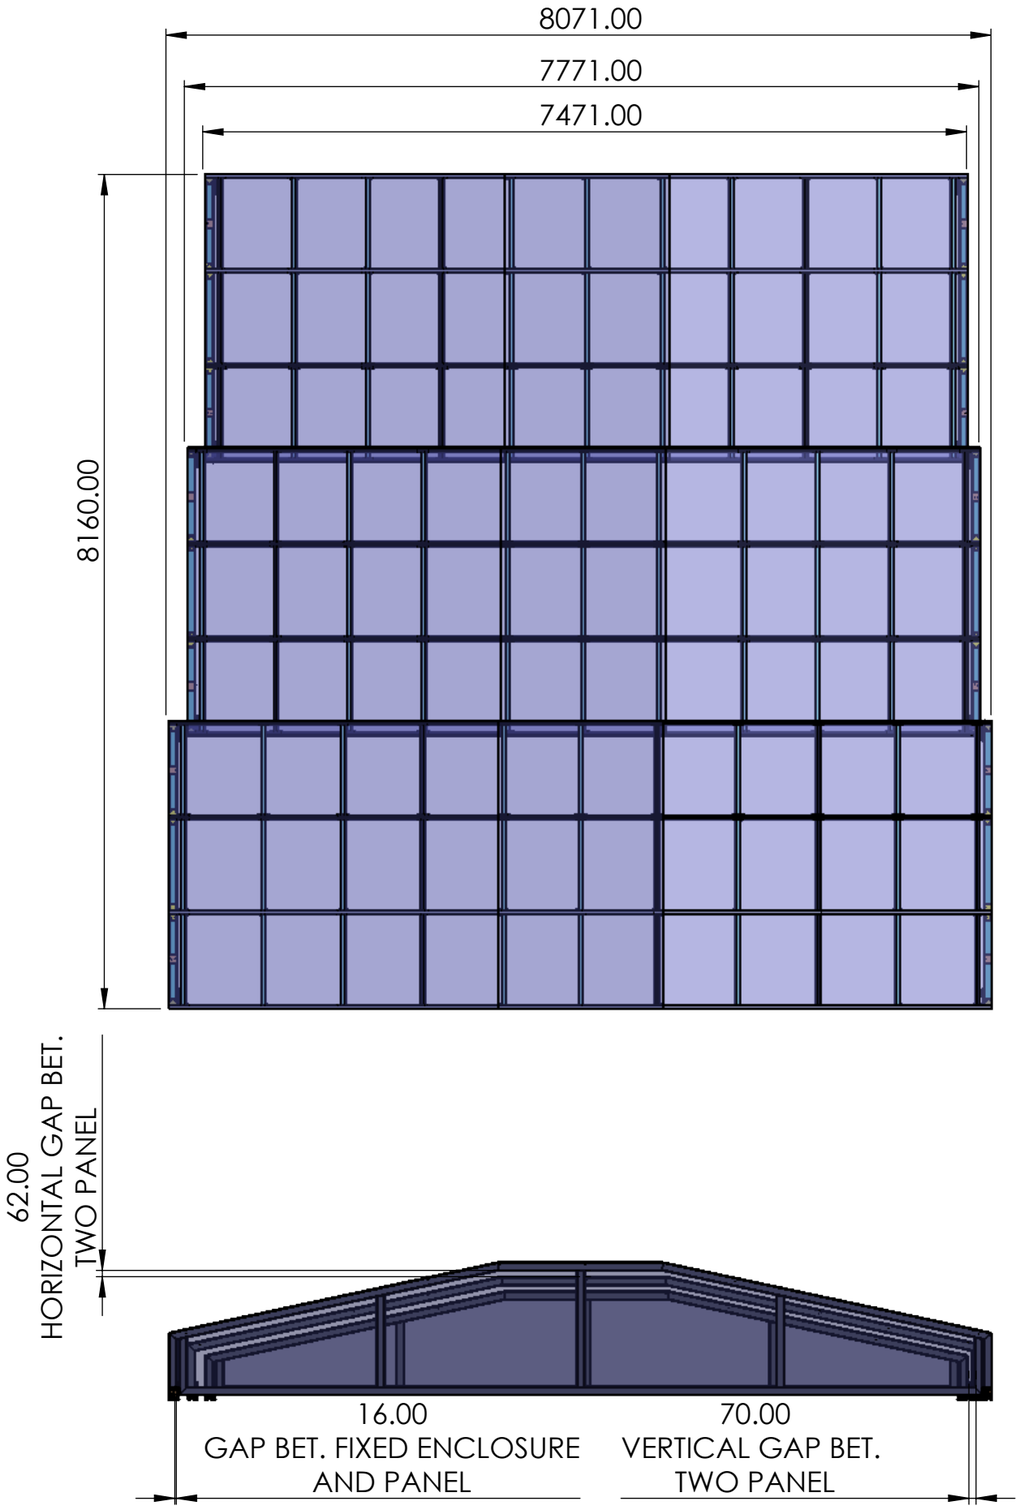


ITEM NO.	PART NUMBER	DESCRIPTION	QTY.
1	R2_PANEL 01 ASM.		1
2	R2_PANEL 02 ASM		1
3	R2_PANEL 03 ASM		1

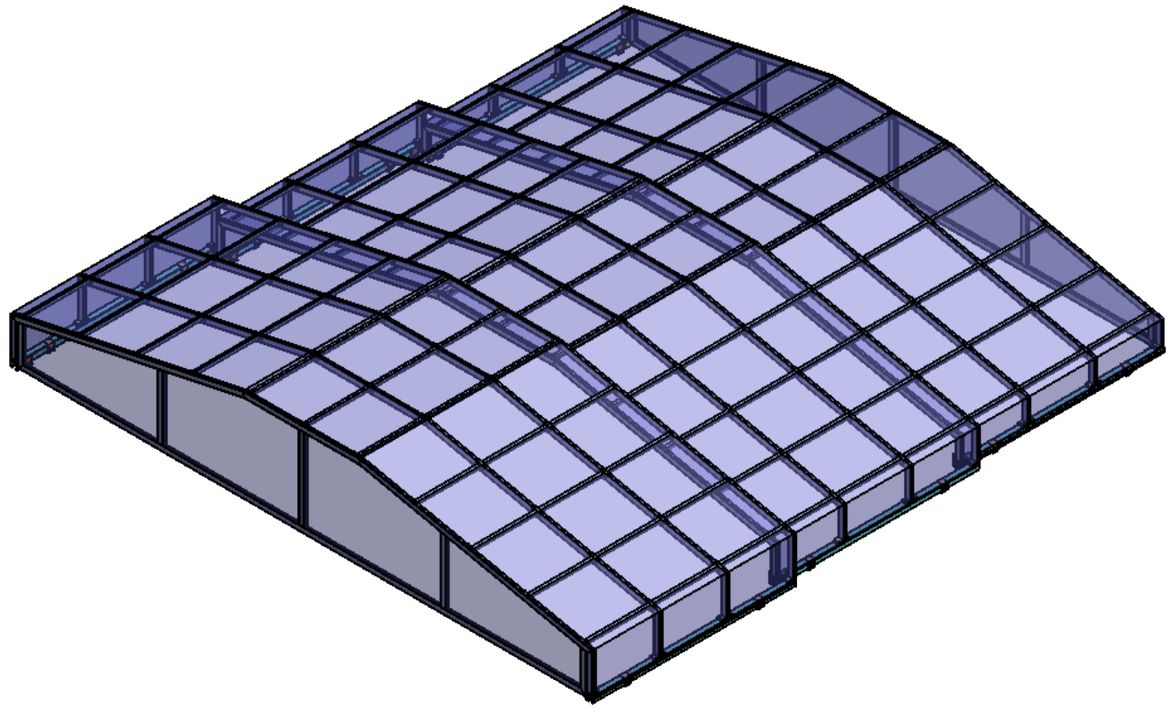



NOTE :- SUB ASM NO. 02
PANEL ASM.


TITLE - ROOF AUTOMATION				NIHVA TECHNOLOGIES PVT.LTD.PUNE
DWG NO - NTPL-281-PM-001-02-00-00				Website - www.nihva.com
	NAME	SIGNATURE	DATE	PROJECT NO - NTPL-281-B-PM
DRAWN	V.G.		25-05-2025	PRODUCT - RETRACTABLE ROOF
CHK'D	S.W.		25-05-2025	SITE LOCATION - AKOLA
APPV'D	V.T.		25-05-2025	
if any queries contact - supportautomation@nihva.com				REVISION - / QTY - 1
ALL DIMENSION ARE IN mm			A3	SCALE - / SHEET 8 OF 41

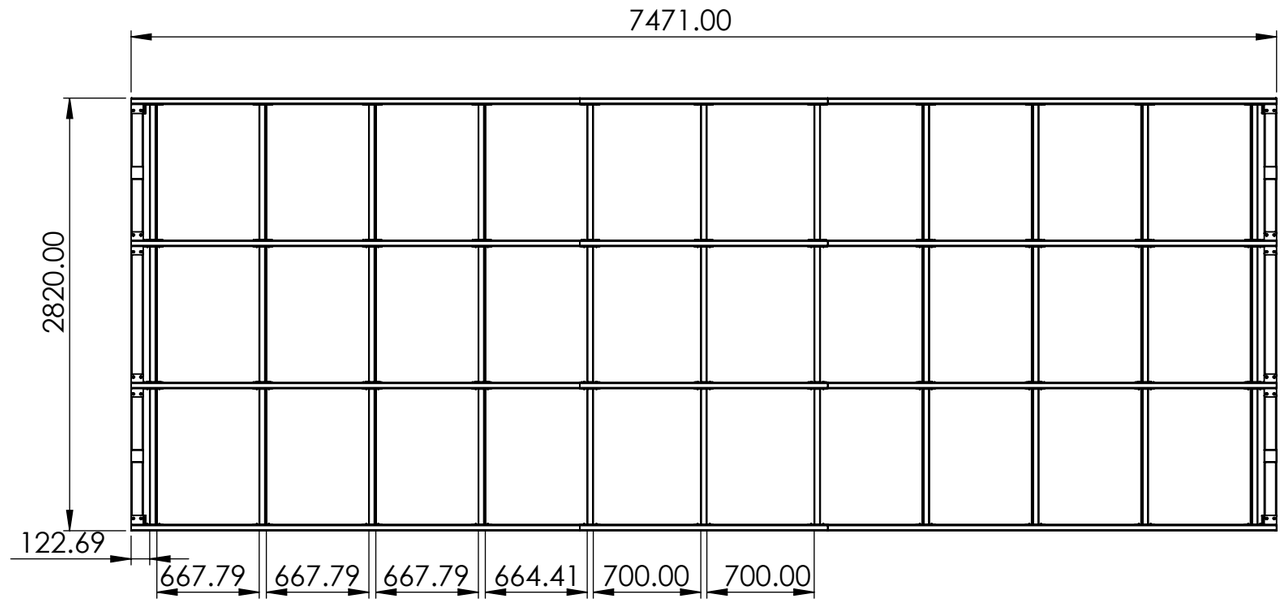


ITEM NO.	PART NUMBER	DESCRIPTION	QTY.
1	R2_REV_APRO PANEL_1		1
2	R2_PANEL BASE		2
3	NP-PLT01_TP	MS - 70X40X10T	4
4	NP-PLT02_TP	MS - 100X90X10T	4
5	NP-PLT03_ TP	MS - 160X100X6T	4
6	NP-PLT04_TP	MS - 100X80X10T	4
7	NP-PLT05_TP	MS - 150X80X10T	4
8	NP-PLT06_TP	MS - 100X80X10T	4
9	NP-PLT07_TP	MS - 150X80X10T	4
10	ROLLER BRG HSG	MS ROLLER BRG HSG	4
11	R2_RIVET AND SUPPORT TUBE ASM		33
12	R2_PANEL 01 SHEET		1
13	R2_REV_APRO PANEL_1 SHEET NEW		1
14	LOCKING PLATE 2	113.42 X 90 X 6 MM THK	4

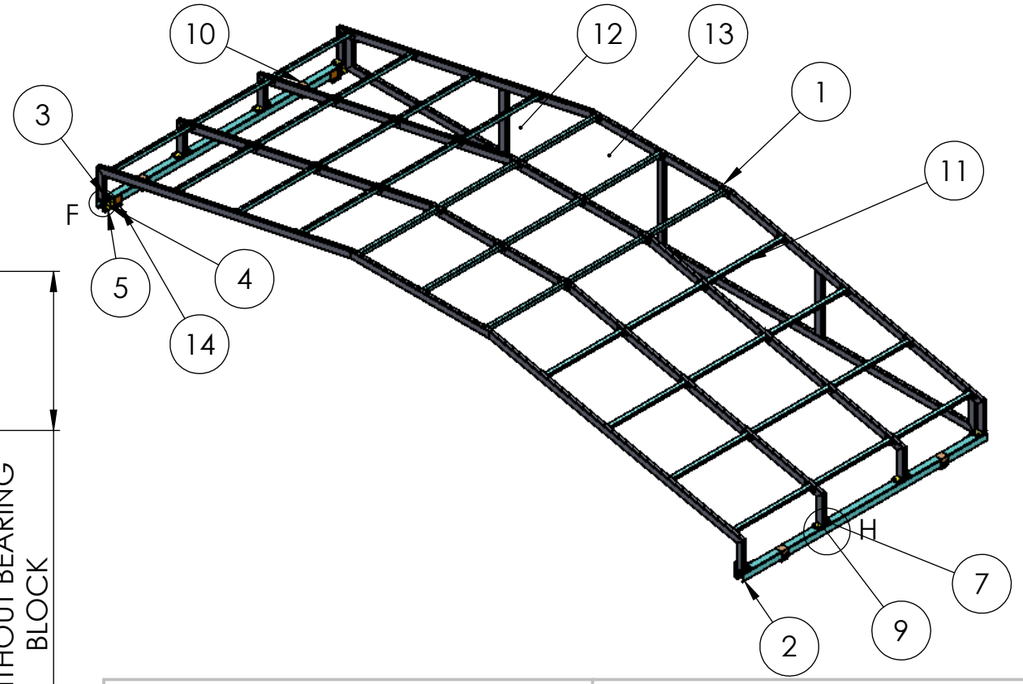

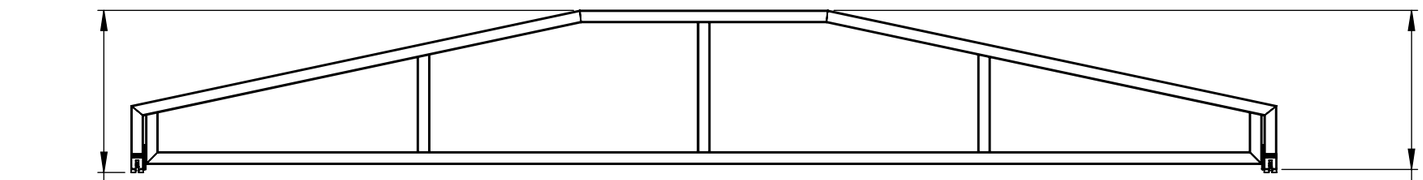

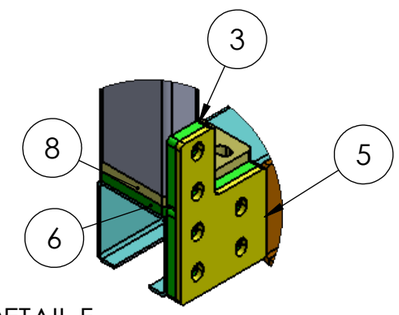

DETAIL F
SCALE 1 : 5

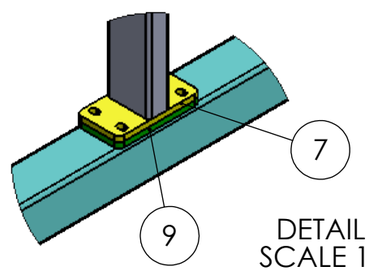


DETAIL H
SCALE 1 : 8


NOTE :- PANEL NO 01 AND FIXED ENCLOSURE ASM.


TITLE - ROOF AUTOMATION				NIHVA TECHNOLOGIES PVT.LTD.PUNE
DWG NO - NTPL-281-PM-001-02-01-00				Website - www.nihva.com
	NAME	SIGNATURE	DATE	PROJECT NO - NTPL-281-B-PM
DRAWN	V.G.		25-05-2025	PRODUCT - RETRACTABLE ROOF
CHK'D	S.W.		25-05-2025	SITE LOCATION - AKOLA
APPV'D	V.T.		25-05-2025	
if any queries contact - supportautomation@nihva.com				REVISION - / QTY - 1
ALL DIMENSION ARE IN mm			A3	SCALE - / SHEET 9 OF 41

ITEM NO.	PART NUMBER	DESCRIPTION	QTY.
1	R2_PANEL_01		1




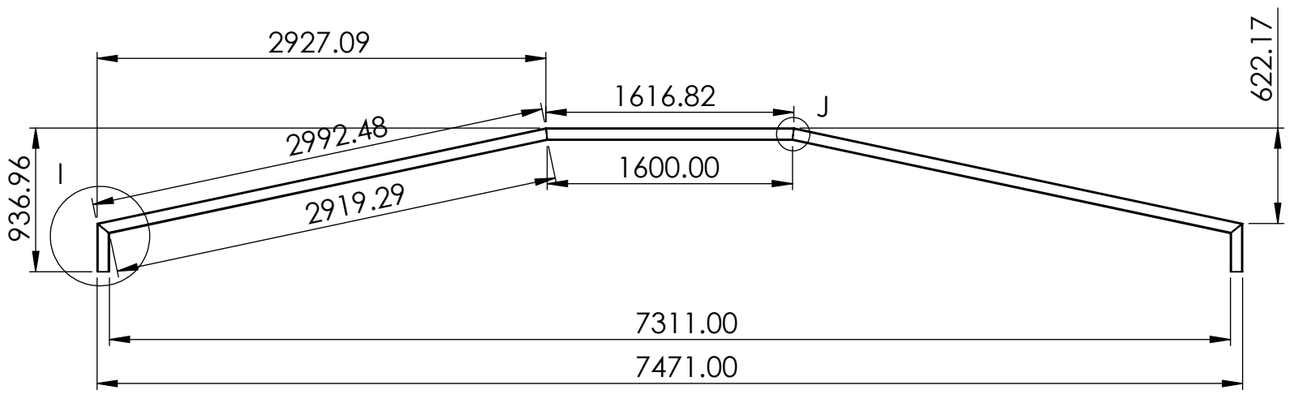

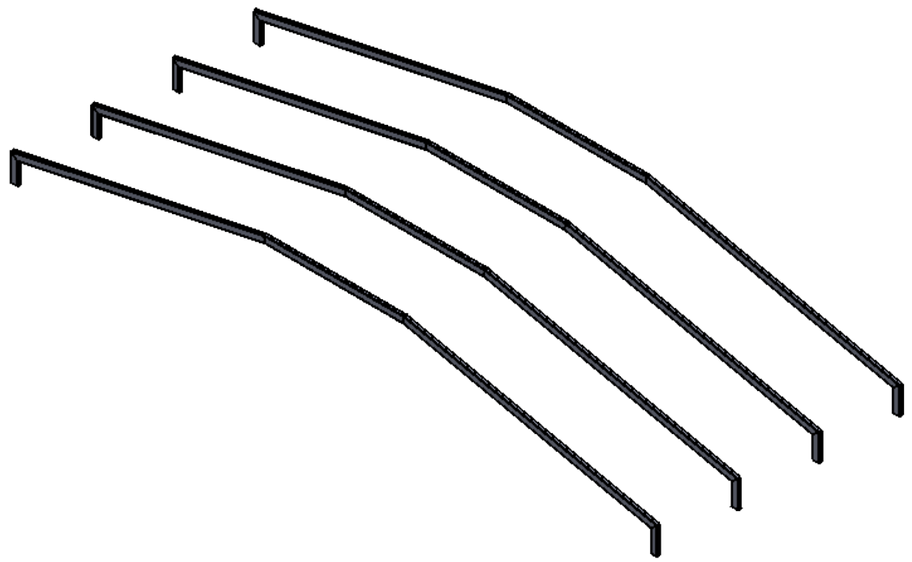

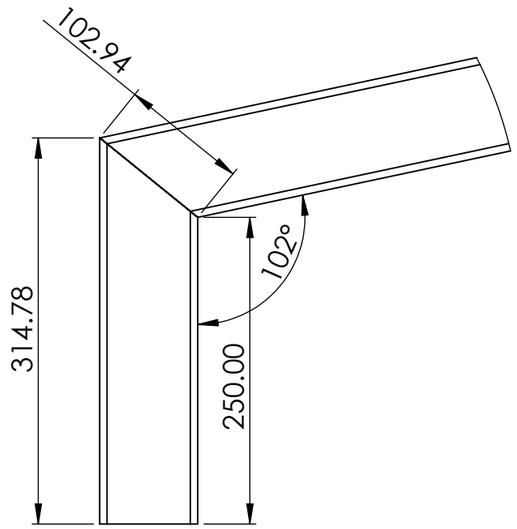

DETAIL I
SCALE 1 : 5

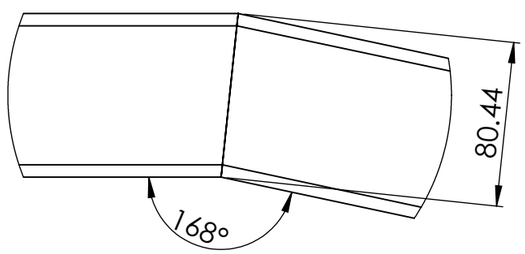



DETAIL J
SCALE 1 : 3

NOTE :- PANEL NO 01

TITLE - ROOF AUTOMATION				NIHVA TECHNOLOGIES PVT.LTD.PUNE
DWG NO - NTPL-281-PM-001-02-001-01				Website - www.nihva.com
	NAME	SIGNATURE	DATE	PROJECT NO - NTPL-281-B-PM
DRAWN	V.G.		25-05-2025	PRODUCT - RETRACTABLE ROOF
CHK'D	S.W.		25-05-2025	SITE LOCATION - AKOLA
APPV'D	V.T.		25-05-2025	
if any queries contact - supportautomation@nihva.com				REVISION - QTY - 1
ALL DIMENSION ARE IN mm		A3		SCALE - SHEET 10 OF 41


ITEM NO.	PART NUMBER	DESCRIPTION	QTY.
1	R2_PANEL_01 FIXED ENCLOSURE		1

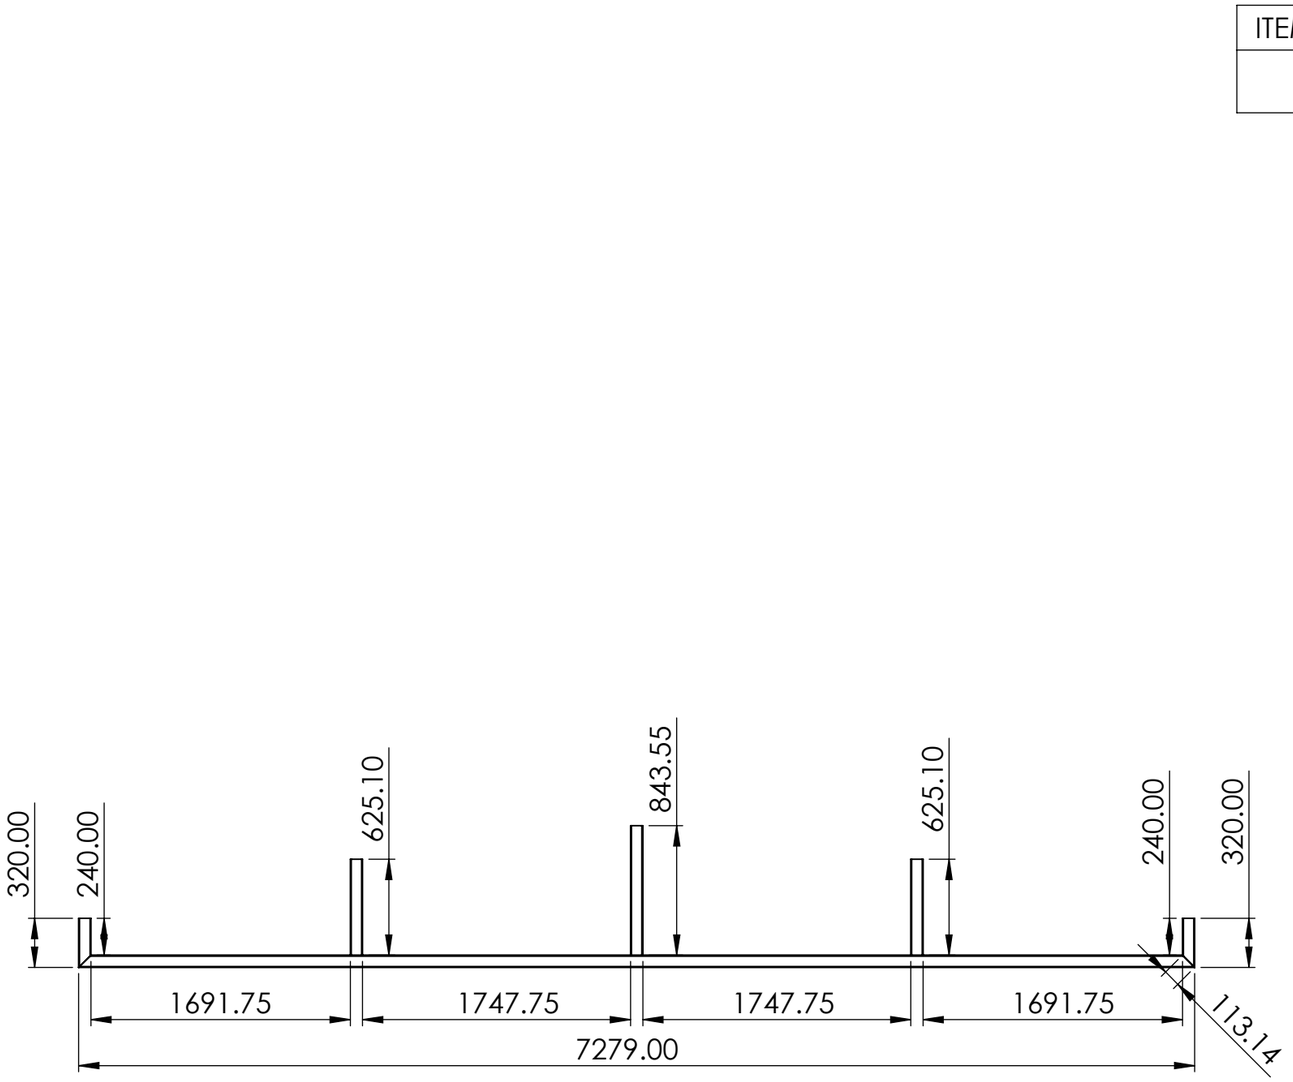

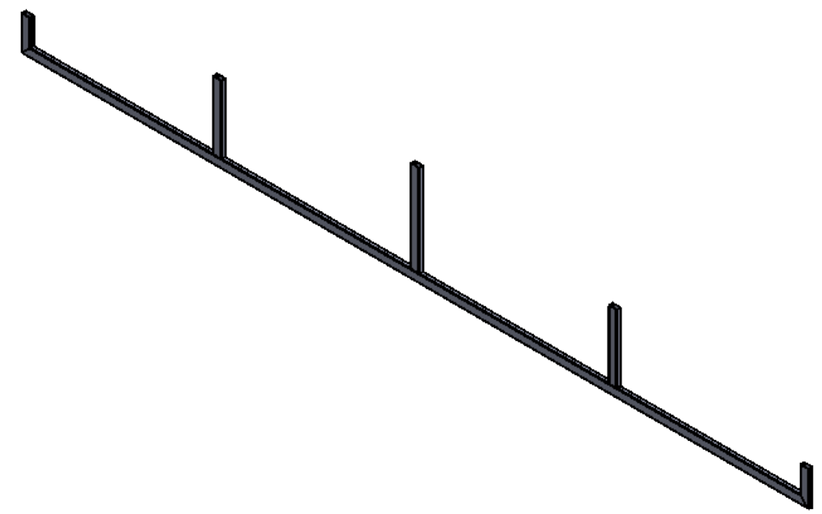



NOTE :- PANEL NO 01
FIXED ENCLOSURE

TITLE - ROOF AUTOMATION				NIHVA TECHNOLOGIES PVT.LTD.PUNE
DWG NO - NTPL-281-PM-001-02-01-02				Website - www.nihva.com
	NAME	SIGNATURE	DATE	PROJECT NO - NTPL-281-B-PM
DRAWN	V.G.		25-05-2025	PRODUCT - RETRACTABLE ROOF
CHK'D	S.W.		25-05-2025	SITE LOCATION - AKOLA
APPV'D	V.T.		25-05-2025	
if any queries contact - supportautomation@nihva.com				REVISION - QTY - 1
ALL DIMENSION ARE IN mm			A3	SCALE - SHEET 11 OF 41

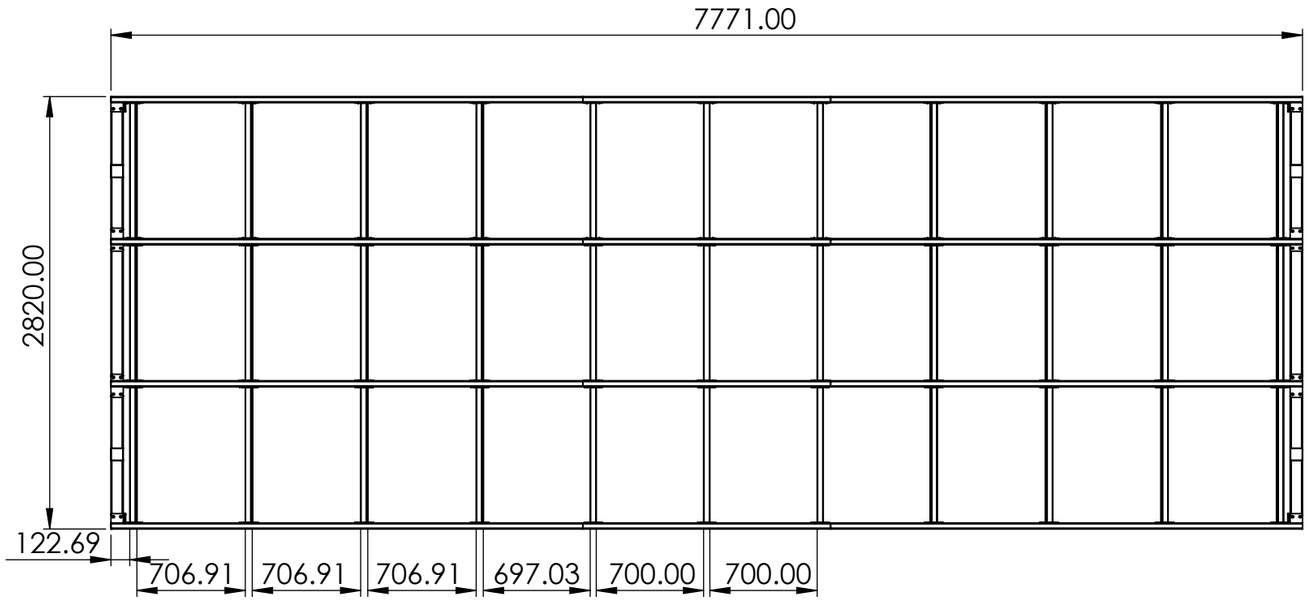

ITEM NO.	PART NUMBER	DESCRIPTION	QTY.
1	R2_REV_BPRO PANEL_2		1
2	R2_PANEL BASE		2
3	NP-PLT01_TP	MS - 70X40X10T	4
4	NP-PLT02_TP	MS - 100X90X10T	4
5	NP-PLT03_ TP	MS - 160X100X6T	4
6	NP-PLT04_TP	MS - 100X80X10T	4
7	NP-PLT05_TP	MS - 150X80X10T	4
8	NP-PLT06_TP	MS - 100X80X10T	4
9	NP-PLT07_TP	MS - 150X80X10T	4
10	ROLLER BRG HSG	MS ROLLER BRG HSG	4
11	R2_RIVET AND SUPPORT TUBE ASM		33
12	R2_PANEL 02 SHEET		1
14	LOCKING PLATE 2	113.42 X 90 X 6 MM THK	4

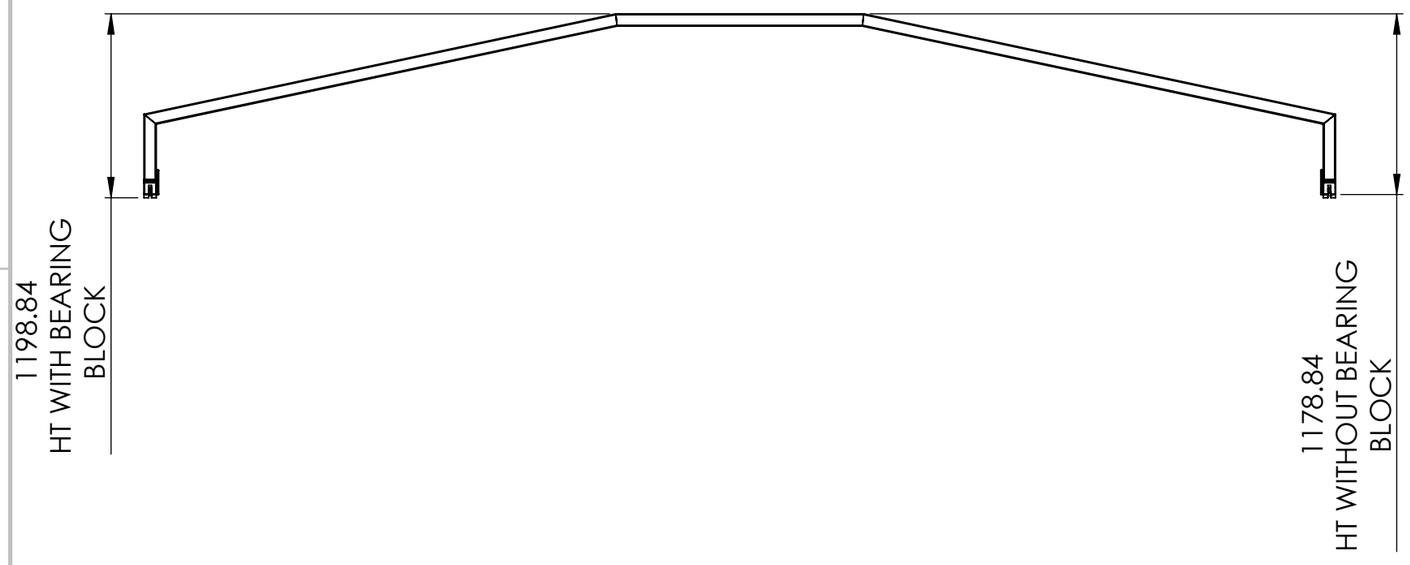

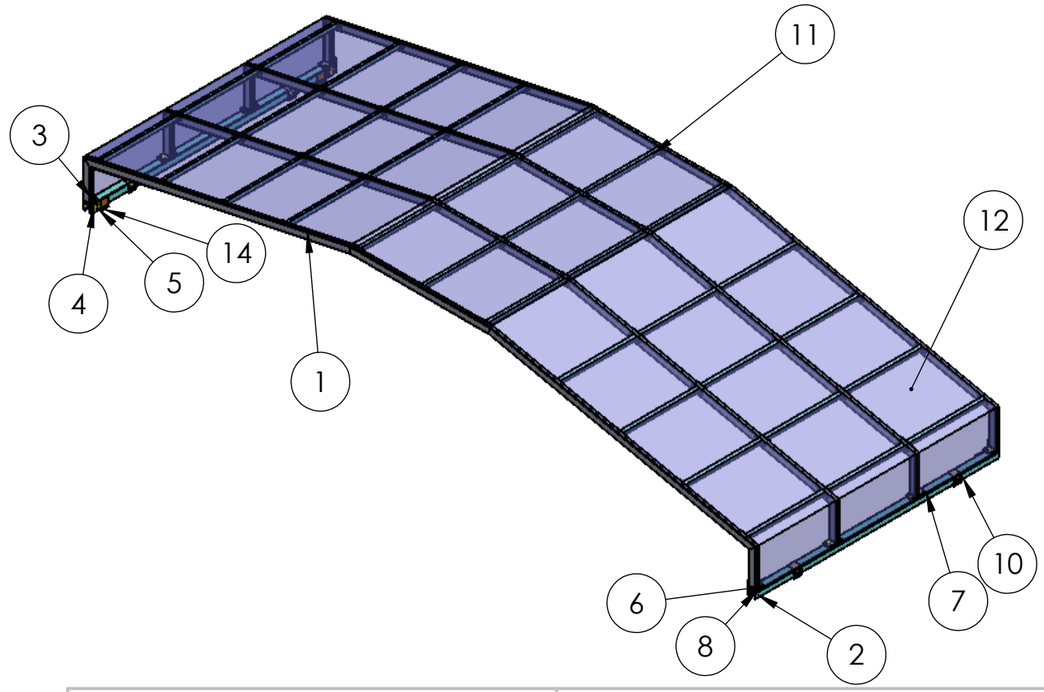



NOTE :- PANEL NO 02 ASM.


TITLE - ROOF AUTOMATION				NIHVA TECHNOLOGIES PVT.LTD.PUNE
DWG NO - NTPL-281-PM-001-02-02-00				Website - www.nihva.com
	NAME	SIGNATURE	DATE	PROJECT NO - NTPL-281-B-PM
DRAWN	V.G.		25-05-2025	PRODUCT - RETRACTABLE ROOF
CHK'D	S.W.		25-05-2025	SITE LOCATION - AKOLA
APPV'D	V.T.		25-05-2025	
if any queries contact - supportautomation@nihva.com				REVISION - / QTY - 1
ALL DIMENSION ARE IN mm			A3	SCALE - / SHEET 12 OF 41

ITEM NO.	PART NUMBER	DESCRIPTION	QTY.
1	R2_REV_BPRO PANEL_2		1




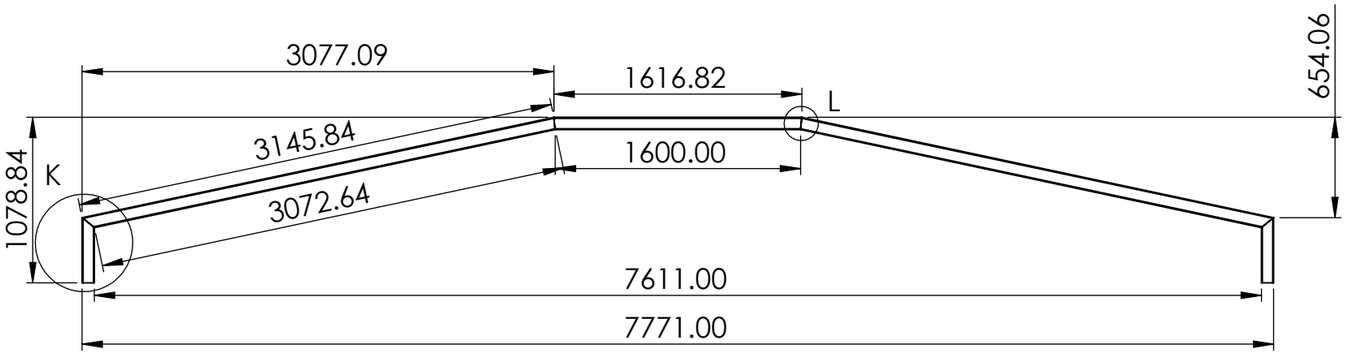

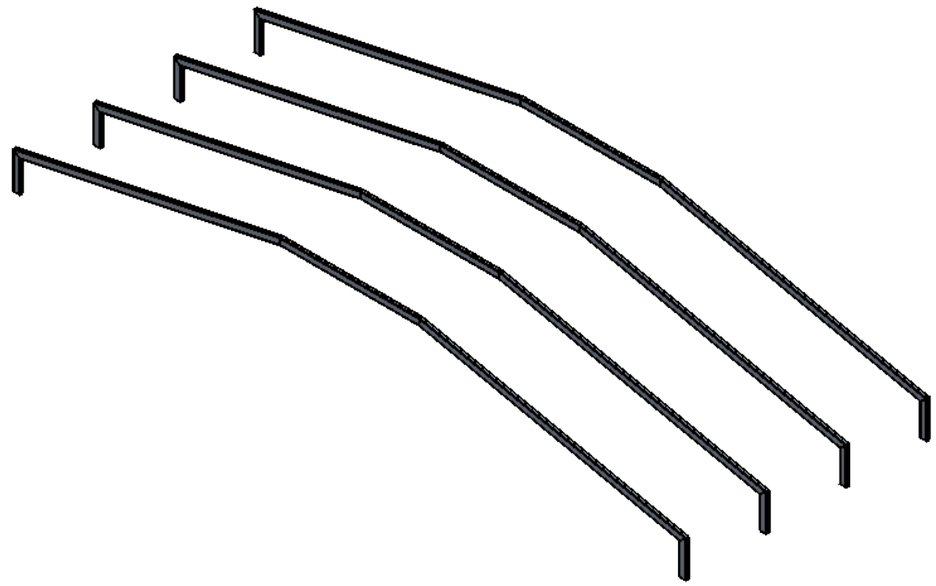

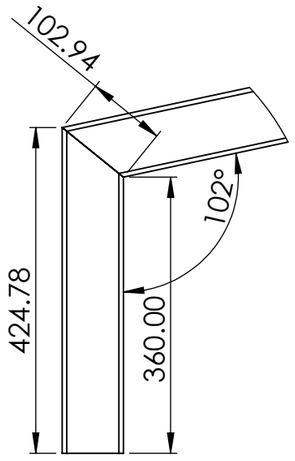


DETAIL K
SCALE 1 : 8

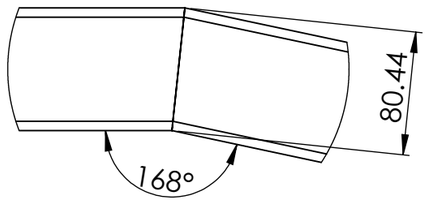


DETAIL L
SCALE 1 : 4


NOTE :- PANEL NO 02

TITLE - ROOF AUTOMATION				NIHVA TECHNOLOGIES PVT.LTD.PUNE
DWG NO - NTPL-281-PM-001-02-02-01				Website - www.nihva.com
	NAME	SIGNATURE	DATE	PROJECT NO - NTPL-281-B-PM
DRAWN	V.G.		25-05-2025	PRODUCT - RETRACTABLE ROOF
CHK'D	S.W.		25-05-2025	SITE LOCATION - AKOLA
APPV'D	V.T.		25-05-2025	
if any queries contact - supportautomation@nihva.com				REVISION - / QTY - 1
ALL DIMENSION ARE IN mm			A3	SCALE - / SHEET 13 OF 41

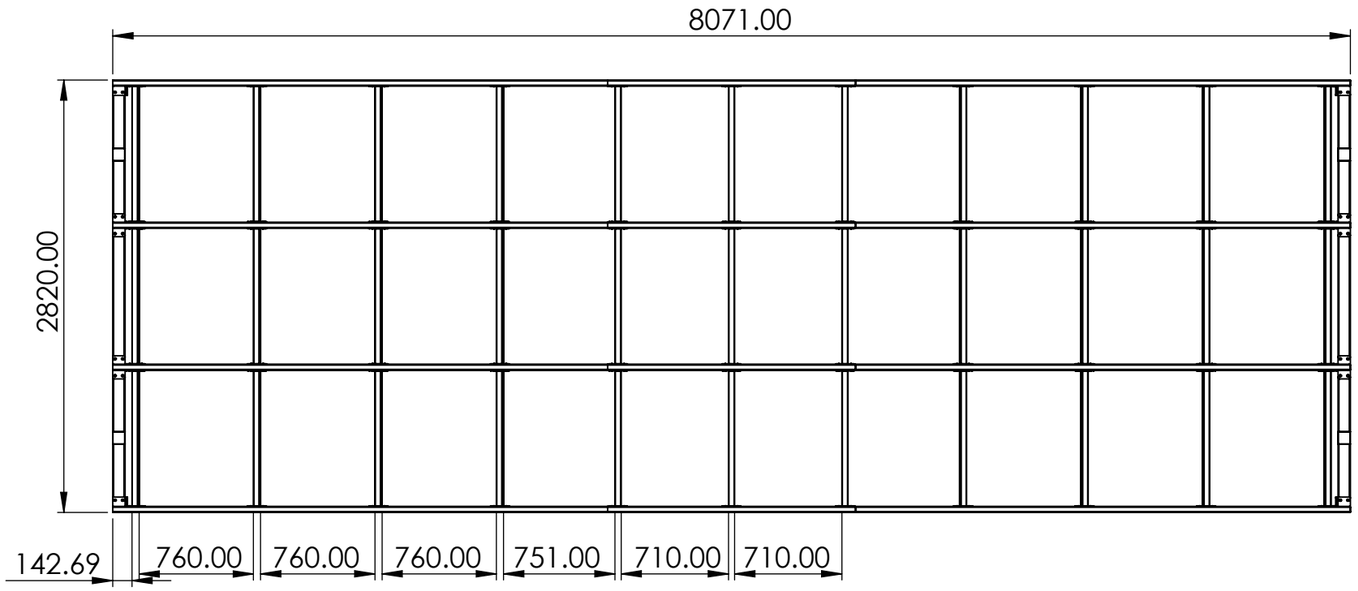

ITEM NO.	PART NUMBER	DESCRIPTION	QTY.
1	DPRO PANEL_3		1
2	R2_PANEL BASE		2
5	NP-PLT01_TP	MS - 70X40X10T	4
6	NP-PLT02_TP	MS - 100X90X10T	4
7	NP-PLT03_ TP	MS - 160X100X6T	4
8	NP-PLT04_TP	MS - 100X80X10T	4
7	NP-PLT05_TP	MS - 150X80X10T	4
8	NP-PLT06_TP	MS - 100X80X10T	4
9	NP-PLT07_TP	MS - 150X80X10T	4
10	ROLLER BRG HSG	MS ROLLER BRG HSG	4
11	R2_RIVET AND SUPPORT TUBE ASM		33
12	PANEL 03 SHEET		1
13	REV_DPRO PANEL_3 SHEET NEW		1
14	LOCKING PLATE 2	113.42 X 90 X 6 MM THK	4

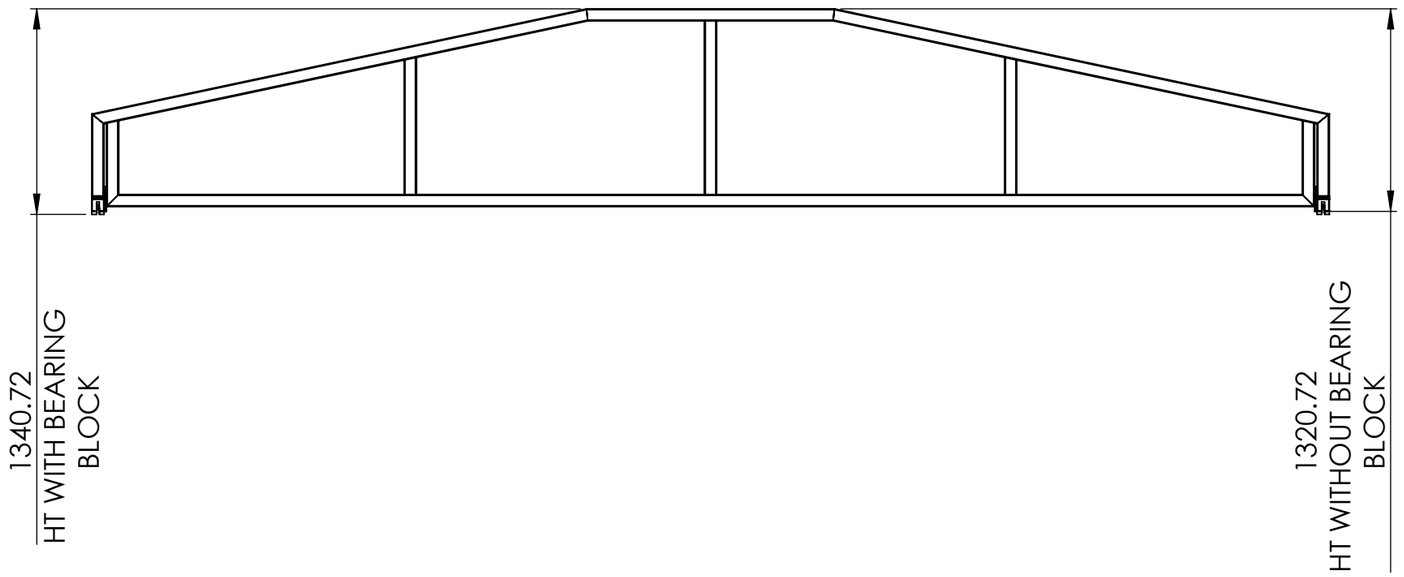


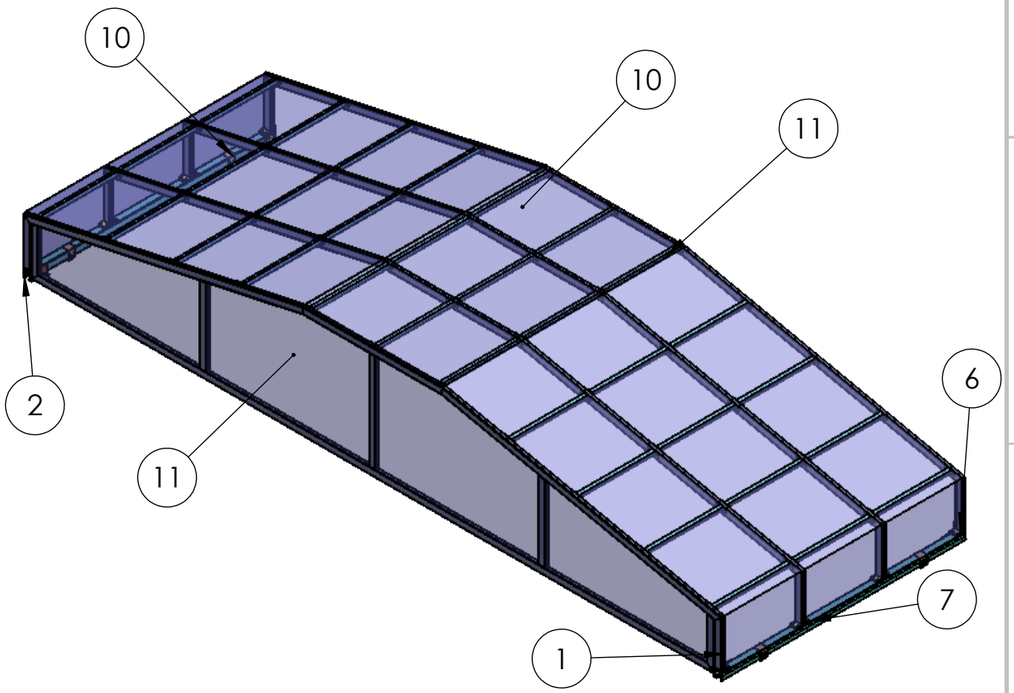


NOTE :- PANEL NO 03 AND FIXED ENCLOSURE ASM.


TITLE - ROOF AUTOMATION				NIHVA TECHNOLOGIES PVT.LTD.PUNE
DWG NO - NTPL-281-PM-001-02-03-00				Website - www.nihva.com
	NAME	SIGNATURE	DATE	PROJECT NO - NTPL-281-B-PM
DRAWN	V.G.		25-05-2025	PRODUCT - RETRACTABLE ROOF
CHK'D	S.W.		25-05-2025	SITE LOCATION - AKOLA
APPV'D	V.T.		25-05-2025	
if any queries contact - supportautomation@nihva.com				REVISION - QTY - 1
ALL DIMENSION ARE IN mm			A3	SCALE - SHEET 14 OF 41

ITEM NO.	PART NUMBER	DESCRIPTION	QTY.
1	DPRO PANEL_3		1

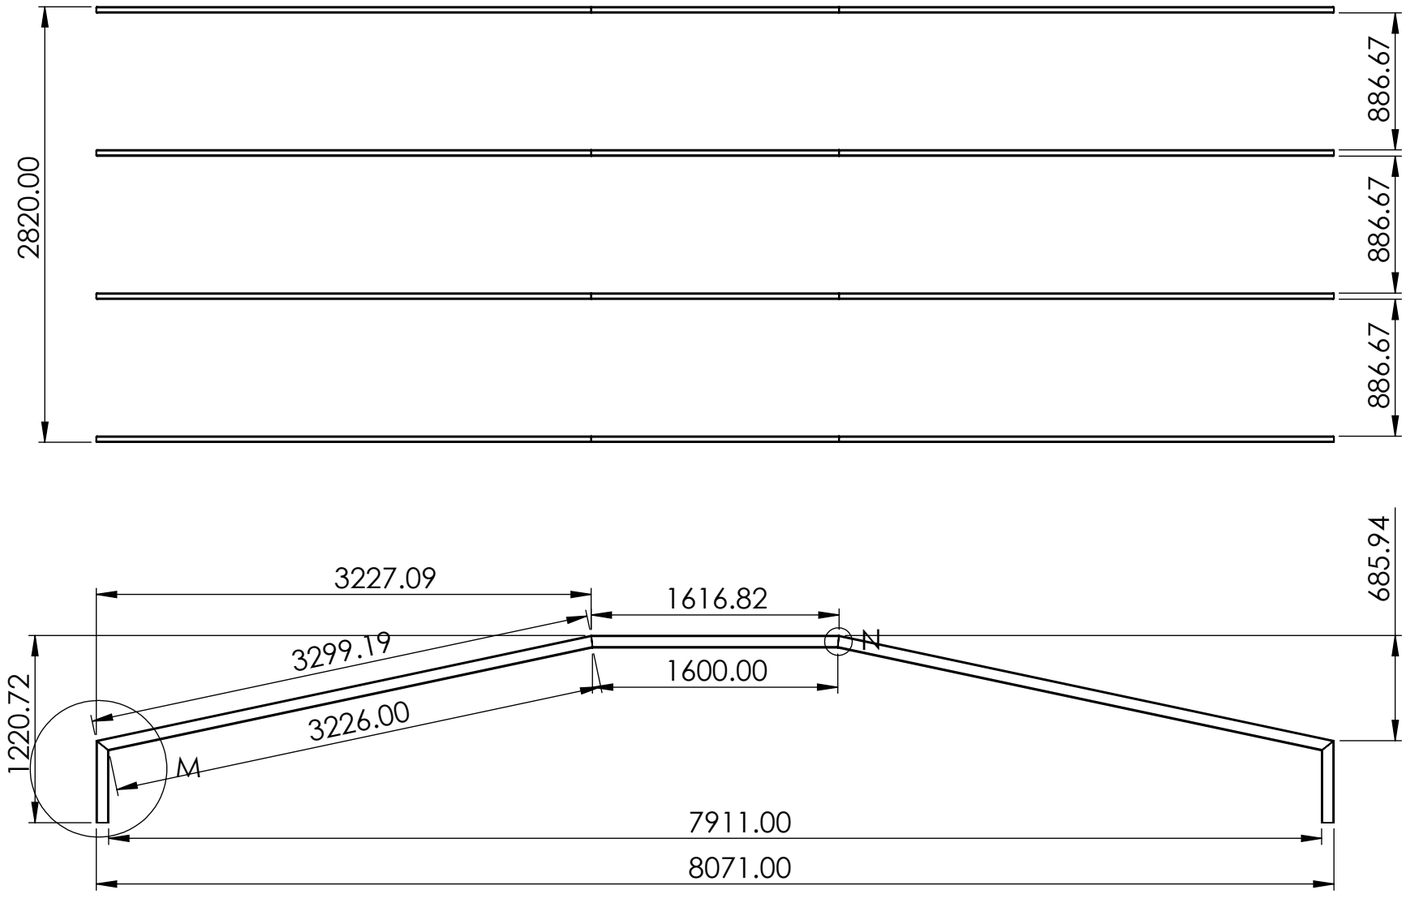


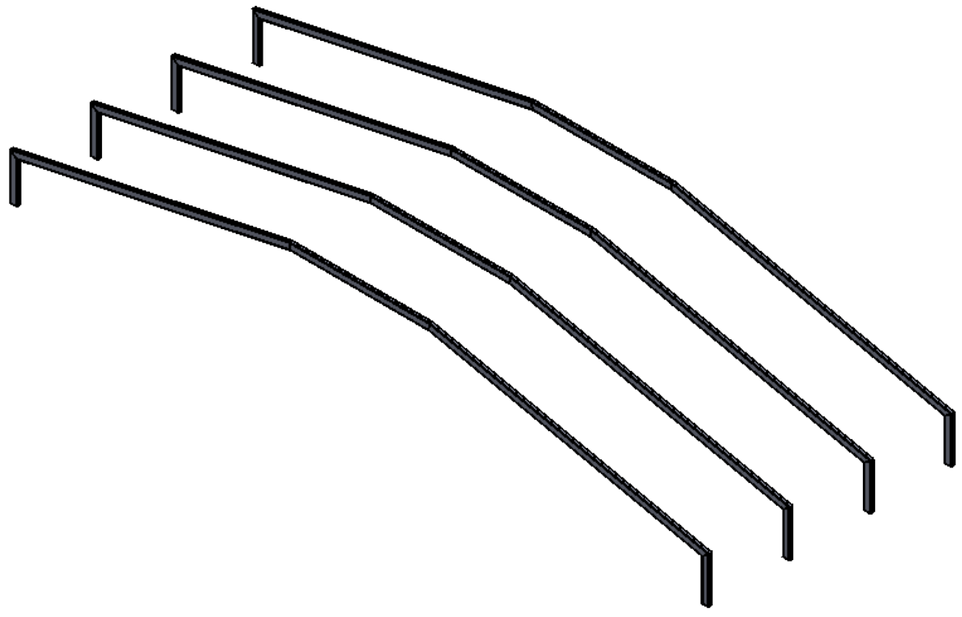

NOTE :- PANEL NO 03

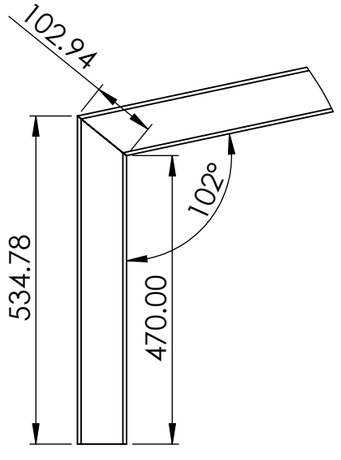


DETAIL M
SCALE 1 : 10

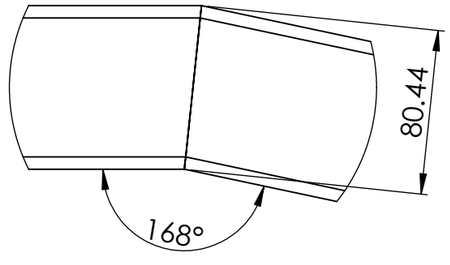


DETAIL N
SCALE 1 : 3

TITLE - ROOF AUTOMATION				NIHVA TECHNOLOGIES PVT.LTD.PUNE
DWG NO - NTPL-281-PM-001-02-03-01				Website - www.nihva.com
	NAME	SIGNATURE	DATE	PROJECT NO - NTPL-281-B-PM
DRAWN	V.G.		25-05-2025	PRODUCT - RETRACTABLE ROOF
CHK'D	S.W.		25-05-2025	SITE LOCATION - AKOLA
APPV'D	V.T.		25-05-2025	
if any queries contact - supportautomation@nihva.com				REVISION - / QTY - 1
ALL DIMENSION ARE IN mm			A3	SCALE - / SHEET 15 OF 41

ITEM NO.	PART NUMBER	DESCRIPTION	QTY.
1	PANEL_03 FIXED ENCLOSURE		1

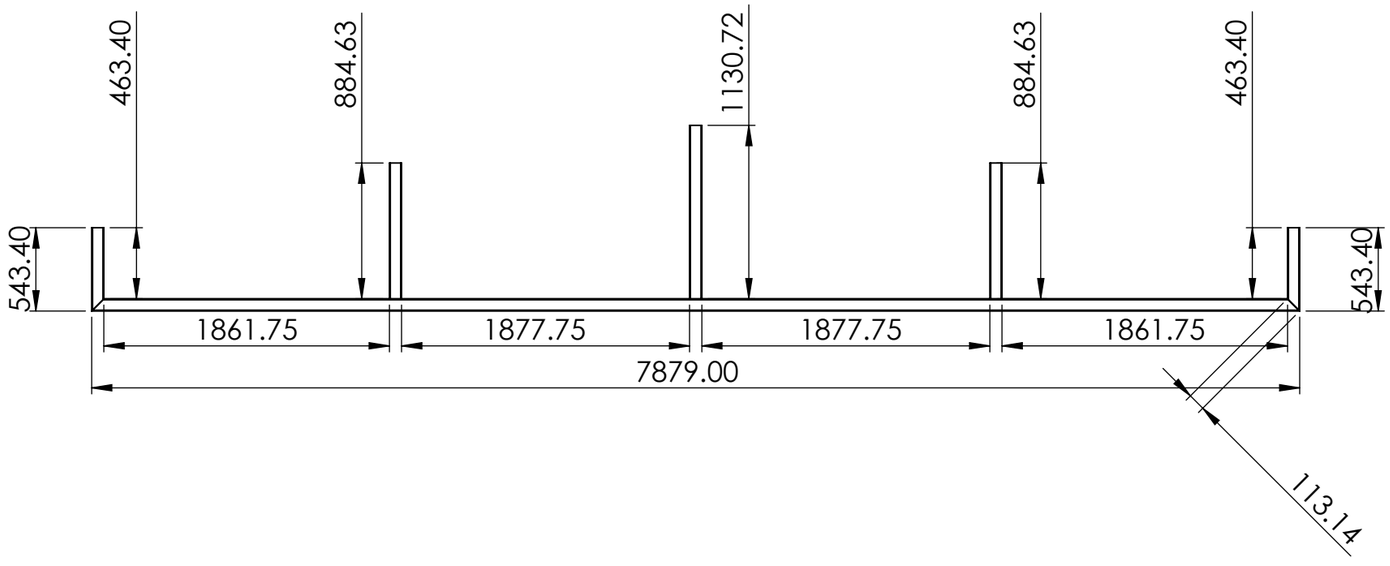


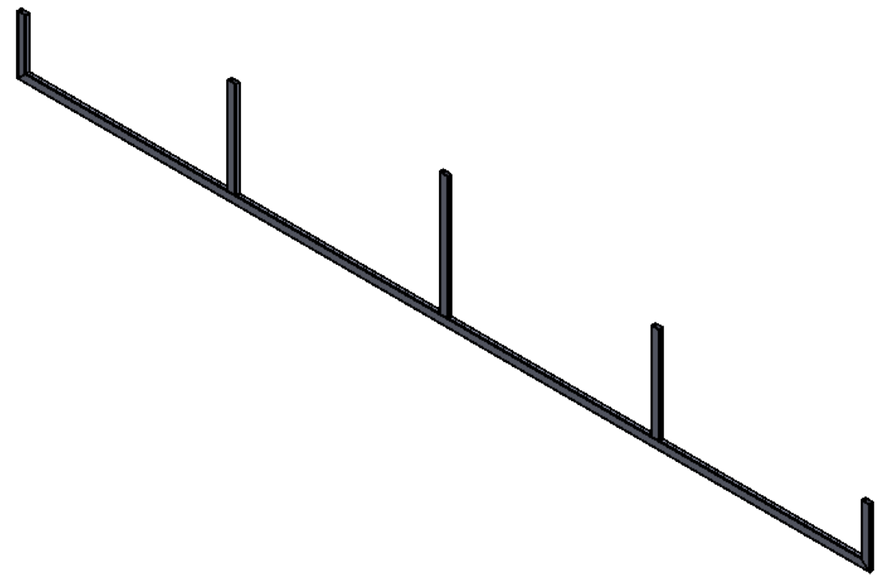



NOTE :- PANEL NO 03
FIXED ENCLOSURE

TITLE - ROOF AUTOMATION				NIHVA TECHNOLOGIES PVT.LTD.PUNE
DWG NO - NTPL-281-PM-001-02-03-02				Website - www.nihva.com
	NAME	SIGNATURE	DATE	PROJECT NO - NTPL-281-B-PM
DRAWN	V.G.		25-05-2025	PRODUCT - RETRACTABLE ROOF
CHK'D	S.W.		25-05-2025	SITE LOCATION - AKOLA
APPV'D	V.T.		25-05-2025	
if any queries contact - supportautomation@nihva.com				REVISION - QTY - 1
ALL DIMENSION ARE IN mm			A3	SCALE - SHEET 16 OF 41

ITEM NO.	PART NUMBER	DESCRIPTION	QTY.
1	R2_PANEL BASE		2

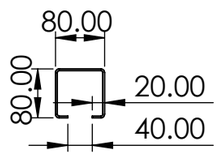


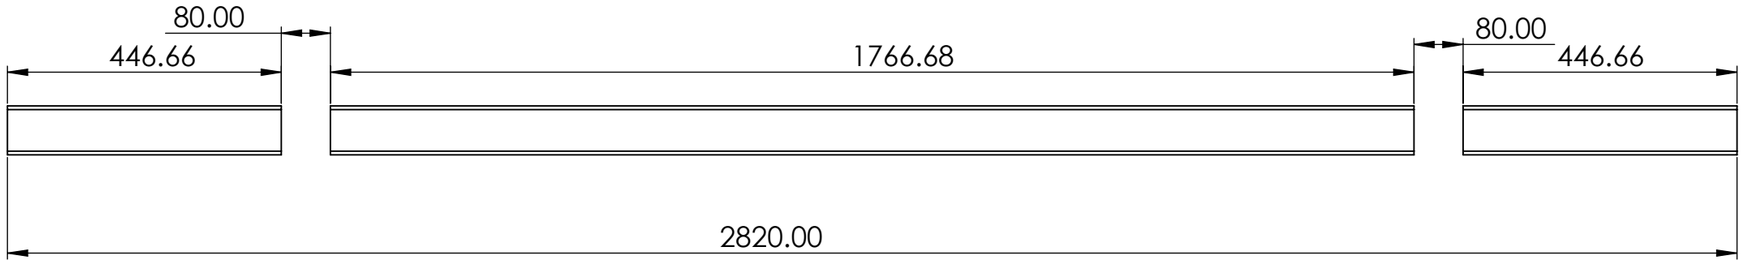


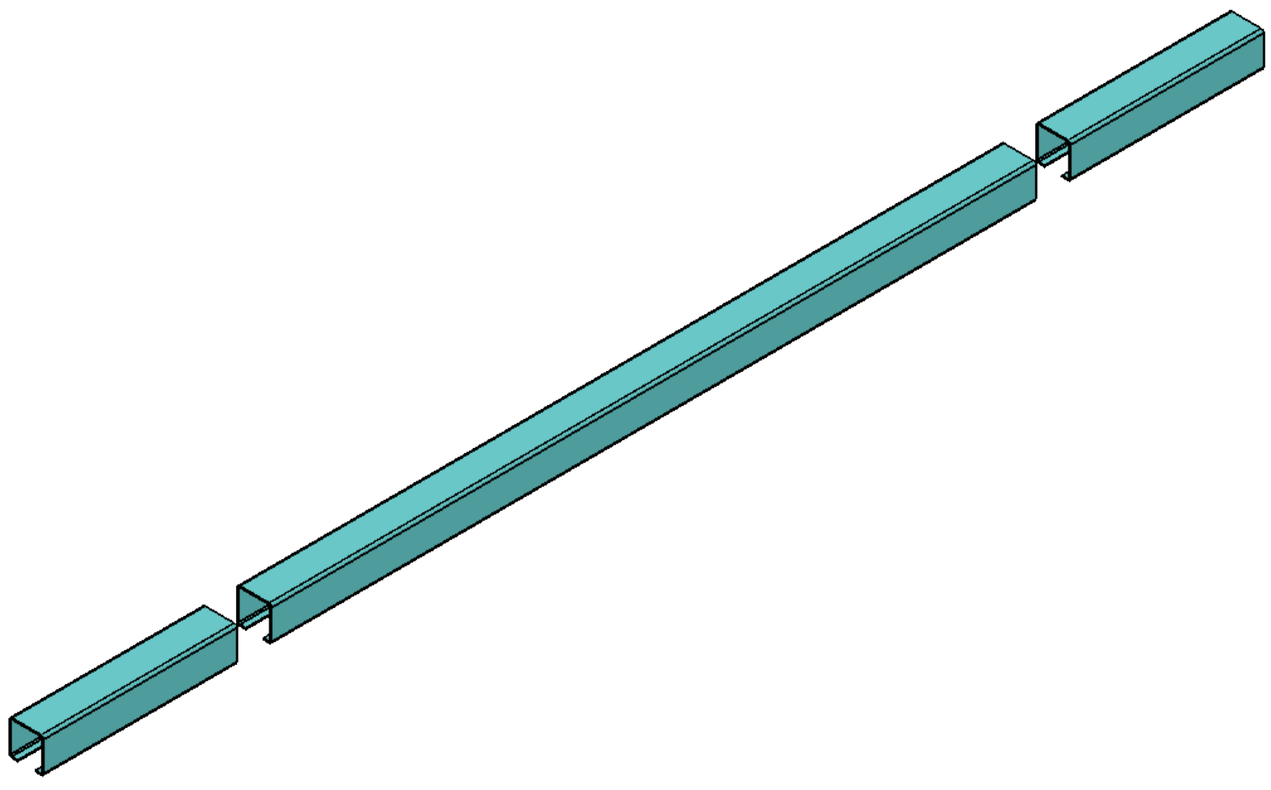


TITLE - ROOF AUTOMATION				NIHVA TECHNOLOGIES PVT.LTD.PUNE Website - www.nihva.com
DWG NO - NTPL-281-PM-001-02-01-03				
	NAME	SIGNATURE	DATE	PROJECT NO - NTPL-281-B-PM
DRAWN	V.G.		25-05-2025	PRODUCT - RETRACTABLE ROOF
CHK'D	S.W.		25-05-2025	SITE LOCATION - AKOLA
APPV'D	V.T.		25-05-2025	
if any queries contact - supportautomation@nihva.com				REVISION - QTY - 1
ALL DIMENSION ARE IN mm			A3	SCALE - SHEET 17 OF 41

ITEM NO.	PART NUMBER	DESCRIPTION	QTY.
1	SUPPORTING TUBES		33
2	R2_APRACTICE rivet_iso_15977_4_x_16_0	RIVET M4X16	132

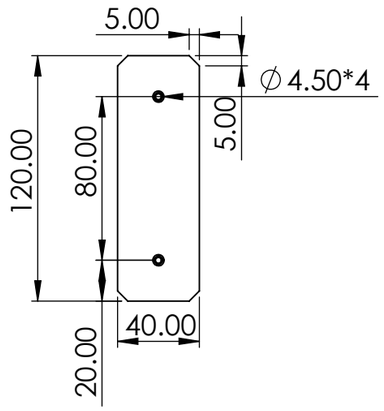

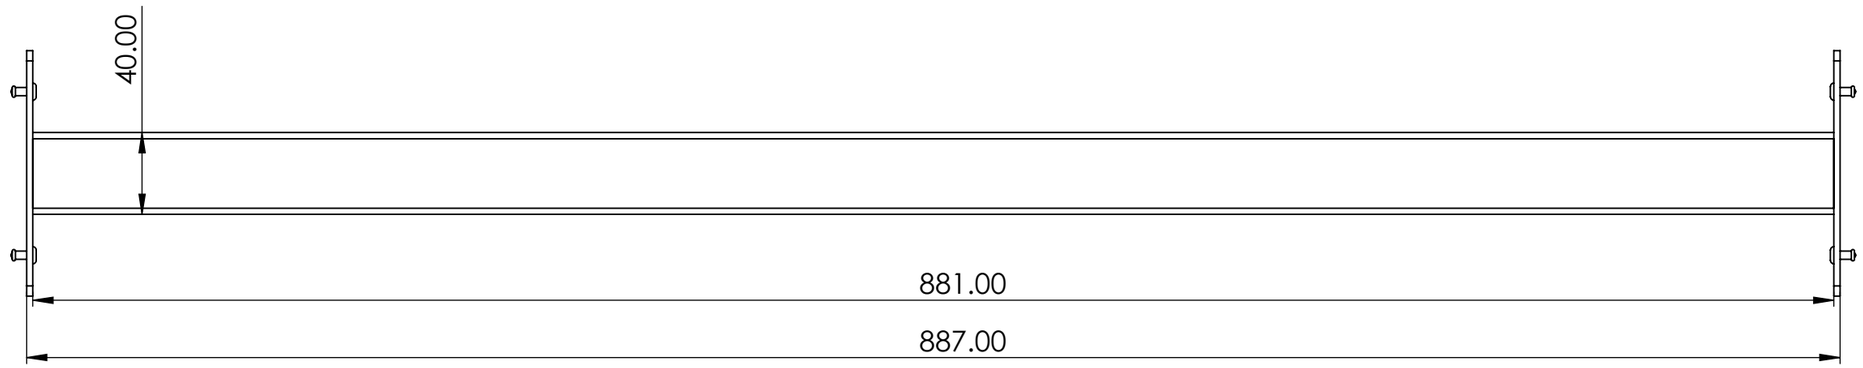


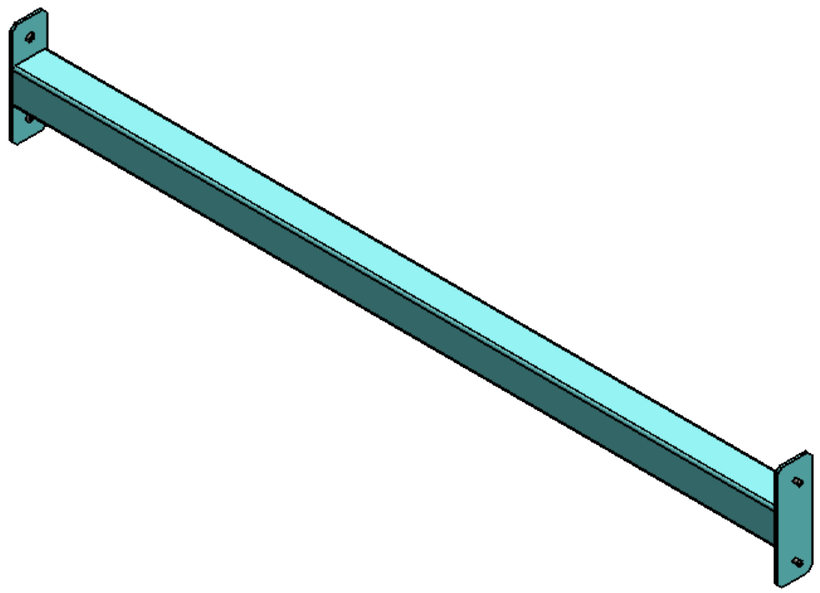



NOTE :- INTERMEDIATE SUPPORT TUBE
ONE PANEL QTY REQ.-33
TOTAL REQ.-99
TOTAL RIVET REQ.-400


TITLE - ROOF AUTOMATION				NIHVA TECHNOLOGIES PVT.LTD.PUNE
DWG NO - NTPL-281-PM-001-02-01-04				Website - www.nihva.com
	NAME	SIGNATURE	DATE	PROJECT NO - NTPL-281-B-PM
DRAWN	V.G.		25-05-2025	PRODUCT - RETRACTABLE ROOF
CHK'D	S.W.		25-05-2025	SITE LOCATION - AKOLA
APPV'D	V.T.		25-05-2025	
if any queries contact - supportautomation@nihva.com				REVISION - / QTY - 1
ALL DIMENSION ARE IN mm			A3	SCALE - / SHEET 18 OF 41

ITEM NO.	PART NUMBER	DESCRIPTION	QTY.
1	ROLLER BRG HSG	100X80X80 MM	1
2	SKF_NATR 12	BRG	2
3	SKF_NATR 8	BRG	2
4	C-MSBL12-35.SLDASM	SHOULDER BOLT	2
5	ISO 7379 - 8 x 30 --- N	SHOULDER BOLT	2

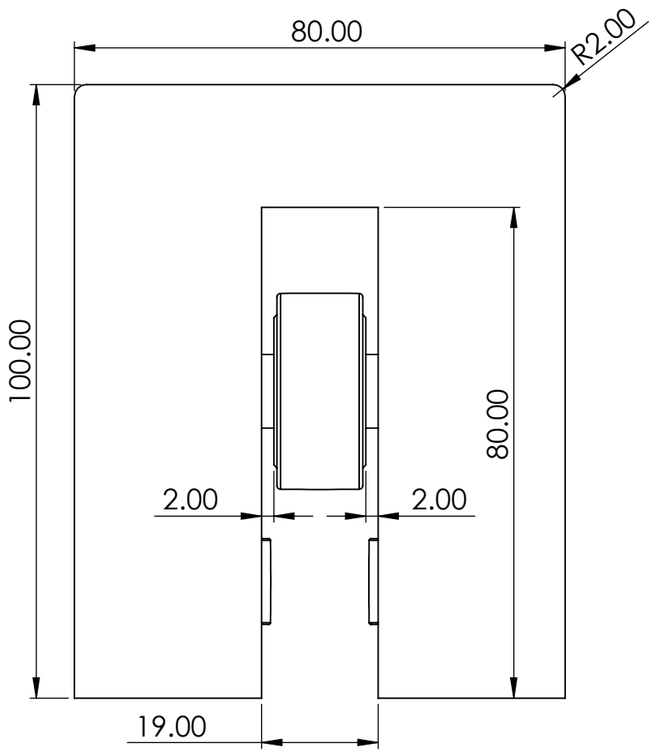

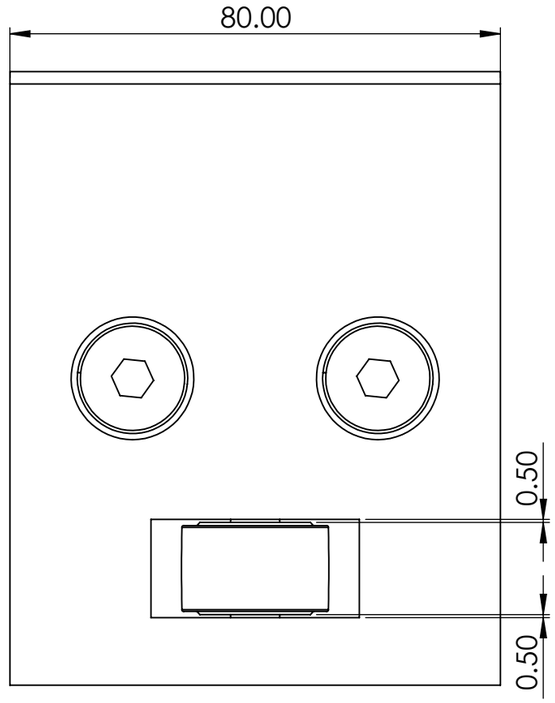

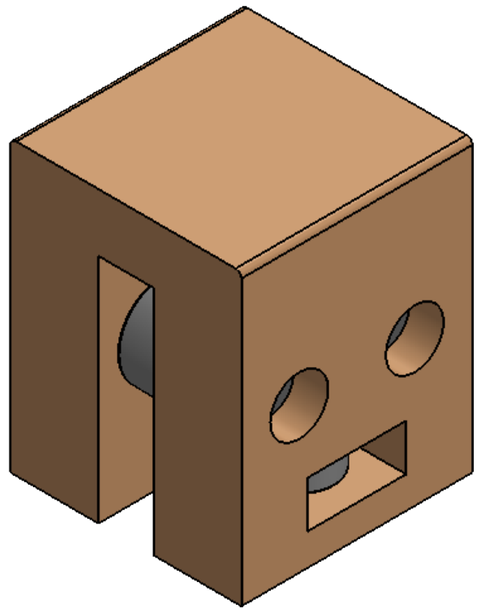


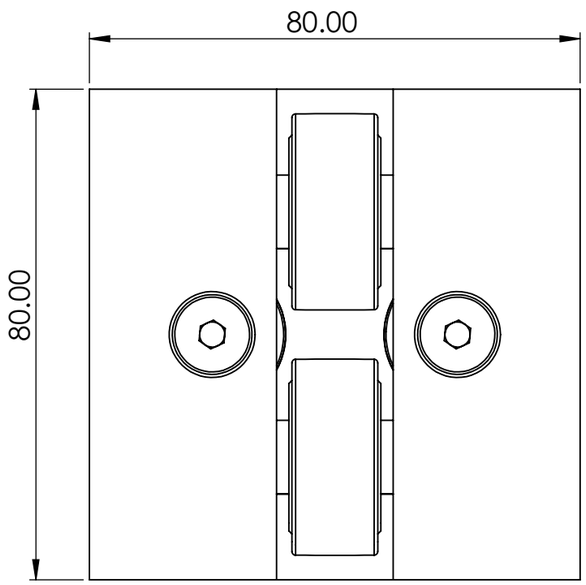



NOTE :- BEARING BLOCK ASM.
THIS ASM. IS USED FOR ALL PANEL
FOR 01 PANEL QTY- 4 REQ.
FOR ALL ASM. QTY-12 REQ.
VMC MACHINING


TITLE - ROOF AUTOMATION				NIHVA TECHNOLOGIES PVT.LTD.PUNE	
DWG NO - NTPL-281-PM-001-02-01-05				Website - www.nihva.com	
	NAME	SIGNATURE	DATE	PROJECT NO - NTPL-281-B-PM	
DRAWN	V.G.		25-05-2025	PRODUCT - RETRACTABLE ROOF	
CHK'D	S.W.		25-05-2025	SITE LOCATION - AKOLA	
APPV'D	V.T.		25-05-2025		
if any queries contact - supportautomation@nihva.com				REVISION -	QTY - 1
ALL DIMENSION ARE IN mm		A3		SCALE -	SHEET 19 OF 41

ITEM NO.	PART NUMBER	DESCRIPTION	QTY.
1	ROLLER BRG HSG	100X80X80 MM	1

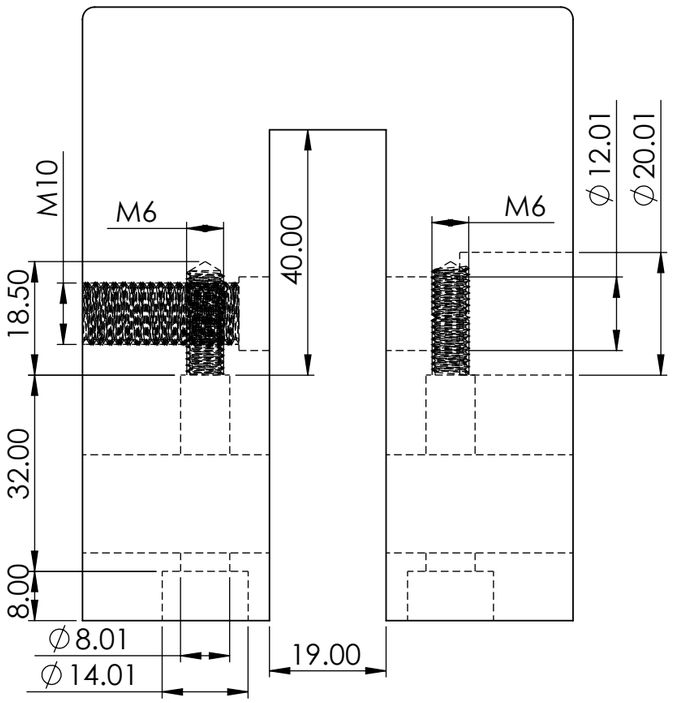

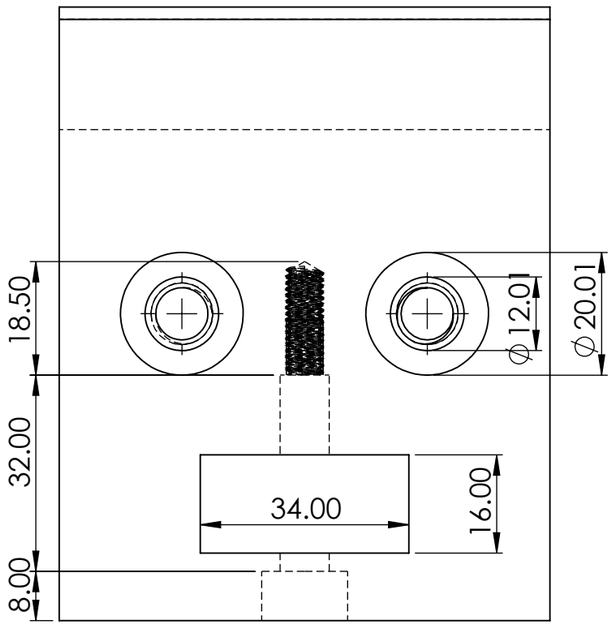

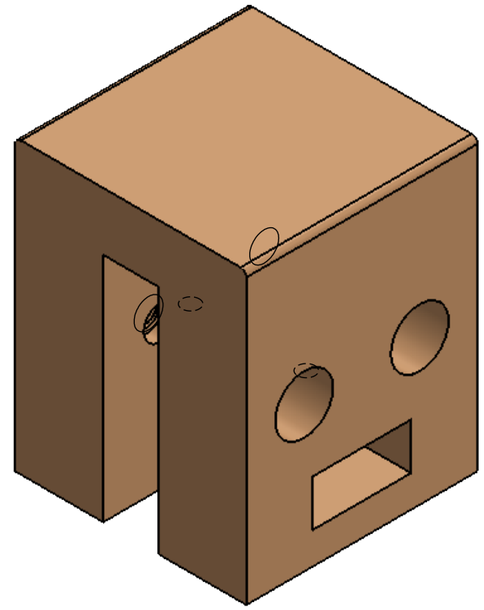


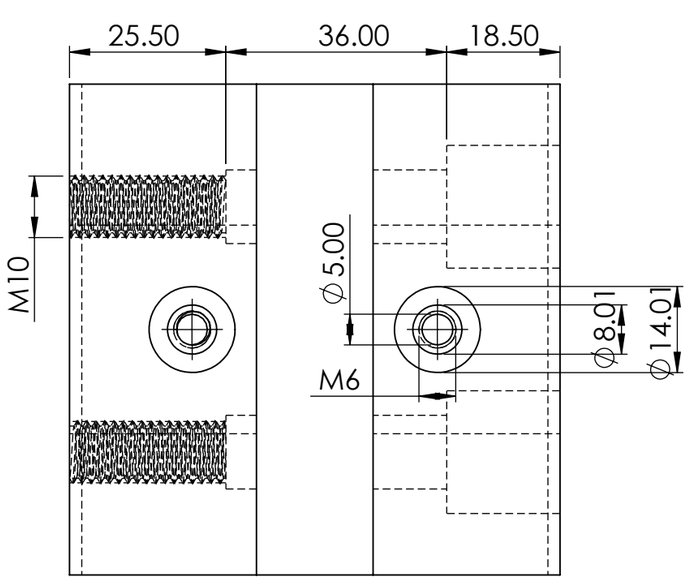



NOTE :- BEARING BLOCK HSG.
THIS HSG. IS USED FOR ALL PANEL
FOR 01 PANEL QTY- 4 REQ.
FOR ALL ASM. QTY-12 REQ.
VMC MACHINING

TITLE - ROOF AUTOMATION				NIHVA TECHNOLOGIES PVT.LTD.PUNE	
DWG NO - NTPL-281-PM-001-02-01-05				Website - www.nihva.com	
	NAME	SIGNATURE	DATE	PROJECT NO - NTPL-281-B-PM	
DRAWN	V.G.		25-05-2025	PRODUCT - RETRACTABLE ROOF	
CHK'D	S.W.		25-05-2025	SITE LOCATION - AKOLA	
APPV'D	V.T.		25-05-2025		
if any queries contact - supportautomation@nihva.com				REVISION -	QTY - 1
ALL DIMENSION ARE IN mm		A3		SCALE -	SHEET 20 OF 41

ITEM NO.	PART NUMBER	DESCRIPTION	QTY.
1	NP-PLT01_TP	MS - 70X40X10T	12

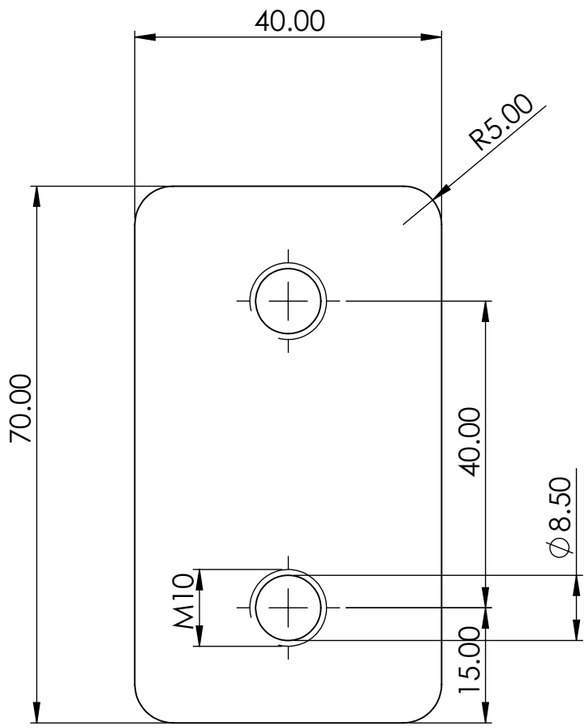

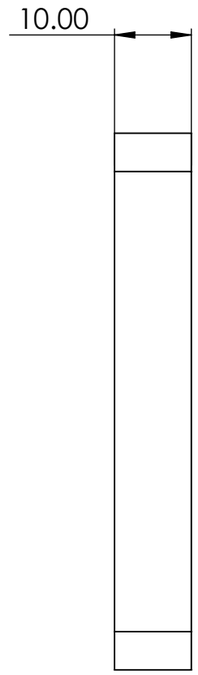

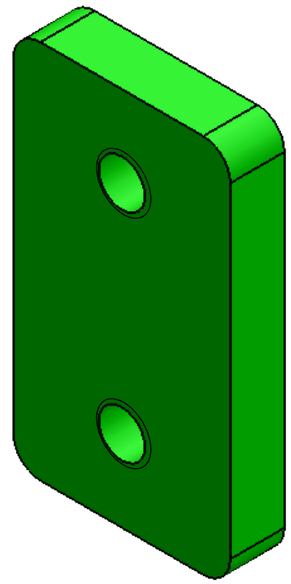



NOTE :- PLATE 01
ALL PANEL THIS PLATE 01 IS USED
LASER CUTTING
THICKNESS - 10 MM

NOTE :- FILLET RADIUS 5 MM SAME FOR ALL CORNERS

TITLE - ROOF AUTOMATION				NIHVA TECHNOLOGIES PVT.LTD.PUNE
DWG NO - NTPL-281-PM-001-02-01-06				Website - www.nihva.com
	NAME	SIGNATURE	DATE	PROJECT NO - NTPL-281-B-PM
DRAWN	V.G.		25-05-2025	PRODUCT - RETRACTABLE ROOF
CHK'D	S.W.		25-05-2025	SITE LOCATION - AKOLA
APPV'D	V.T.		25-05-2025	
if any queries contact - supportautomation@nihva.com				REVISION - / QTY - 1
ALL DIMENSION ARE IN mm			A3	SCALE - / SHEET 21 OF 41

ITEM NO.	PART NUMBER	DESCRIPTION	QTY.
1	NP-PLT02_TP	MS - 100X90X10T	12

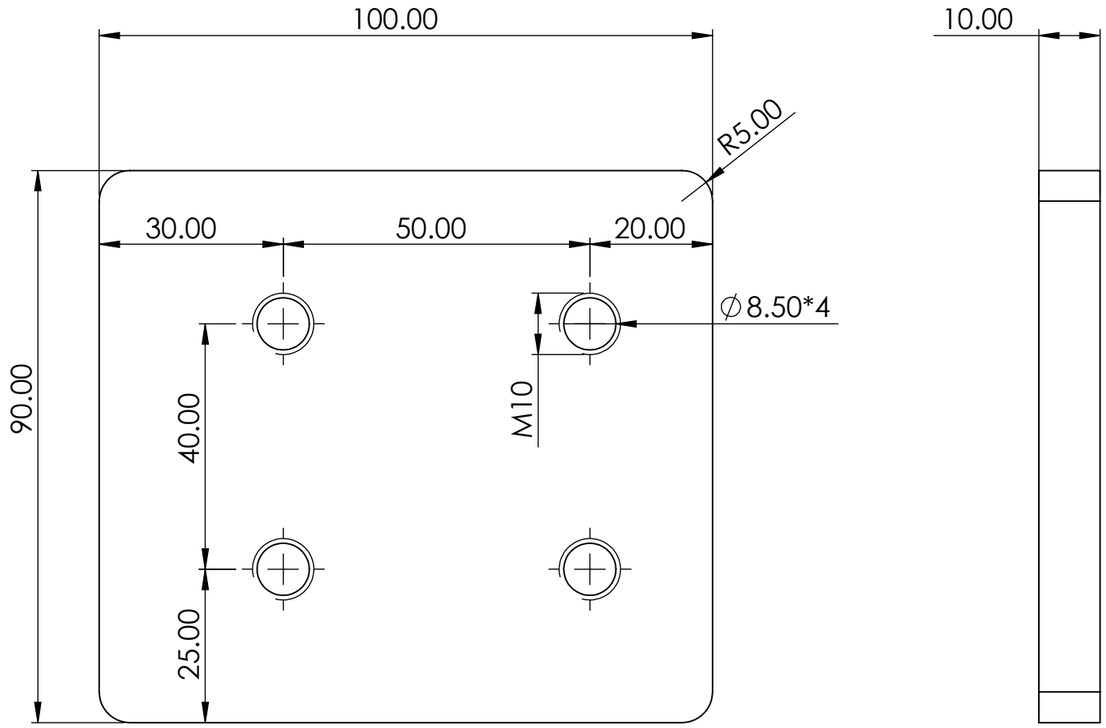

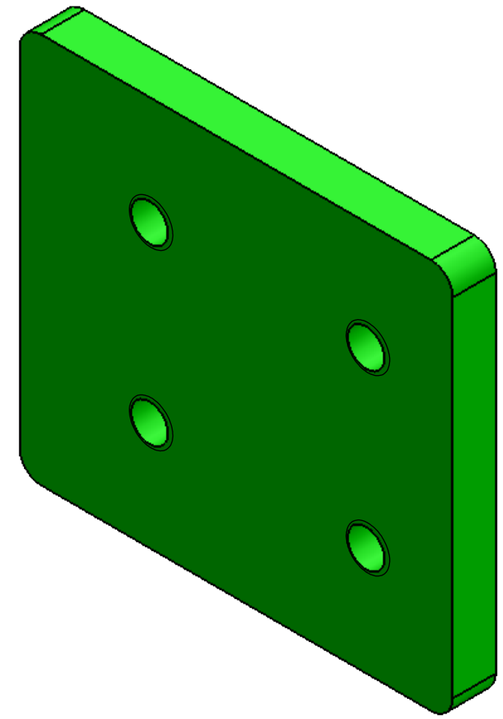



NOTE :- PLATE 02
ALL PANEL THIS PLATE 02 IS USED
LASER CUTTING
THICKNESS - 10 MM

NOTE :- FILLET RADIUS 5 MM SAME FOR ALL CORNERS

TITLE - ROOF AUTOMATION				NIHVA TECHNOLOGIES PVT.LTD.PUNE	
DWG NO - NTPL-281-PM-001-02-01-07				Website - www.nihva.com	
	NAME	SIGNATURE	DATE	PROJECT NO - NTPL-281-B-PM	
DRAWN	V.G.		25-05-2025	PRODUCT - RETRACTABLE ROOF	
CHK'D	S.W.		25-05-2025	SITE LOCATION - AKOLA	
APPV'D	V.T.		25-05-2025		
if any queries contact - supportautomation@nihva.com				REVISION -	QTY - 1
ALL DIMENSION ARE IN mm		A3		SCALE -	SHEET 22 OF 41

ITEM NO.	PART NUMBER	DESCRIPTION	QTY.
1	NP-PLT03_ TP	MS - 160X100X6T	1

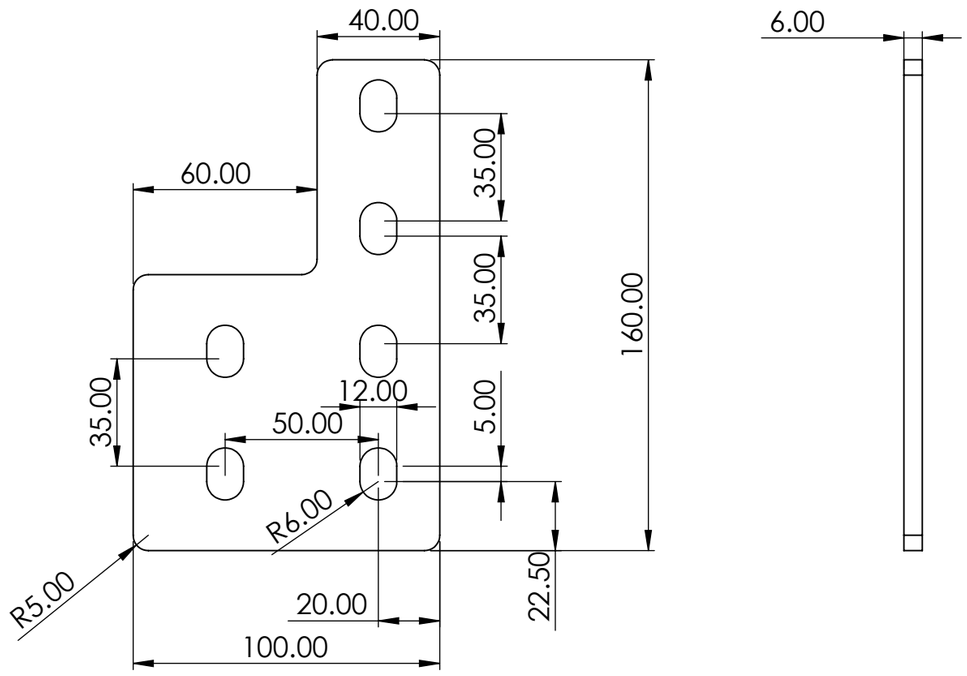

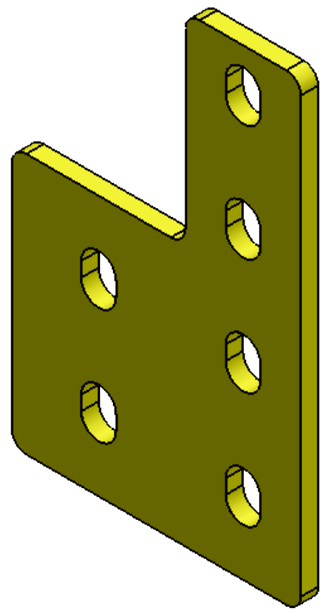



NOTE :- PLATE 03
ALL PANEL THIS PLATE 03 IS USED
LASER CUTTING
THICKNESS - 6 MM

NOTE :- FILLET RADIUS 5 MM SAME FOR ALL CORNERS

TITLE - ROOF AUTOMATION				NIHVA TECHNOLOGIES PVT.LTD.PUNE
DWG NO - NTPL-281-PM-001-02-01-08				Website - www.nihva.com
	NAME	SIGNATURE	DATE	PROJECT NO - NTPL-281-B-PM
DRAWN	V.G.		25-05-2025	PRODUCT - RETRACTABLE ROOF
CHK'D	S.W.		25-05-2025	SITE LOCATION - AKOLA
APPV'D	V.T.		25-05-2025	
if any queries contact - supportautomation@nihva.com				REVISION - QTY - 1
ALL DIMENSION ARE IN mm		A3		SCALE - SHEET 23 OF 41

ITEM NO.	PART NUMBER	DESCRIPTION	QTY.
1	NP-PLT04_TP	MS - 100X80X10T	12

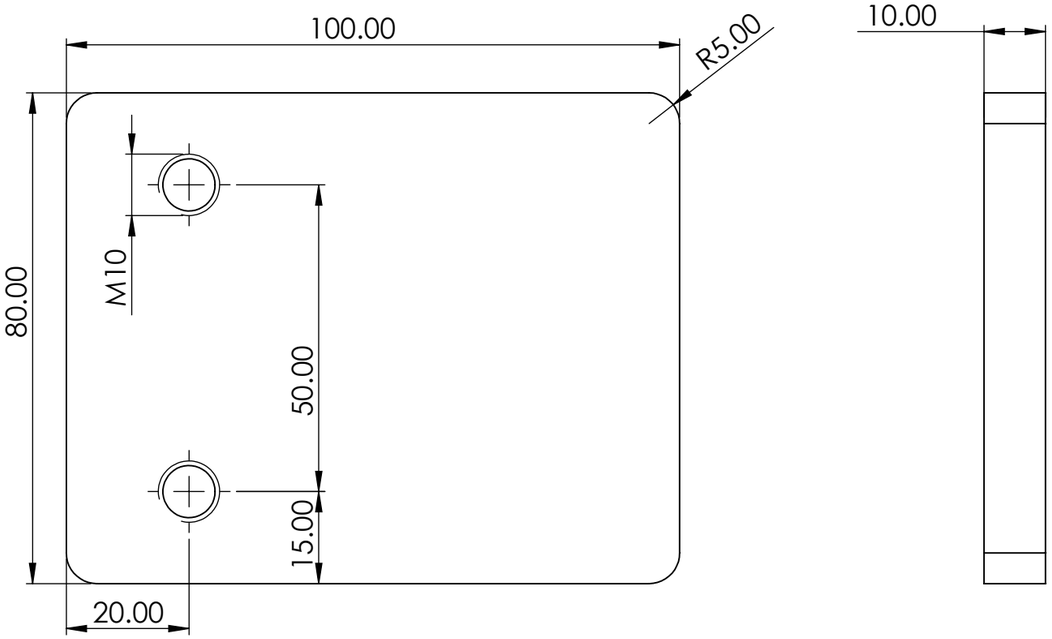

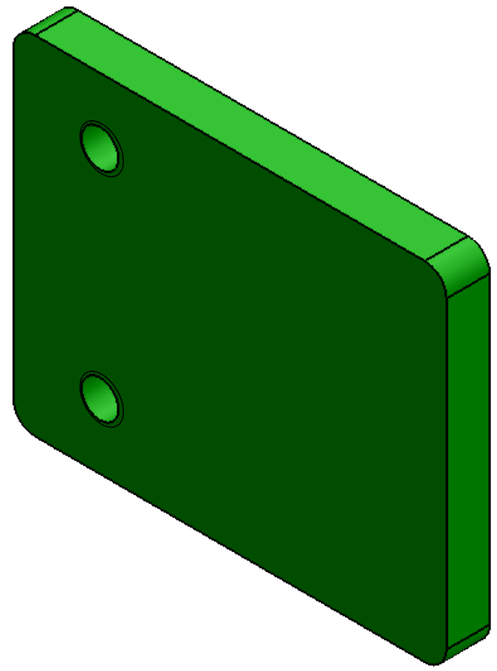



NOTE :- PLATE 04
ALL PANEL THIS PLATE 04 IS USED
LASER CUTTING
THICKNESS - 10 MM


NOTE :- FILLET RADIUS 5 MM SAME FOR ALL CORNERS

TITLE - ROOF AUTOMATION				NIHVA TECHNOLOGIES PVT.LTD.PUNE Website - www.nihva.com
DWG NO - NTPL-281-PM-001-02-01-09				
	NAME	SIGNATURE	DATE	PROJECT NO - NTPL-281-B-PM
DRAWN	V.G.		25-05-2025	PRODUCT - RETRACTABLE ROOF
CHK'D	S.W.		25-05-2025	SITE LOCATION - AKOLA
APPV'D	V.T.		25-05-2025	
if any queries contact - supportautomation@nihva.com				REVISION - / QTY - 1
ALL DIMENSION ARE IN mm		A3		SCALE - / SHEET 24 OF 41

ITEM NO.	PART NUMBER	DESCRIPTION	QTY.
1	NP-PLT06_TP	MS - 100X80X10T	12

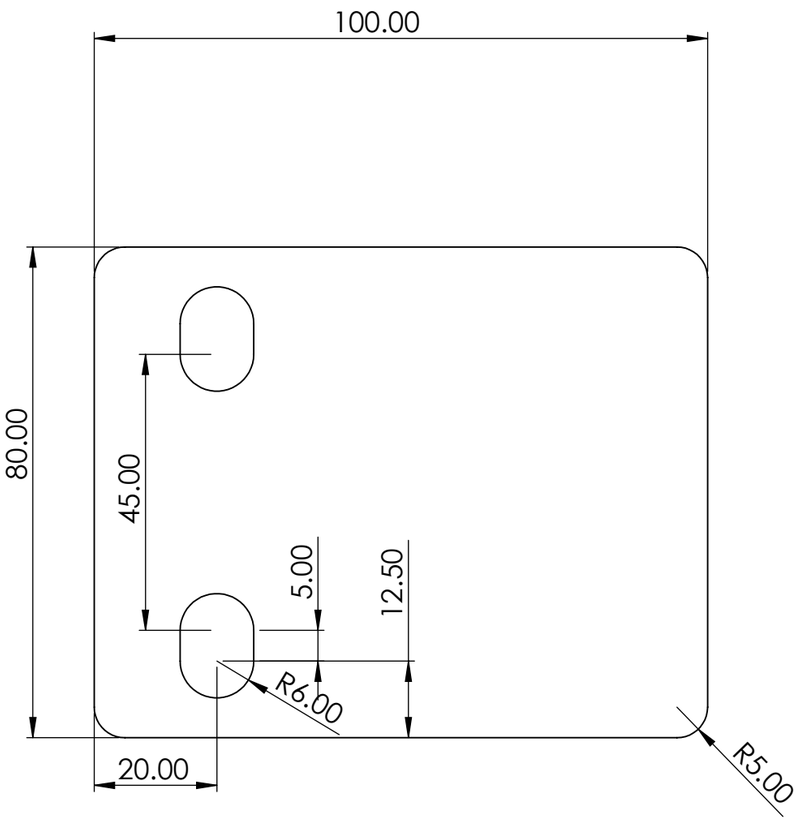

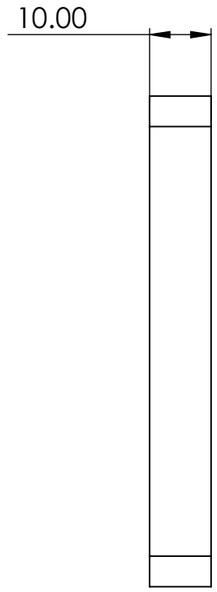

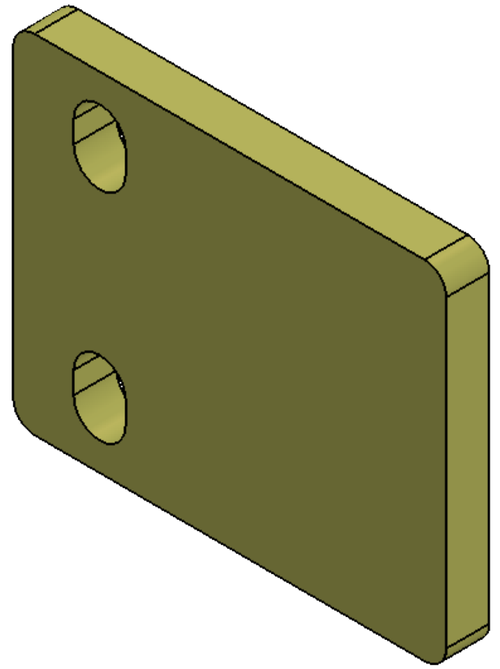



NOTE :- PLATE 06
ALL PANEL THIS PLATE 06 IS USED
LASER CUTTING
THICKNESS - 10 MM


NOTE :- FILLET RADIUS 5 MM SAME FOR ALL CORNERS

TITLE - ROOF AUTOMATION				NIHVA TECHNOLOGIES PVT.LTD.PUNE
DWG NO - NTPL-281-PM-001-02-01-10				Website - www.nihva.com
	NAME	SIGNATURE	DATE	PROJECT NO - NTPL-281-B-PM
DRAWN	V.G.		25-05-2025	PRODUCT - RETRACTABLE ROOF
CHK'D	S.W.		25-05-2025	SITE LOCATION - AKOLA
APPV'D	V.T.		25-05-2025	
if any queries contact - supportautomation@nihva.com				REVISION - QTY - 1
ALL DIMENSION ARE IN mm		A3		SCALE - SHEET 25 OF 41

ITEM NO.	PART NUMBER	DESCRIPTION	QTY.
1	NP-PLT05_TP	MS - 150X80X10T	12

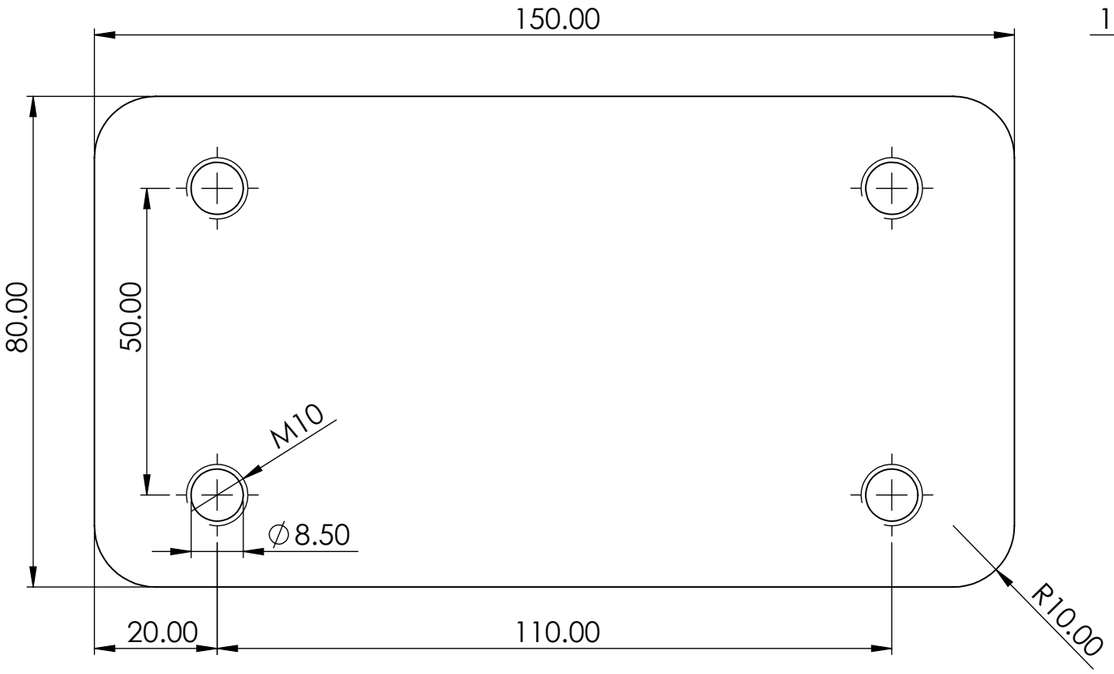

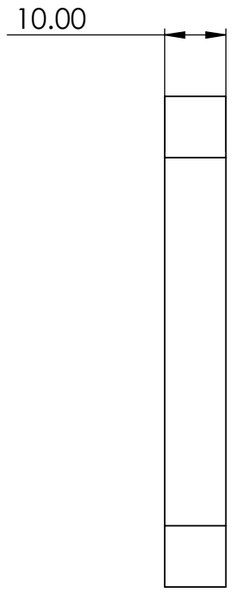

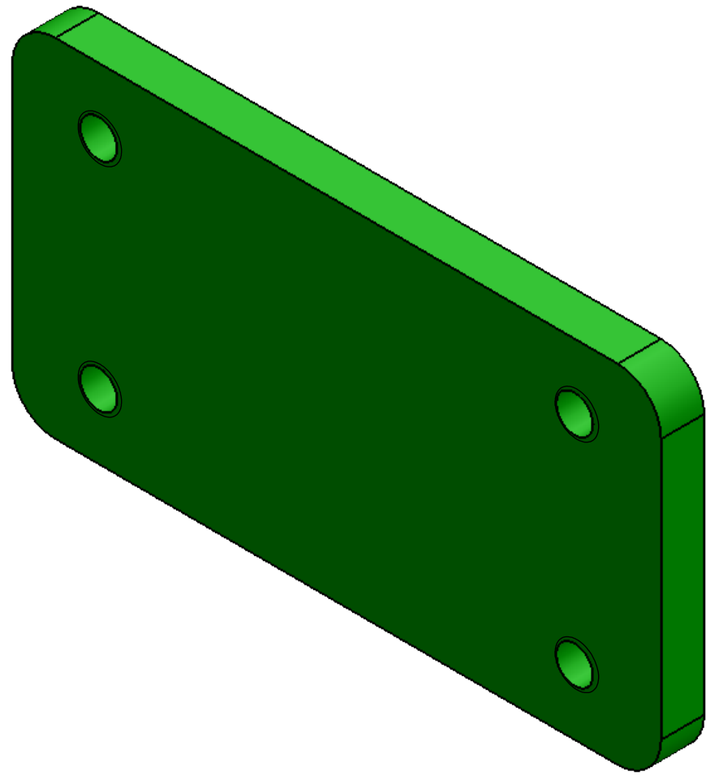



NOTE :- PLATE 05
ALL PANEL THIS PLATE 05 IS USED
LASER CUTTING
THICKNESS - 10 MM


NOTE :- FILLET RADIUS 10 MM SAME FOR ALL CORNERS

TITLE - ROOF AUTOMATION				NIHVA TECHNOLOGIES PVT.LTD.PUNE
DWG NO - NTPL-281-PM-001-02-01-11				Website - www.nihva.com
	NAME	SIGNATURE	DATE	PROJECT NO - NTPL-281-B-PM
DRAWN	V.G.		25-05-2025	PRODUCT - RETRACTABLE ROOF
CHK'D	S.W.		25-05-2025	SITE LOCATION - AKOLA
APPV'D	V.T.		25-05-2025	
if any queries contact - supportautomation@nihva.com				REVISION - / QTY - 1
ALL DIMENSION ARE IN mm		A3		SCALE - / SHEET 26 OF 41

ITEM NO.	PART NUMBER	DESCRIPTION	QTY.
1	NP-PLT07_TP	MS - 150X80X10T	12

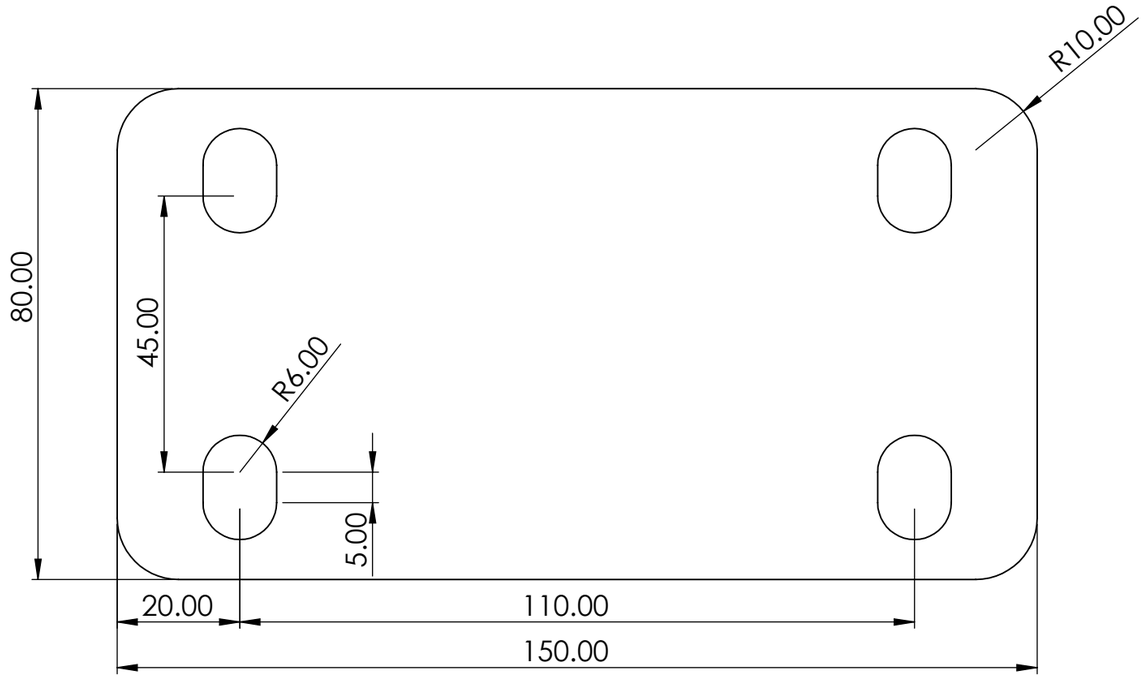

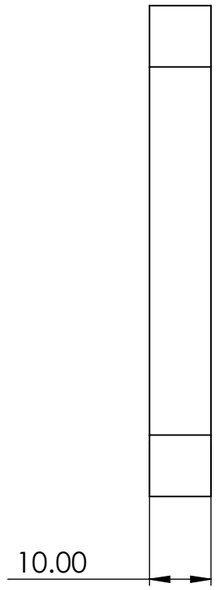

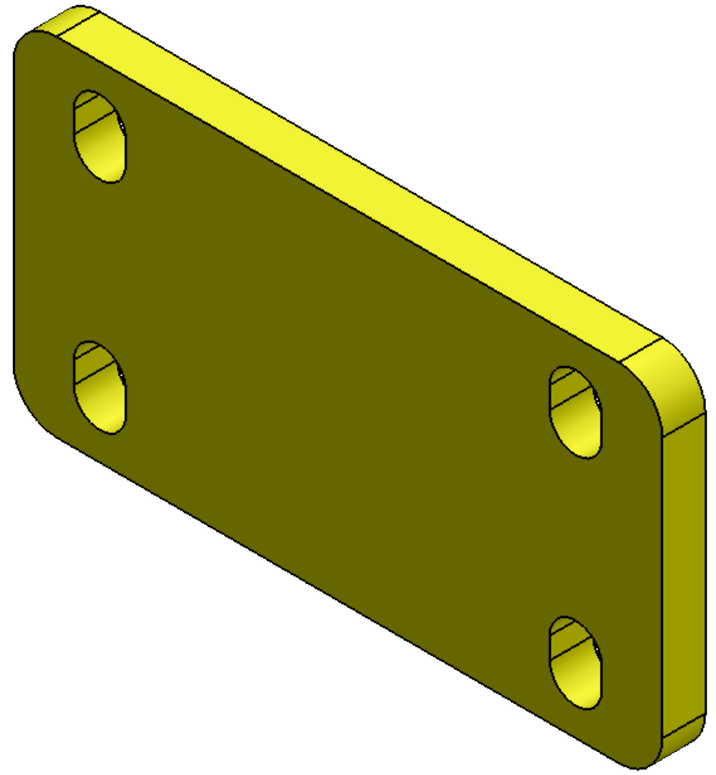



NOTE :- PLATE 07
ALL PANEL THIS PLATE 07 IS USED
LASER CUTTING
THICKNESS - 10 MM

NOTE :- FILLET RADIUS 10 MM SAME FOR ALL CORNERS

TITLE - ROOF AUTOMATION				NIHVA TECHNOLOGIES PVT.LTD.PUNE
DWG NO - NTPL-281-PM-001-02-01-12				Website - www.nihva.com
	NAME	SIGNATURE	DATE	PROJECT NO - NTPL-281-B-PM
DRAWN	V.G.		25-05-2025	PRODUCT - RETRACTABLE ROOF
CHK'D	S.W.		25-05-2025	SITE LOCATION - AKOLA
APPV'D	V.T.		25-05-2025	
if any queries contact - supportautomation@nihva.com				REVISION - / QTY - 1
ALL DIMENSION ARE IN mm			A3	SCALE - / SHEET 27 OF 41


ITEM NO.	PART NUMBER	DESCRIPTION	QTY.
1	NYLON STOPPER SMALL		2

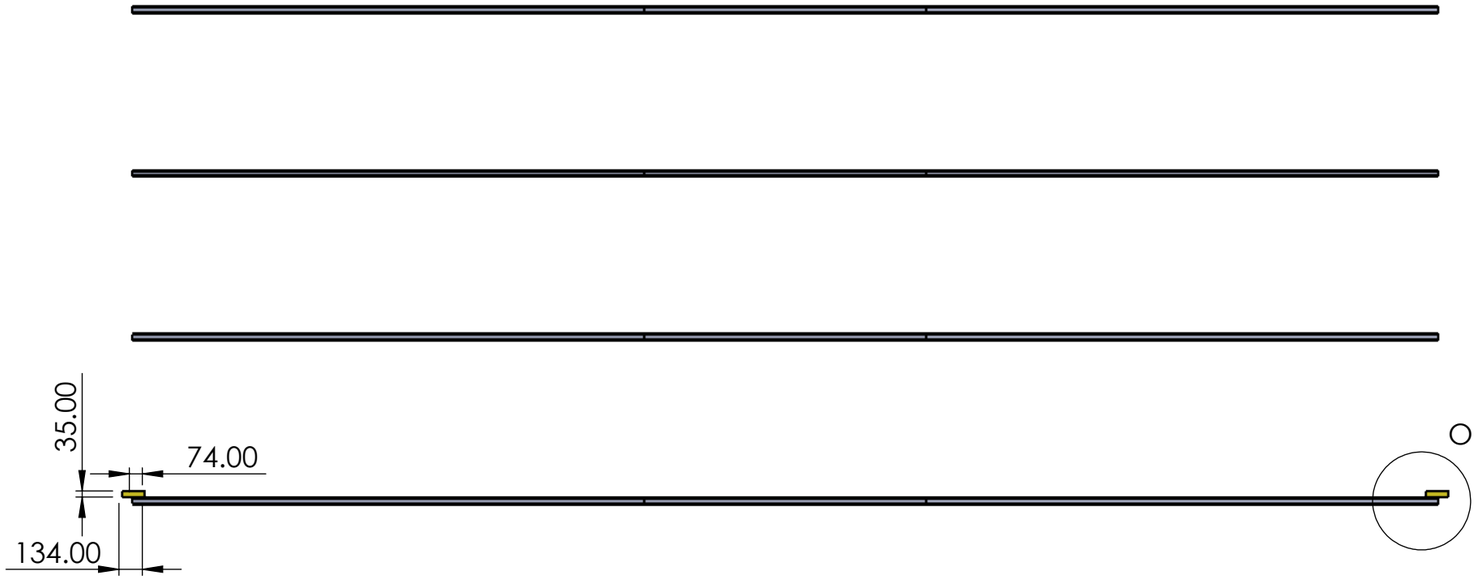

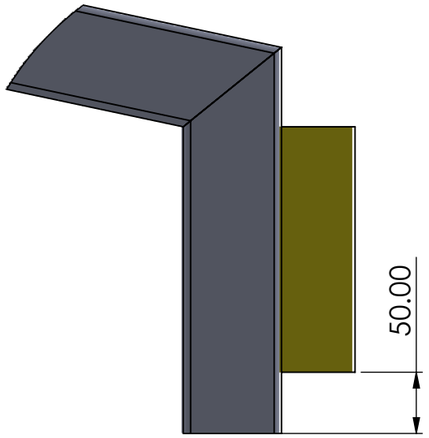



DETAIL P
SCALE 1 : 5

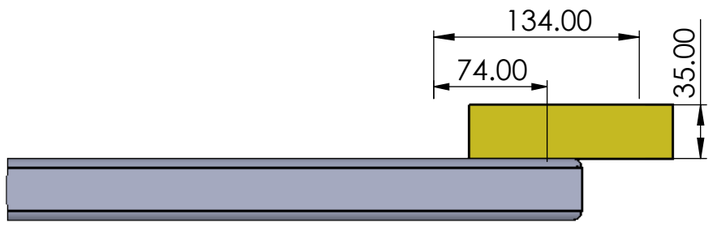


DETAIL O
SCALE 1 : 4

NOTE :- THIS NYLON STOPER PLACED ON 1ST PROFILE
OTHER NYLON STOPER PLACED AT JUST ITS
OPPOSITE SITE


PANEL NO 01

TITLE - ROOF AUTOMATION				NIHVA TECHNOLOGIES PVT.LTD.PUNE
DWG NO - NTPL-281-PM-001-02-01-13				Website - www.nihva.com
	NAME	SIGNATURE	DATE	PROJECT NO - NTPL-281-B-PM
DRAWN	V.G.		25-05-2025	PRODUCT - RETRACTABLE ROOF
CHK'D	S.W.		25-05-2025	SITE LOCATION - AKOLA
APPV'D	V.T.		25-05-2025	
if any queries contact - supportautomation@nihva.com				REVISION - / QTY - 1
ALL DIMENSION ARE IN mm		A3		SCALE - / SHEET 28 OF 41


ITEM NO.	PART NUMBER	DESCRIPTION	QTY.
1	NYLON STOPPER SMALL		4

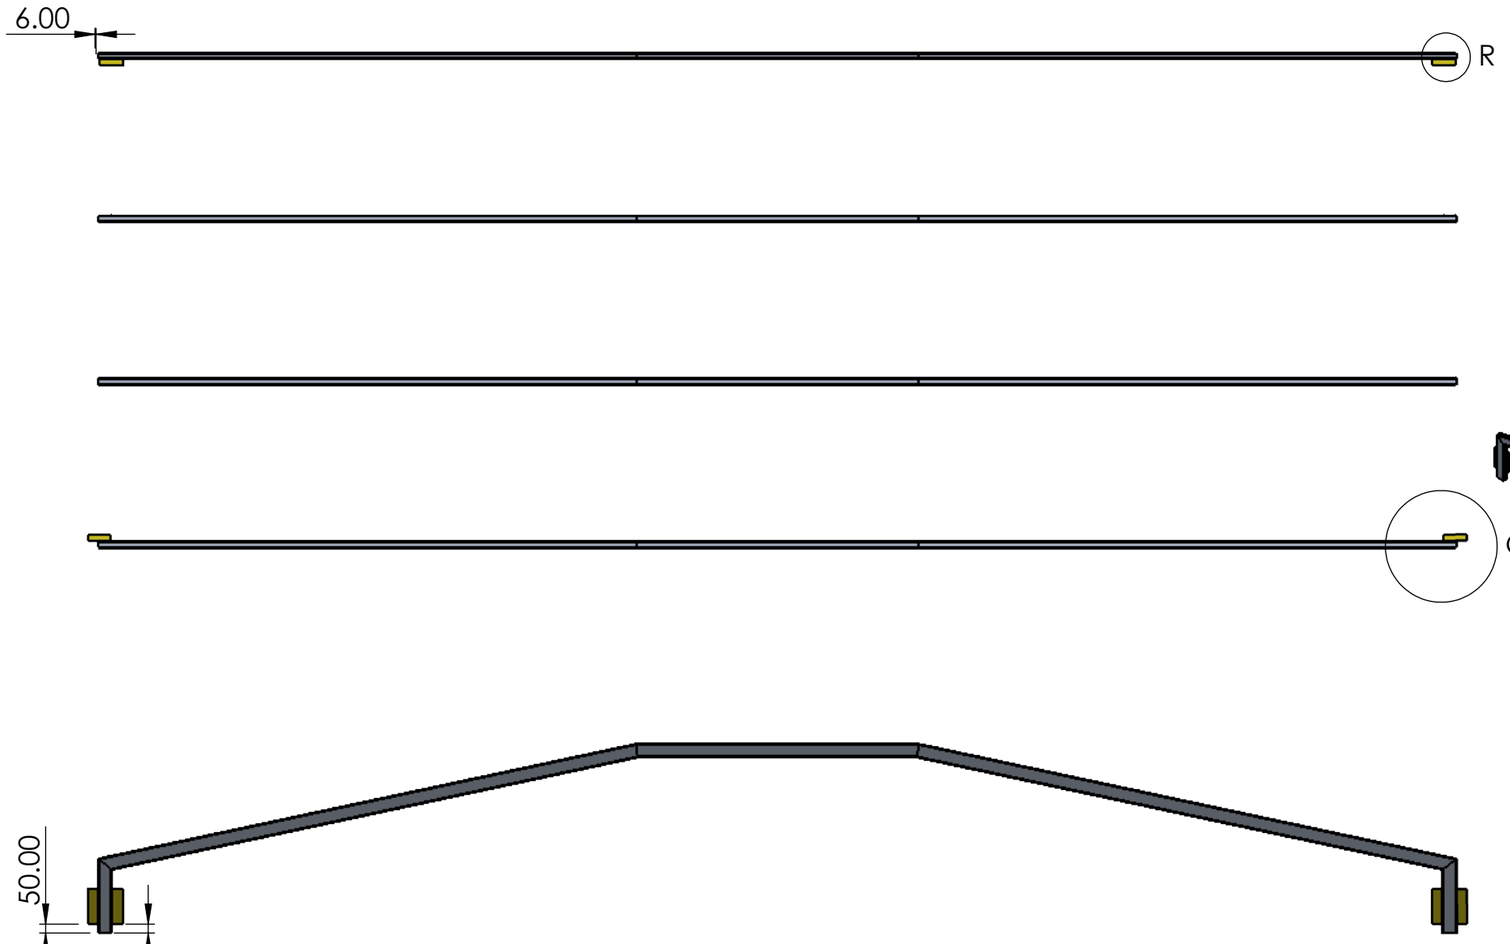



DETAIL Q
SCALE 2 : 15

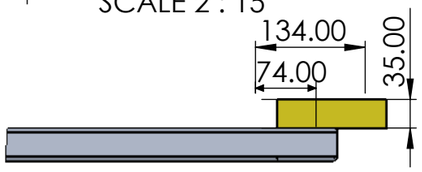


DETAIL R
SCALE 2 : 15

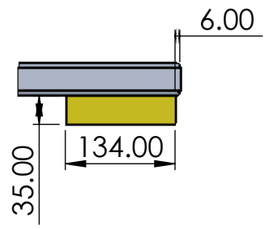

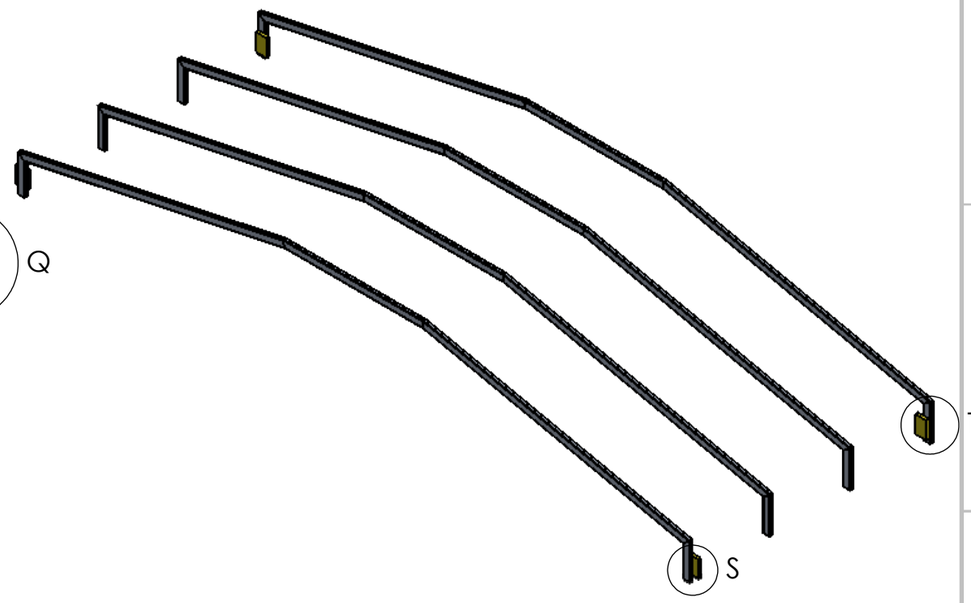

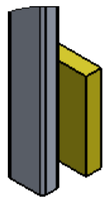

DETAIL S
SCALE 1 : 10

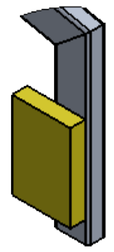


DETAIL T
SCALE 1 : 10

NOTE :- THIS NYLON STOPER PLACED ON 1ST AND LAST PROFILE
OTHER NYLON STOPER PLACED AT JUST ITS OPPOSITE SITE

PANEL NO 02


TITLE - ROOF AUTOMATION				NIHVA TECHNOLOGIES PVT.LTD.PUNE
DWG NO - NTPL-281-PM-001-02-02-01				Website - www.nihva.com
	NAME	SIGNATURE	DATE	PROJECT NO - NTPL-281-B-PM
DRAWN	V.G.		25-05-2025	PRODUCT - RETRACTABLE ROOF
CHK'D	S.W.		25-05-2025	SITE LOCATION - AKOLA
APPV'D	V.T.		25-05-2025	
if any queries contact - supportautomation@nihva.com				REVISION - / QTY - 1
ALL DIMENSION ARE IN mm			A3	SCALE - / SHEET 29 OF 41


ITEM NO.	PART NUMBER	DESCRIPTION	QTY.
1	NYLON STOPPER SMALL		2
2	NYLON STOPPER BIG		2

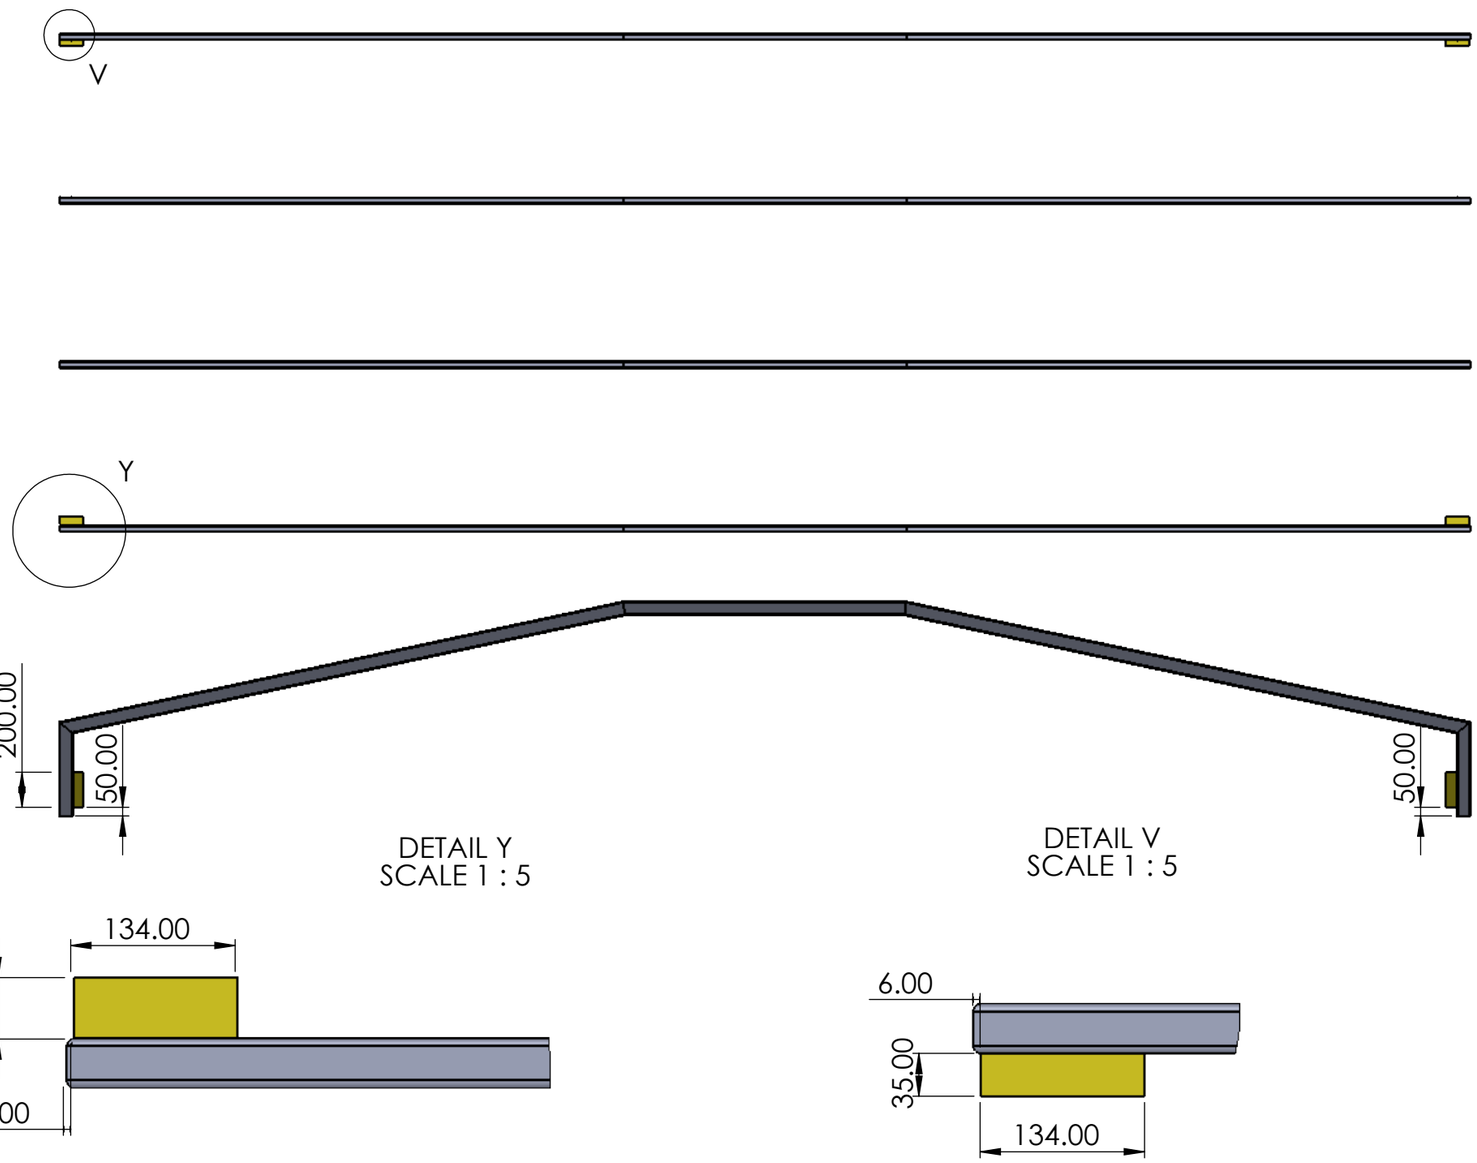


DETAIL Y
SCALE 1 : 5

DETAIL V
SCALE 1 : 5

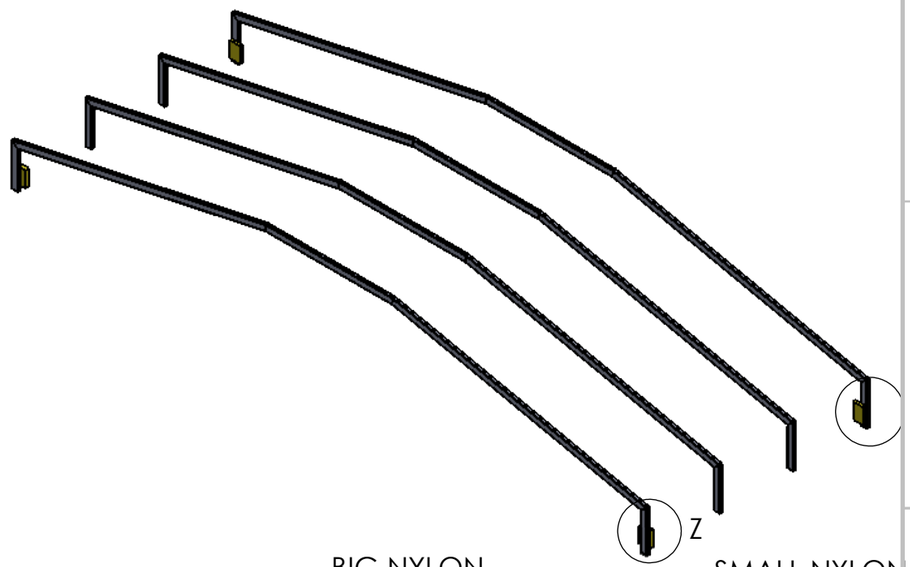

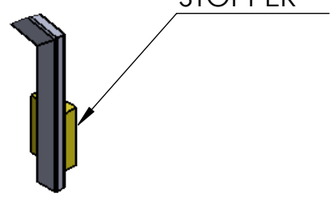

DETAIL Z
SCALE 2 : 35

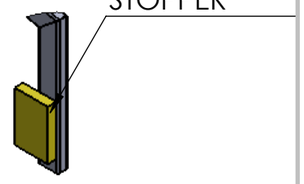

DETAIL AA
SCALE 2 : 35


NOTE :- THIS NYLON STOPER PLACED ON 1ST AND LAST PROFILE
OTHER NYLON STOPER PLACED AT JUST ITS OPPOSITE SITE


PANEL NO 03

TITLE - ROOF AUTOMATION				NIHVA TECHNOLOGIES PVT.LTD.PUNE
DWG NO - NTPL-281-PM-001-02-03-01				Website - www.nihva.com
	NAME	SIGNATURE	DATE	PROJECT NO - NTPL-281-B-PM
DRAWN	V.G.		25-05-2025	PRODUCT - RETRACTABLE ROOF
CHK'D	S.W.		25-05-2025	SITE LOCATION - AKOLA
APPV'D	V.T.		25-05-2025	
if any queries contact - supportautomation@nihva.com				REVISION - / QTY - 1
ALL DIMENSION ARE IN mm			A3	SCALE - / SHEET 30 OF 41

ITEM NO.	PART NUMBER	DESCRIPTION	QTY.
1	NYLON STOPPER BIG		2



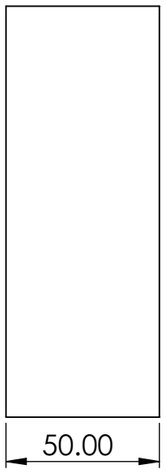


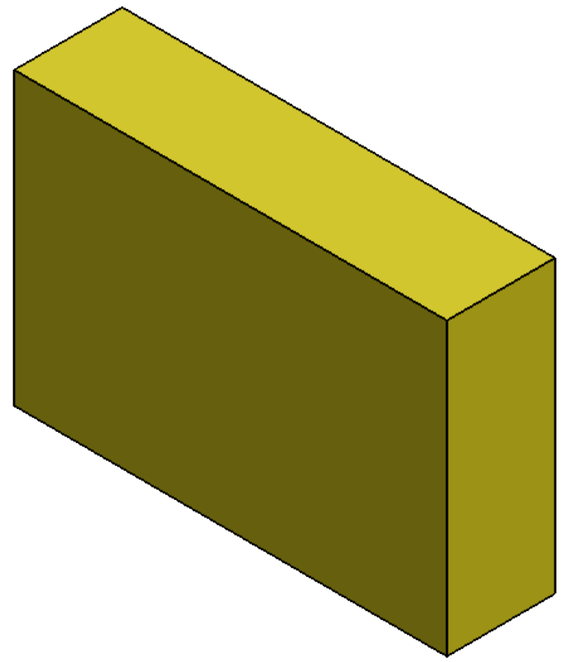


BIG NYLON STOPPER

TITLE - ROOF AUTOMATION				NIHVA Technologies Pvt. Ltd.	NIHVA TECHNOLOGIES PVT.LTD.PUNE Website - www.nihva.com
DWG NO - NTPL-281-PM-001-03-00-00					
	NAME	SIGNATURE	DATE	PROJECT NO - NTPL-281-B-PM	
DRAWN	V.G.		25-05-2025	PRODUCT - RETRACTABLE ROOF	
CHK'D	S.W.		25-05-2025	SITE LOCATION - AKOLA	
APPV'D	V.T.		25-05-2025		
if any queries contact - supportautomation@nihva.com				REVISION -	QTY - 1
ALL DIMENSION ARE IN mm		A3		SCALE -	SHEET 31 OF 41

ITEM NO.	PART NUMBER	DESCRIPTION	QTY.
1	NYLON STOPPER SMALL		8

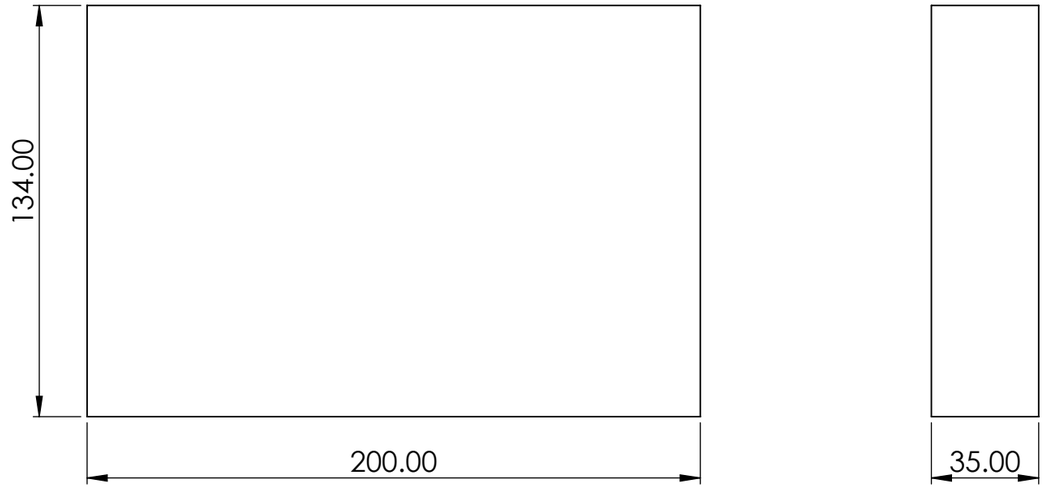


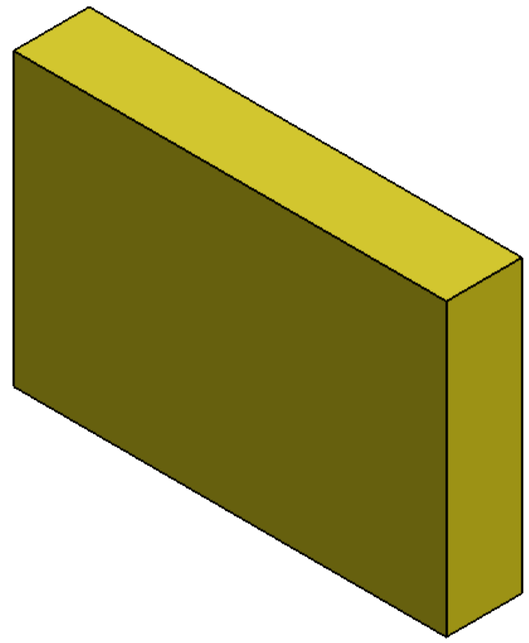



SMALL NYLON STOPPER

TITLE - ROOF AUTOMATION				NIHVA TECHNOLOGIES PVT.LTD.PUNE
DWG NO - NTPL-281-PM-001-04-00-00				Website - www.nihva.com
	NAME	SIGNATURE	DATE	PROJECT NO - NTPL-281-B-PM
DRAWN	V.G.		25-05-2025	PRODUCT - RETRACTABLE ROOF
CHK'D	S.W.		25-05-2025	SITE LOCATION - AKOLA
APPV'D	V.T.		25-05-2025	
if any queries contact - supportautomation@nihva.com				REVISION - QTY - 1
ALL DIMENSION ARE IN mm		A3		SCALE - SHEET 32 OF 41

ITEM NO.	PART NUMBER	DESCRIPTION	QTY.
1	RACK SUPPORT	STD	14

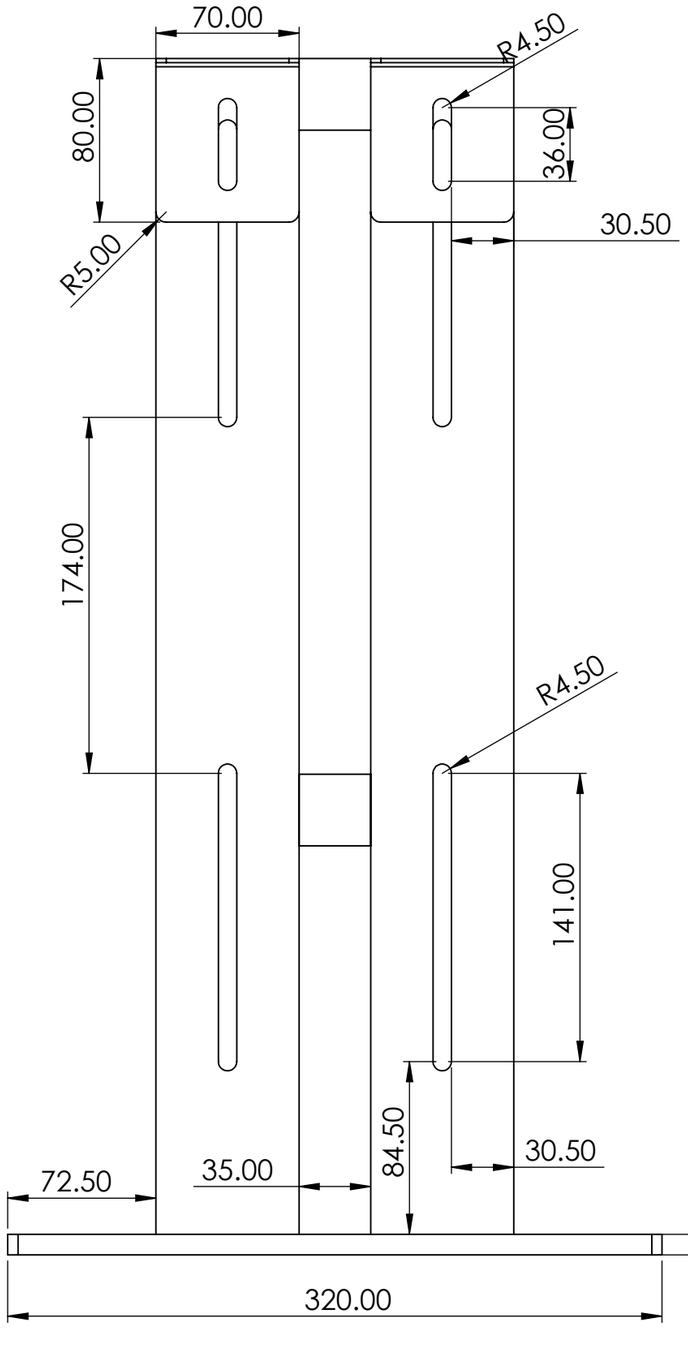

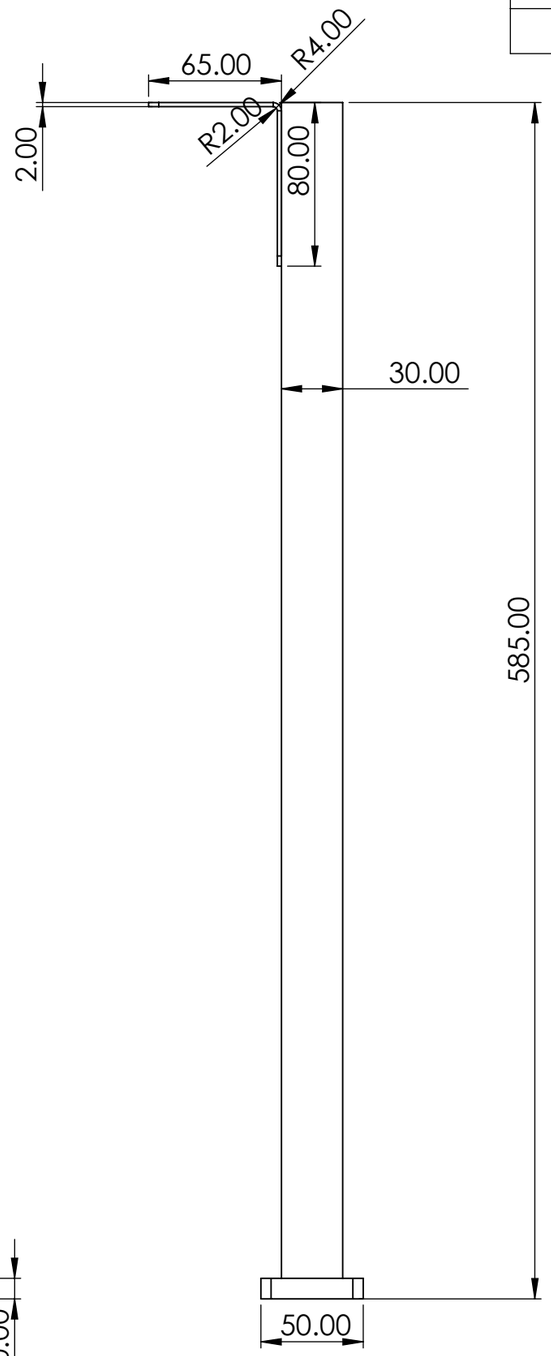


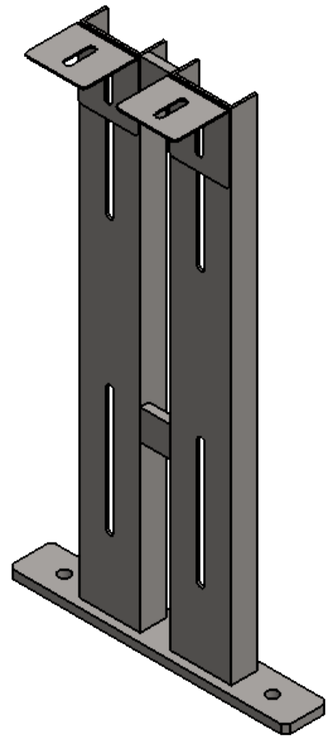



RACK SUPPORT

TITLE - ROOF AUTOMATION				NIHVA TECHNOLOGIES PVT.LTD.PUNE
DWG NO - NTPL-281-PM-001-05-00-00				Website - www.nihva.com
	NAME	SIGNATURE	DATE	PROJECT NO - NTPL-281-B-PM
DRAWN	V.G.		25-05-2025	PRODUCT - RETRACTABLE ROOF
CHK'D	S.W.		25-05-2025	SITE LOCATION - AKOLA
APPV'D	V.T.		25-05-2025	
if any queries contact - supportautomation@nihva.com				REVISION - / QTY - 1
ALL DIMENSION ARE IN mm		A3		SCALE - / SHEET 33 OF 41

ITEM NO.	PART NUMBER	DESCRIPTION	QTY.
1	ANCHOR BOLT M10 x 75 MM	STD	6

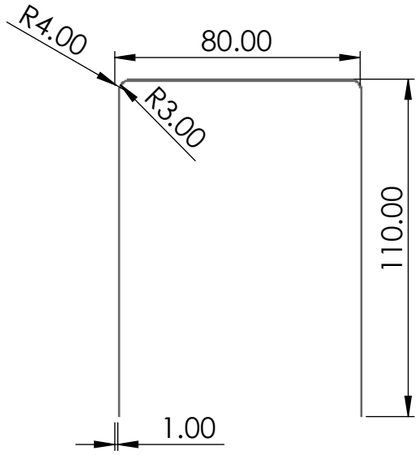

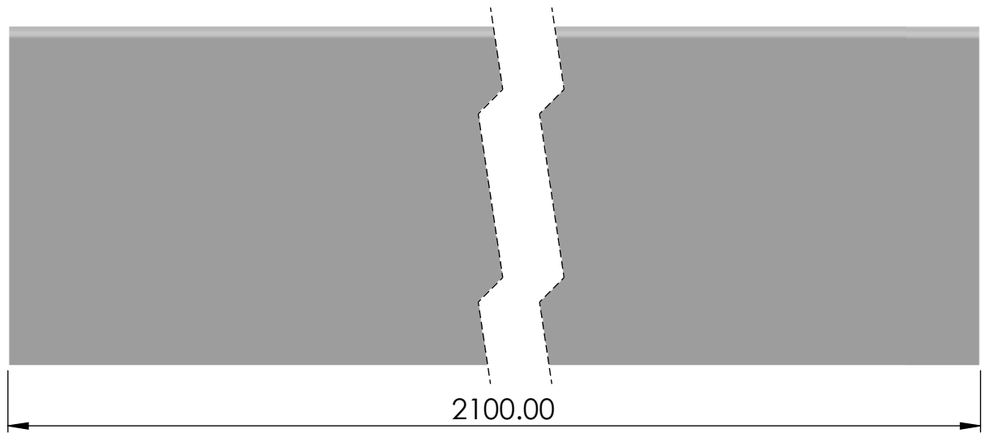


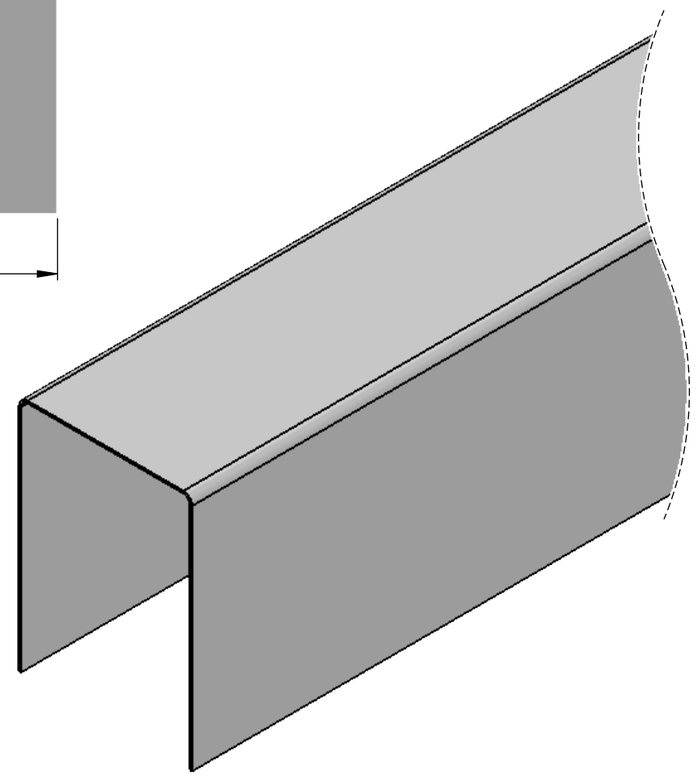


BUSBAR FLASHER

TITLE - ROOF AUTOMATION				NIHVA TECHNOLOGIES PVT.LTD.PUNE Website - www.nihva.com
DWG NO - NTPL-281-PM-001-06-00-00				
	NAME	SIGNATURE	DATE	PROJECT NO - NTPL-281-B-PM
DRAWN	V.G.		25-05-2025	PRODUCT - RETRACTABLE ROOF
CHK'D	S.W.		25-05-2025	SITE LOCATION - AKOLA
APPV'D	V.T.		25-05-2025	
if any queries contact - supportautomation@nihva.com				REVISION - / QTY - 1
ALL DIMENSION ARE IN mm			A3	SCALE - / SHEET 34 OF 41

ITEM NO.	PART NUMBER	DESCRIPTION	QTY.
1	GUIDE RAILS-T89-1B	STD (5 M LENGTH)	11

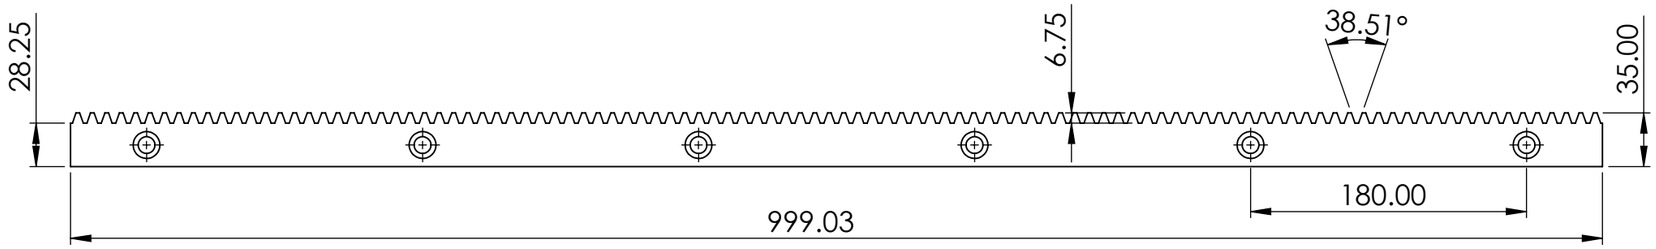


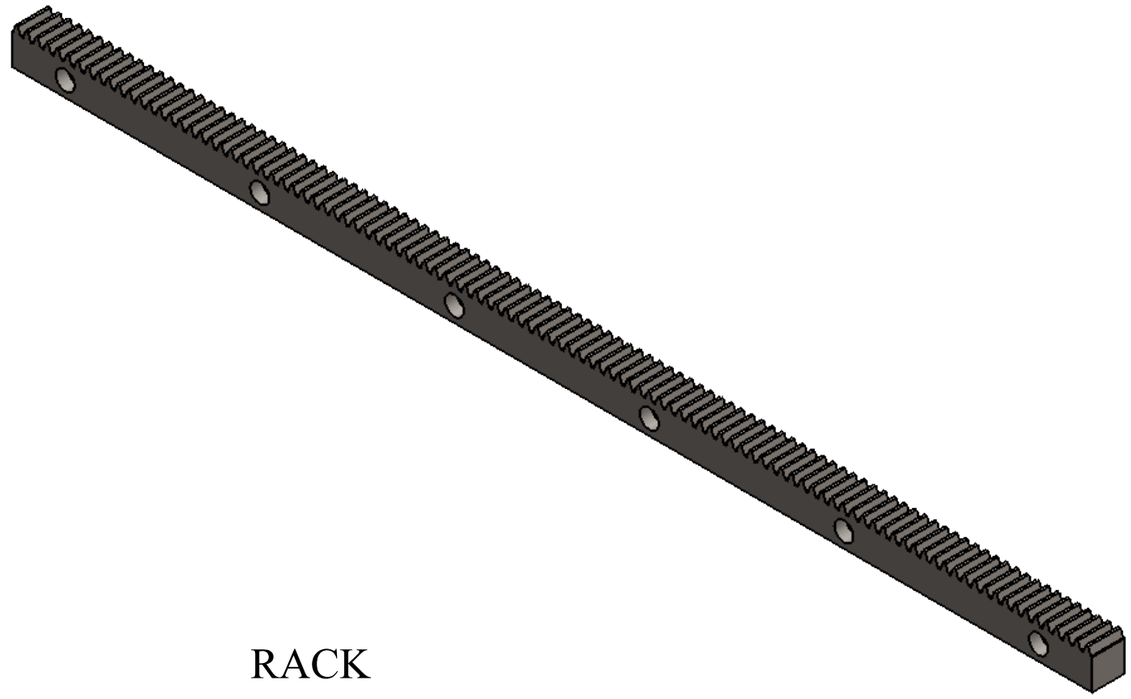



RACK


TITLE - ROOF AUTOMATION				NIHVA TECHNOLOGIES PVT.LTD.PUNE
DWG NO - NTPL-281-PM-001-07-00-00				Website - www.nihva.com
	NAME	SIGNATURE	DATE	PROJECT NO - NTPL-281-B-PM
DRAWN	V.G.		25-05-2025	PRODUCT - RETRACTABLE ROOF
CHK'D	S.W.		25-05-2025	SITE LOCATION - AKOLA
APPV'D	V.T.		25-05-2025	
if any queries contact - supportautomation@nihva.com				REVISION - QTY - 1
ALL DIMENSION ARE IN mm		A3		SCALE - SHEET 35 OF 41

ITEM NO.	PART NUMBER	DESCRIPTION	QTY.
1	MOTOR MTG BRT PLATE 1_NICE_1.8T	454X400X5MM THK	1

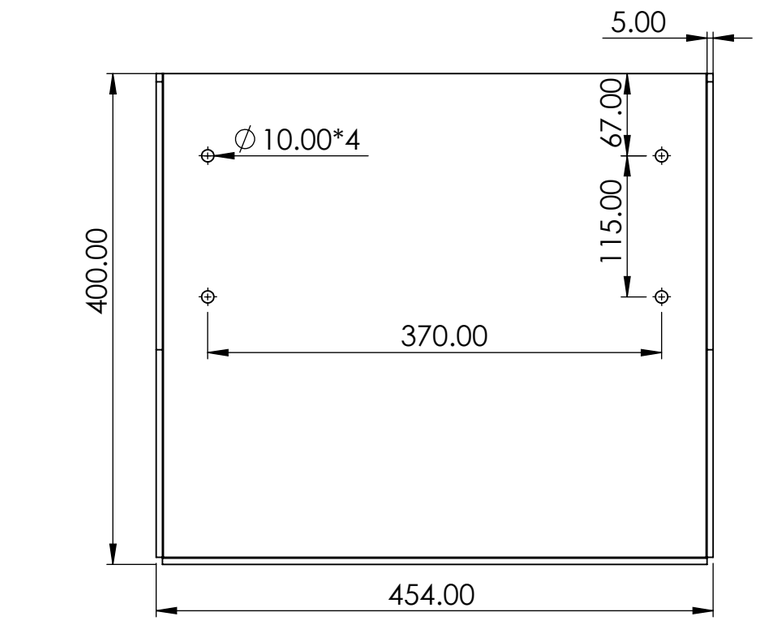

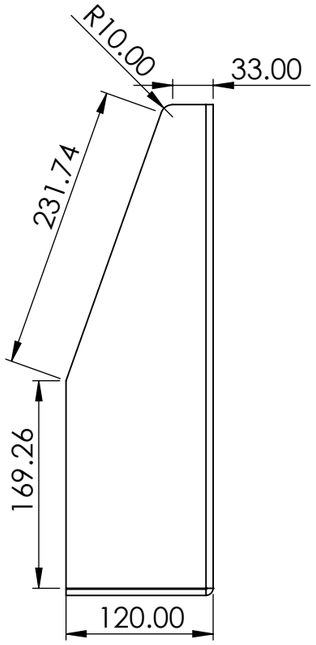

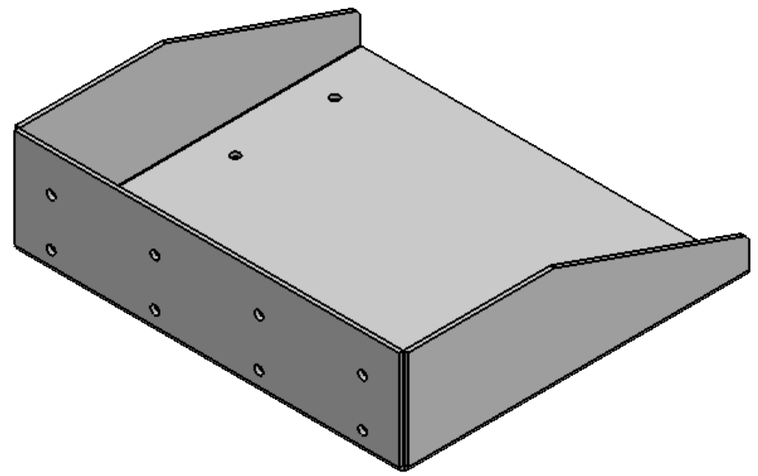


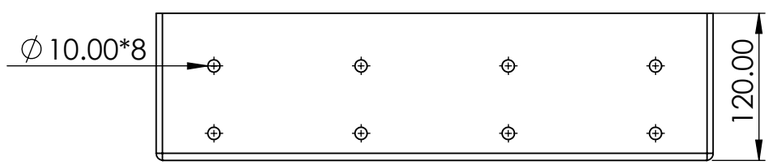



MOTOR BRACKET

TITLE - ROOF AUTOMATION				NIHVA TECHNOLOGIES PVT.LTD.PUNE
DWG NO - NTPL-281-PM-001-08-00-00				Website - www.nihva.com
	NAME	SIGNATURE	DATE	PROJECT NO - NTPL-281-B-PM
DRAWN	V.G.		25-05-2025	PRODUCT - RETRACTABLE ROOF
CHK'D	S.W.		25-05-2025	SITE LOCATION - AKOLA
APPV'D	V.T.		25-05-2025	
if any queries contact - supportautomation@nihva.com				REVISION - / QTY - 1
ALL DIMENSION ARE IN mm		A3		SCALE - / SHEET 36 OF 41

ITEM NO.	PART NUMBER	DESCRIPTION	QTY.
1	NICE RB 2.5T		1

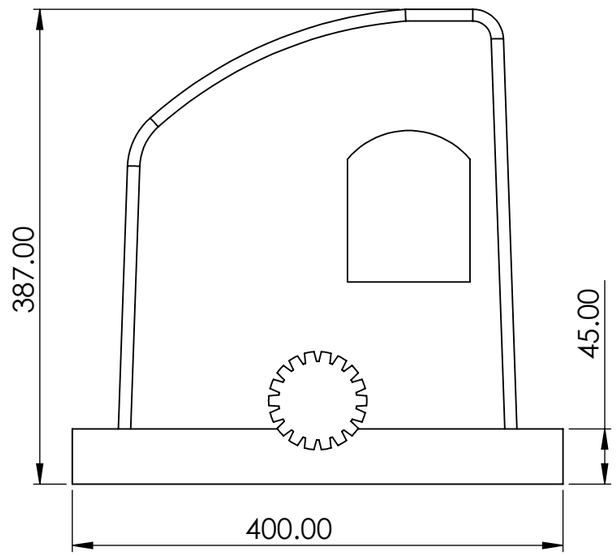

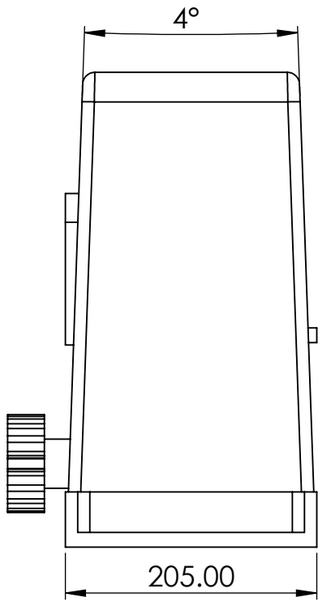


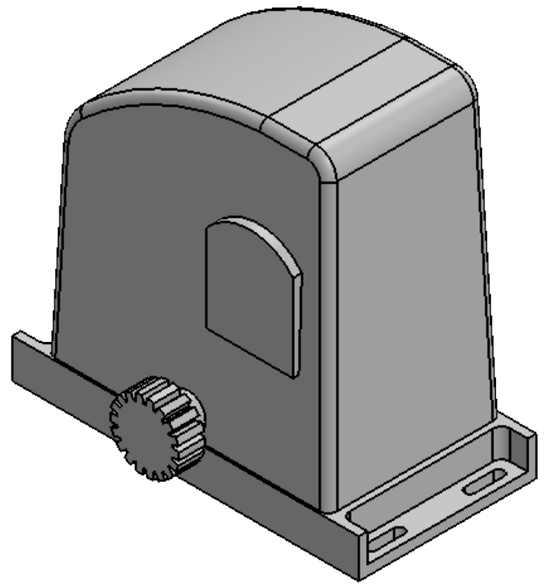



NICE 2.5T MOTOR

TITLE - ROOF AUTOMATION				NIHVA TECHNOLOGIES PVT.LTD.PUNE
DWG NO - NTPL-281-PM-001-09-00-00				Website - www.nihva.com
	NAME	SIGNATURE	DATE	PROJECT NO - NTPL-281-B-PM
DRAWN	V.G.		25-05-2025	PRODUCT - RETRACTABLE ROOF
CHK'D	S.W.		25-05-2025	SITE LOCATION - AKOLA
APPV'D	V.T.		25-05-2025	
if any queries contact - supportautomation@nihva.com				REVISION - QTY - 1
ALL DIMENSION ARE IN mm			A3	SCALE - SHEET 37 OF 41

ITEM NO.	PART NUMBER	DESCRIPTION	QTY.
1	LOCKING PLATE 1	78.85 X 90 X 6MM THK	24

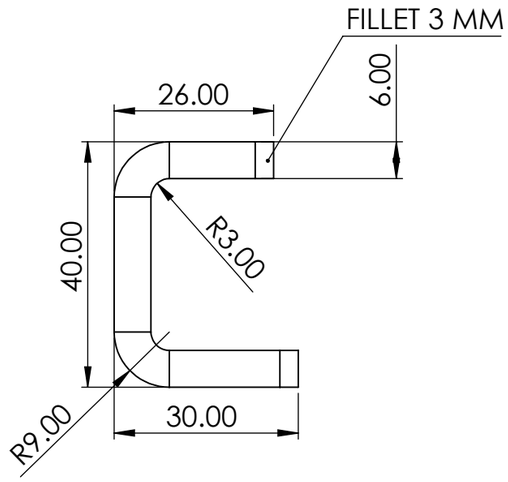

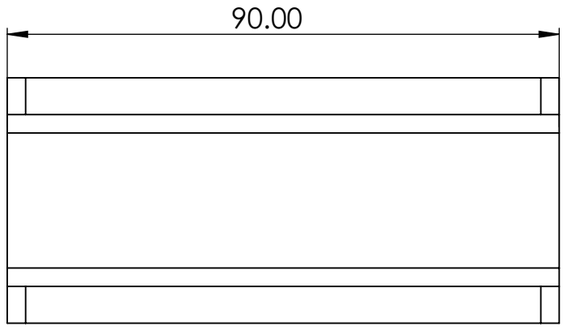


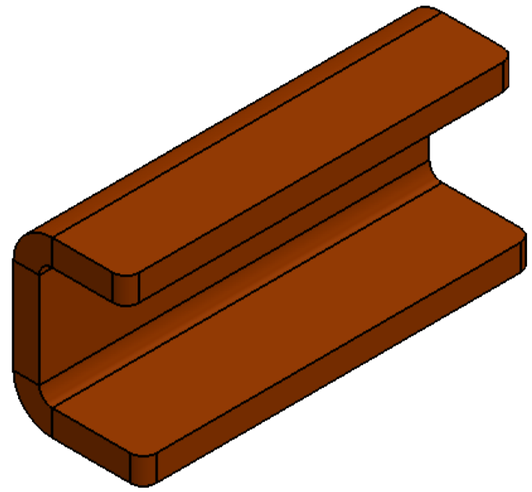


LOCKING PLATE 01

TITLE - ROOF AUTOMATION				NIHVA TECHNOLOGIES PVT.LTD.PUNE Website - www.nihva.com
DWG NO - NTPL-281-PM-001-10-00-00				
	NAME	SIGNATURE	DATE	PROJECT NO - NTPL-281-B-PM
DRAWN	V.G.		25-05-2025	PRODUCT - RETRACTABLE ROOF
CHK'D	S.W.		25-05-2025	SITE LOCATION - AKOLA
APPV'D	V.T.		25-05-2025	
if any queries contact - supportautomation@nihva.com				REVISION - / QTY - 1
ALL DIMENSION ARE IN mm		A3		SCALE - / SHEET 38 OF 41


ITEM NO.	PART NUMBER	DESCRIPTION	QTY.
1	LOCKING PLATE 2	113.42 X 90 X 6 MM THK	12

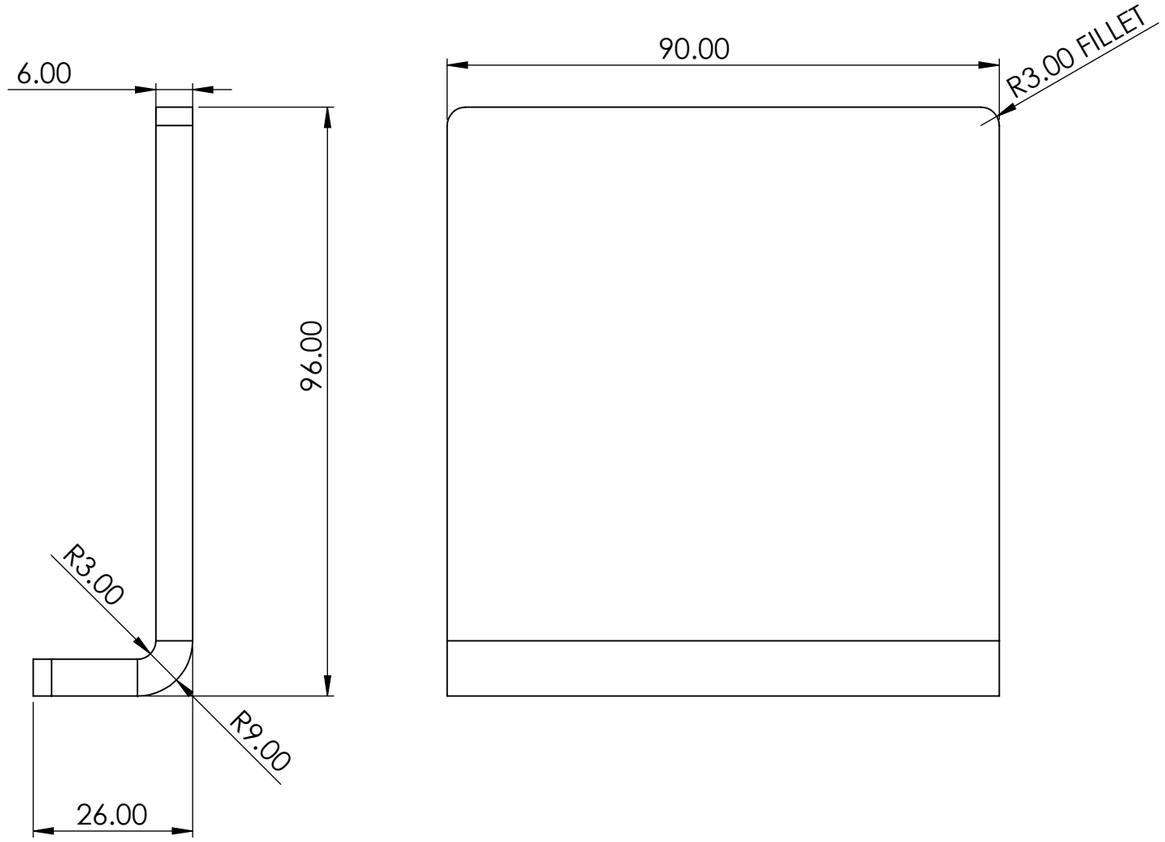


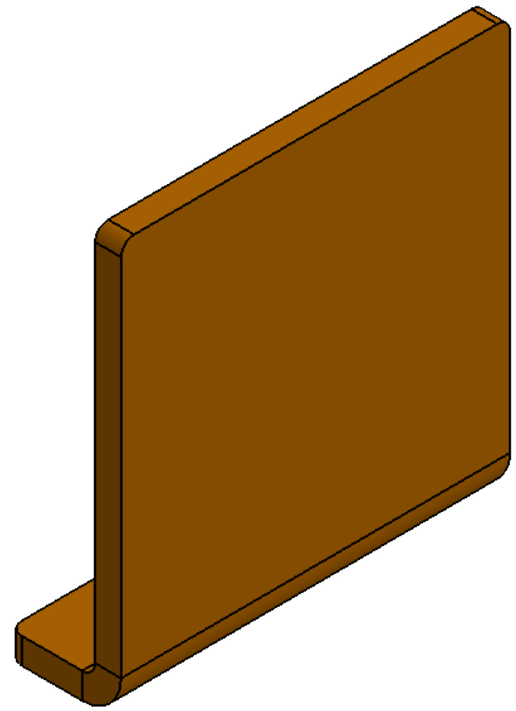


LOCKING PLATE 02

TITLE - ROOF AUTOMATION				NIHVA TECHNOLOGIES PVT.LTD.PUNE
DWG NO - NTPL-281-PM-001-02-01-014				Website - www.nihva.com
	NAME	SIGNATURE	DATE	PROJECT NO - NTPL-281-B-PM
DRAWN	V.G.		25-05-2025	PRODUCT - RETRACTABLE ROOF
CHK'D	S.W.		25-05-2025	SITE LOCATION - AKOLA
APPV'D	V.T.		25-05-2025	
if any queries contact - supportautomation@nihva.com				REVISION - QTY - 1
ALL DIMENSION ARE IN mm		A3		SCALE - SHEET 39 OF 41

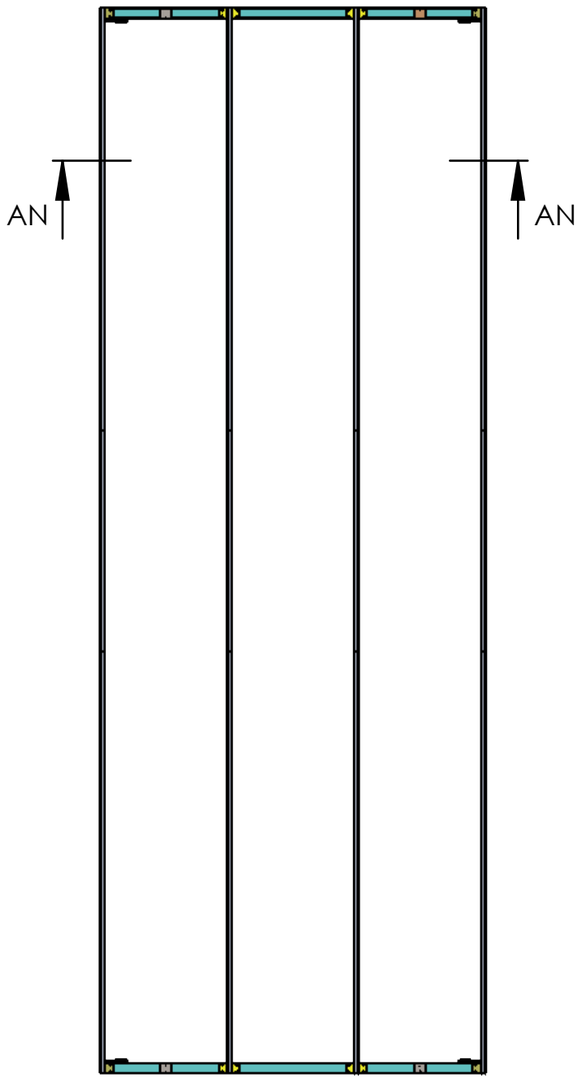

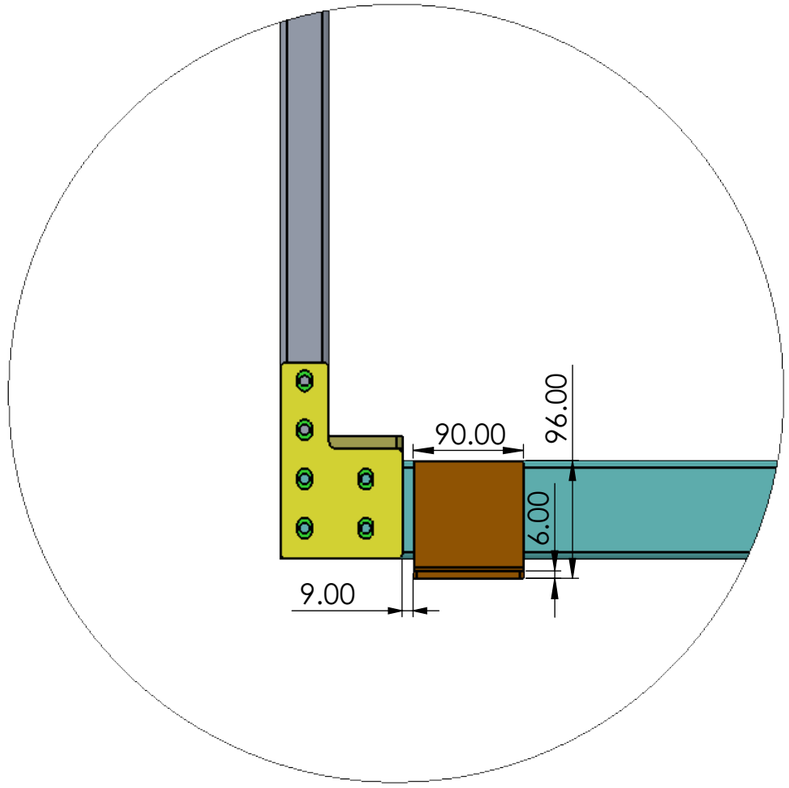


DETAIL AO
SCALE 1 : 5

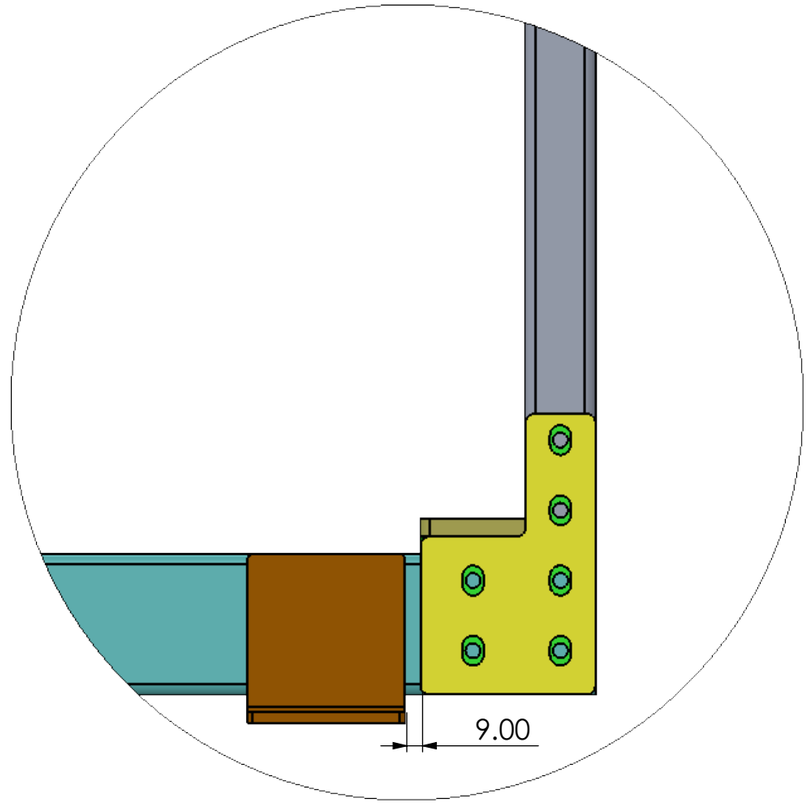


DETAIL AP
SCALE 1 : 3.5

NOTE :- LOCKING PLATE 02 FITTING POSITION
ON ALL PANELS ARE SAME AND OPPOSITE
SIDE OF EACH OTHER

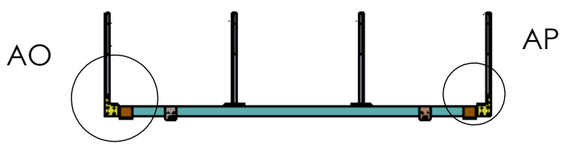

SECTION AN-AN
SCALE 1 : 45

TITLE - ROOF AUTOMATION				NIHVA TECHNOLOGIES PVT.LTD.PUNE
DWG NO - NTPL-281-PM-001-02-02-00				Website - www.nihva.com
	NAME	SIGNATURE	DATE	PROJECT NO - NTPL-281-B-PM
DRAWN	V.G.		25-05-2025	PRODUCT - RETRACTABLE ROOF
CHK'D	S.W.		25-05-2025	SITE LOCATION - AKOLA
APPV'D	V.T.		25-05-2025	
if any queries contact - supportautomation@nihva.com				REVISION - QTY - 1
ALL DIMENSION ARE IN mm			A3	SCALE - SHEET 40 OF 41

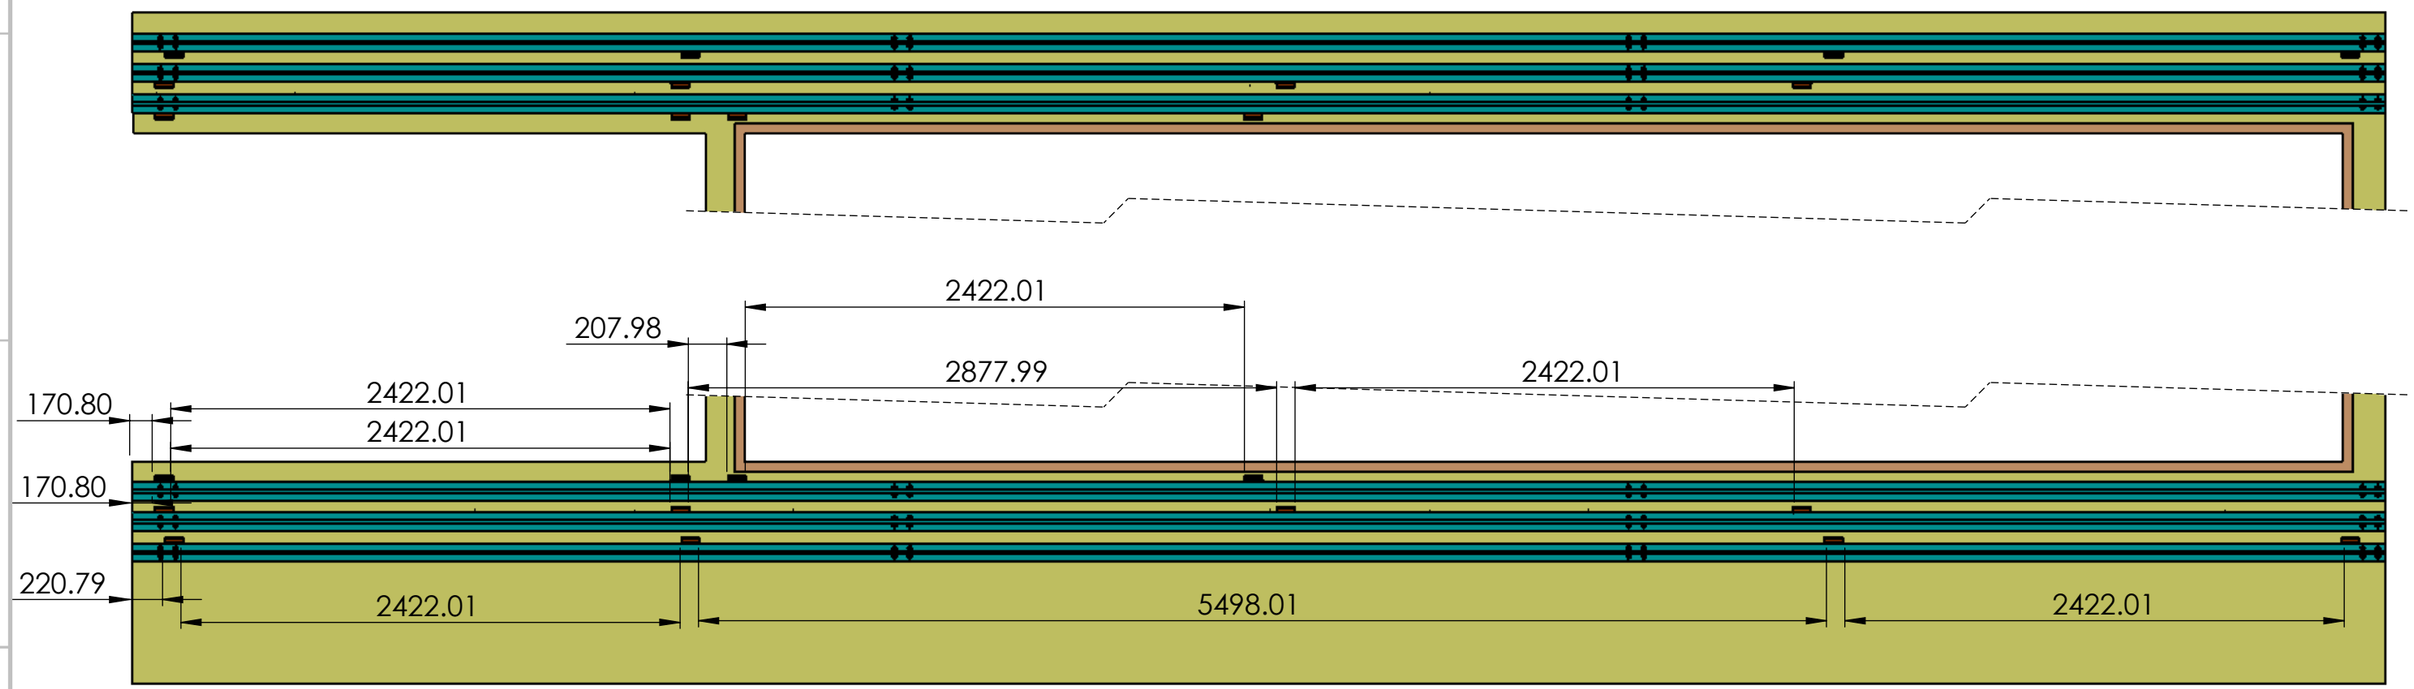

NOTE :- LOCKING PLATE 01 POSITION ON TRACK AT MOTOR SIDE
AS SHOWN IN ABOVE AND OTHER SIDE TRACK LOCKING
PLATE POSITION AND DIMENSIONS ARE SAME.

TITLE - ROOF AUTOMATION				NIHVA TECHNOLOGIES PVT.LTD.PUNE
DWG NO - NTPL-281-PM-001-00-00-00				Website - www.nihva.com
	NAME	SIGNATURE	DATE	PROJECT NO - NTPL-281-B-PM
DRAWN	V.G.		25-05-2025	PRODUCT - RETRACTABLE ROOF
CHK'D	S.W.		25-05-2025	SITE LOCATION - AKOLA
APPV'D	V.T.		25-05-2025	
if any queries contact - supportautomation@nihva.com				REVISION - QTY - 1
ALL DIMENSION ARE IN mm		A3		SCALE - SHEET 41 OF 41