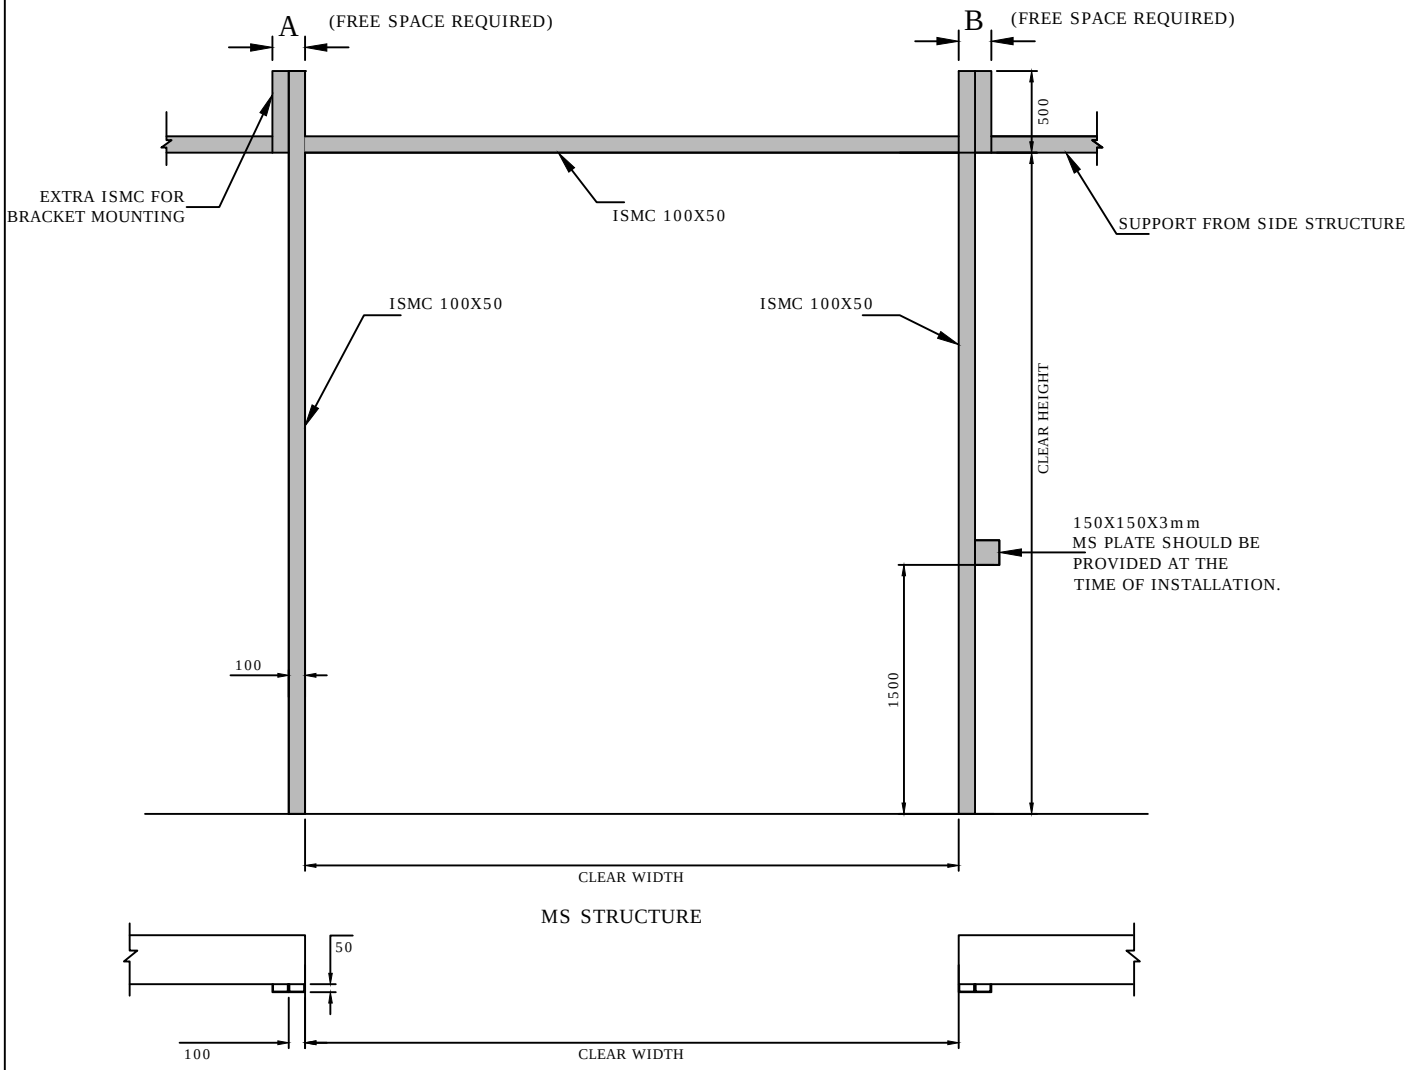


DIMENSION :

| CLEAR WIDTH | CLEAR HEIGHT | QUANTITY |
|---|---|---|
| 2500 mm | 2500 mm | 02 NOS. |
| 3500 mm | 3500 mm | 01 NOS. |
| 2500 mm | 2500 mm | 01 NOS. |

MATERIAL :

THICKNESS :

NIHVA TECHNOLOGY PVT. LTD. PUNE
NIHVA TECHNOLOGIES PVT. LTD.
Email:- info@nihva.com
Website:- www.nihva.com

TITLE:

STRUCTURE FOR
DOUBLE WALL ROLLING SHUTTER

CLIENT'S APPROVAL :

CLIENT - INGERSOLL-RAND (INDIA) LTD.

PROJECT -

SITE LOCATION -AHMEDABAD

DWG. NO. : NIHVA/16-17/129

| SCALE: NTS | WT: | SHEET:1 OF 1 |
|---|---|---|

| | |
|---|---|
| DRAWN BY: SURAJ | DATE: 21-01-2017 |
| CHECK : OMKAR | DATE: 21-01-2017 |
| APPROVED BY: R.K | DATE: 21-01-2017 |

If any queries contact : projects@nihva.com

NOTE: ALL DIMENSION ARE IN mm

| SHUTTER TYPE | CLEAR WIDTH | CLEAR HEIGHT | A | B | QUANTITY |
|---|---|---|---|---|---|
| DOUBLE WALL ROLLING SHUTTER | 2500 mm | 2500 mm | 400 | 600 | 02 NOS. |
| DOUBLE WALL ROLLING SHUTTER | 3500 mm | 3500 mm | 400 | 600 | 01 NOS. |
| SINGLE WALL ROLLING SHUTTER | 2500 mm | 2500 mm | 300 | 600 | 01 NOS. |

THIS DRAWING & DESIGNING IS THE PROPERTY OF NIHVA TECHNOLOGIES. NOT BE SOLD OR COPY TO ANY OTHER CONCERN.