
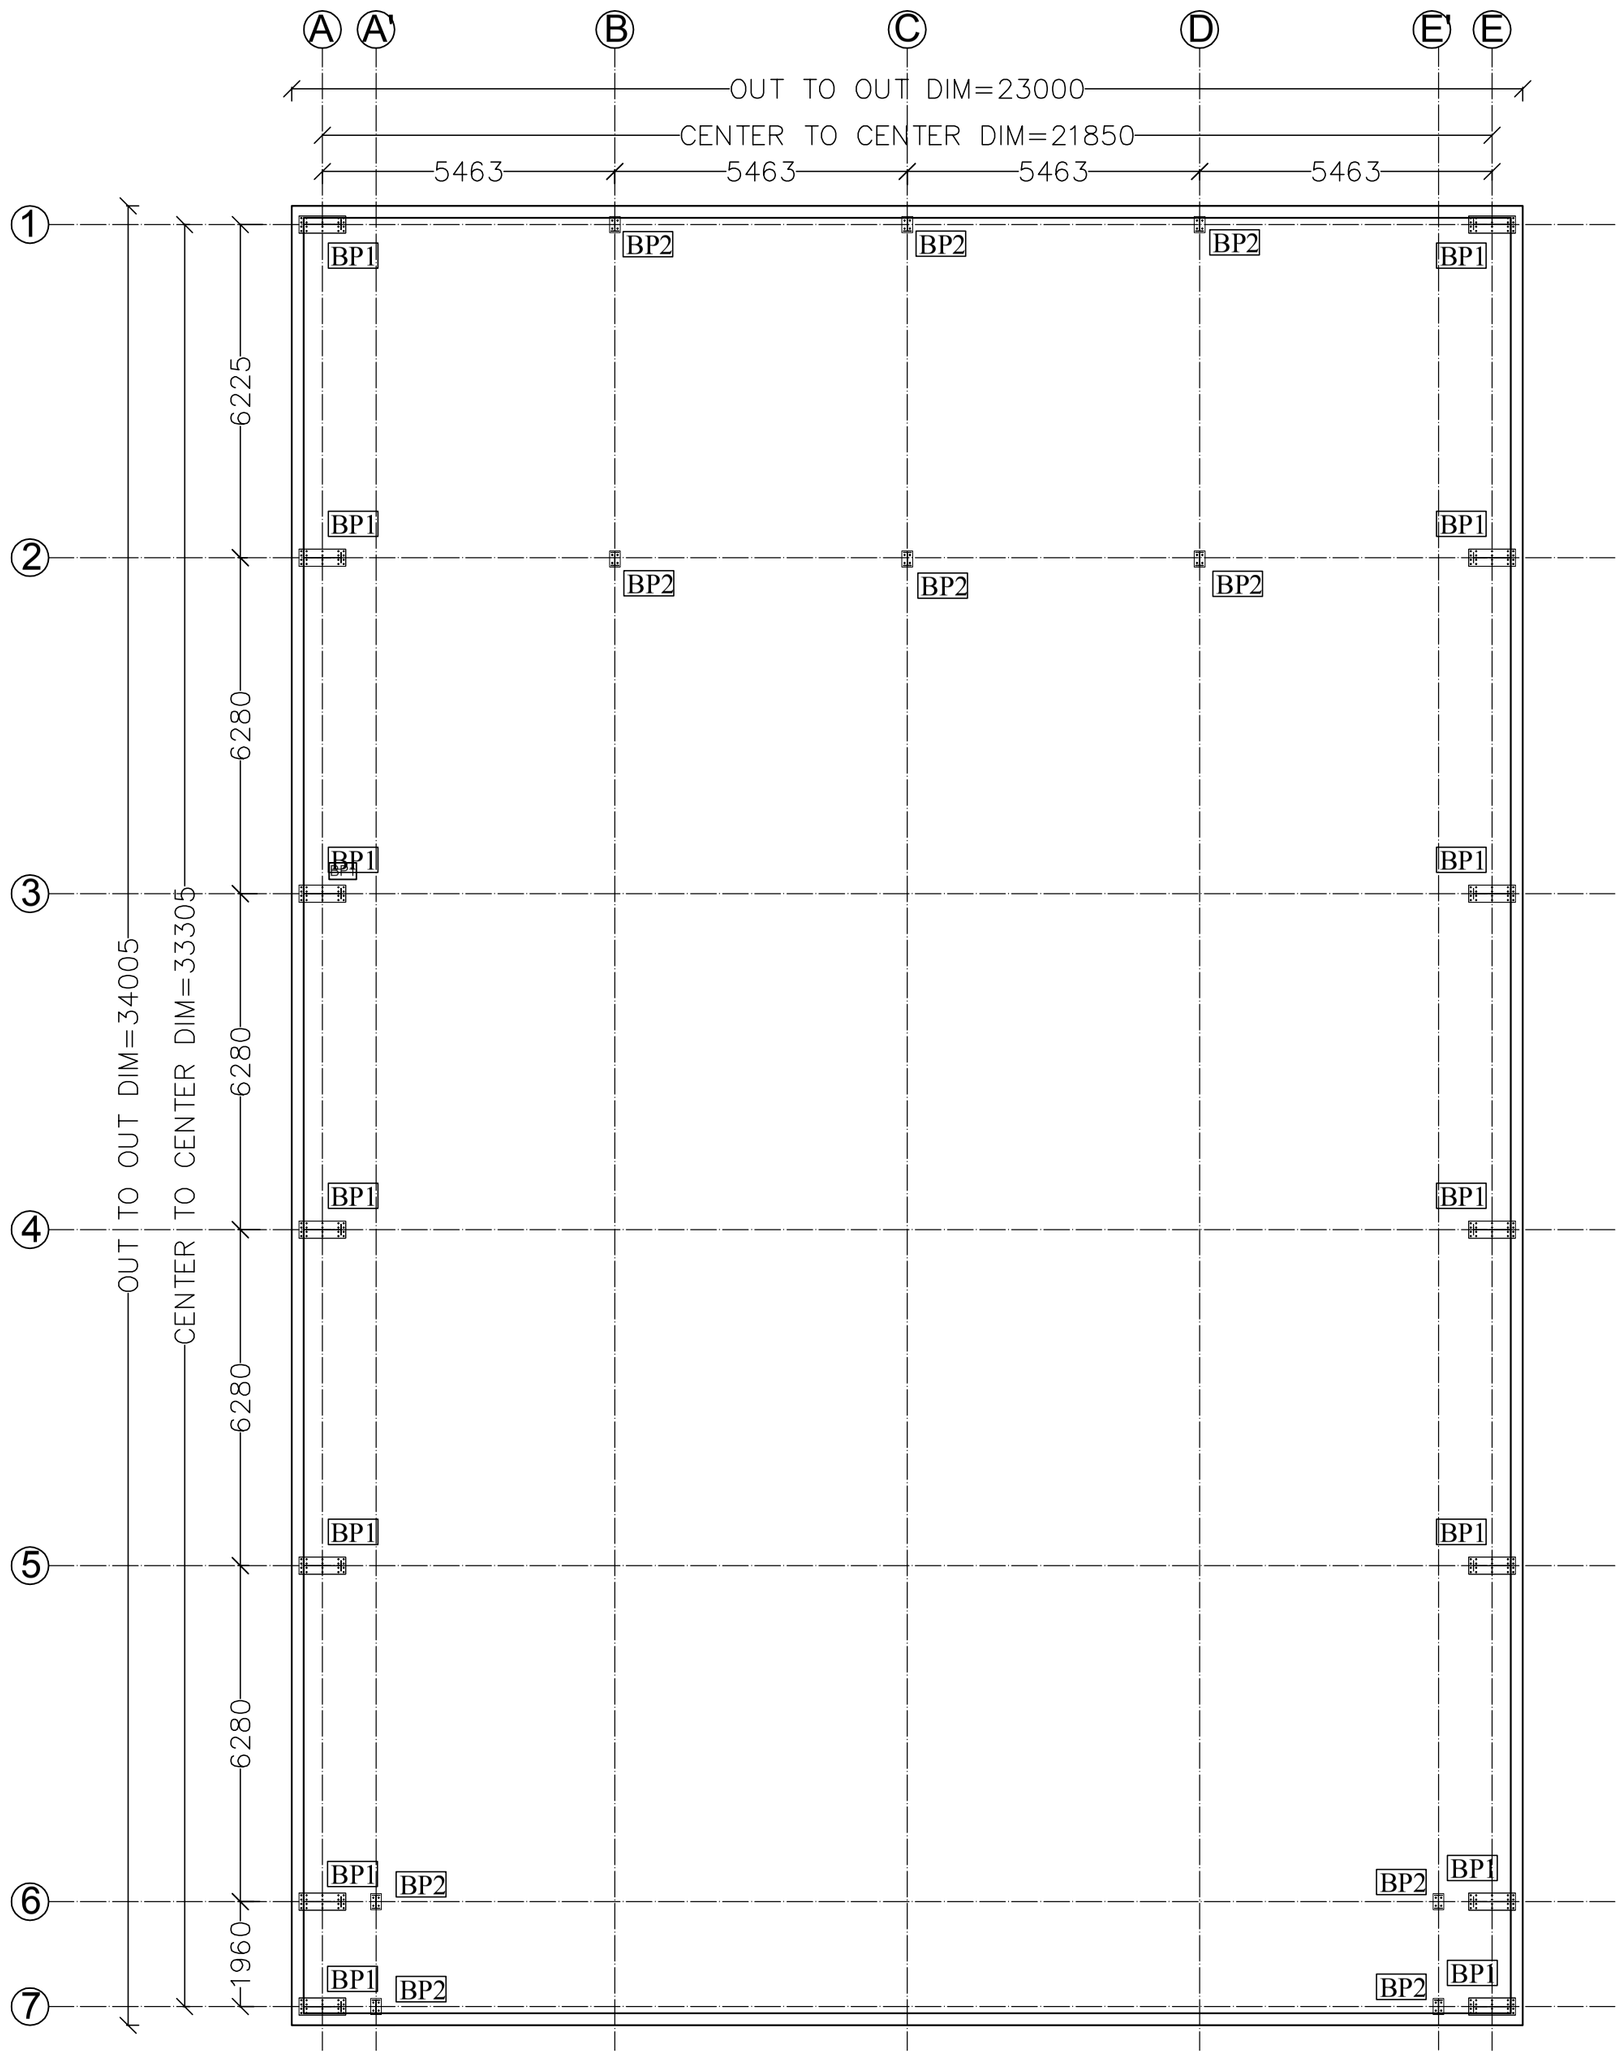


INDEX PLAN

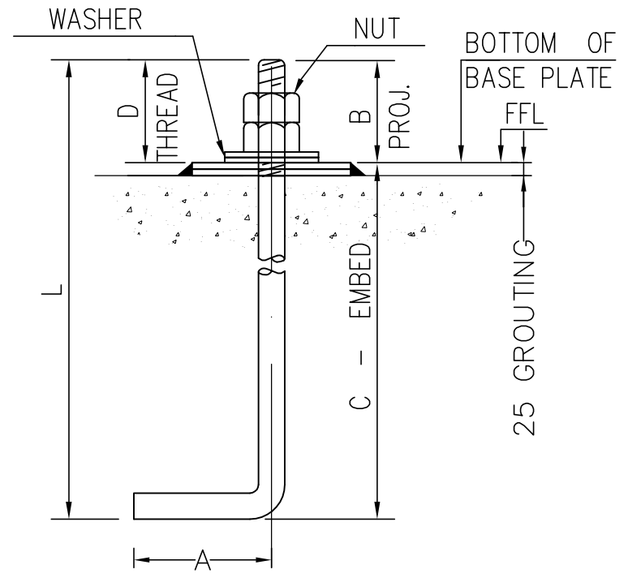


TYPICAL ANCHOR BOLT DETAILS

ANCHOR BOLT SETTINGS


ANCHOR BOLT SCHEDULE –								
SYMBOL	QUANTITY	DIAMETER	L	A	B	C	D	MARK NO.
⊕	320	20	605	120	100	385	100	--

BASE PLATE SEATTINGS

BASE PLATE TYPE	BASE PLATE SIZE	NO OF PLATES
BP1	874X320X20MM	14
BP2	200X300X16MM	10

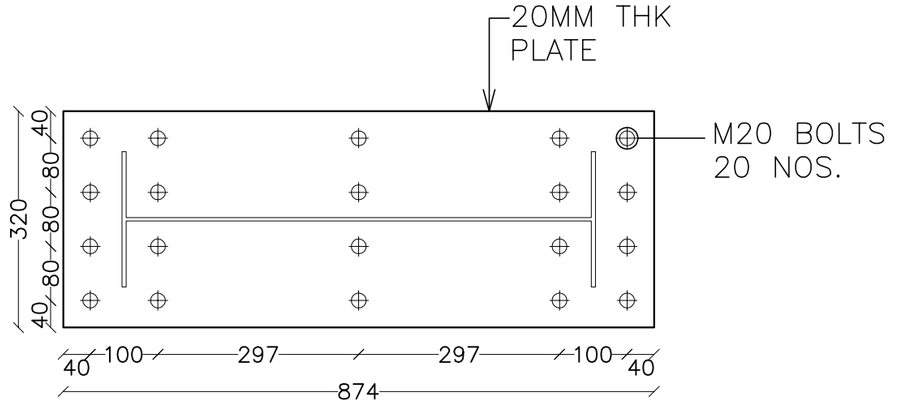

BASE PLATE DETAILS -BP1

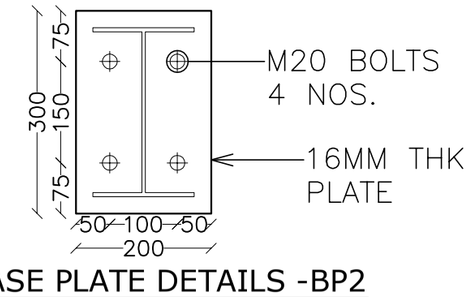

BASE PLATE DETAILS -BP2

KEY PLAN :-

LEGEND :-
- REINFORCED CONCRETE
- 230MM THK BRICK WALL
- STRUCTURAL GLAZING

N

GENERAL NOTES :

ALL DIMENSIONS ARE IN MILLIMETRES AND ARE UNFINISHED DIMENSIONS UNLESS OTHERWISE SPECIFIED.

ALL LEVELS ARE IN METRES AND ARE UNFINISHED LEVELS UNLESS OTHERWISE SPECIFIED.

DO NOT SCALE DRAWINGS. ONLY WRITTEN DIMENSIONS SHALL BE FOLLOWED. ANY DISCREPANCIES NOTED SHALL BE BROUGHT TO THE NOTICE OF THE ARCHITECT PRIOR TO EXECUTION.

SCHEDULE OF JOINERY

TYPE	DESCRIPTION	SIZE	NO.
RS	HANGER DOOR	24000 x 9000	01
W	WINDOW	1500 x 1200	20
D	DOOR	1200 x 2200	0

STRUCTURAL NOTES :

* ANCHOR BOLTS OF GRADE 4.6
* CONCRETE GRADE M30
* REBAR GRADE Fe 415

REV.	DESCRIPTION	DATE	BY	CHD.
R1	ISSUED FOR APPROVAL	20-07-17	CMF	SSF
R0	ISSUED FOR APPROVAL	20-07-17	CMF	SSF

AMENDMENT

GRAPHIC SCALE: 0 0.5M 2M 4M / 0.5M 0 1M 3M 5M

ARCHITECT

CLIENT:
HANGER
AT PUNE

PROJECT LOCATION:
PUNE

DRAWING TITLE:
ABBP PLAN

SCALE : NTS | DRAWN : SRK | DATE : 02-08-2018 | CHKD : SRK | R0

PROJECT ID: 1718-AI-052-PEB

DRAWING NO: PD: 01

Astre Infra
Private Limited
imagine and its done
691, Bemciel Indl. Estate,
Khanapur Rd,
Udyambag, Belgaum- 590008.
www.astreinfra.com

THESE DRAWINGS ARE UNDER COPYRIGHT AND ARE THE PROPERTY OF ASTRE INFRA PVT. LTD.. NONE OF THE DRAWINGS AND RELATED DOC-UMENTS CAN BE REPRODUCED, COPIED IN WHOLE OR IN PART WITHOUT PRIOR EXPRESSED WRITTEN CONSENT OF ASTRE INFRA PVT.LTD. THESE DRAWINGS ARE ISSUED ON THE CONDITION THAT THEY SHALL NOT BE USED FOR ANY PURPOSE OTHER THAN WHICH IT HAS BEEN LOANED, AFTER FULFILLING THE PURPOSE OF ISSUE THE DRAWINGS SHALL BE RETURNED TO ASTRE INFRA PVT.LTD.