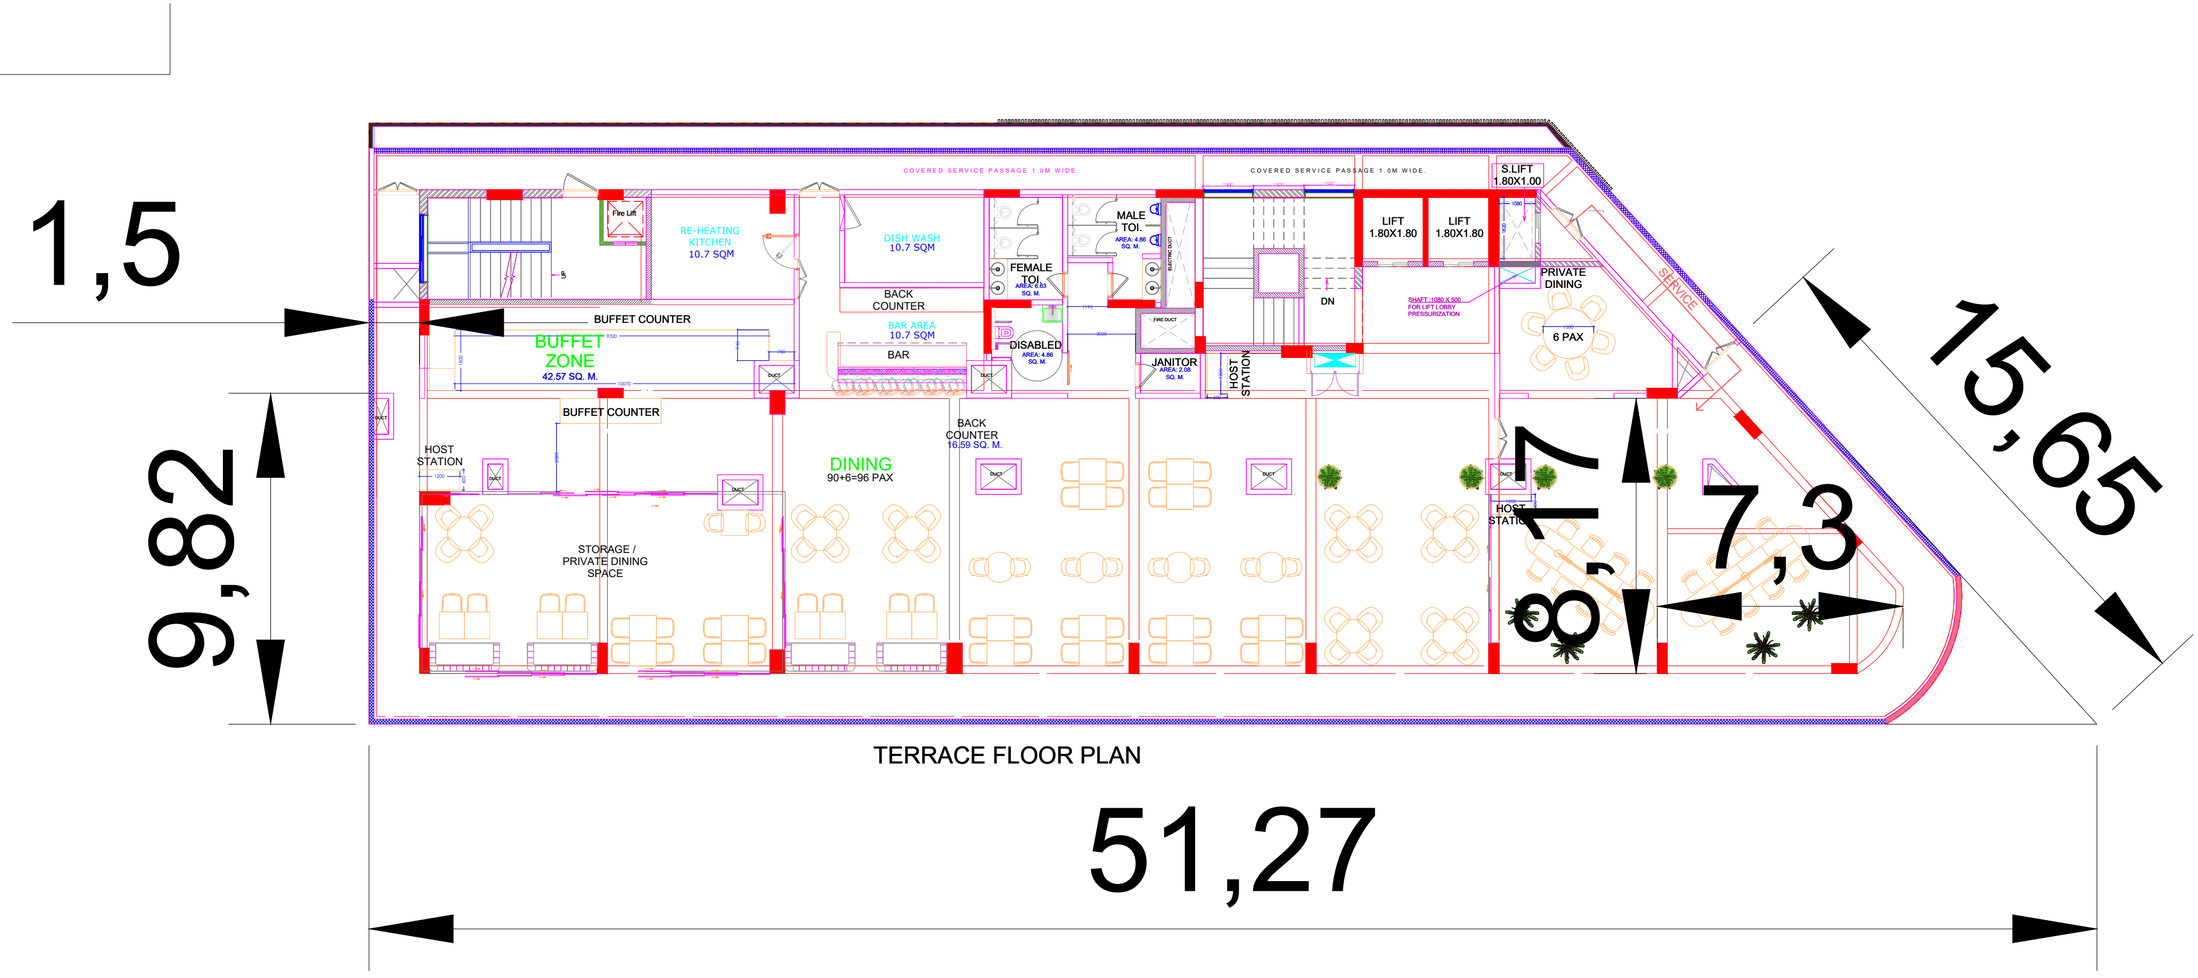

1,5
6,82
COVERED SERVICE PASSAGE 1.0M WIDE.
COVERED SERVICE PASSAGE 1.0M WIDE.
S.LIFT
1.80X1.00
LIFT
1.80X1.80
LIFT
1.80X1.80
SERVICE
15,65
Fire Lift
RE-HEATING
KITCHEN
10.7 SQM
DISH WASH
10.7 SQM
MALE
TOI.
AREA: 4.86
SQ. M.
FEMALE
TOI.
AREA: 4.86
SQ. M.
DISABLED
AREA: 4.86
SQ. M.
JANITOR
AREA: 2.06
SQ. M.
HOST
STATION
DN
SHAFT - 1080 X 500
FOR LIFT LOBBY
PRESSURIZATION
PRIVATE
DINING
6 PAX
BUFFET COUNTER
BUFFET
ZONE
42.57 SQ. M.
BACK
COUNTER
BAR AREA
10.7 SQM
BAR
BUFFET COUNTER
HOST
STATION
DINING
90+6=96 PAX
BACK
COUNTER
16.59 SQ. M.
STORAGE /
PRIVATE DINING
SPACE
HOST
STATION
3,17
7,3
8,5
TERRACE FLOOR PLAN
51,27