

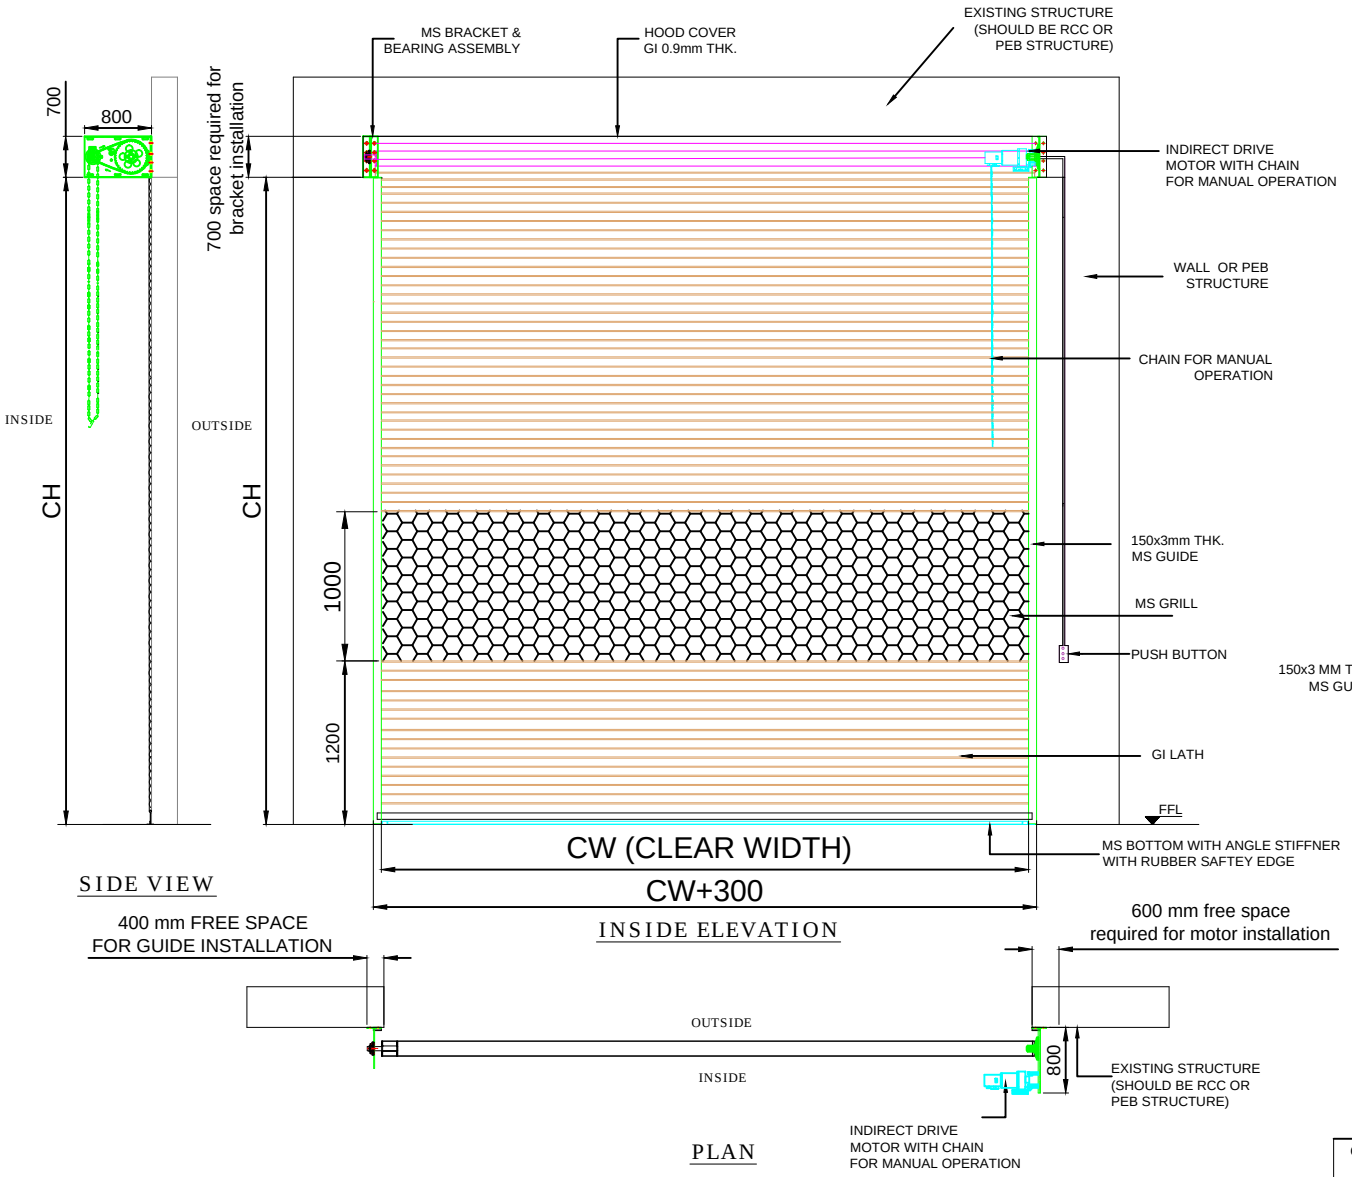


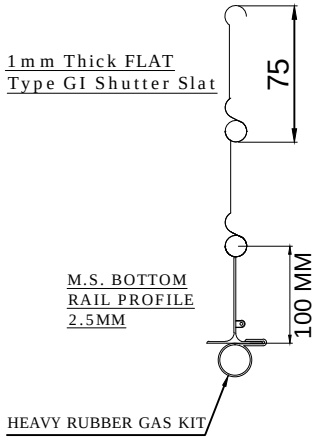

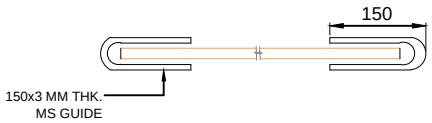

CLEAR WIDTH (CW)	CLEAR HEIGHT (CH)	QUANTITY
4800	6000	1

DIMENSION :

CLEAR WIDTH	CLEAR HEIGHT	QUANTITY
4800 mm	6000 mm	01 NOS.

MATERIAL :

THICKNESS :

NOTE:
1.REQUIRED STRUCTURE FOR SHUTTER SHALL BE IN CLIENT SCOPE.
2.ONE COAT OF RED OXIDE PRIMER WILL BE GIVEN TO NON GI COMPONENT OF SHUTTER.

NIHVA TECHNOLOGIES PVT. LTD.
NIHVA TECHNOLOGIES PVT. LTD. PUNE
Email:- info@nihva.com
Website:- www.nihva.com

TITLE:

MOTORIZED ROLLING SHUTTER

CLIENT'S APPROVAL :

CLIENT - S.S.GHORPADE

PROJECT - ROSS PROCESS EQUIPMENT

SITE LOCATION - CHAKAN

DWG. NO. : NIHVA/17-18/0002/R01

SCALE: NTS	WT:	SHEET:1 OF 1

DRAWN BY: SURAJ	DATE: 05-04-2017
CHECK : SAGAR P	DATE: 05-04-2017
APPROVED BY- R.K.	DATE: 05-04-2017

If any queries contact : projects@nihva.com

NOTE: ALL DIMENSIONS ARE IN mm

THIS DRAWING & DESIGN IS THE PROPERTY OF NIHVA TECHNOLOGIES. NOT TO BE SOLD OR COPY TO ANY OTHER CONCERN.