

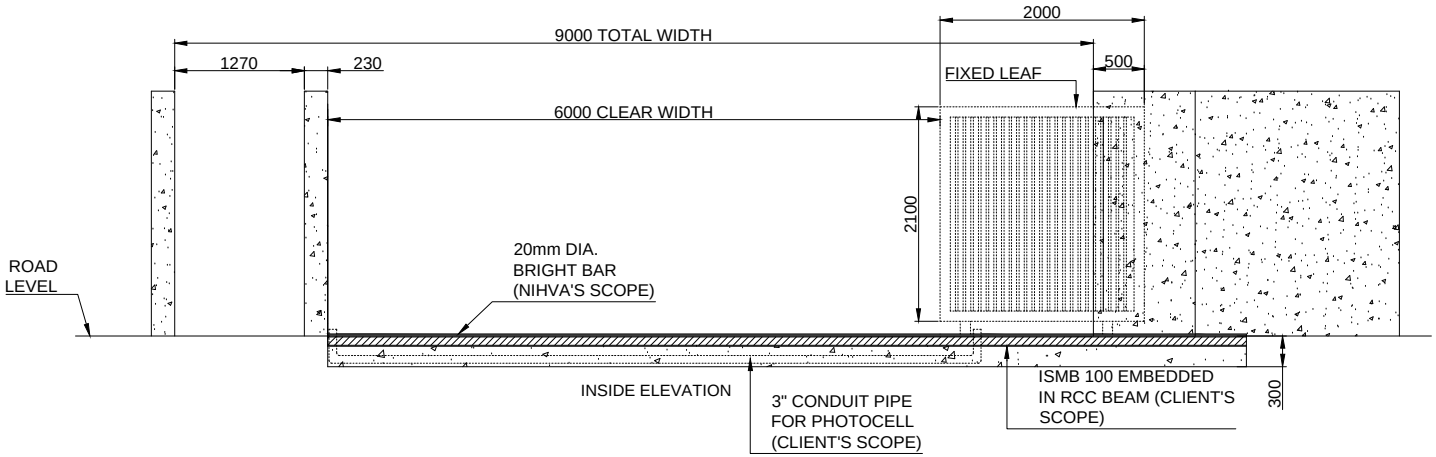


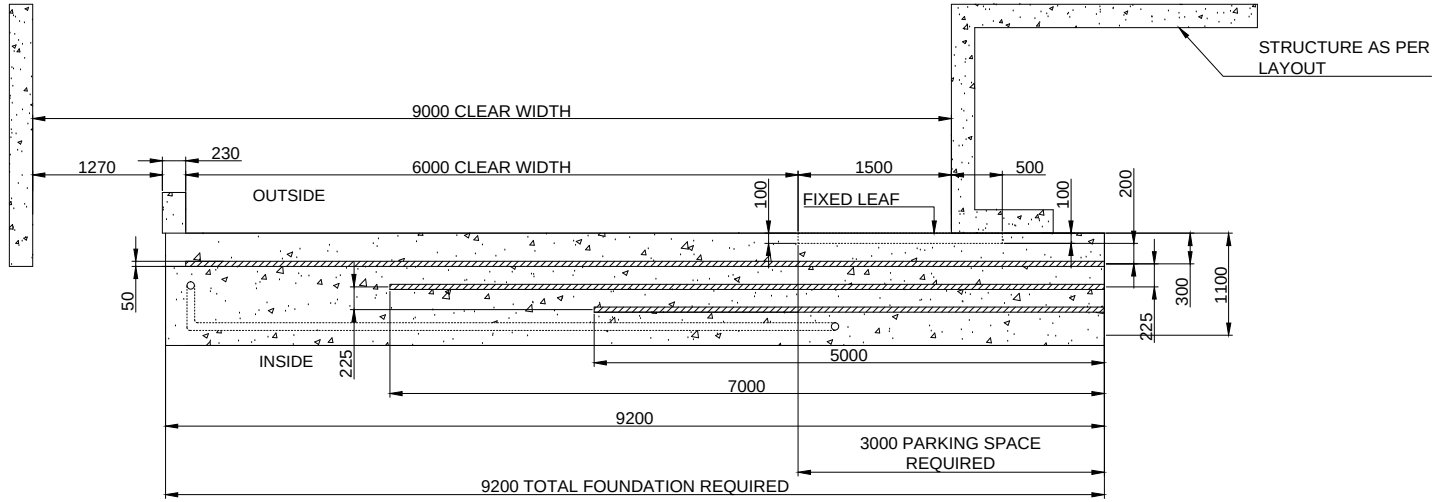

PLAN

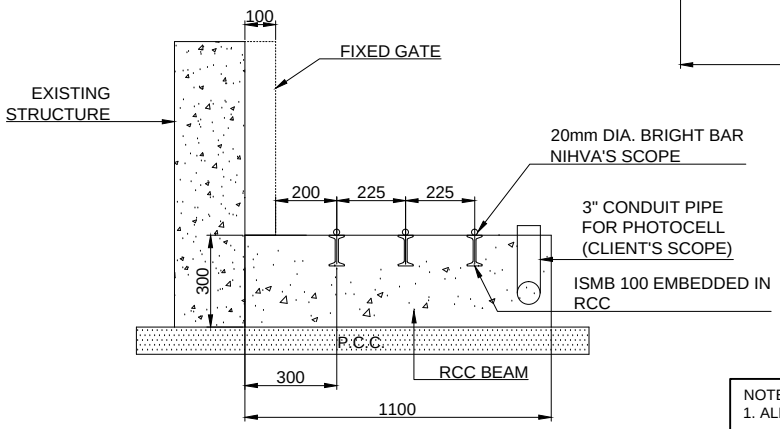

SIDE VIEW

REV 1- A. FOUNDATION WIDTH REVISED FROM 1000 TO 1100mm.

NOTE-
1. ALL REQUIRED CIVIL WORK WILL BE IN CLIENTS SCOPE.

GATE WIDTH	GATE HEIGHT	QUANTITY	LOCATION
6000mm	2100mm	1 NOS	SECURITY CABIN 1

This drawing & design is the property of NIHVA TECHNOLOGIES. Not to be sold or copied to any other concern.

TITLE
AUTOMATIC THREE LEAF TELESCOPIC GATE (6X2.1m) 2 FOUNDATION DRAWING

	NAME	DATE
DRAWN	OMKAR	30/10/17
CHECK	SHEKHAR	30/10/17
REV.		
APPROVAL	SHEKHAR	30/10/17

If any queries contact : projects@nihva.com

ALL DIMENSION ARE IN mm

NIHVA TECHNOLOGIES PVT. LTD.
NIHVA TECHNOLOGIES PVT. LTD. PUNE
Tel : 020 66304033
Email:- info@nihva.com
Website:- www.nihva.com

CLIENT - LUPIN LIMITED
PROJECT -
SITE LOCATION - MIHAN, NAGPUR
DWG. NO. : NIHVA/17-18/0251/R01 | REV -1
SCALE: NTS | WT: | SHEET: 01 OF 01