


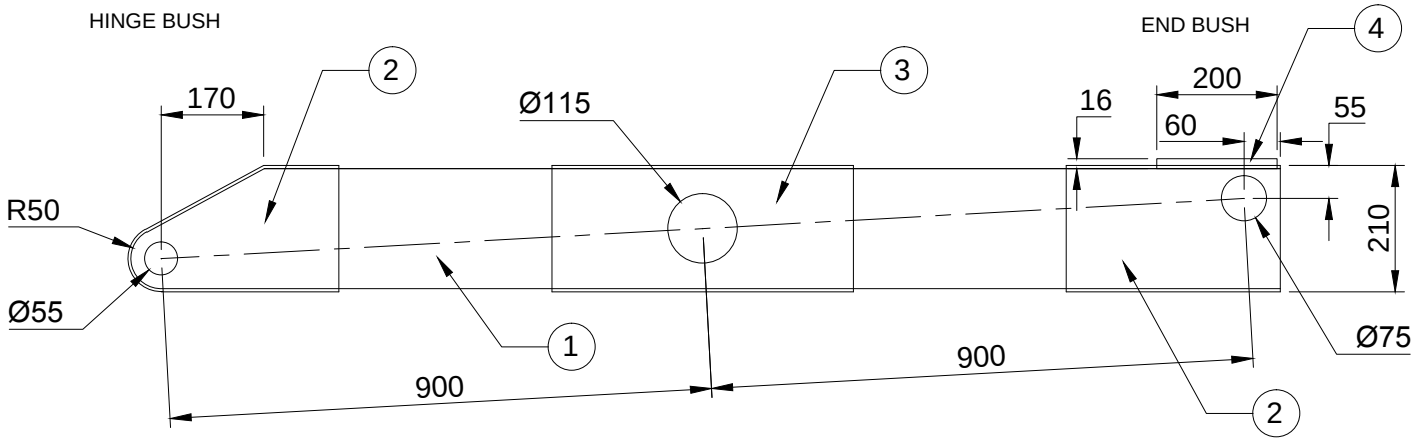

NOTE : MTL = M.S

1. ISMB 200 X 100 X 1915L = 2 NOS
2. PROFILE 210 X 8 THK X 350L = 8 NOS
3. PROFILE 210 X 8 THK X 500L = 4 NOS
4. FLAT 100 X 16 X 200L = 2 NOS

This drawing & design is the property of NIHVA TECHNOLOGIES. Not to be sold or copied to any other concern.

TITLE : - BOTTOM INNER SCISSOR			NIHVA TECHNOLOGIES PVT. LTD. PUNE Tel : 020 66304033 Email:- info@nihva.com Website:- www.nihva.com
	SIGN	DATE	
DRAWN	P.A	10.01.19	CLIENT -
CHECK	R.D	10.01.19	PROJECT -
REV.			SITE -
APPROVAL			DWG. NO. : NIHVA/18-19//MFG/NSCL327/05
If any queries contact : projects@nihva.com			SCALE: NTS / WT: / SHEET: 01 OF 01
ALL DIMENSION ARE IN mm			