

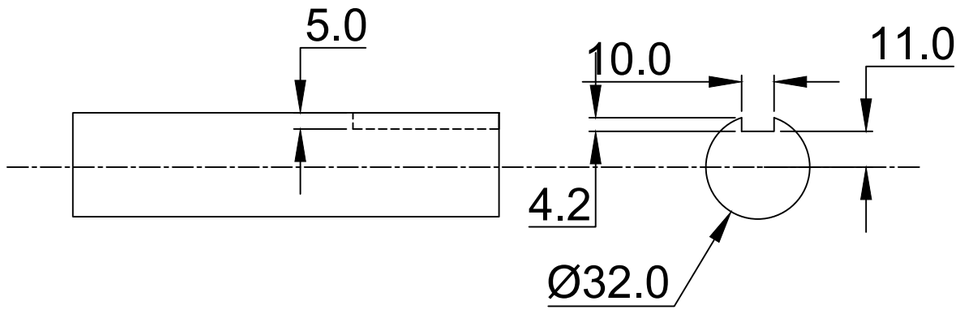


SHAFT DIA. 32 MM

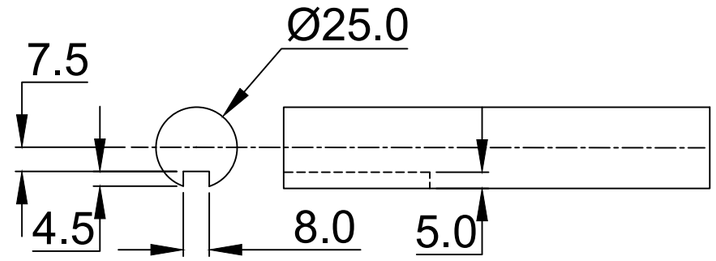

SHAFT DIA. 25 MM

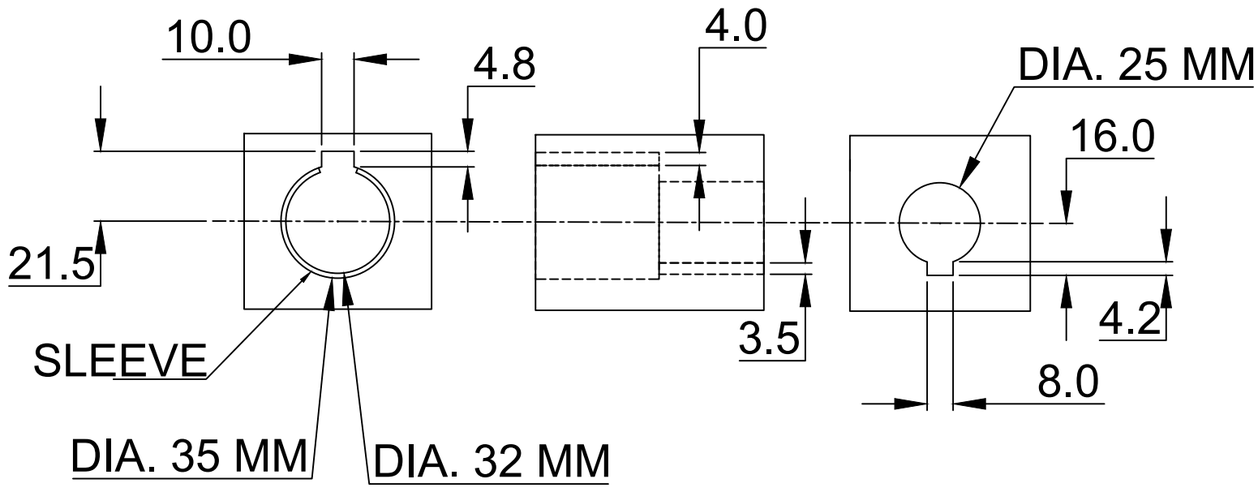

COUPLING DIA. 32 MM & 25 MM

KEY SIZES-

1. W 8 MM X H 8 MM
2. W 10 MM X H 10 MM

DOOR QTY : 02 NOS

This drawing & design is the property of NIHVA TECHNOLOGIES. Not to be sold or copied to any other concern.

TITLE	KEY-WAY DWG FOR COUPLING AND SHAFTS			NIHVA TECHNOLOGIES PVT. LTD.
	NAME	SIGN	DATE	
DRAWN	MAHESH S.		24.08.2022	CLIENT -
CHECK	MAHESH S.		24.08.2022	PROJECT -
APPRD.	AMIT K.		24.08.2022	SITE LOCATION -
If any queries contact : sales@nihva.com				DWG. NO. : NIHVA/22-23/VDR/0067 REV- 0
ALL DIMENSION ARE IN mm				SCALE: NTS WT: SHEET: 01 OF 01

NIHVA TECHNOLOGIES PVT. LTD. PUNE
Tel : 020 66304033
Email:- info@nihva.com
Website:- www.nihva.com