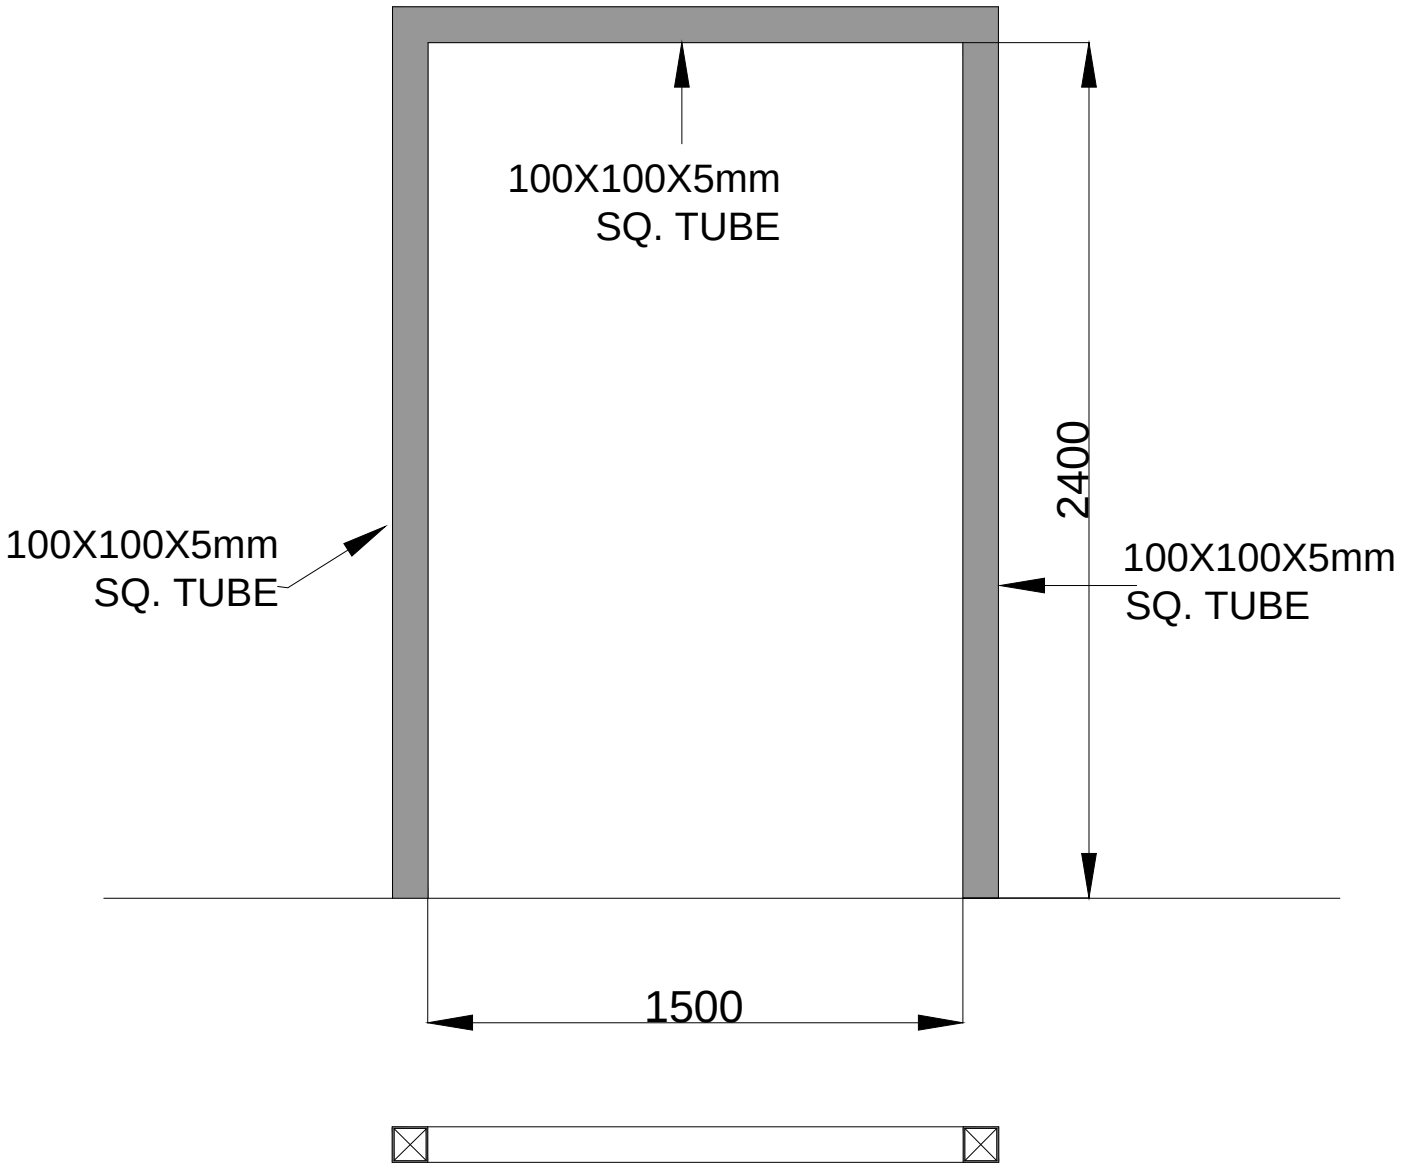

This drawing & design is the property of NIHVA TECHNOLOGIES. Not to be sold or copied to any other concern.

TITLE

STRUCTURE FOR FIRE DOOR

CLIENT APPROVAL

ALL DIMENSION ARE IN mm

NIHVA TECHNOLOGIES PVT. LTD.

NIHVA TECHNOLOGIES PVT. LTD. PUNE
Tel : 020 66304033
Email:- info@nihva.com
Website:- www.nihva.com

	SIGN	DATE
DRAWN	OMKAR	07/10/2017
CHECK	SHEKHAR.	07/10/2017
APPRD.	SHEKHAR	07/10/2017
REV.		
MFG		
Ref. No.		

CLIENT -FERRERO INDIA PVT. LTD

PROJECT -

SITE -BARAMATI

DWG. NO. - NIHVA/17-18/0234

SCALE: NTS | WT: | SHEET: 01 OF 01

If any queries contact : projects@nihva.com